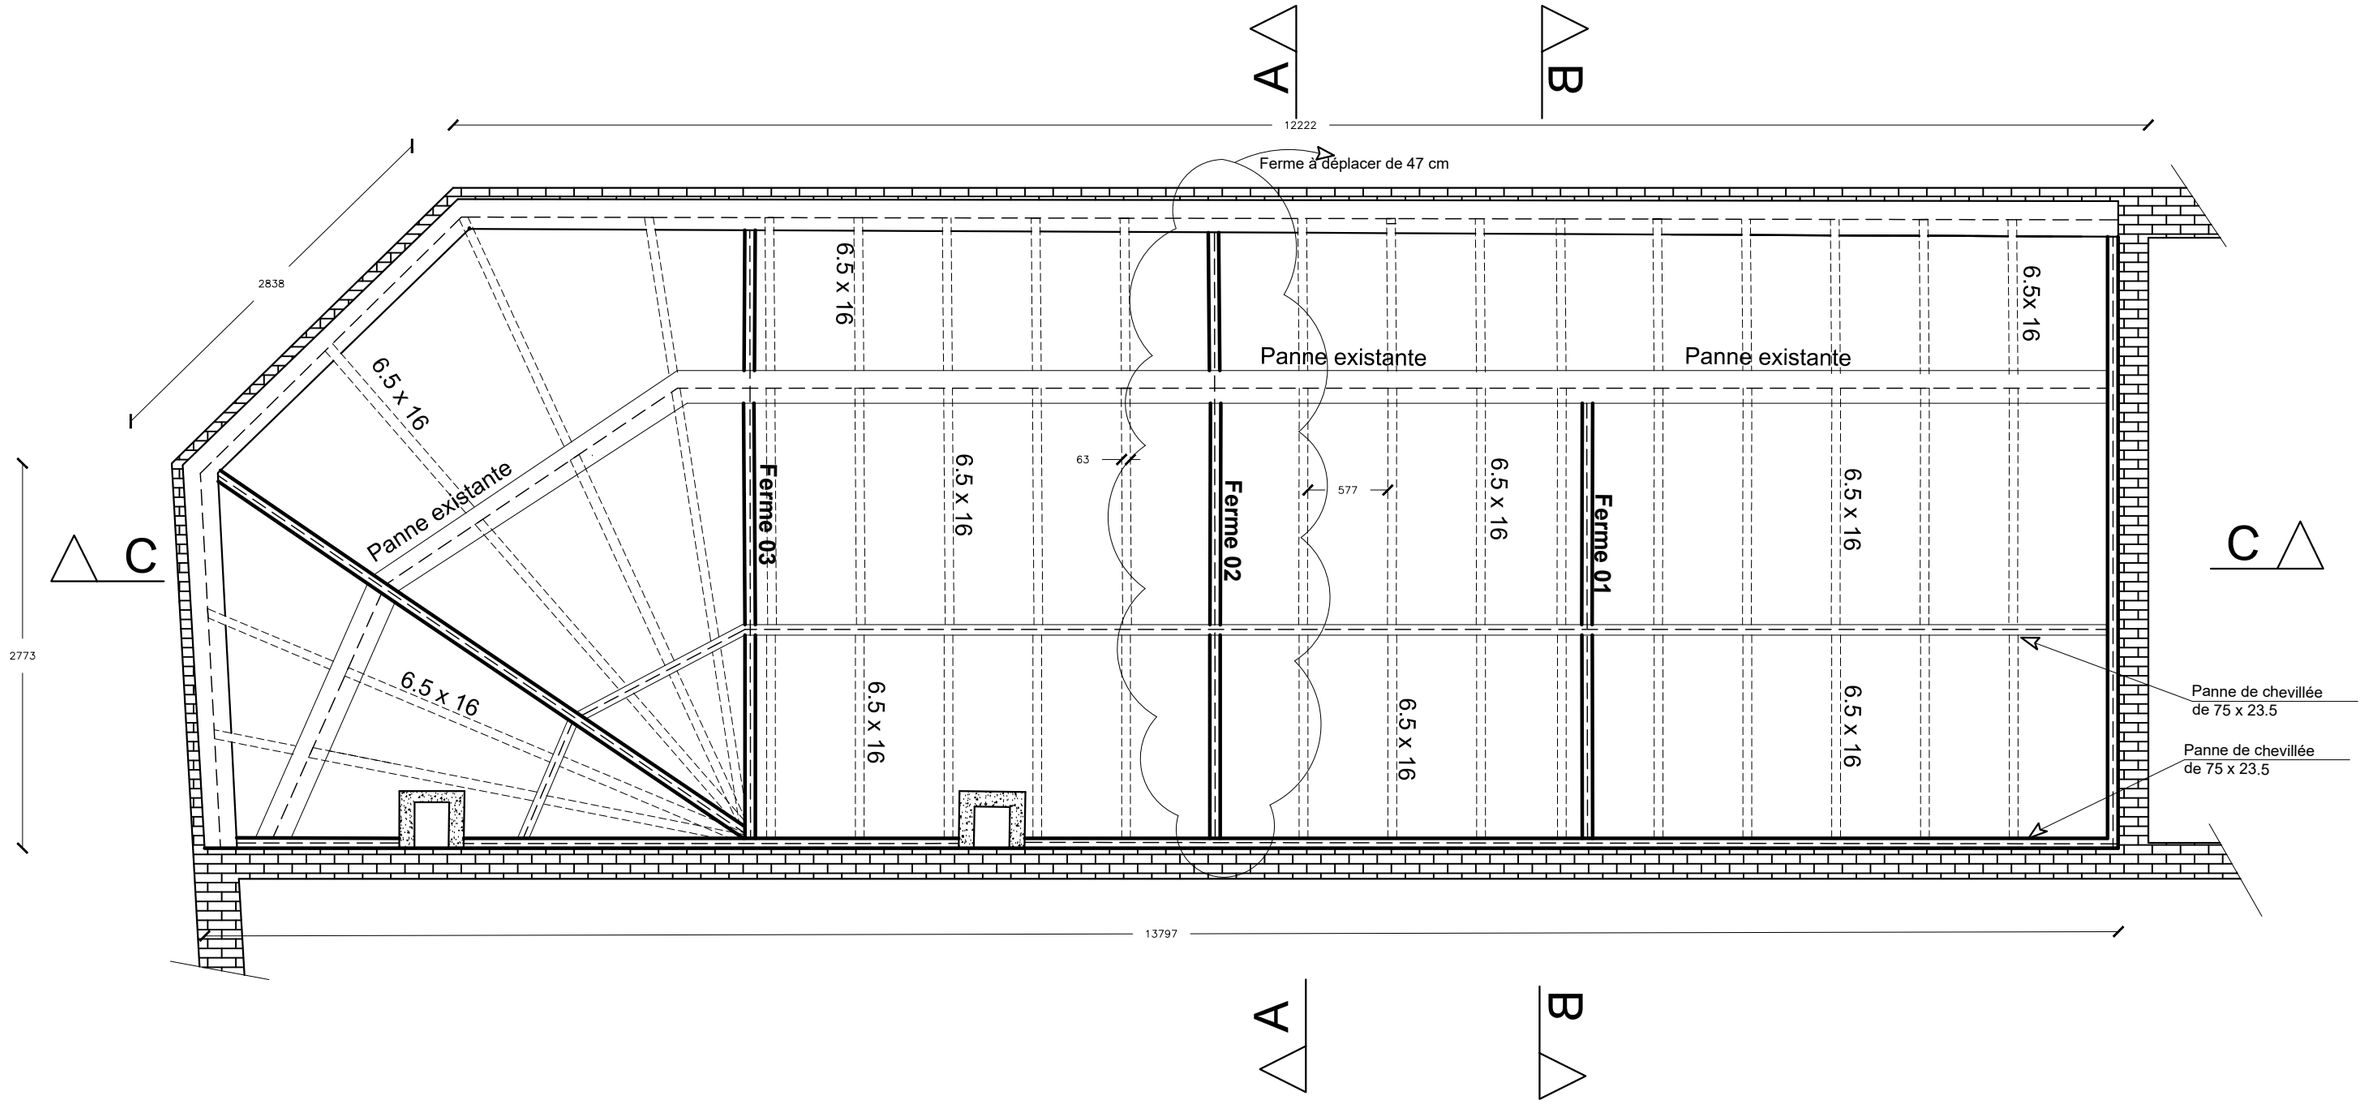


Maîtrise de l'Ouvrage :
Solution travaux
Services Nord
26 Chemin d'Esquermes
59790 Ronchin

BET STRUCTURE :
J.K.F. STRUCTURE
92 Bd du GLE du Gaulle
59100 Roubaix


Création d'une charpente en bois dans un batiment existant

Dossier Etude Béton Armé

Vue en plan existant

Plan N° : GO 01

Ech : S0

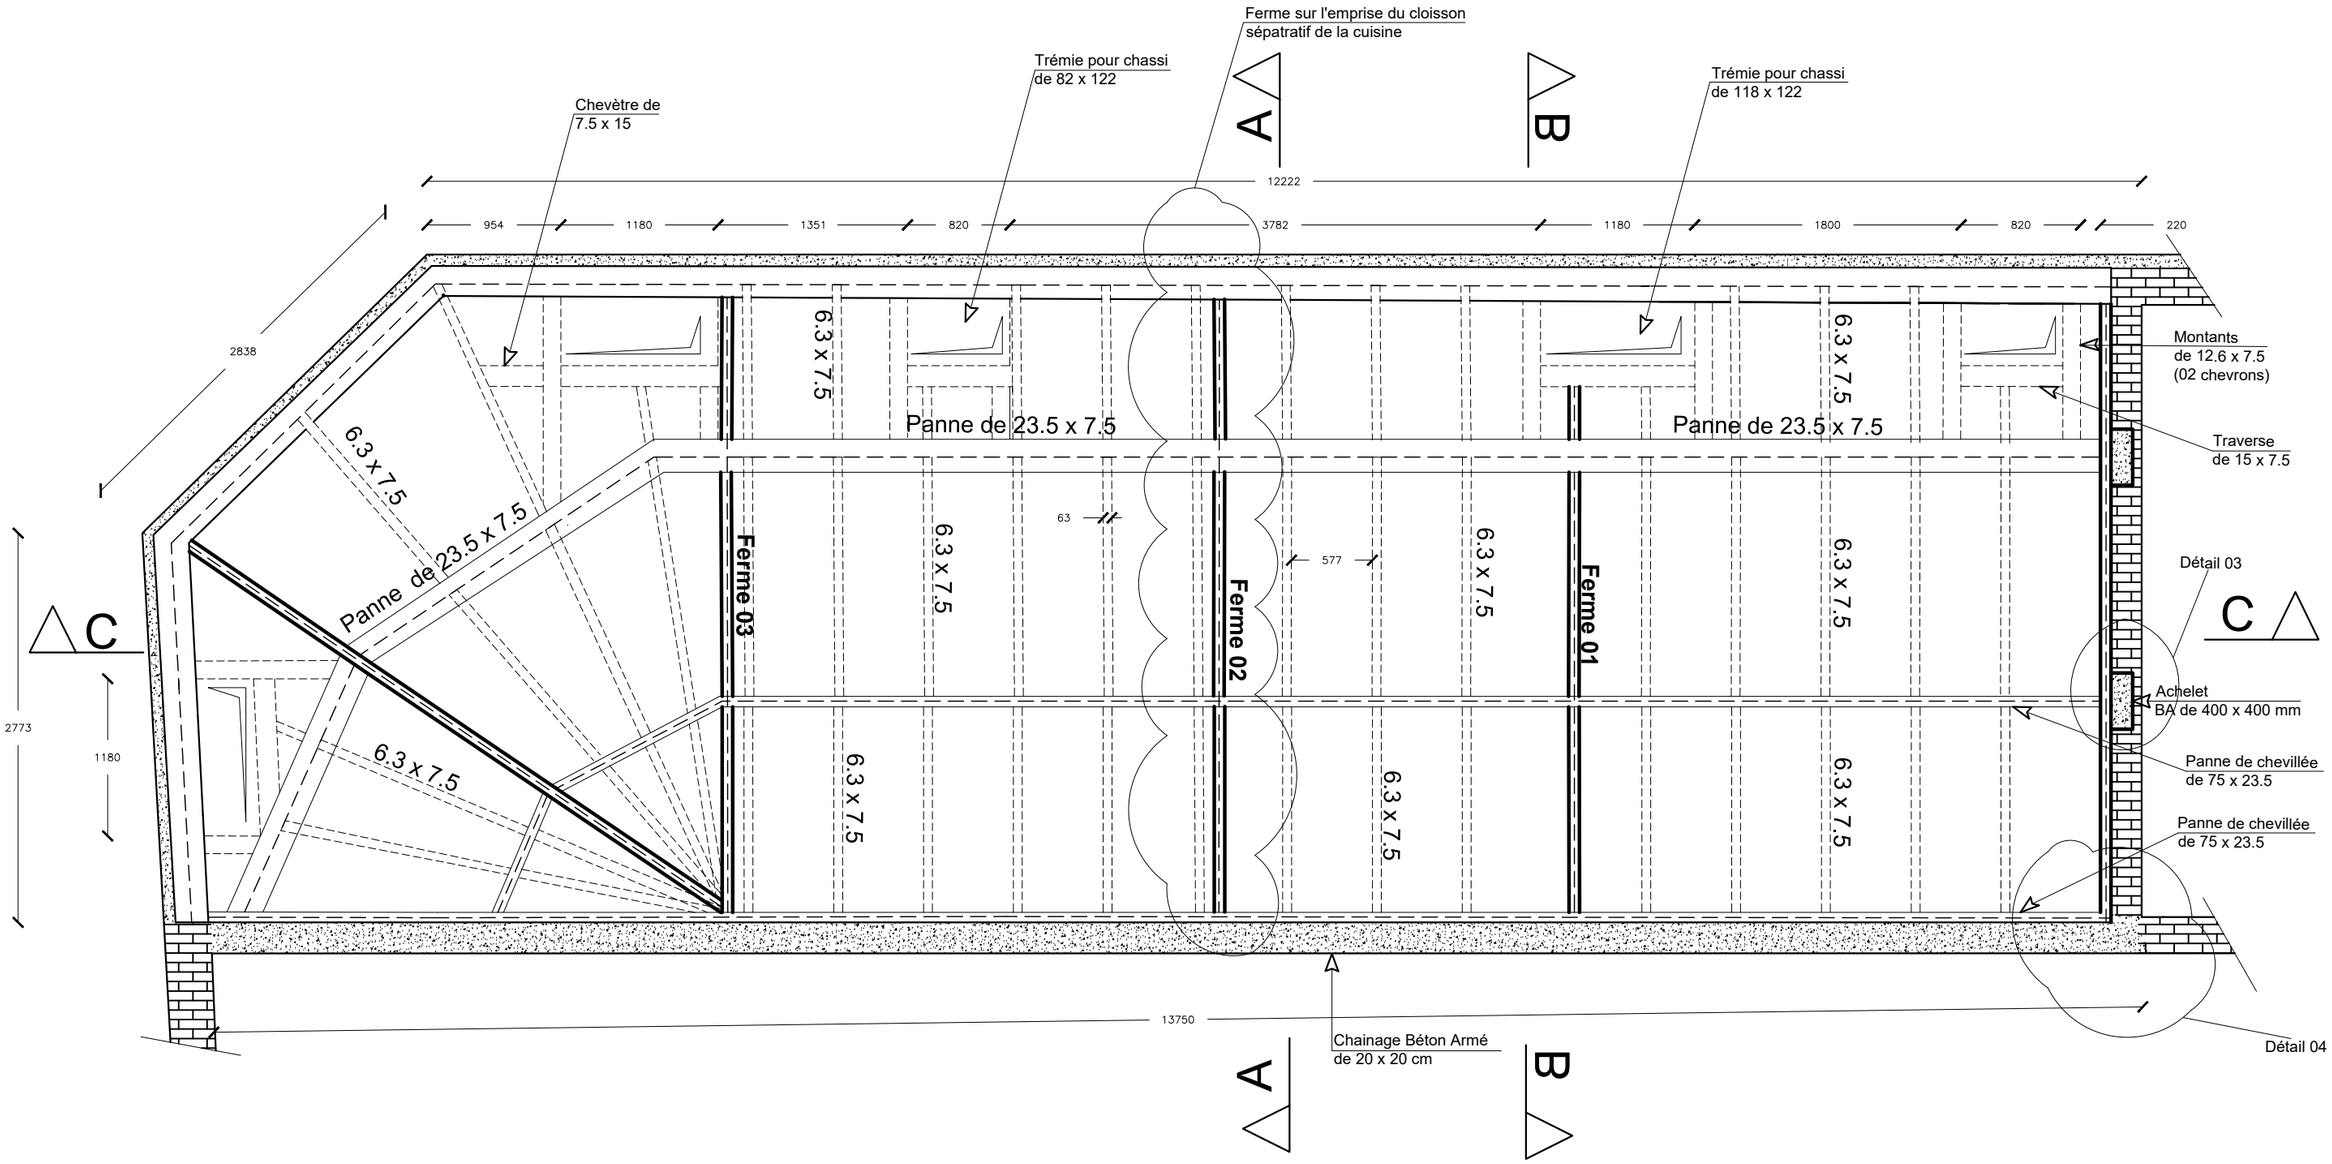

Maîtrise de l'Ouvrage :
Solution travaux
Services Nord
26 Chemin d'Esquermes
59790 Ronchin

BET STRUCTURE :
J.K.F. STRUCTURE
92 Bd du GLE du Gaulle
59100 Roubaix


Création d'une charpente en bois
dans un batiment existant

Dossier Etude Béton Armé

Vue en plan projet

Plan N° : GO 02

Ech : S0

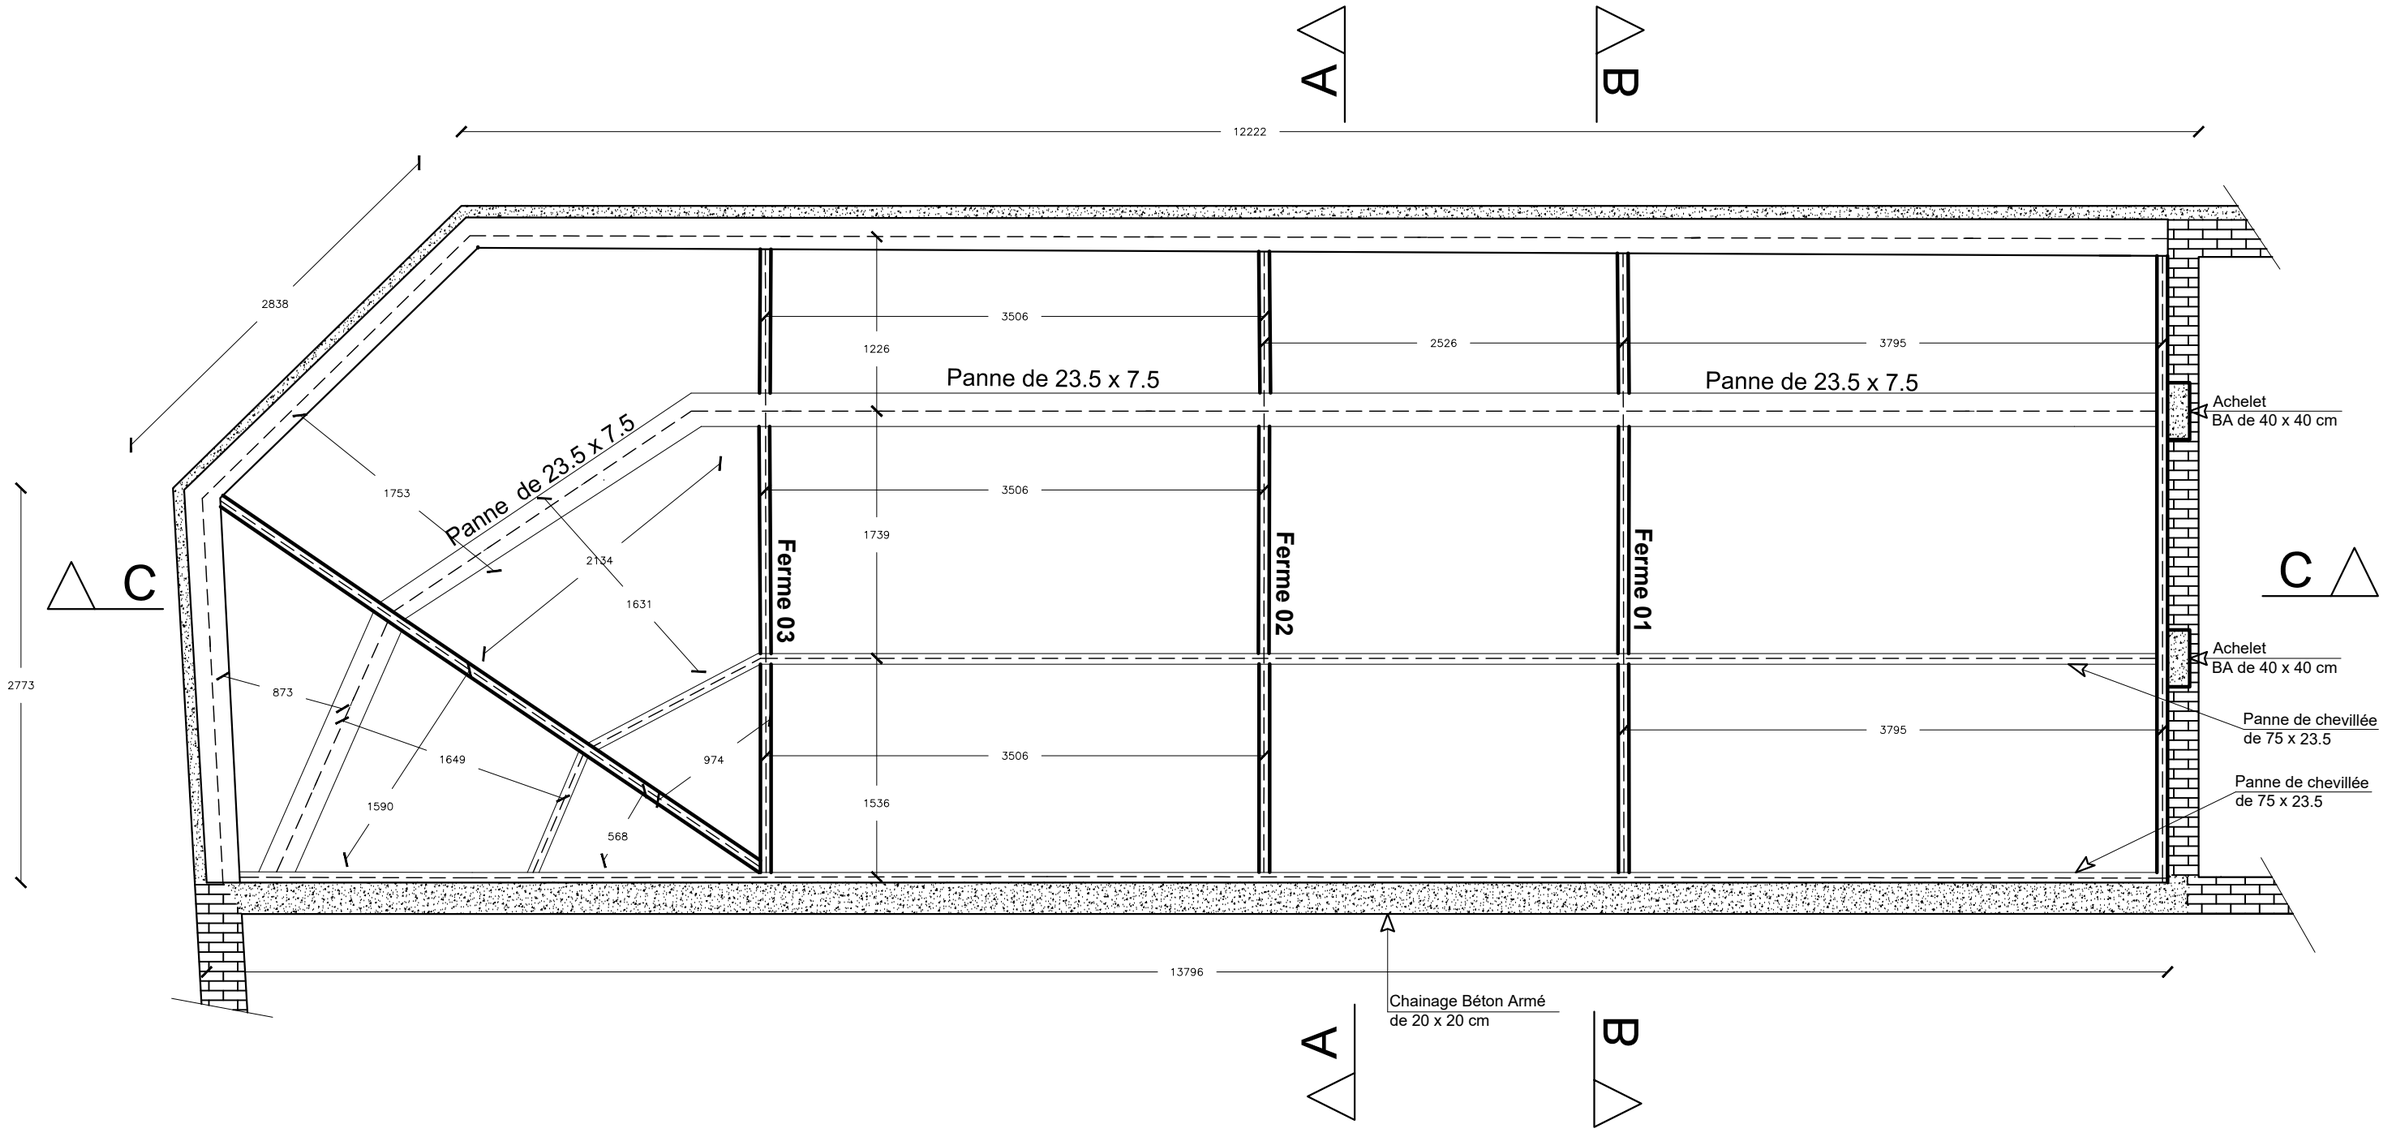

Maîtrise de l'Ouvrage :
Solution travaux
Services Nord
26 Chemin d'Esquermes
59790 Ronchin


BET STRUCTURE :
J.K.F. STRUCTURE
92 Bd du GLE du Gaulle
59100 Roubaix

Création d'une charpente en bois dans un batiment existant

Dossier Etude Béton Armé
Vue en plan projet
Structure primaire


Plan N° : GO 03

Ech : S0

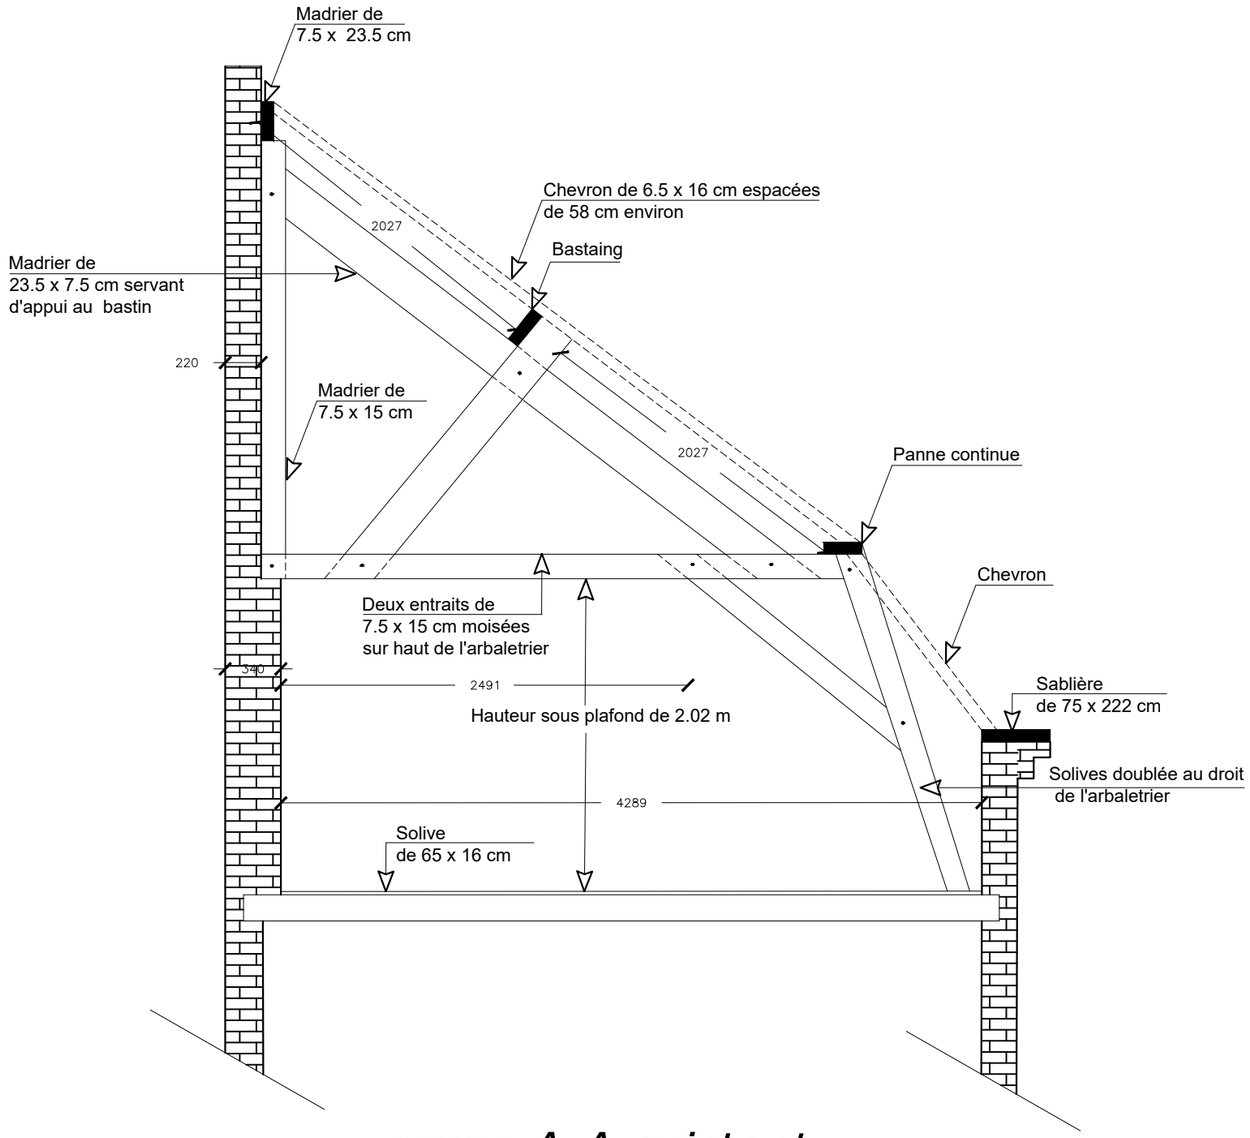

coupe A-A existant

Détail 01

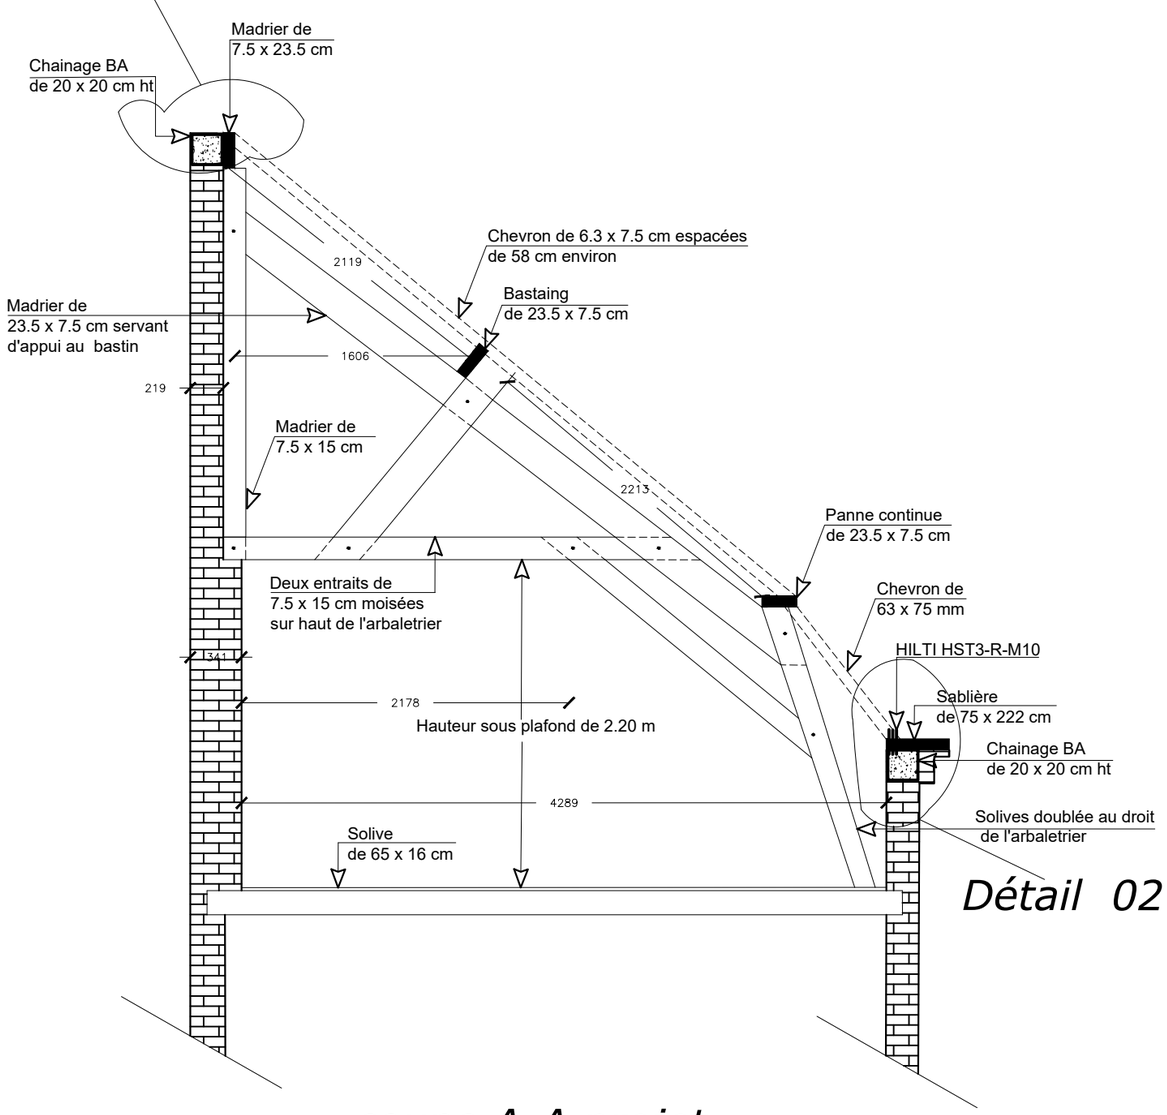

Détail 02

coupe A-A projet

Maîtrise de l'Ouvrage :
Solution travaux
Services Nord
26 Chemin d'Esquermes
59790 Ronchin

BET STRUCTURE :
J.K.F. STRUCTURE
92 Bd du GLE du Gaulle
59100 Roubaix


Création d'une charpente en bois dans un batiment existant

Dossier Etude Béton Armé

Coupe A-A existant / Coupe A-A projet


Plan N° : GO 04

Ech : S0

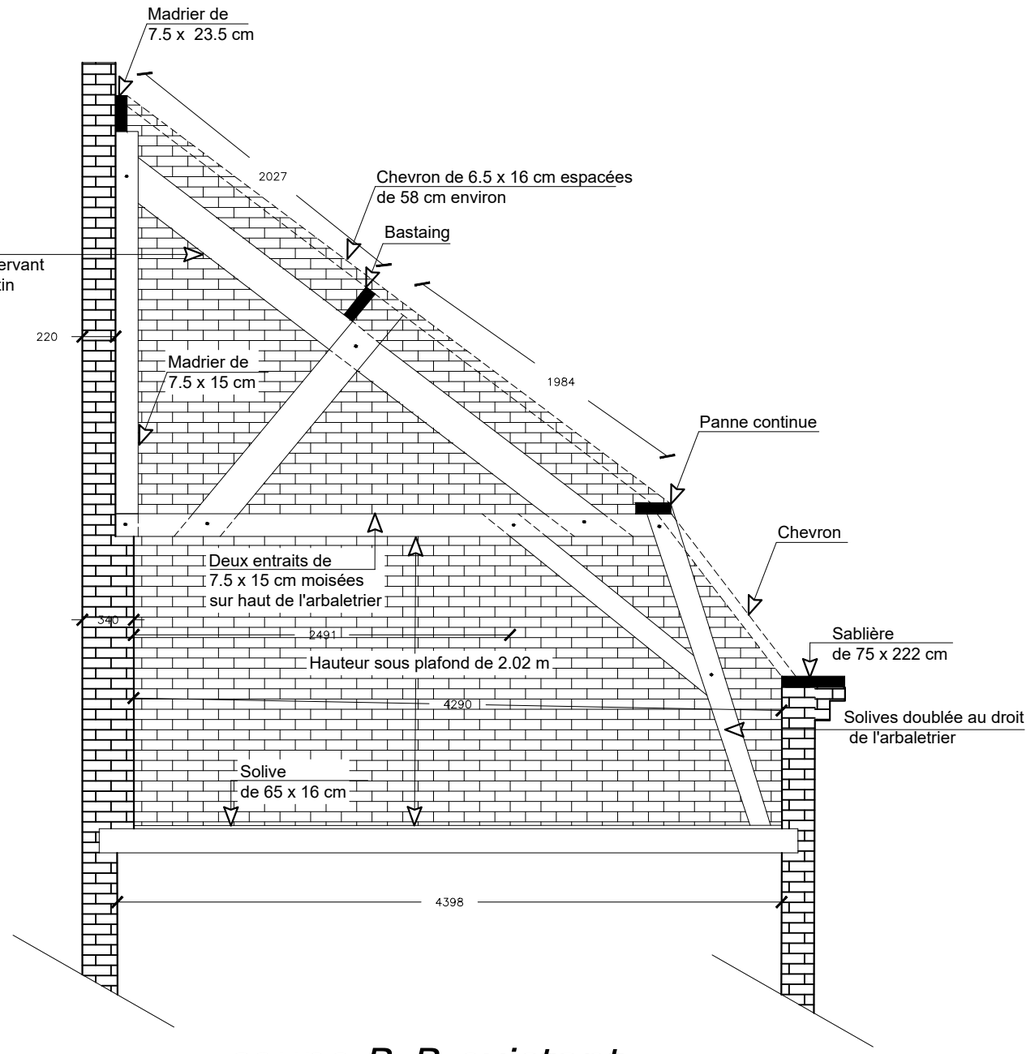

coupe B-B existant

Détail 01

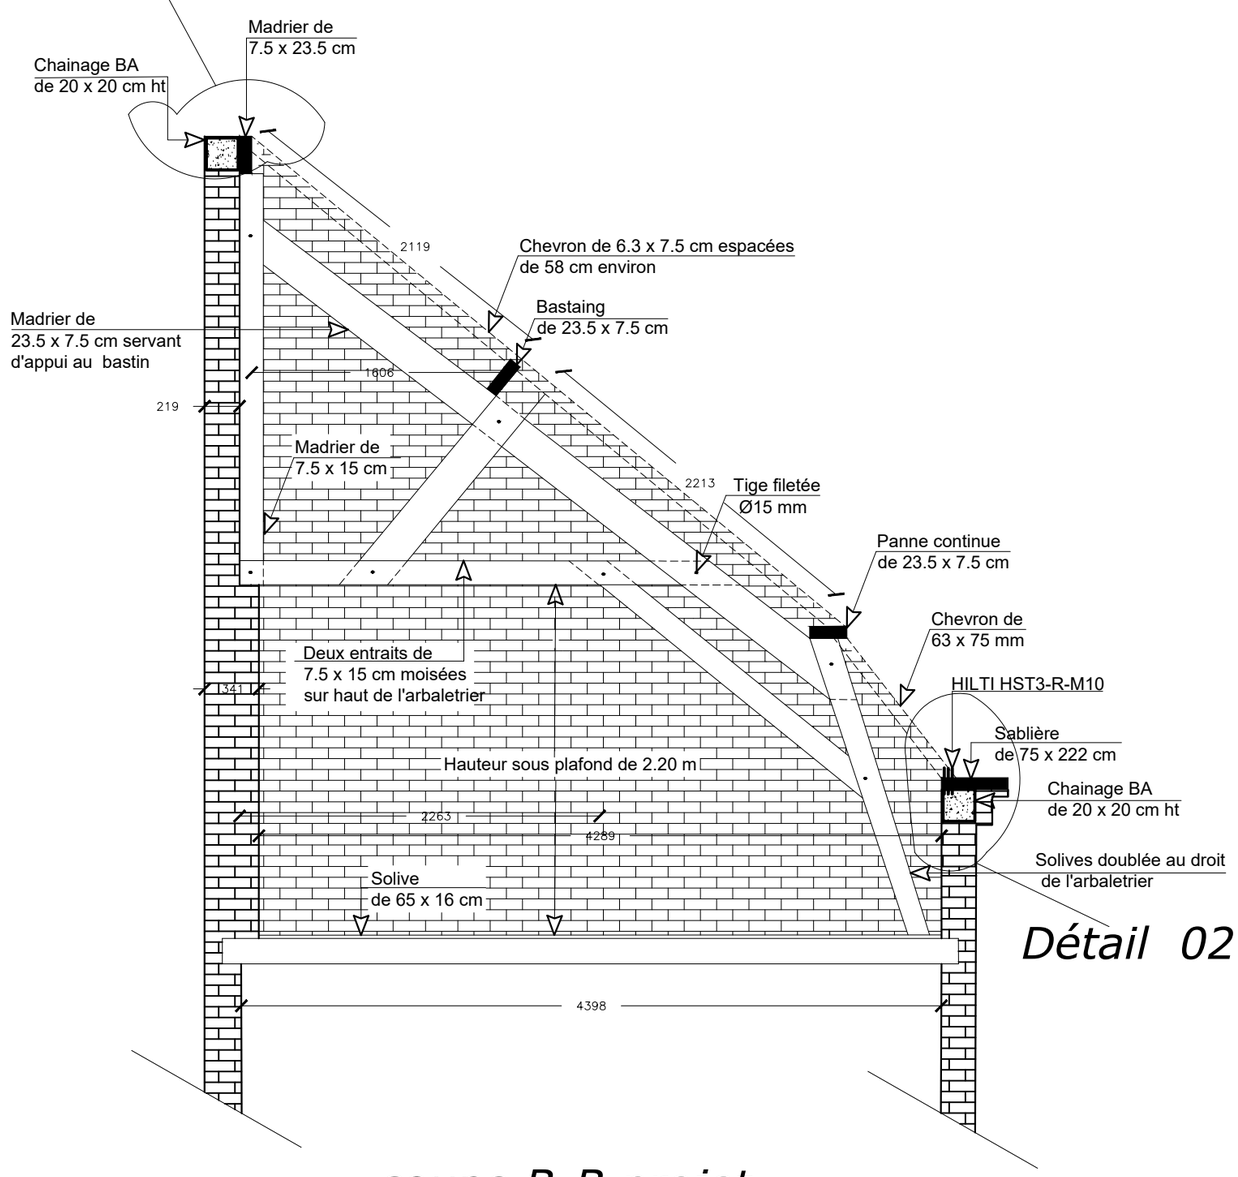

Détail 02

coupe B-B projet

Maîtrise de l'Ouvrage :
Solution travaux
Services Nord
26 Chemin d'Esquermes
59790 Ronchin

BET STRUCTURE :
J.K.F. STRUCTURE
92 Bd du GLE du Gaulle
59100 Roubaix


Création d'une charpente en bois
dans un batiment existant

Dossier Etude Béton Armé


Coupe B-B existant /Coupe B- B projet

Plan N° : GO 05

Ech : S0

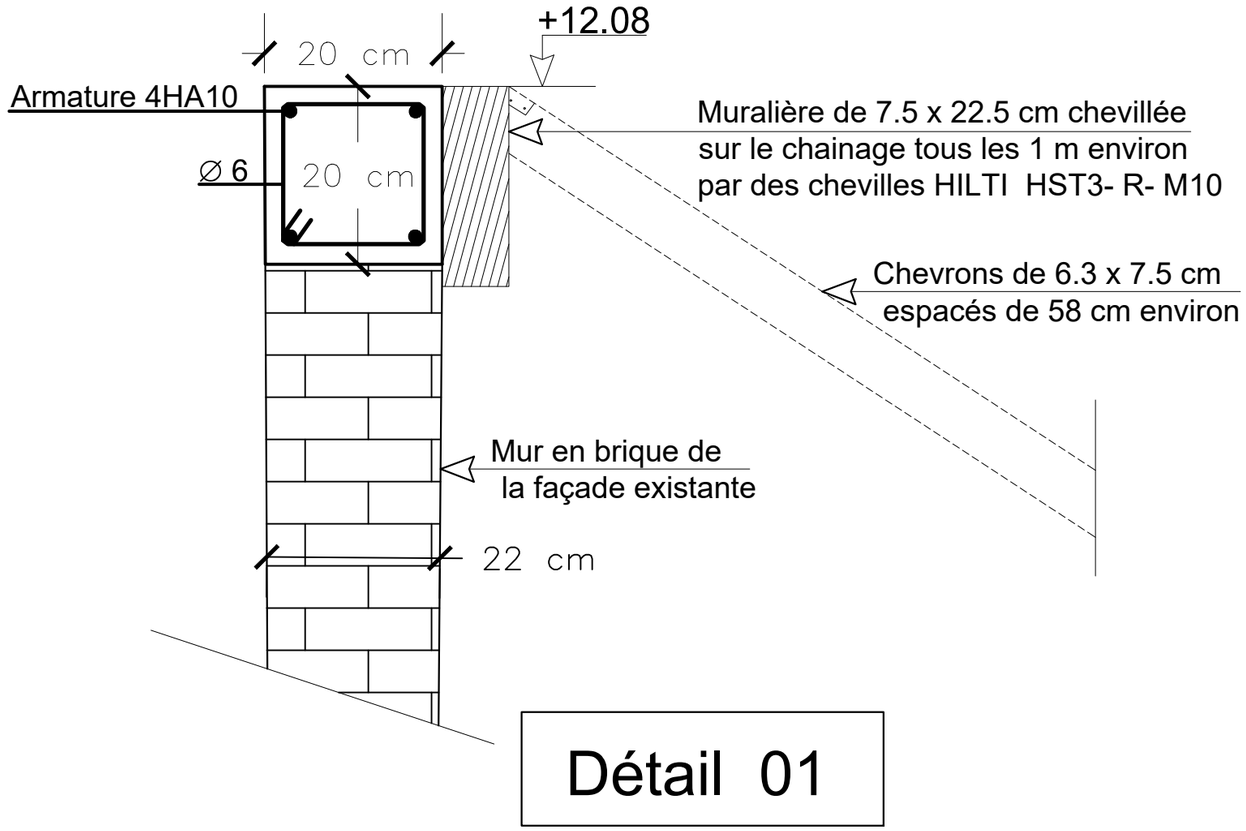

Détail 01

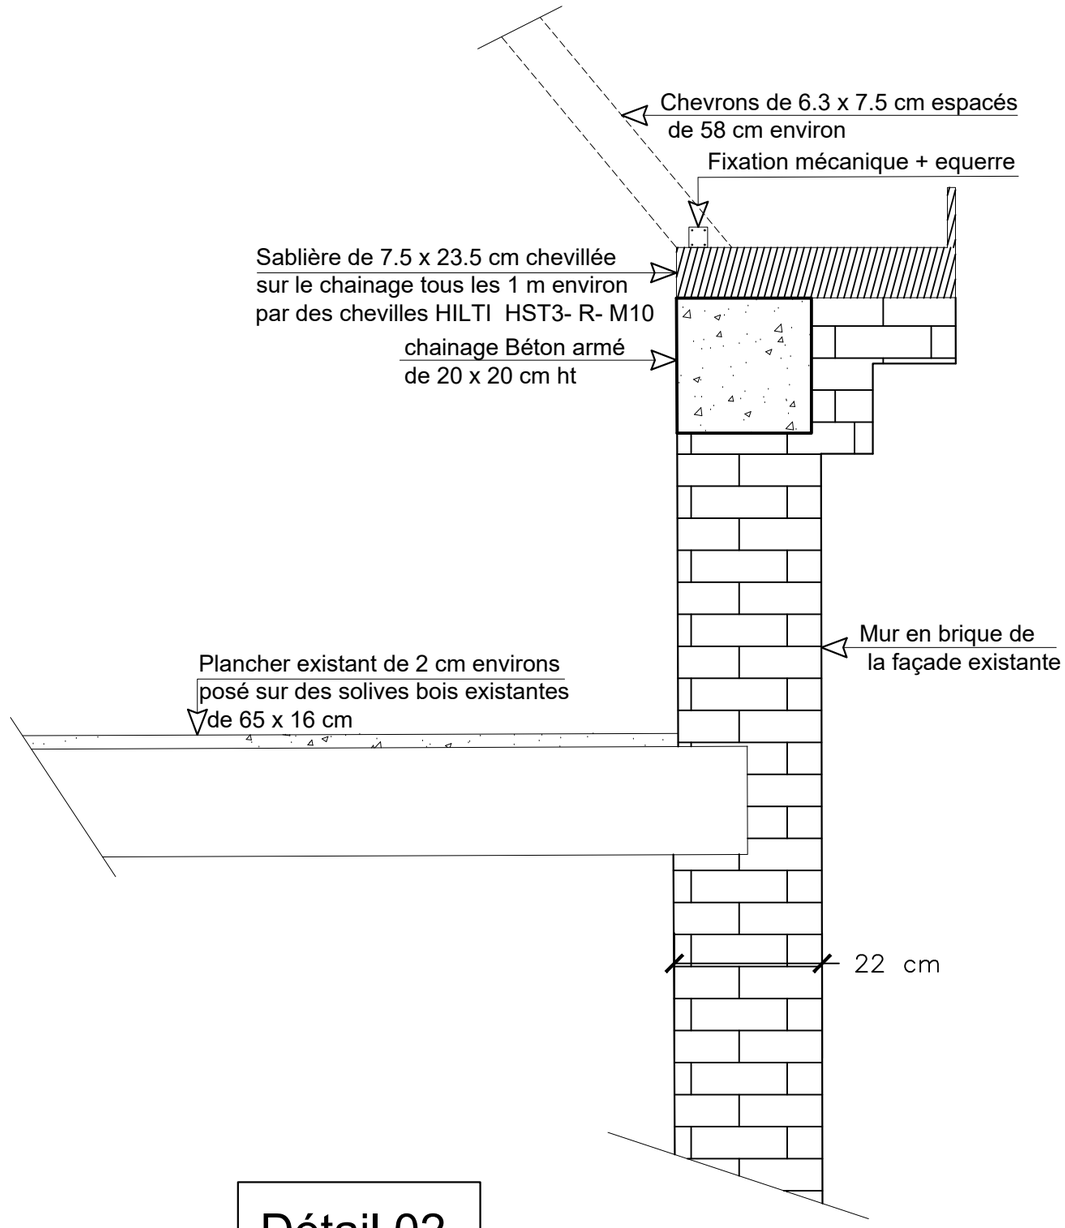

Détail 02

Maîtrise de l'Ouvrage :
Solution travaux
Services Nord
26 Chemin d'Esquermes
59790 Ronchin

BET STRUCTURE :
J.K.F. STRUCTURE
92 Bd du GLE du Gaulle
59100 Roubaix

Création d'une charpente en bois
dans un batiment existant


Dossier Etude Béton Armé

Détail 01 / Détail 02


Plan N° : GO 06


Ech : S0

Ferraillage achelets :
4 HA 10 + 3 étriés Ø 6 mm.
Avec un enrobage
de 2 cm minimum sur
les quatre faces.

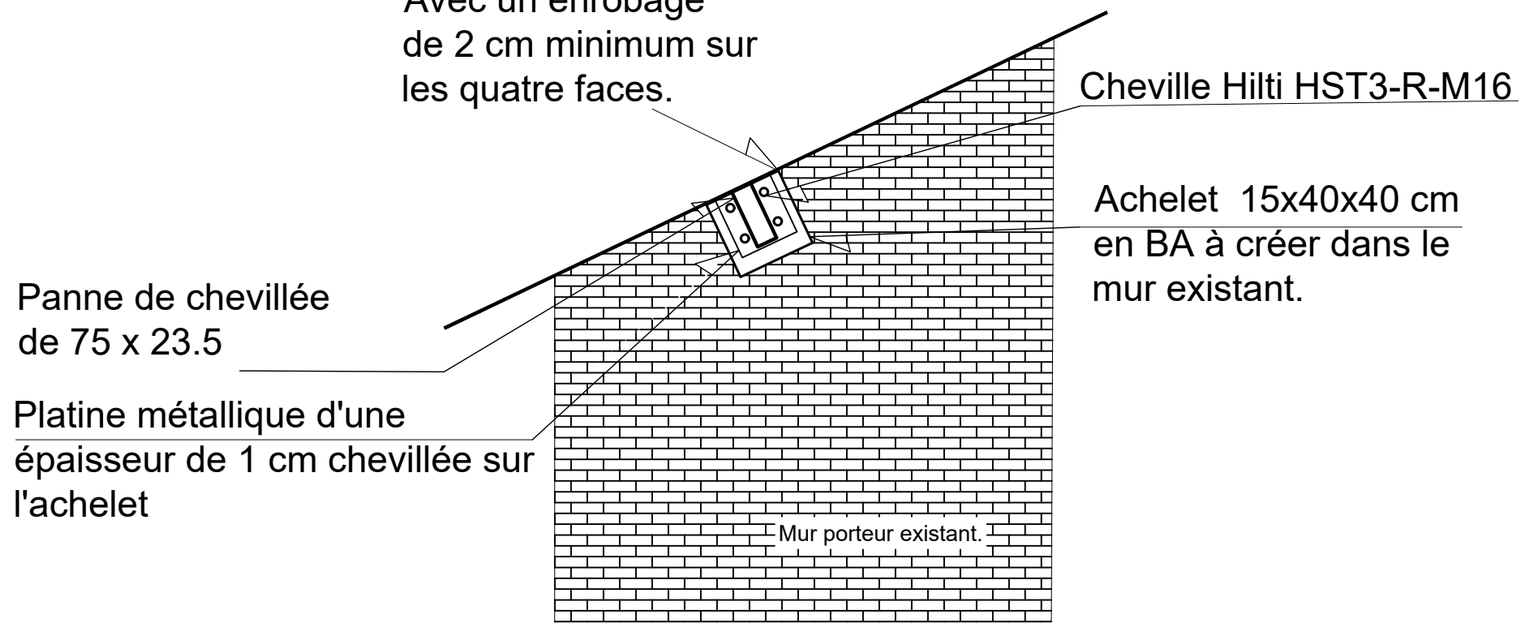

Détail 03

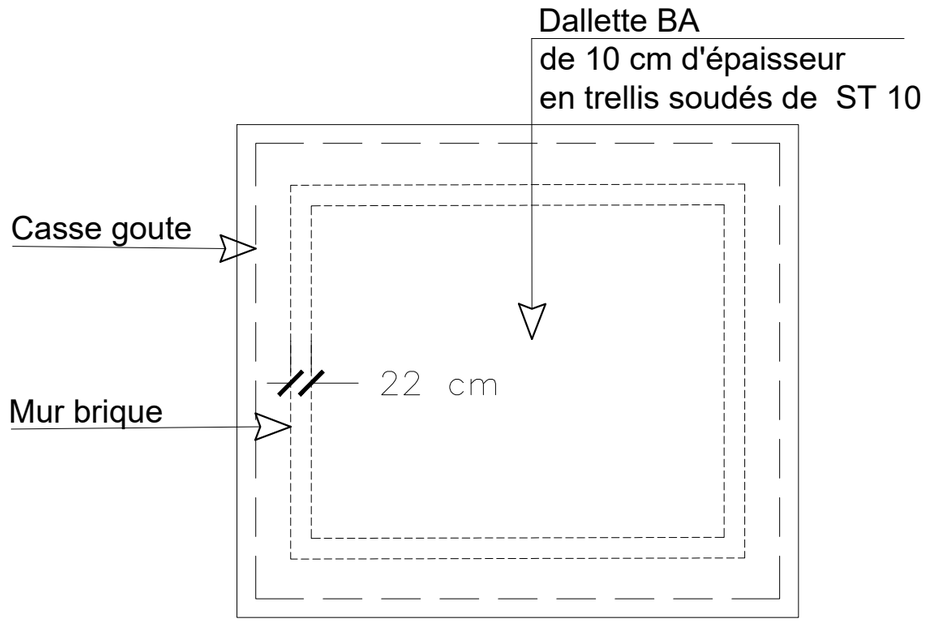

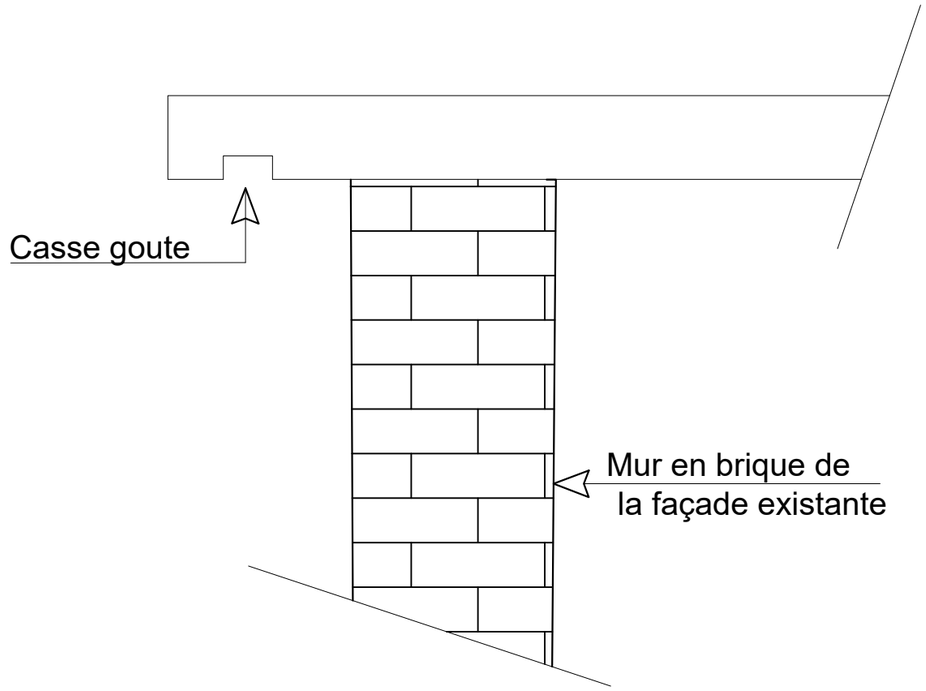

Détail 04

Maîtrise de l'Ouvrage :
Solution travaux
Services Nord
26 Chemin d'Esquermes
59790 Ronchin

BET STRUCTURE :
J.K.F. STRUCTURE
92 Bd du GLE du Gaulle
59100 Roubaix

Création d'une charpente en bois
dans un batiment existant

Dossier Etude Béton Armé

Détail 03 / Détail 04

Plan N° : GO 07

Ech : S0