

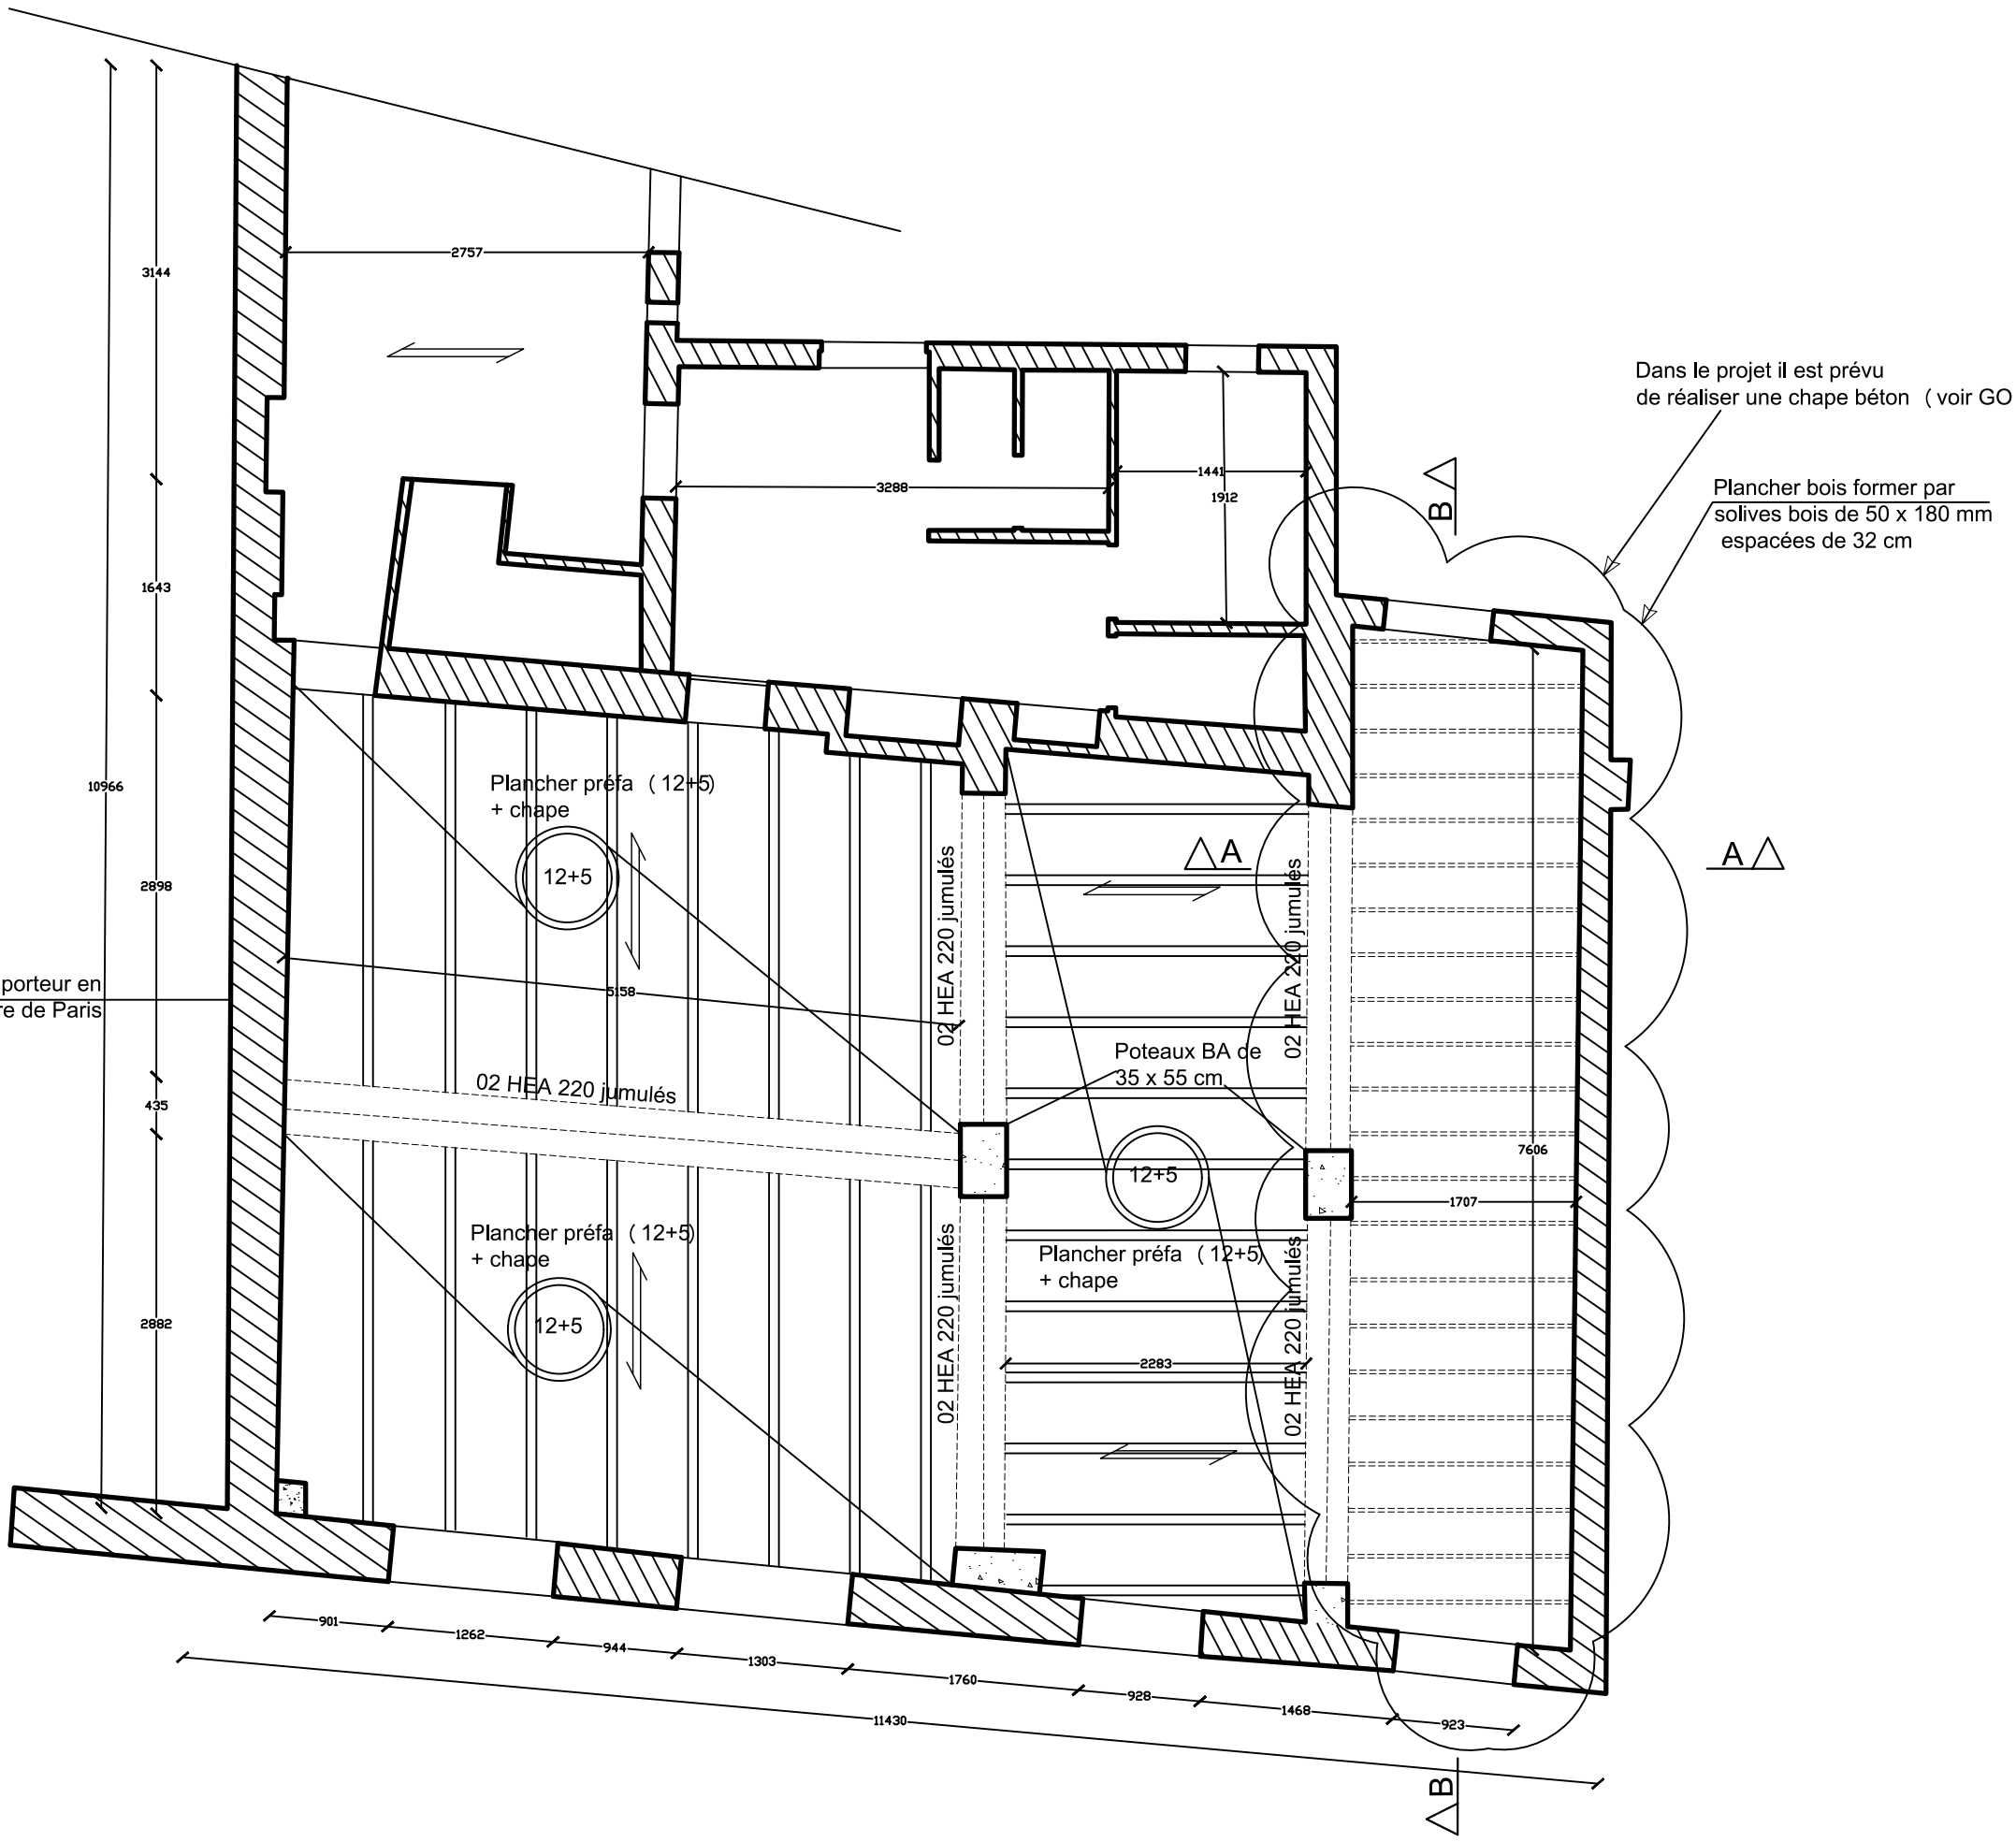


PH Rdc

Maîtrise d'Ouvrage : Mairie de montataire 7 place Auguste Génie 60160 Montataire	**BET STRUCTURE :** J.K.F. STRUCTURE 92 Bd du GLE du Gaulle 59100 Roubaix	Définition des charges maximales que peuvent supporter les planchers existants	**Dossier d'Etude Structurelle :** PH Rdc	**Plan N° : GO 01** Ech : 1/50

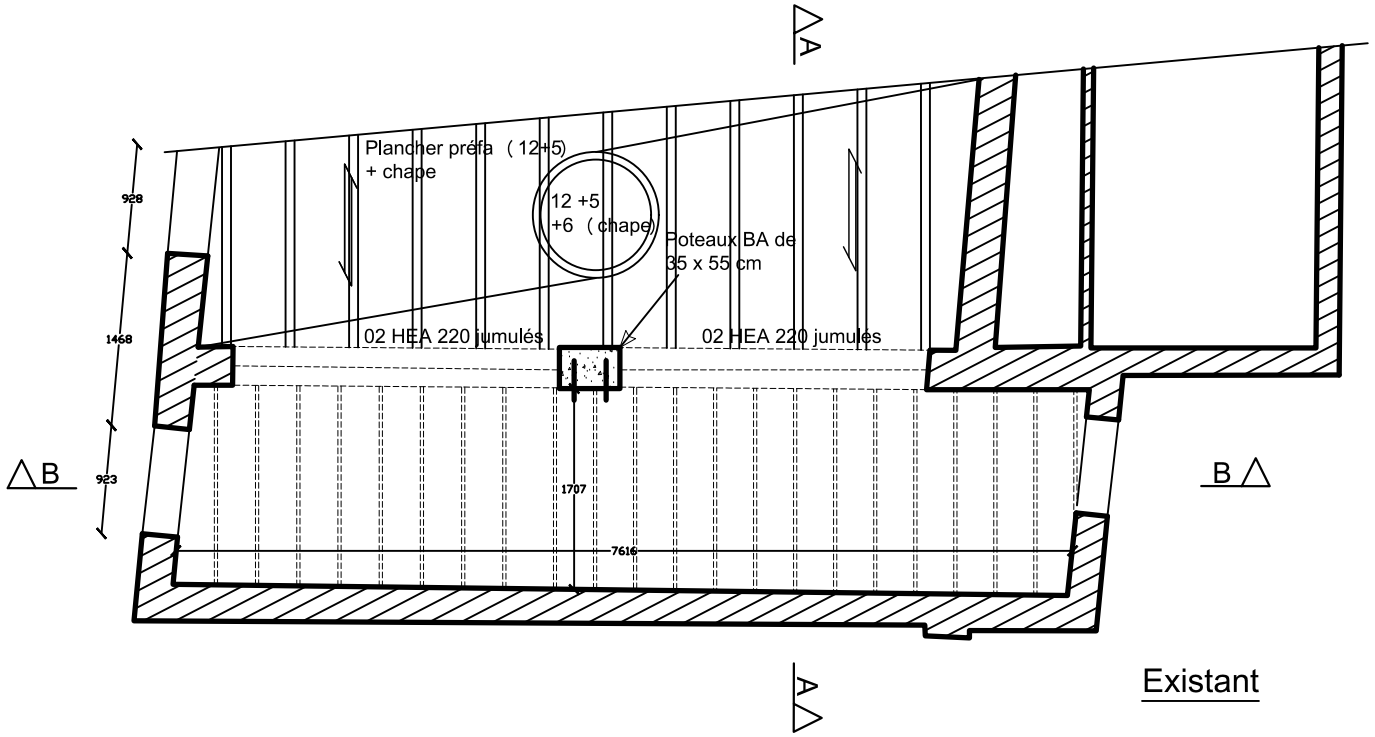

Existant

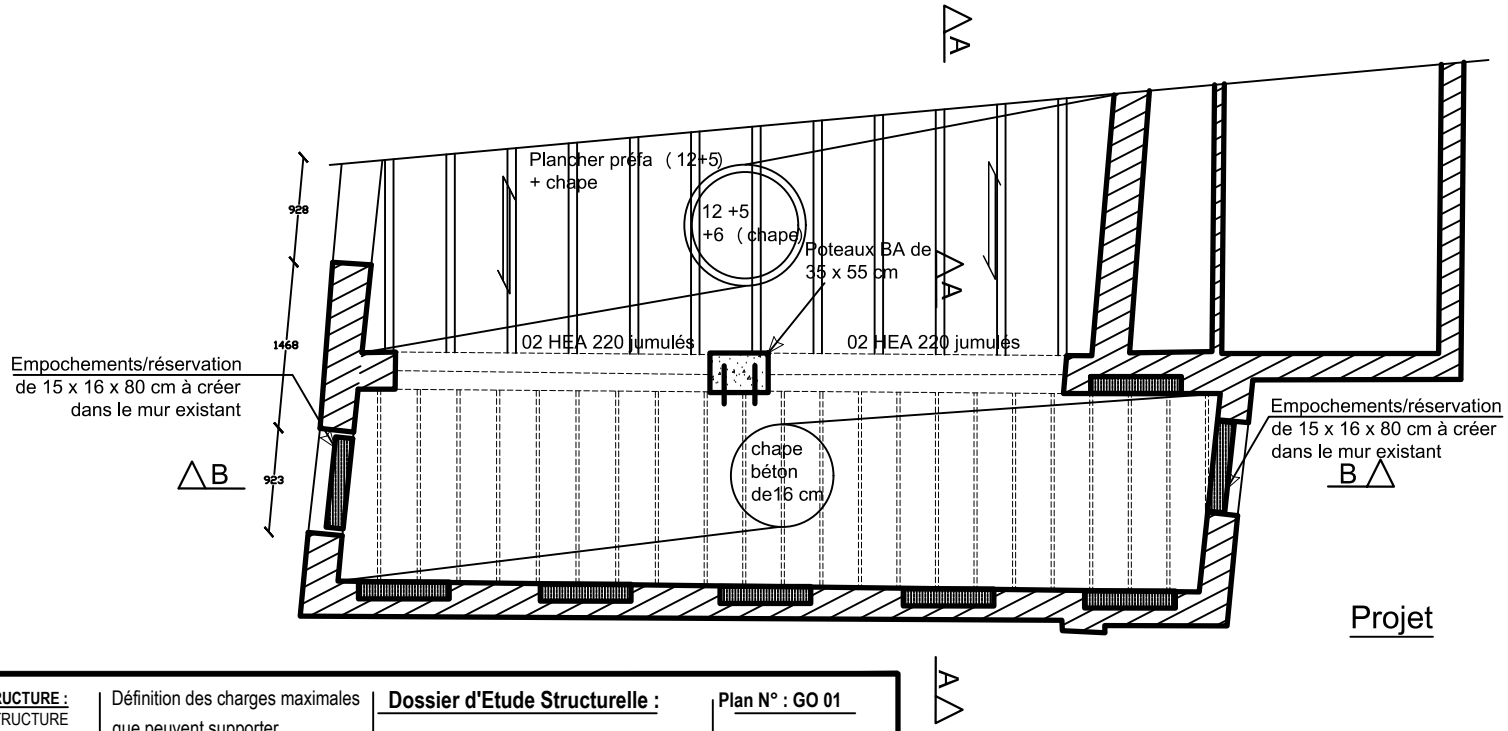

Projet


Maîtrise d'Ouvrage :
Mairie de montataire
7 place Auguste Génie
60160 Montataire

BET STRUCTURE :
J.K.F. STRUCTURE
92 Bd du GLE du Gaulle
59100 Roubaix

Définition des charges maximales que peuvent supporter les planchers existants

Dossier d'Etude Structurelle :
PH Rdc

Plan N° : GO 01
Ech : 1/75

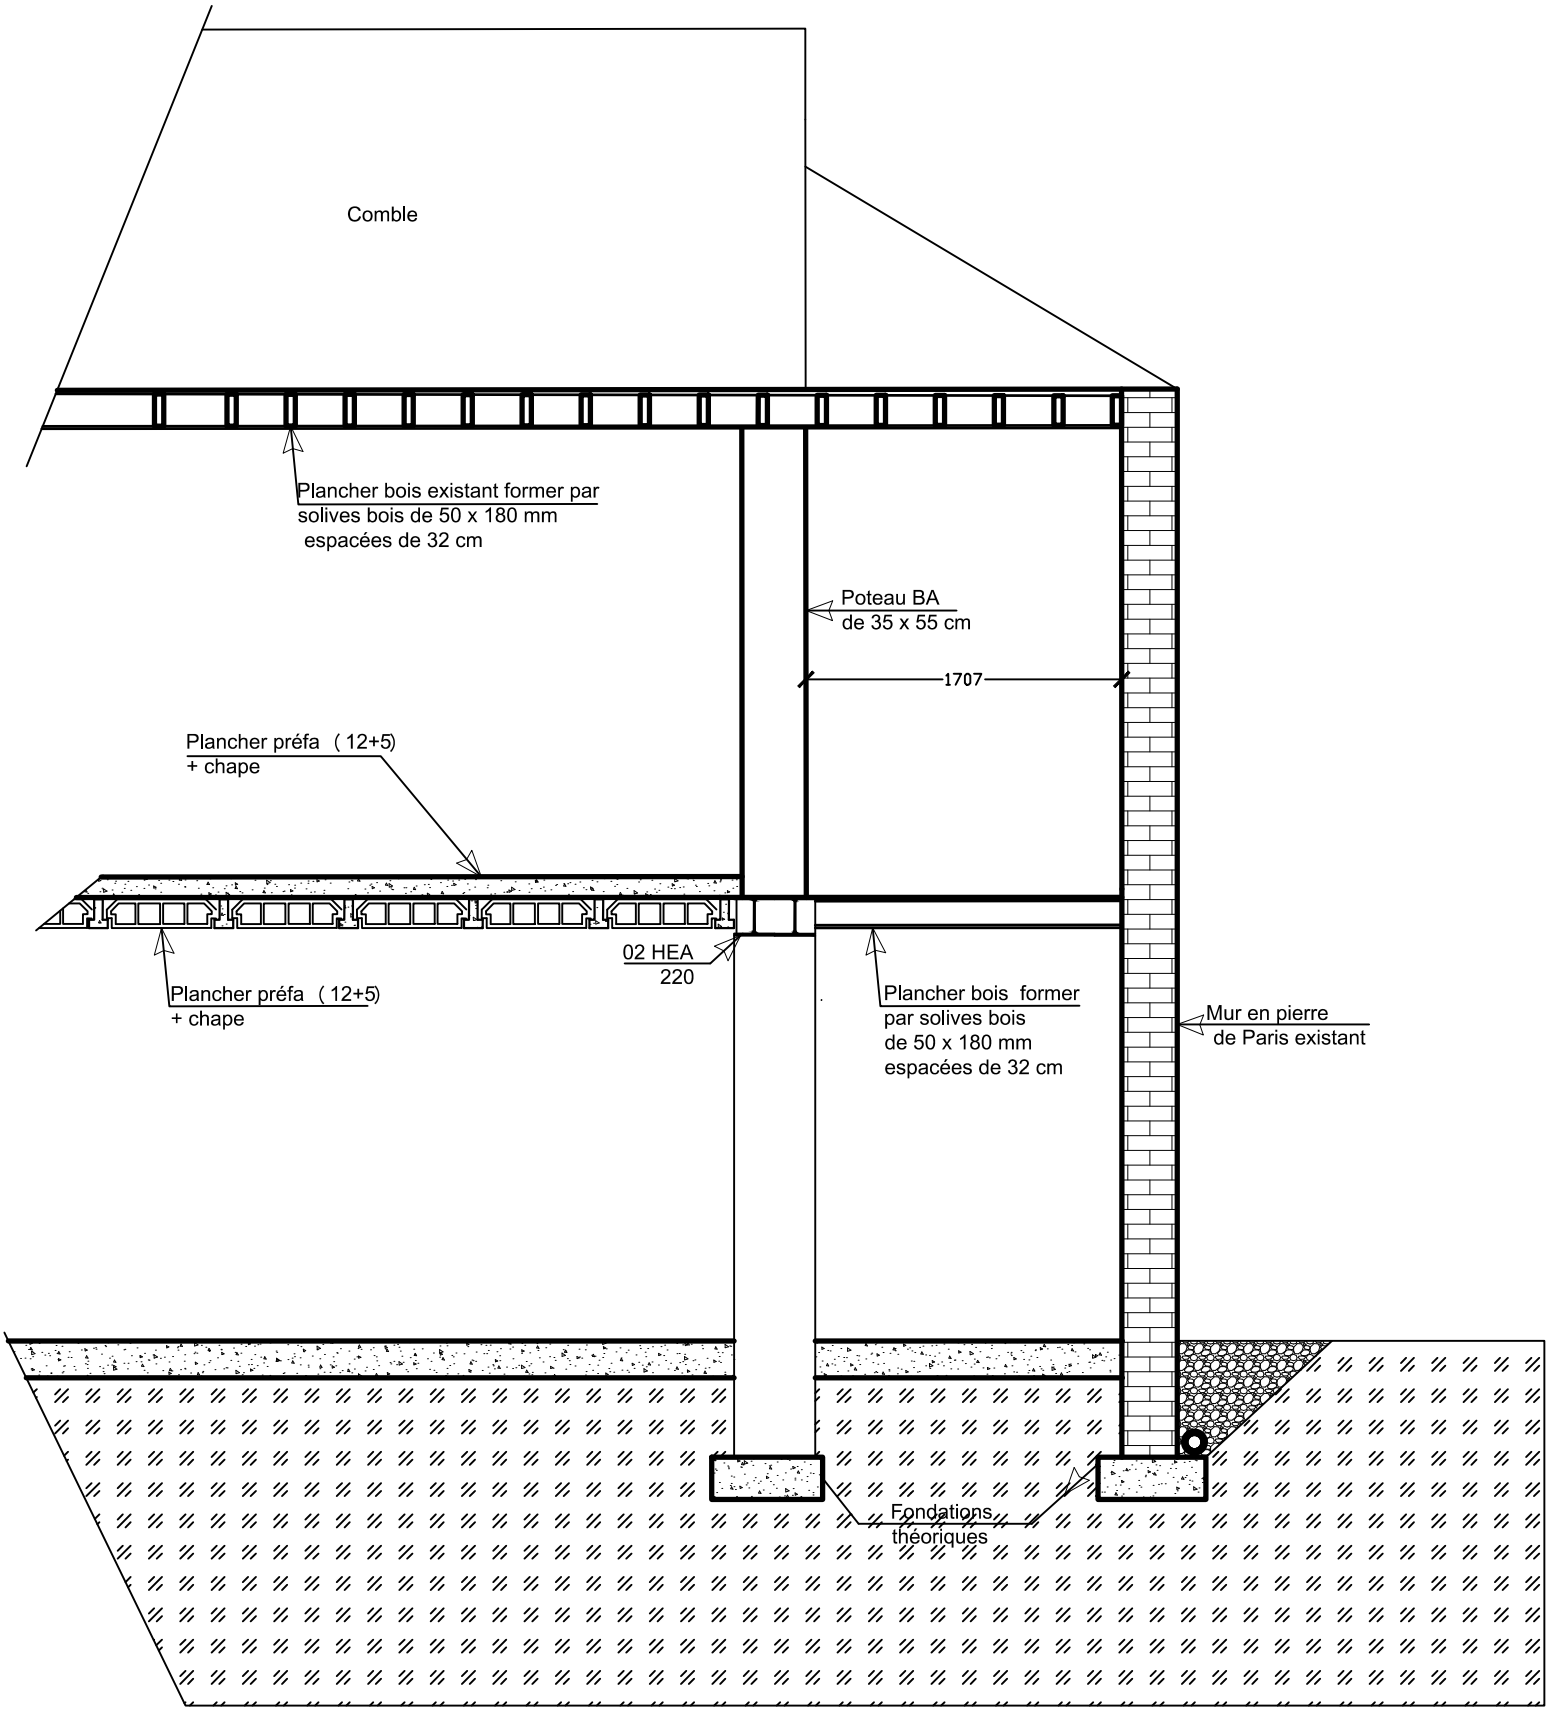

Coupe A-A existant


Maîtrise d'Ouvrage :
Mairie de montataire
7 place Auguste Génie
60160 Montataire

BET STRUCTURE :
J.K.F. STRUCTURE
92 Bd du GLE du Gaulle
59100 Roubaix

Définition des charges maximales
que peuvent supporter
les planchers existants

Dossier d'Etude Structurelle :
Coupe A-A existant

Plan N° : GO 03
Ech : 1/50

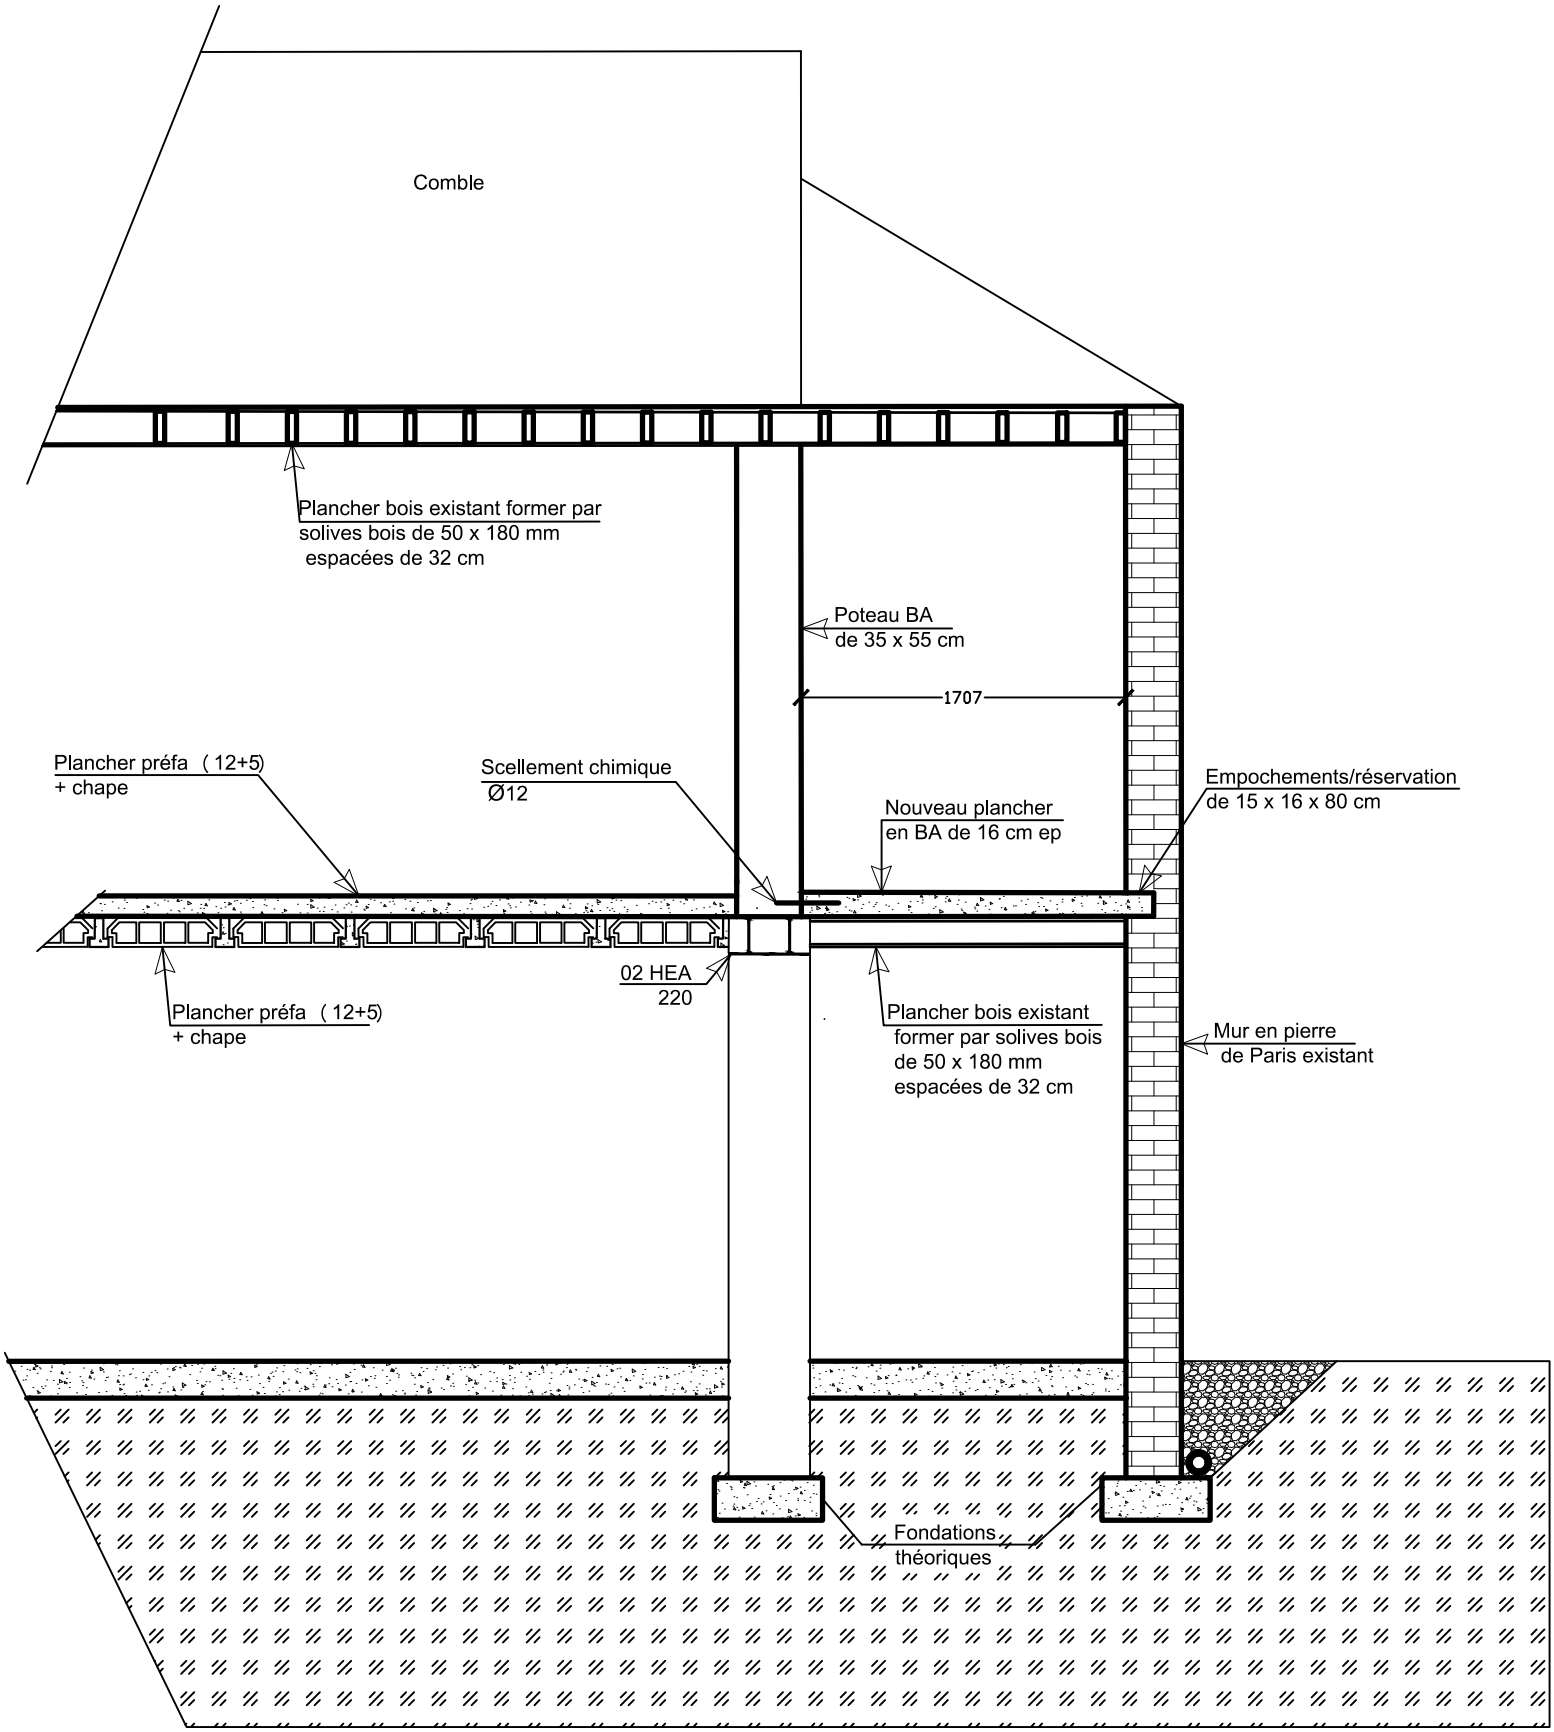

Coupe A-A projet


Maîtrise d'Ouvrage :
Mairie de montataire
7 place Auguste Génie
60160 Montataire

BET STRUCTURE :
J.K.F. STRUCTURE
92 Bd du GLE du Gaulle
59100 Roubaix

Définition des charges maximales que peuvent supporter les planchers existants

Dossier d'Etude Structurelle :
Coupe A-A projet

Plan N° : GO 03
Ech : 1/50

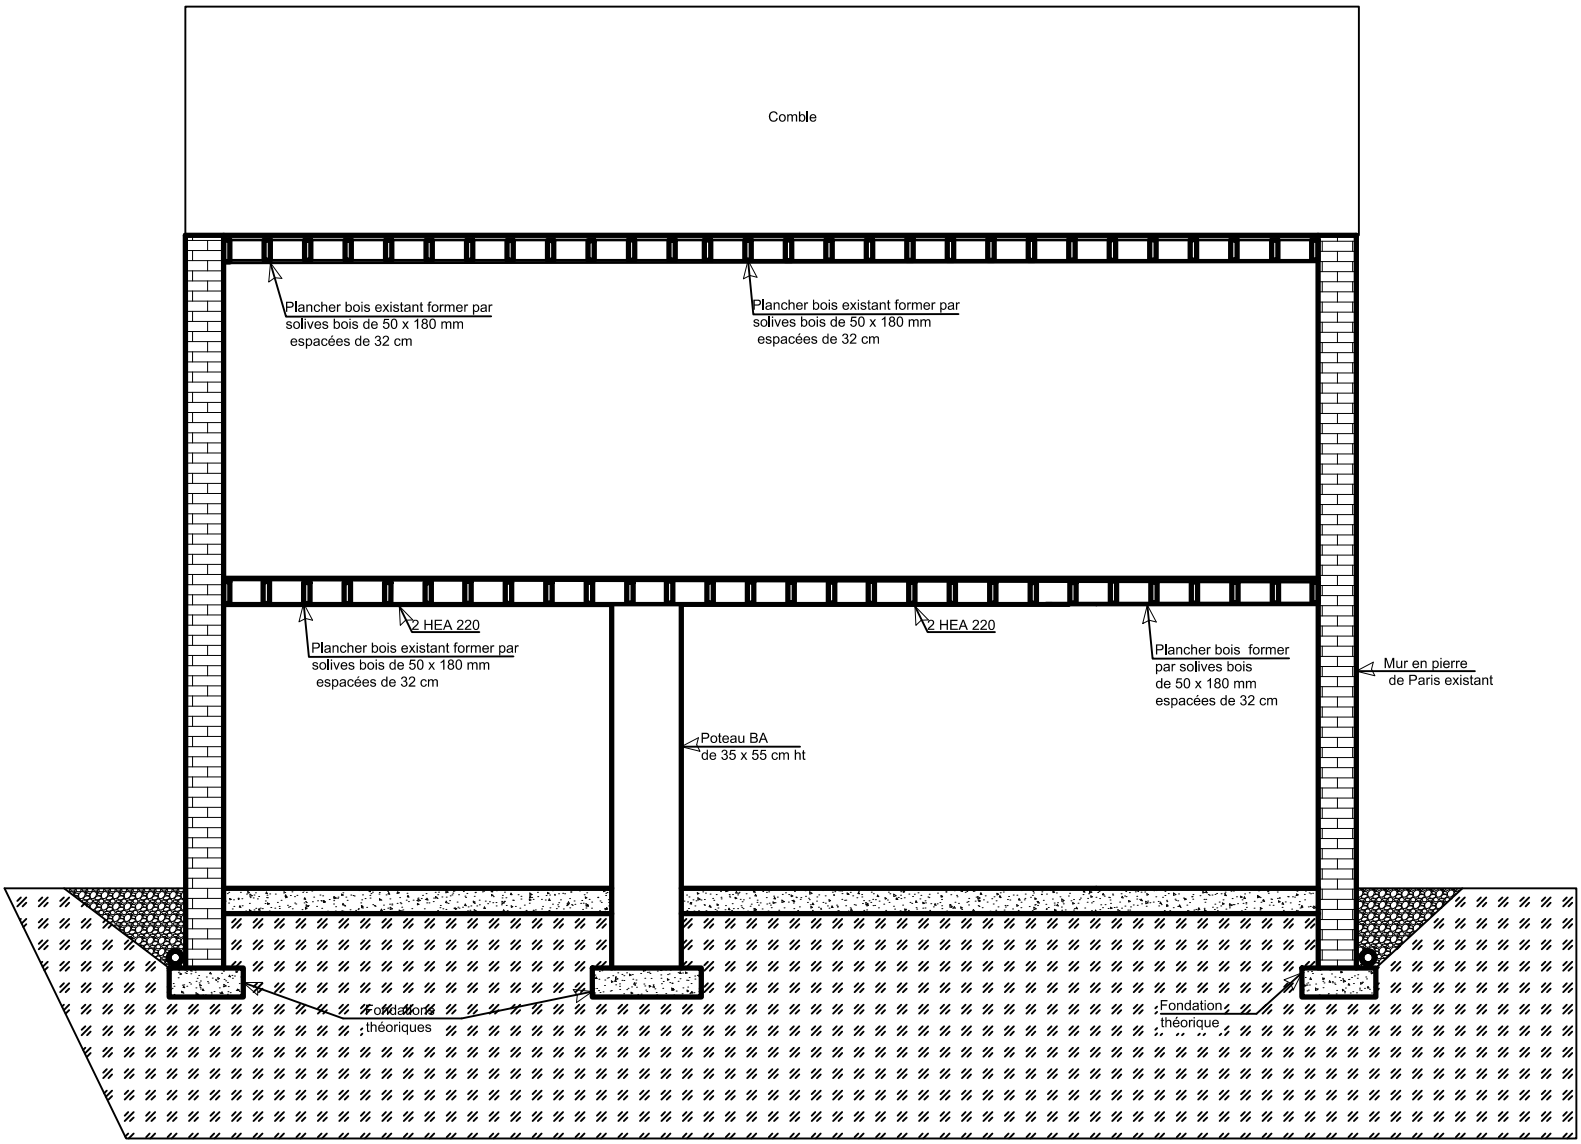

Coupe B-B existant

Maîtrise d'Ouvrage :
Mairie de montataire
7 place Auguste Génie
60160 Montataire

BET STRUCTURE :
J.K.F. STRUCTURE
92 Bd du GLE du Gaulle
59100 Roubaix

Définition des charges maximales que peuvent supporter les planchers existants

Dossier d'Etude Structurelle :
Coupe B-B existant


Plan N° : GO 04
Ech : 1/50

Empochement /réservation

Mur Brique existant


Hypothèses de calculs :

FeE500
Béton fc25 = 25 Mpa
Enrobage e = 2 cm
Charge d'exploitation Q = 500 daN/m²
Treillis soudé : TS ST35

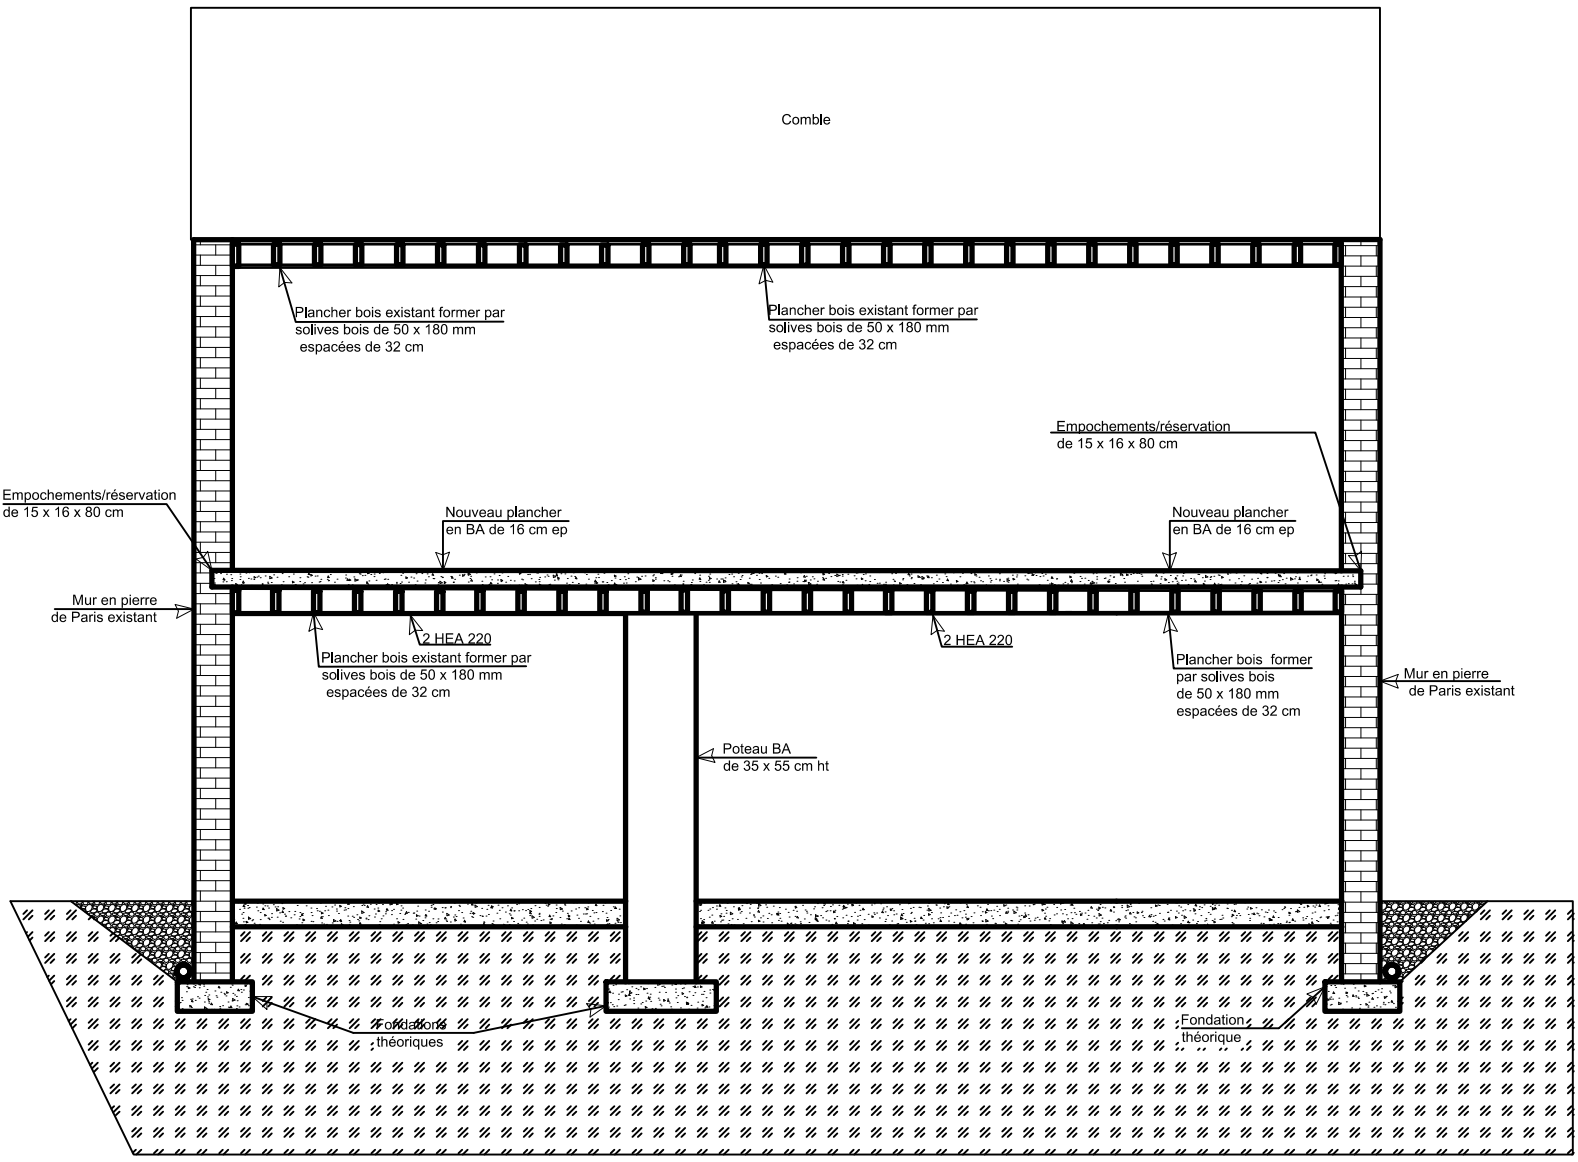


Coupe B-B projet

Maîtrise d'Ouvrage : Mairie de montataire 7 place Auguste Génie 60160 Montataire	**BET STRUCTURE :** J.K.F. STRUCTURE 92 Bd du GLE du Gaulle 59100 Roubaix	Définition des charges maximales que peuvent supporter les planchers existants	**Dossier d'Etude Structurelle :** Coupe B-B projet	**Plan N° : GO 05** Ech : 1/50

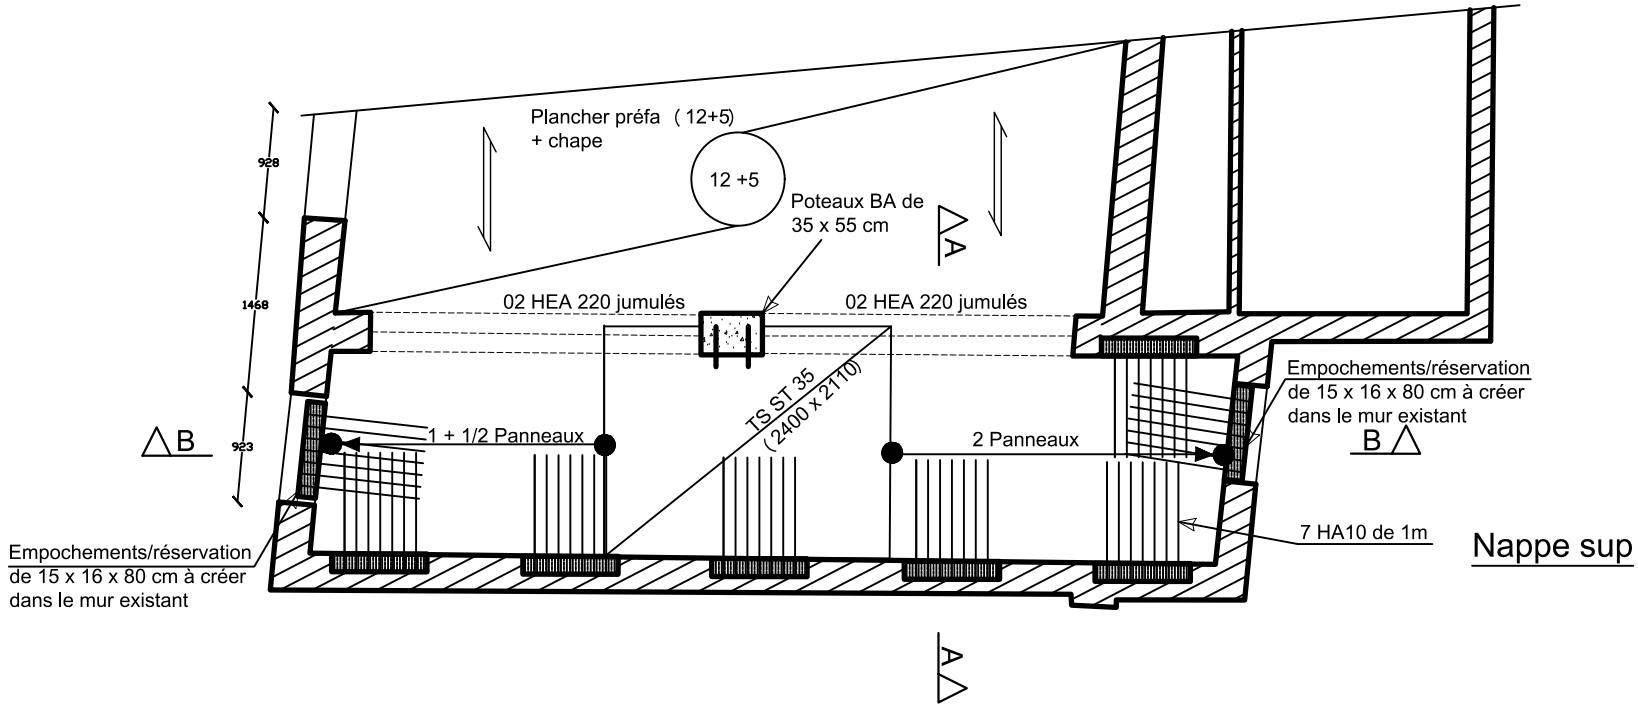

Nappe sup

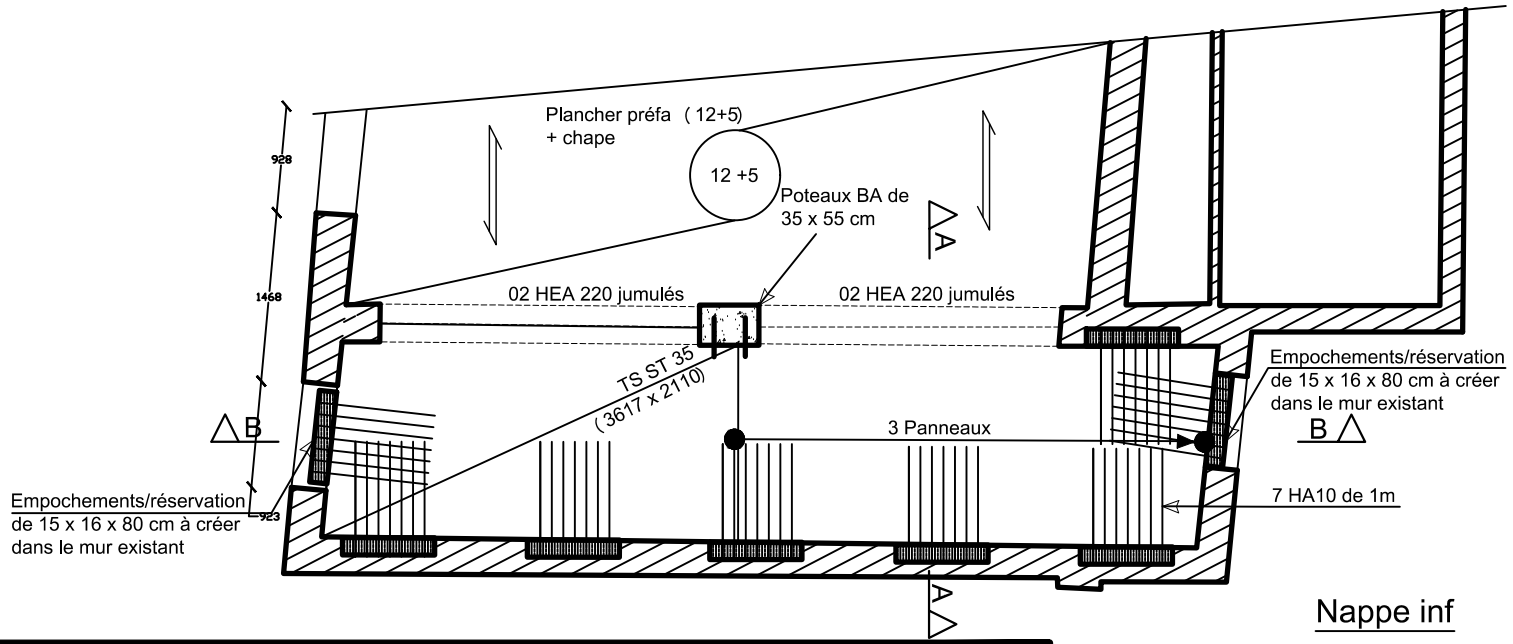

Nappe inf

Maîtrise d'Ouvrage :
Mairie de montataire
7 place Auguste Génie
60160 Montataire

BET STRUCTURE :
J.K.F. STRUCTURE
92 Bd du GLE du Gaulle
59100 Roubaix

Définition des charges maximales
que peuvent supporter
les planchers existants

Dossier d'Etude Structurelle :
Feraillage dalle
Nappe inférieure/Nappe supérieure

Plan N° : GO 06

Ech : 1/50