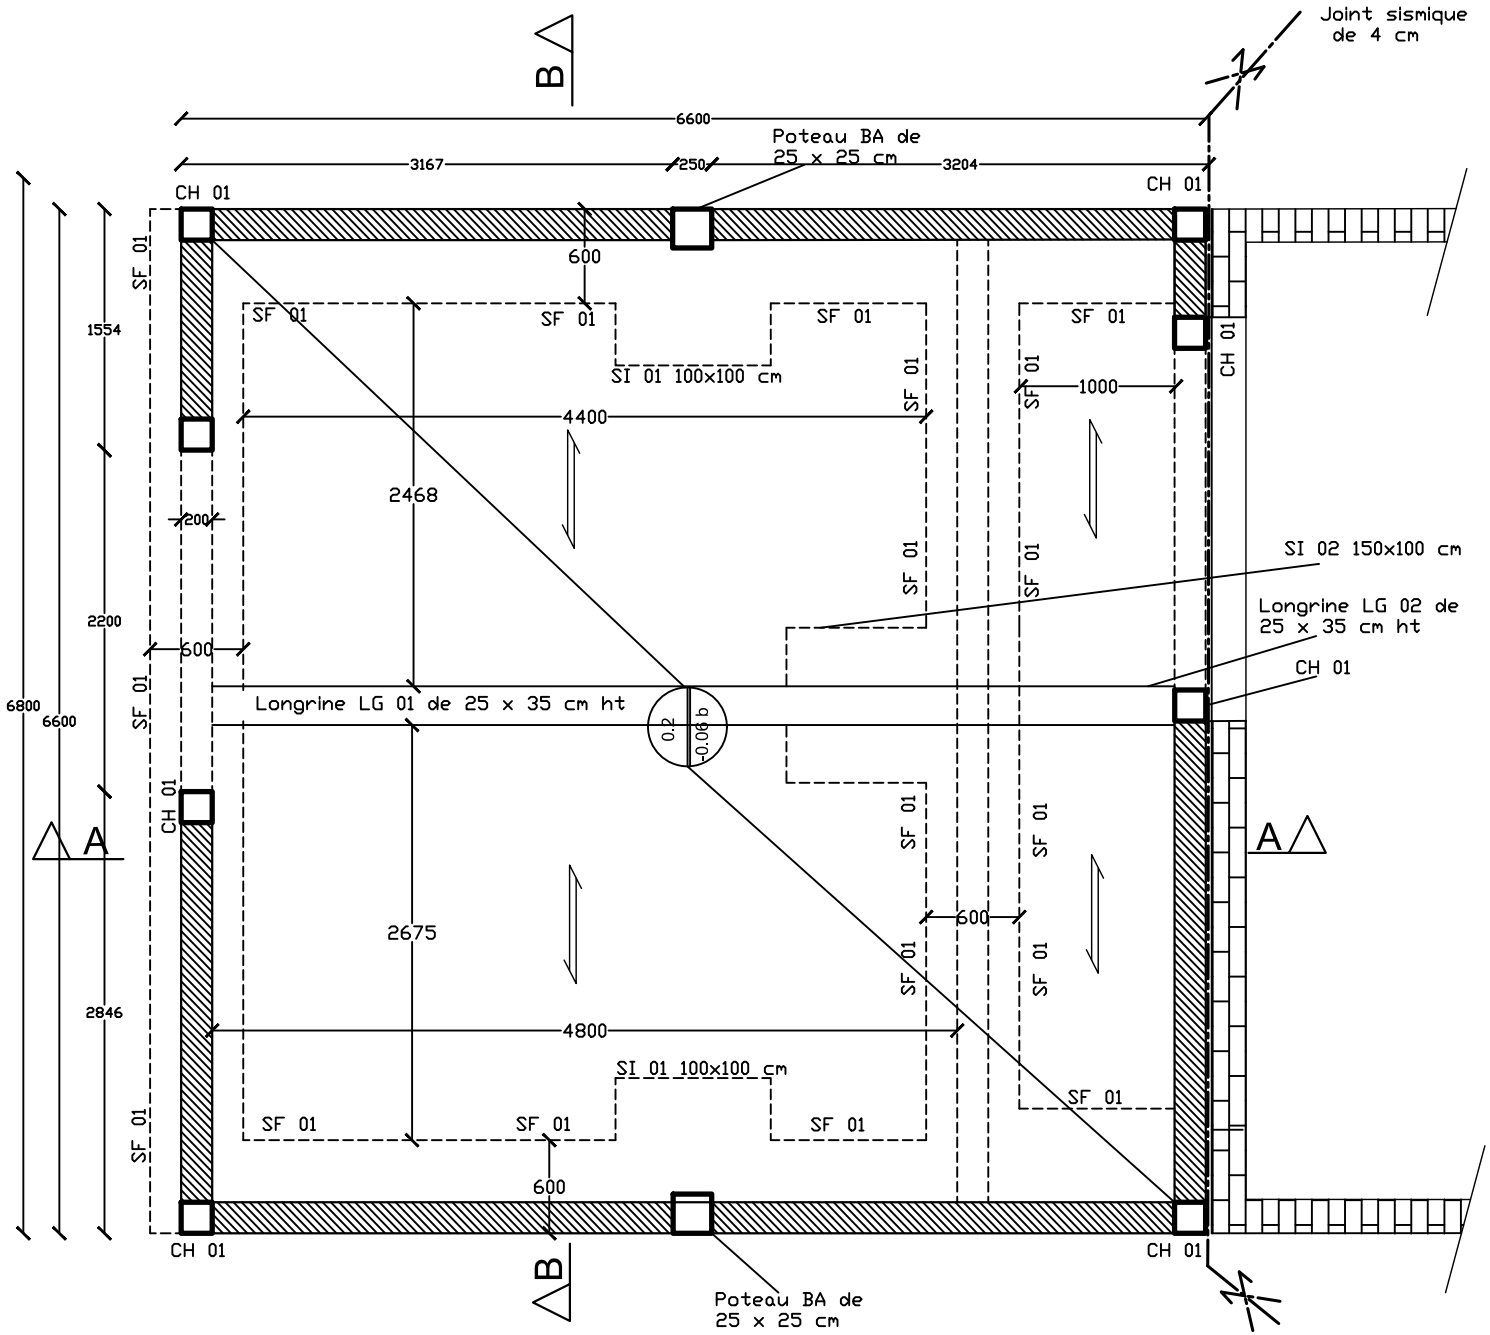


Maçonnerie BBM e = 20cm

Mur Brique existant

CH 01: Chainage vertical BA 20 x 20 cm ht

CH 02: Chainage horizontal BA 20 x 20 cm ht


P 01 : Poteau BA 25 x 25 cm ht

LG 01 : Longrine BA 25 x 35 cm ht

LG 02 : Longrine BA 25 x 35 cm ht

Hypothèses de calculs :

Zone sismique (zone 03)
bâtiment de catégorie II,
la structure est soumise à une
conception parasismique.

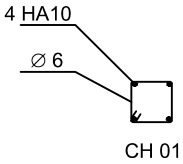

Zone de neige : A1


Zone du vent : zone 3

Conformément à l'étude de sols,

les fondations sont réalisées par

des fondations superficielles

Charges d'exploitation Q = 1.5 Kn / m²

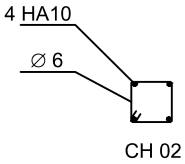

SF 01 : Semelle Filante 60 x 25 cm ht.

SF 02 : Semelle Filante excentrée 60 x 25 cm ht.

Sl 01 : Semelle Isolée 100 x 100 cm ht.

Sl 02 : Semelle Isolée 150 x 100 cm ht.

Maîtrise d'Ouvrage :
M Leveque et Mme Lenquette
21 Rue Leon Gambetta
59730 St- Pithon

BET STRUCTURE :
J.K.F. STRUCTURE
92 Bd du GLE du Gaulle
59100 Roubaix


Etude BA pour la création d'une extension

Dossier d'Etude Structurelle :


Plan de fondations

Plan N° : GO 01

Ech : 1/50

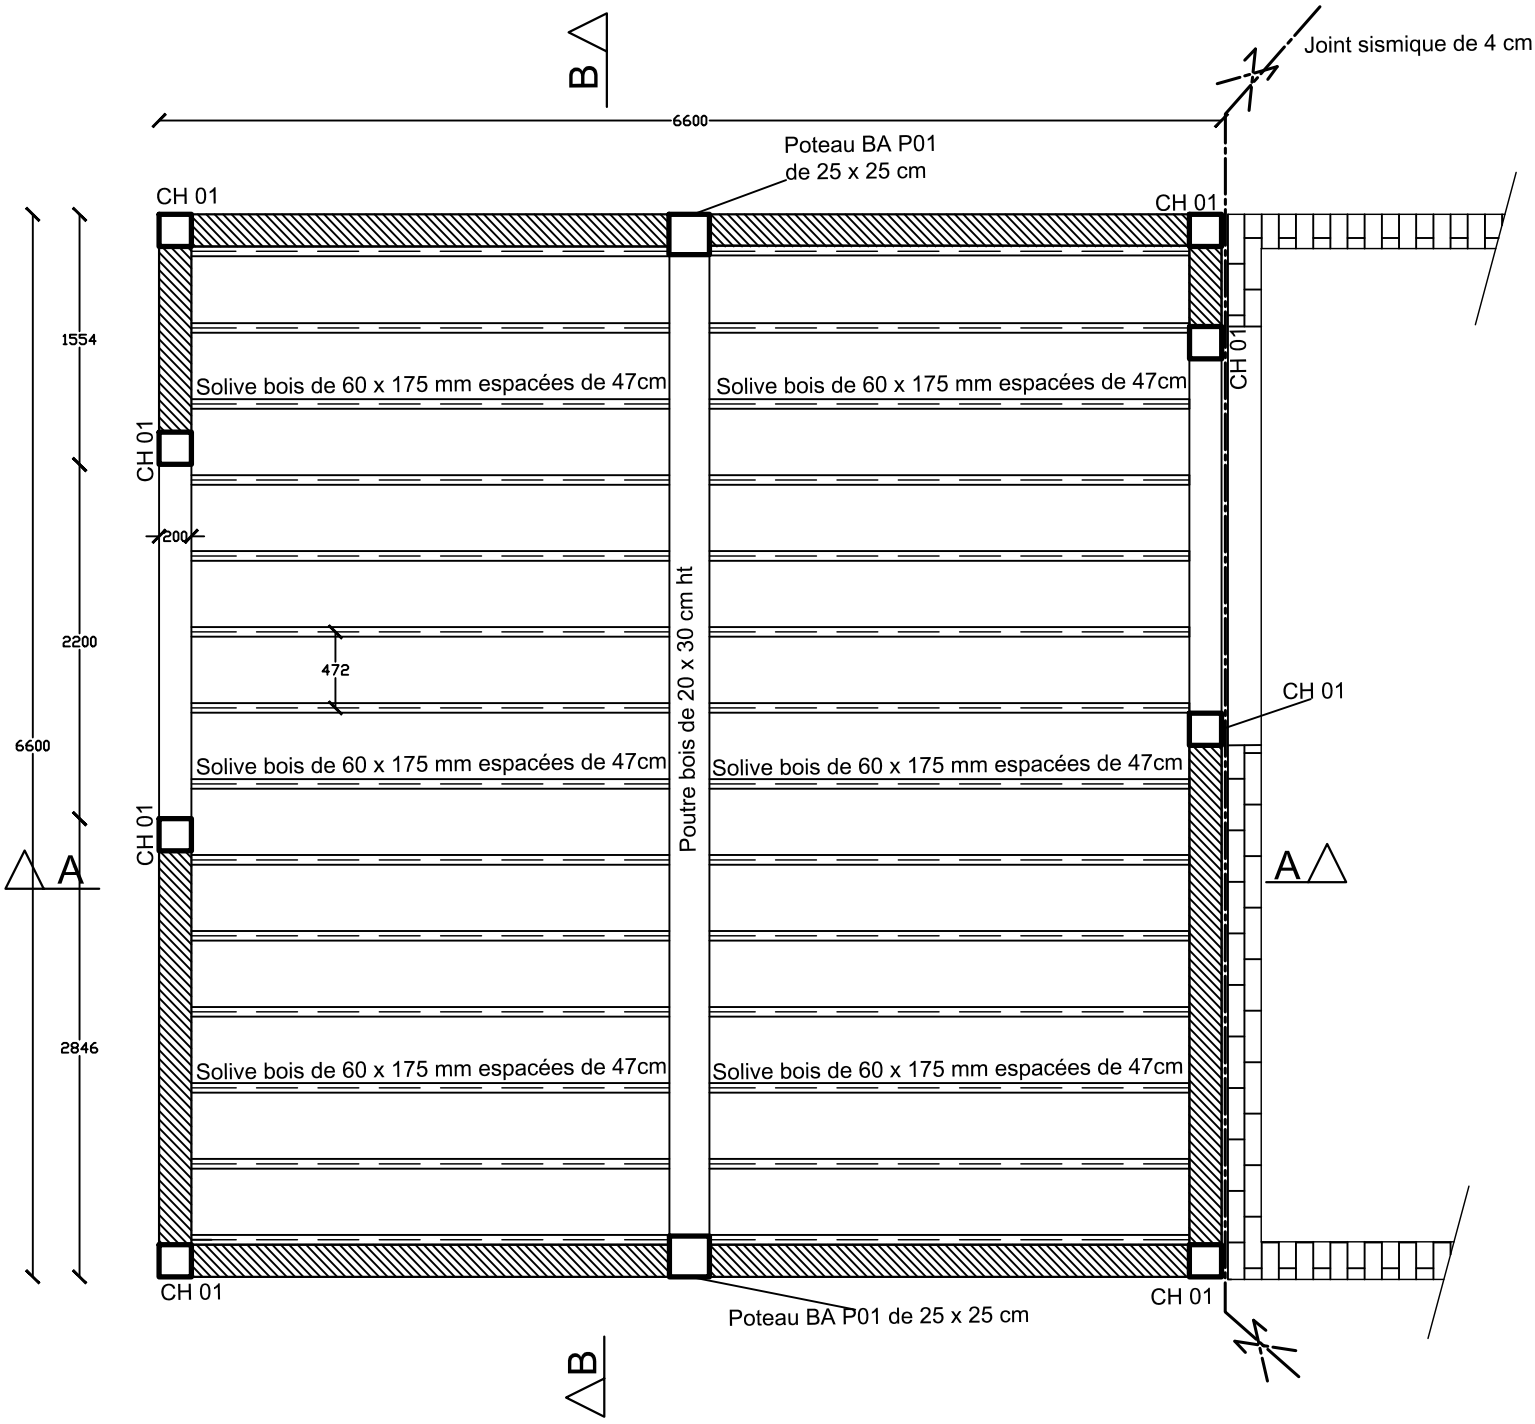


Maîtrise d'Ouvrage : M Leveque et Mme Lenquette 21 Rue Leon Gambetta 59730 St- Pithon	**BET STRUCTURE :** J.K.F. STRUCTURE 92 Bd du GLE du Gaulle 59100 Roubaix	Etude BA pour la création d'une extension	**Dossier d'Etude Structurelle :** Ph rdc	**Plan N° : GO 02** Ech : 1/50

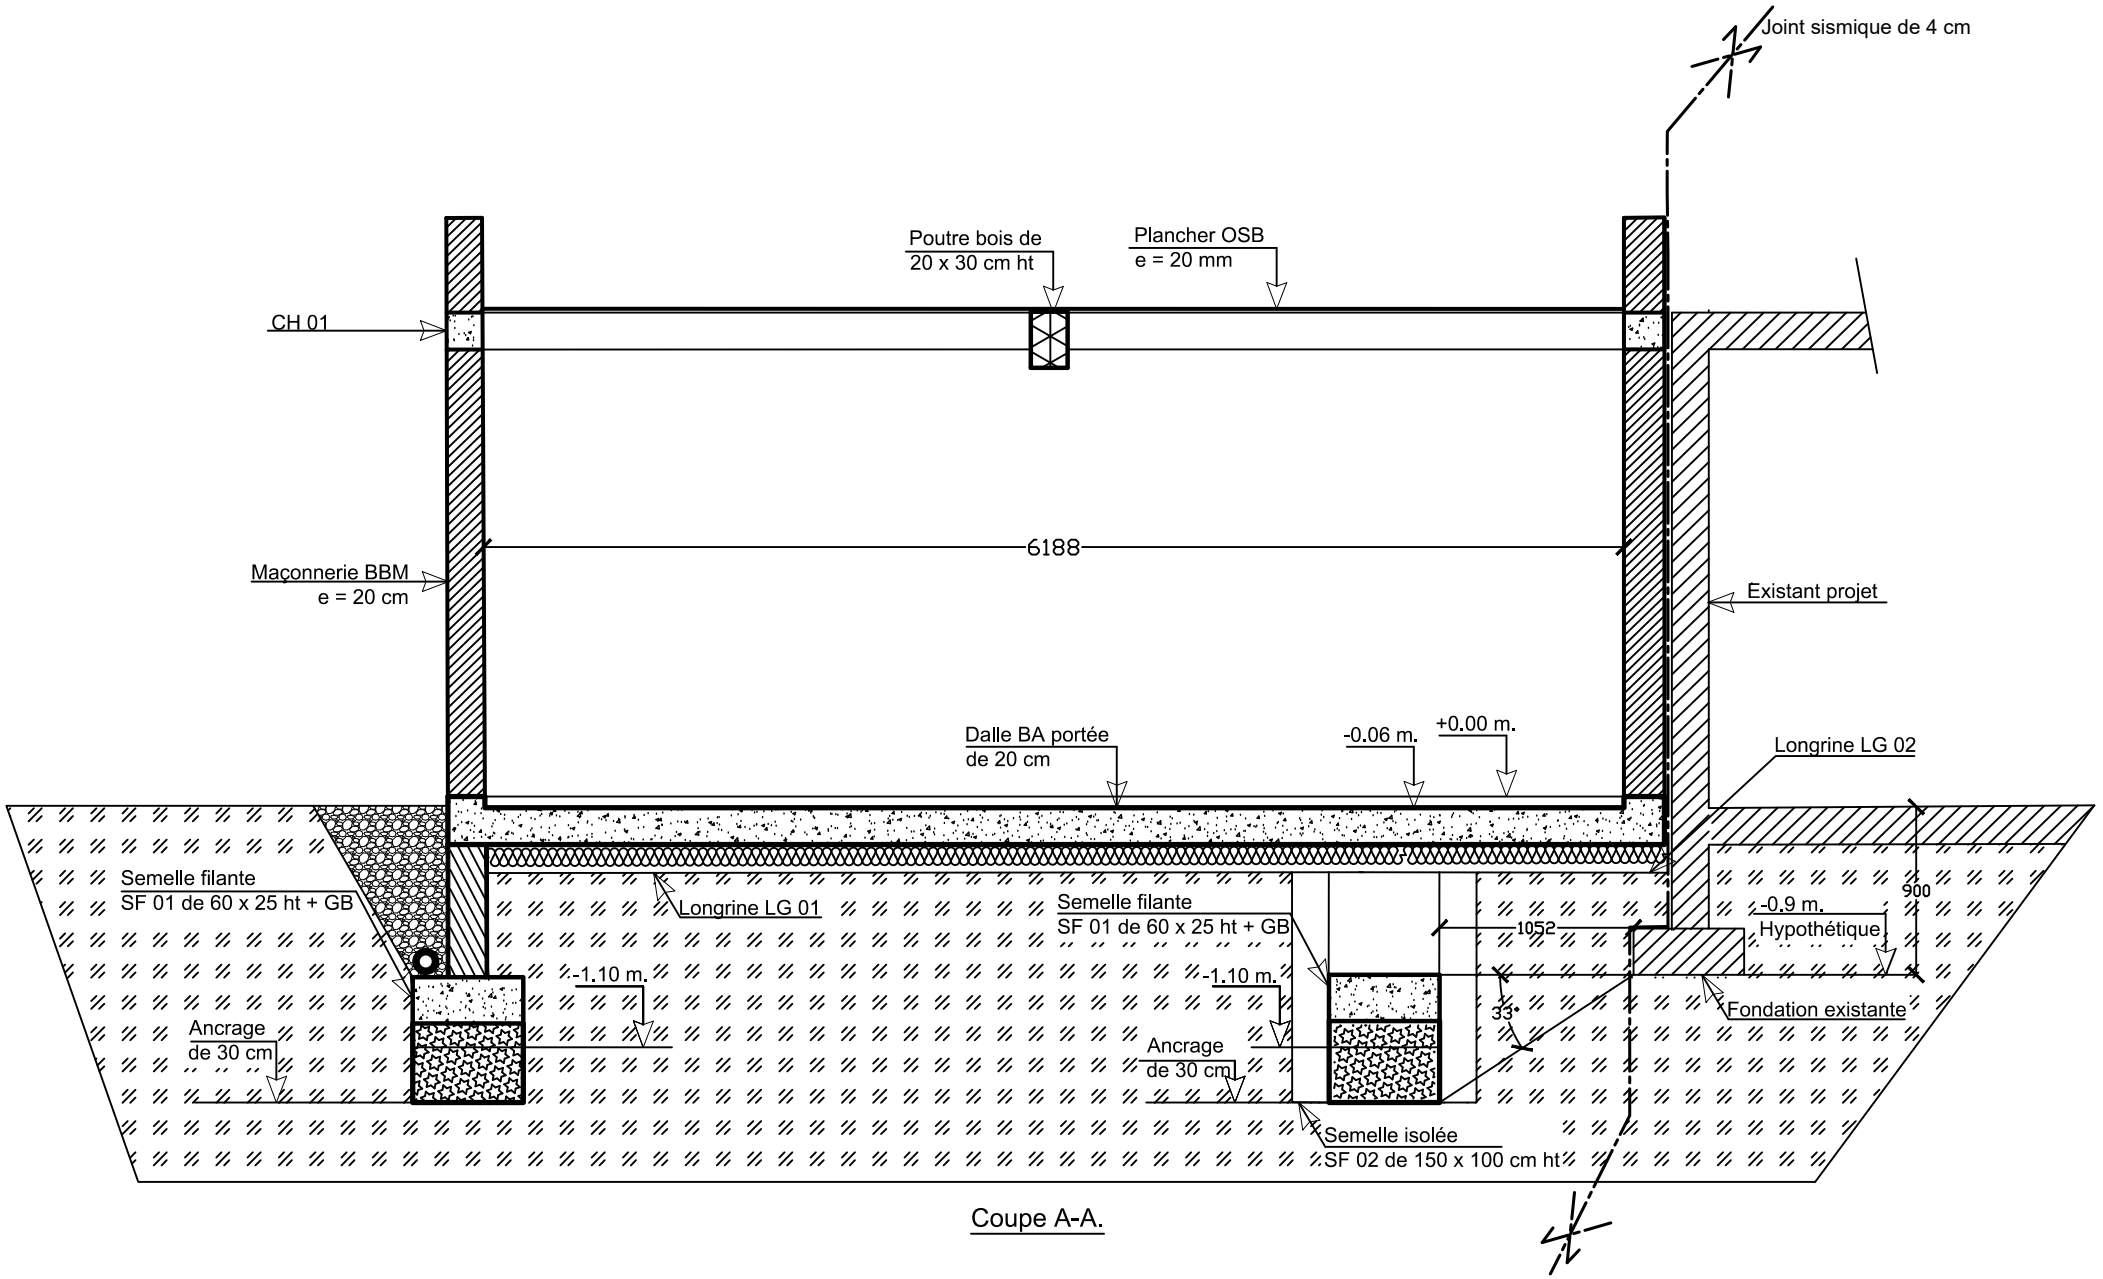


Coupe A-A.

Maîtrise d'Ouvrage : M Leveque et Mme Lenquette 21 Rue Leon Gambetta 59730 St- Pithon	**BET STRUCTURE :** J.K.F. STRUCTURE 92 Bd du GLE du Gaulle 59100 Roubaix	Etude BA pour la création d'une extension	**Dossier d'Etude Structurelle :** Coupe A-A	**Plan N° : GO 03** Ech : 1/50

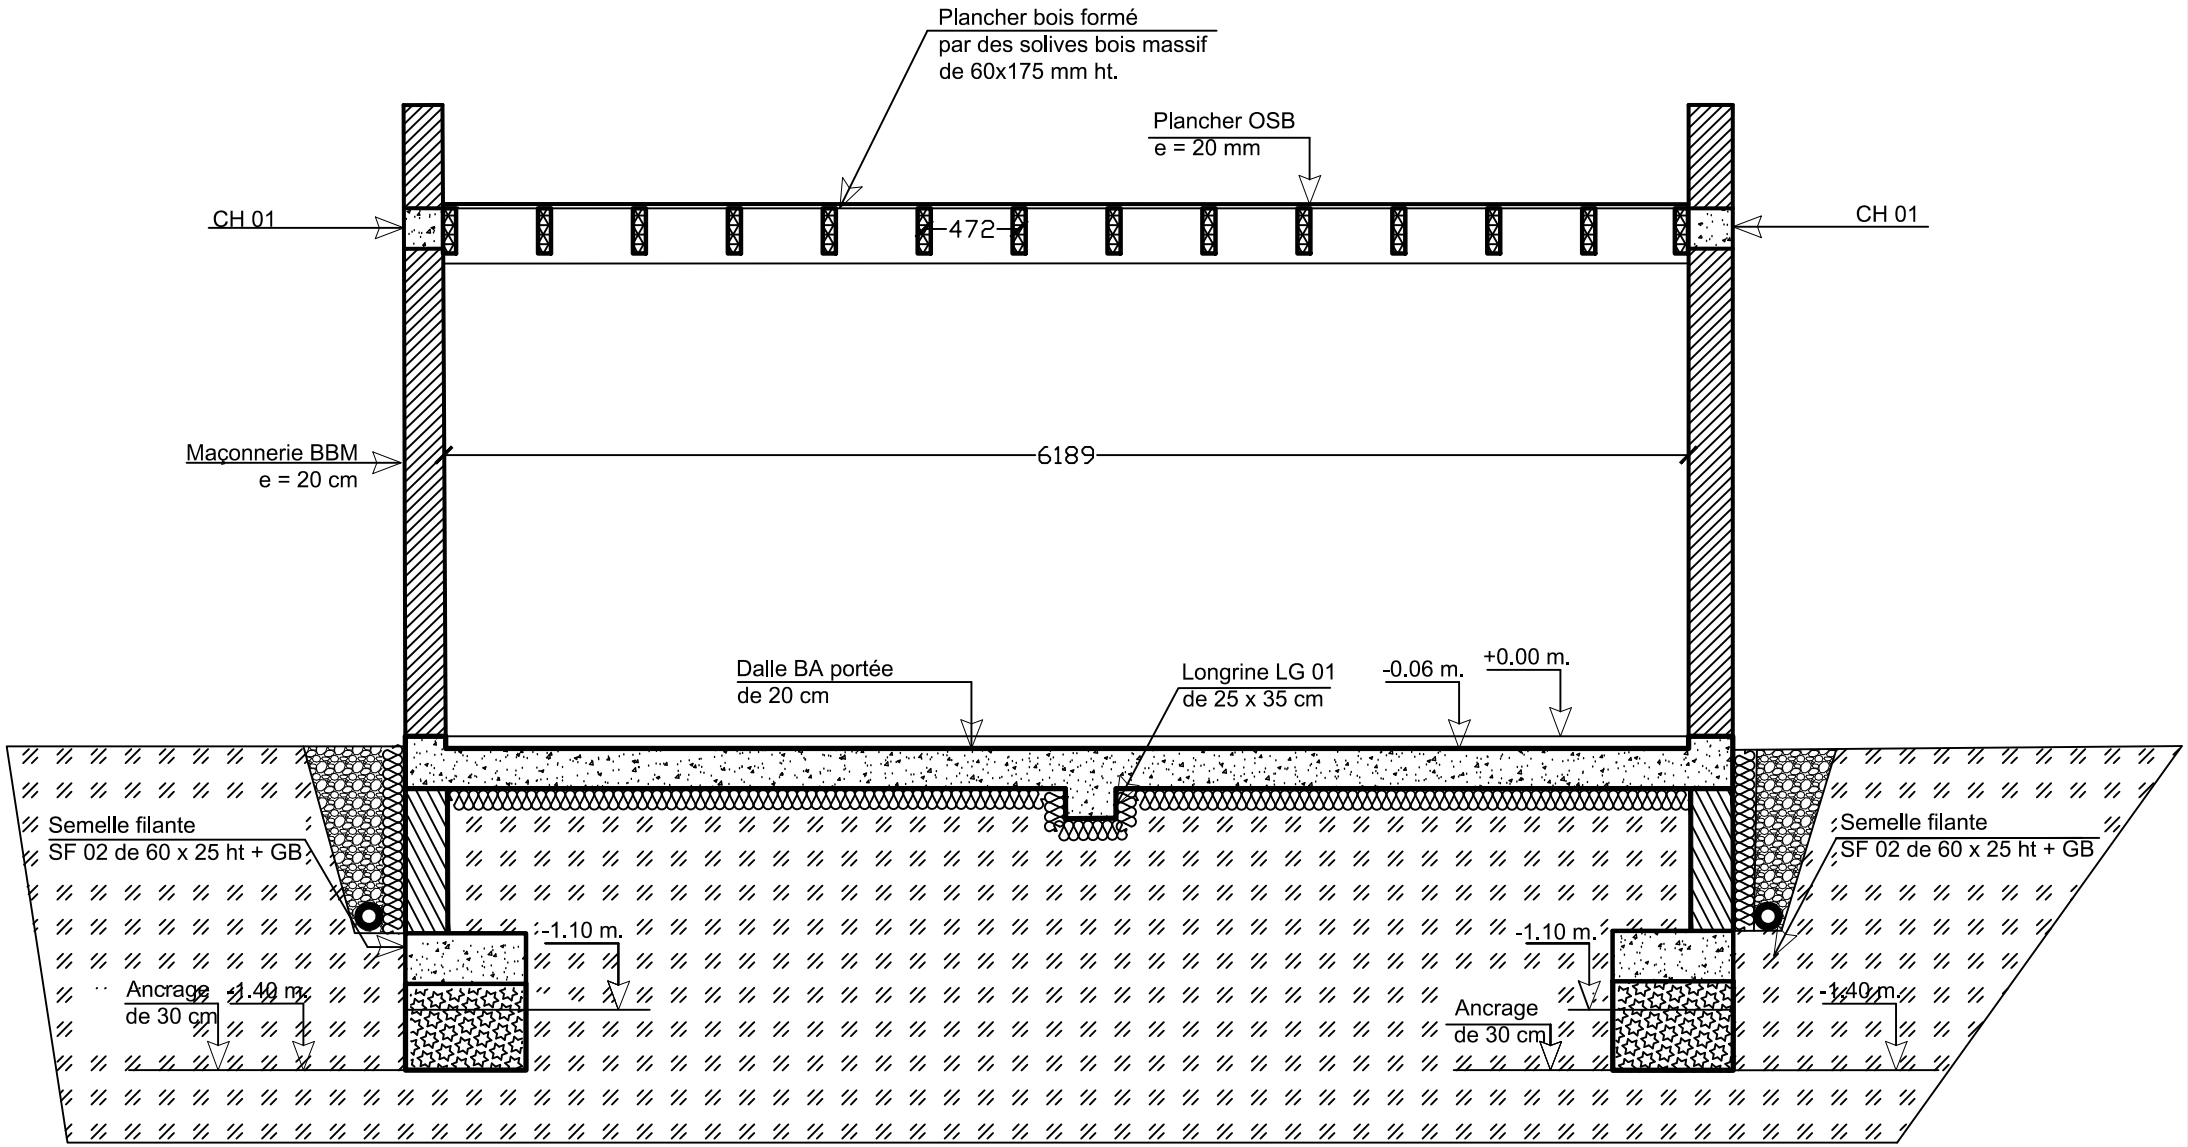

Coupe B-B.

Maîtrise d'Ouvrage : M Leveque et Mme Lenquette 21 Rue Leon Gambetta 59730 St- Pithon	**BET STRUCTURE :** J.K.F. STRUCTURE 92 Bd du GLE du Gaulle 59100 Roubaix	Etude BA pour la création d'une extension	**Dossier d'Etude Structurelle :** Coupe B-B	**Plan N° : GO 04** Ech : 1/50

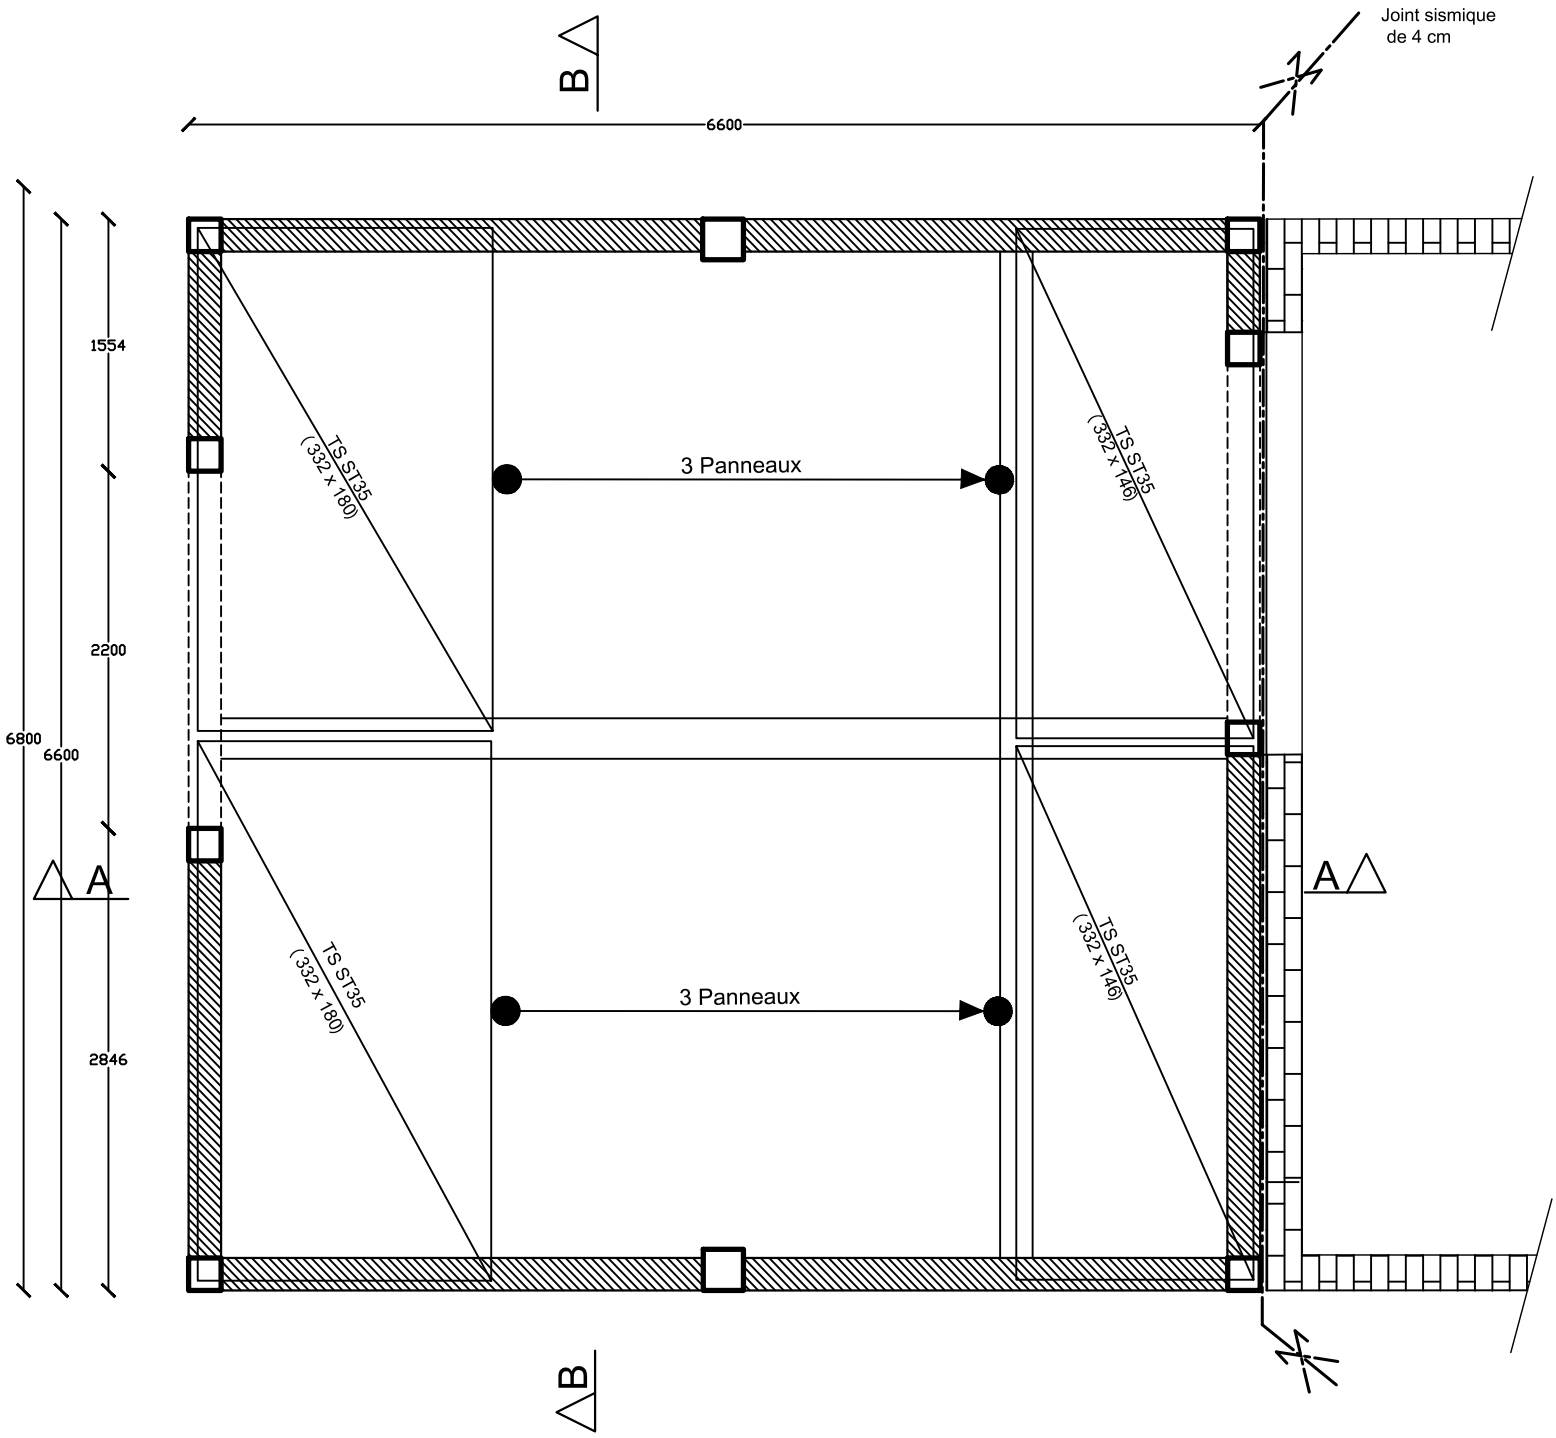

Nappe inf

Maîtrise d'Ouvrage :
M Leveque et Mme Lenquette
21 Rue Leon Gambetta
59730 St- Pithon


BET STRUCTURE :
J.K.F. STRUCTURE
92 Bd du GLE du Gaulle
59100 Roubaix

Etude BA pour la création d'une extension

Dossier d'Etude Structurelle :
Feraillage dalle
Nappe inférieure

Plan N° : GO 05

Ech : 1/50

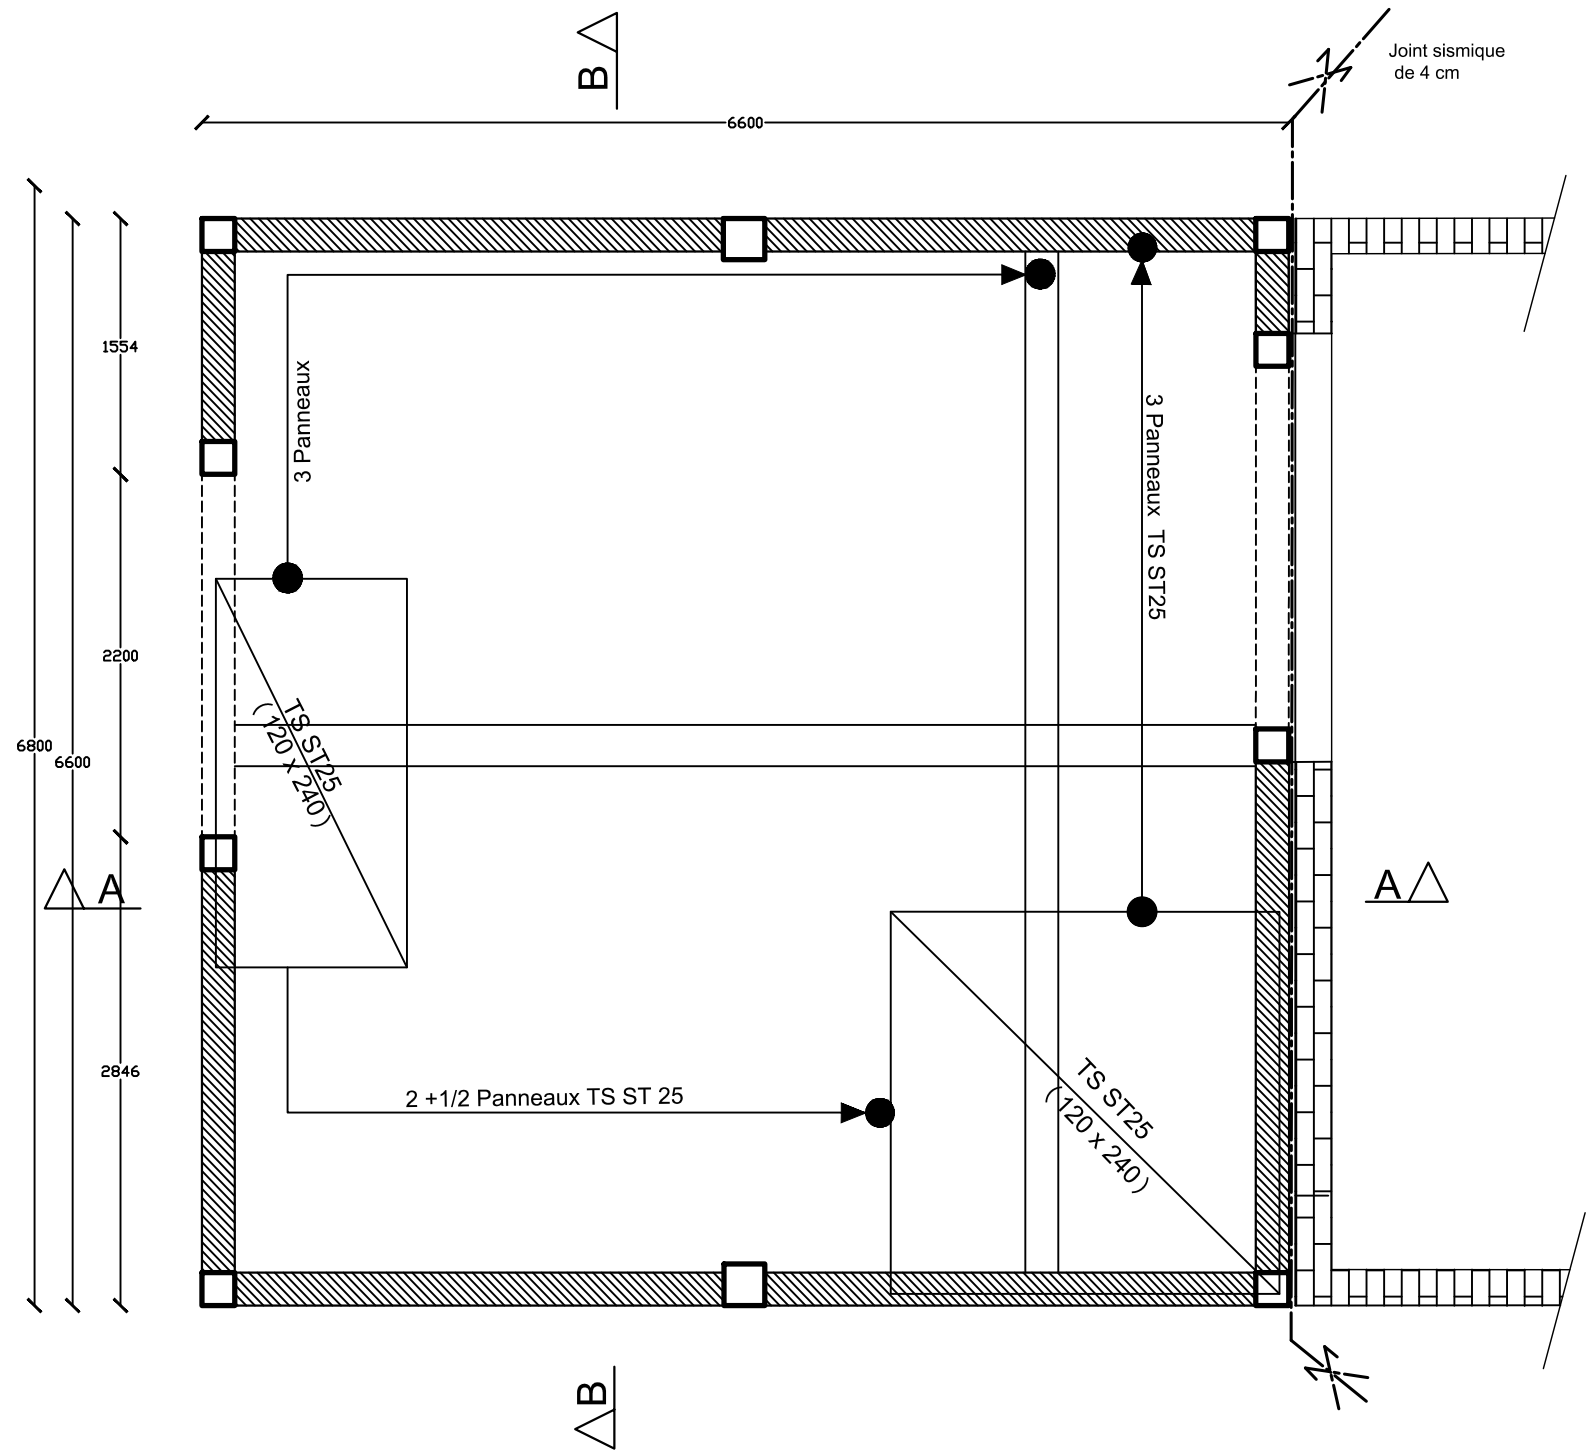

Nappe sup

Maîtrise d'Ouvrage :
M Leveque et Mme Lenquette
21 Rue Leon Gambetta
59730 St- Pithon

BET STRUCTURE :
J.K.F. STRUCTURE
92 Bd du GLE du Gaulle
59100 Roubaix

Etude BA pour la création d'une extension

Dossier d'Etude Structurelle :
Feraillage dalle
Nappe supérieure

Plan N° : GO 06

Ech : 1/50