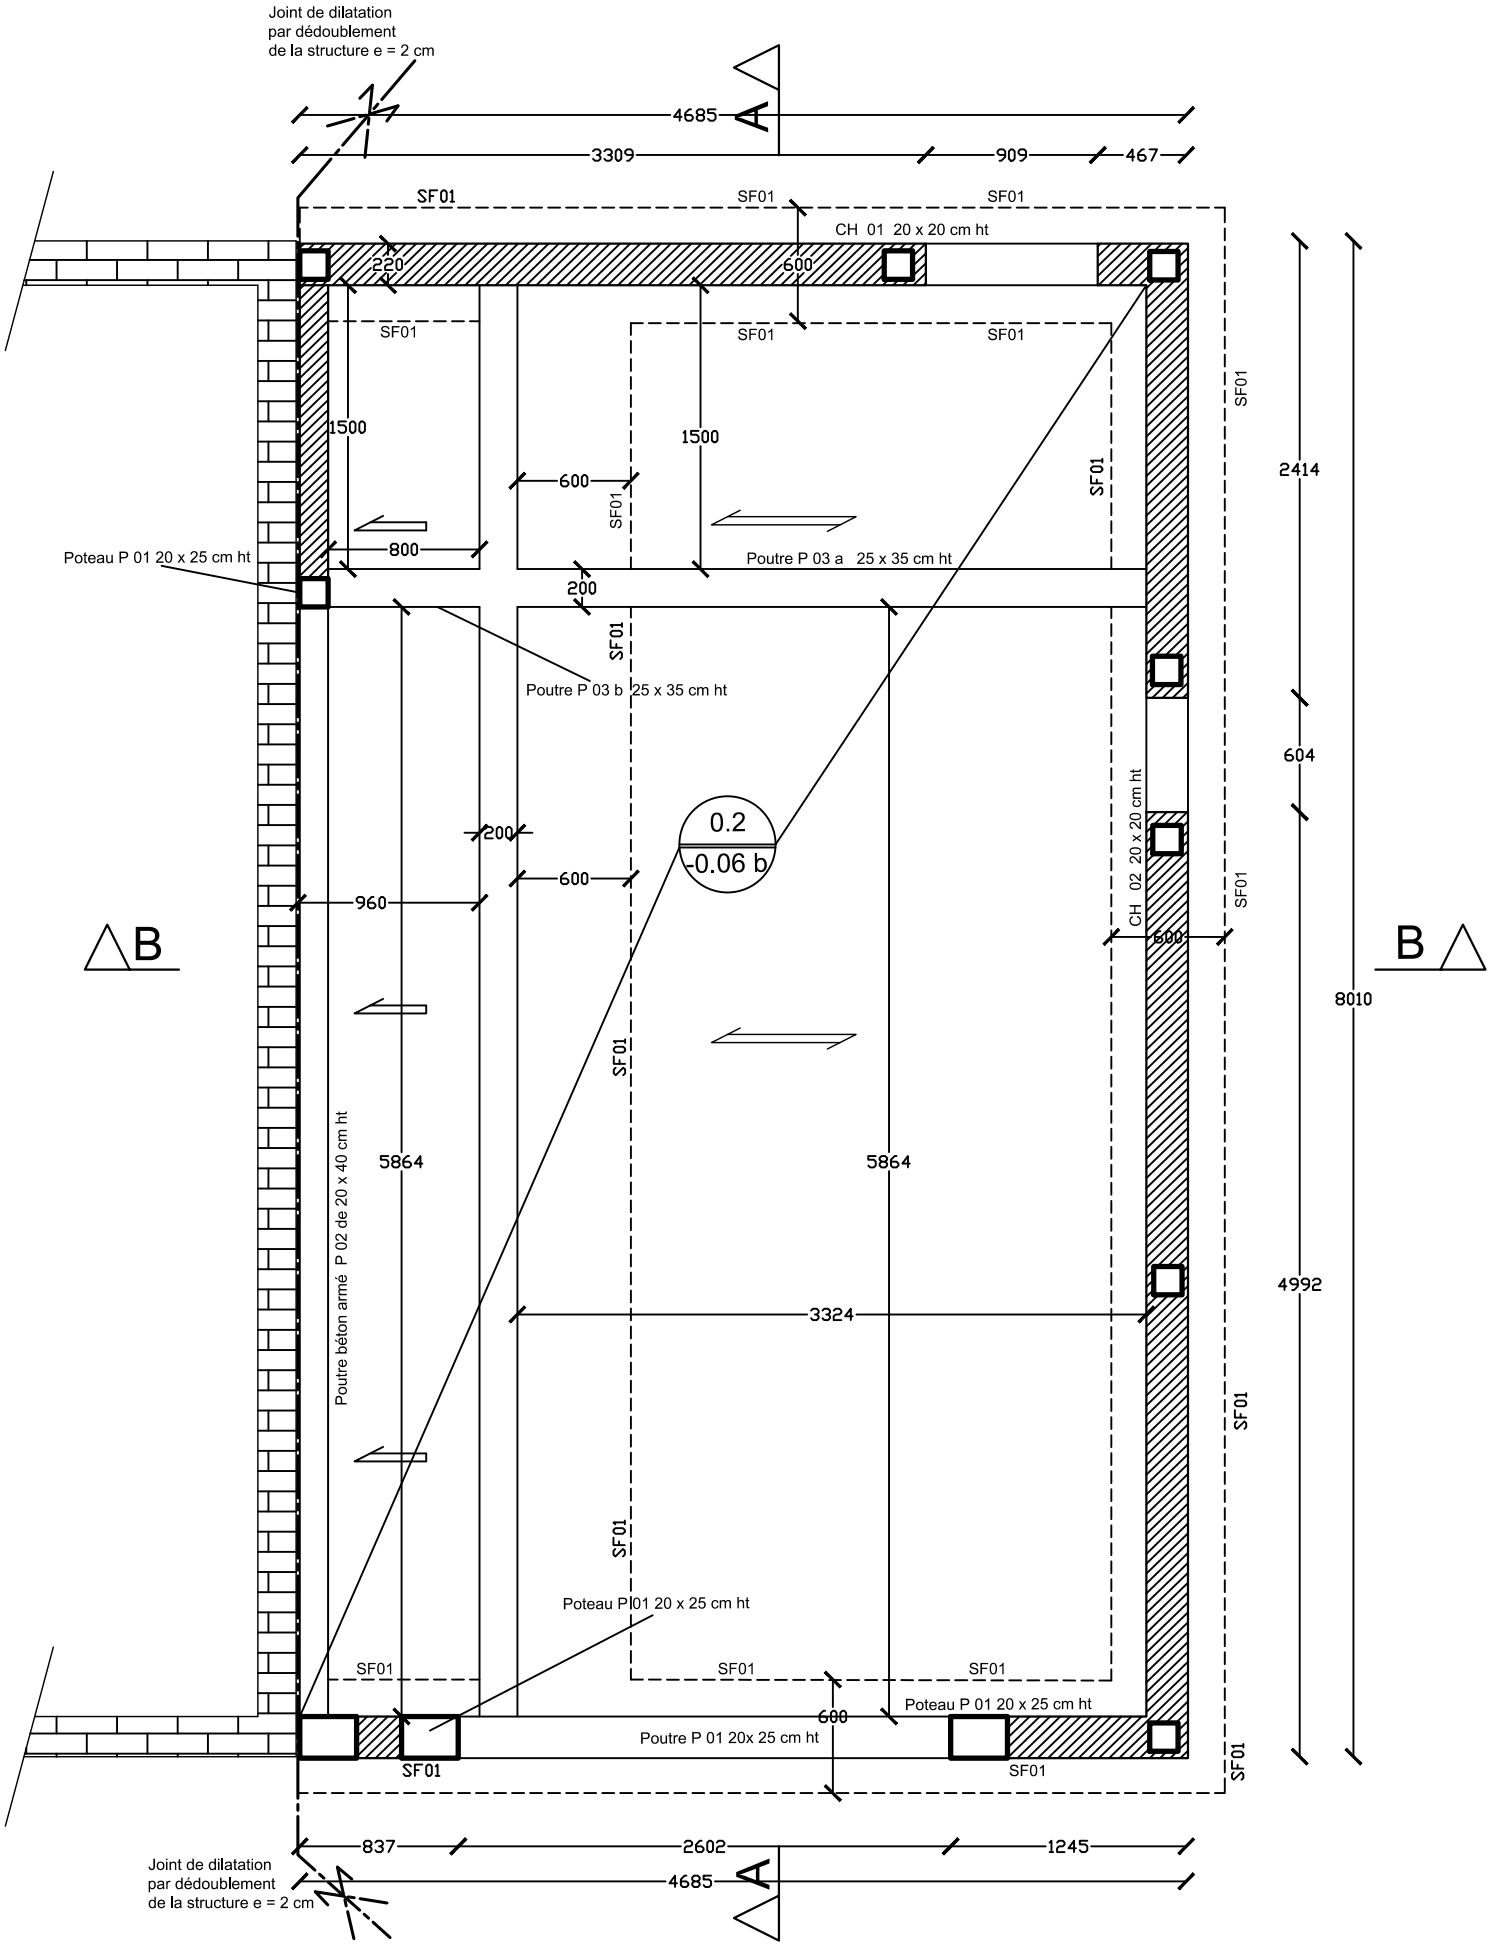



Maîtrise d'Ouvrage :
M et Me Tison Bock
38 Allée du Bois
59830 Wannehain.

BET STRUCTURE :
J.K.F. STRUCTURE
92 Bd du GLE du Gaulle
59100 Roubaix

Etude BA pour la création d'une extension

Dossier d'Etude Structurelle :
Plan de fondation

Plan N° : GO 01
Ech : 1/50

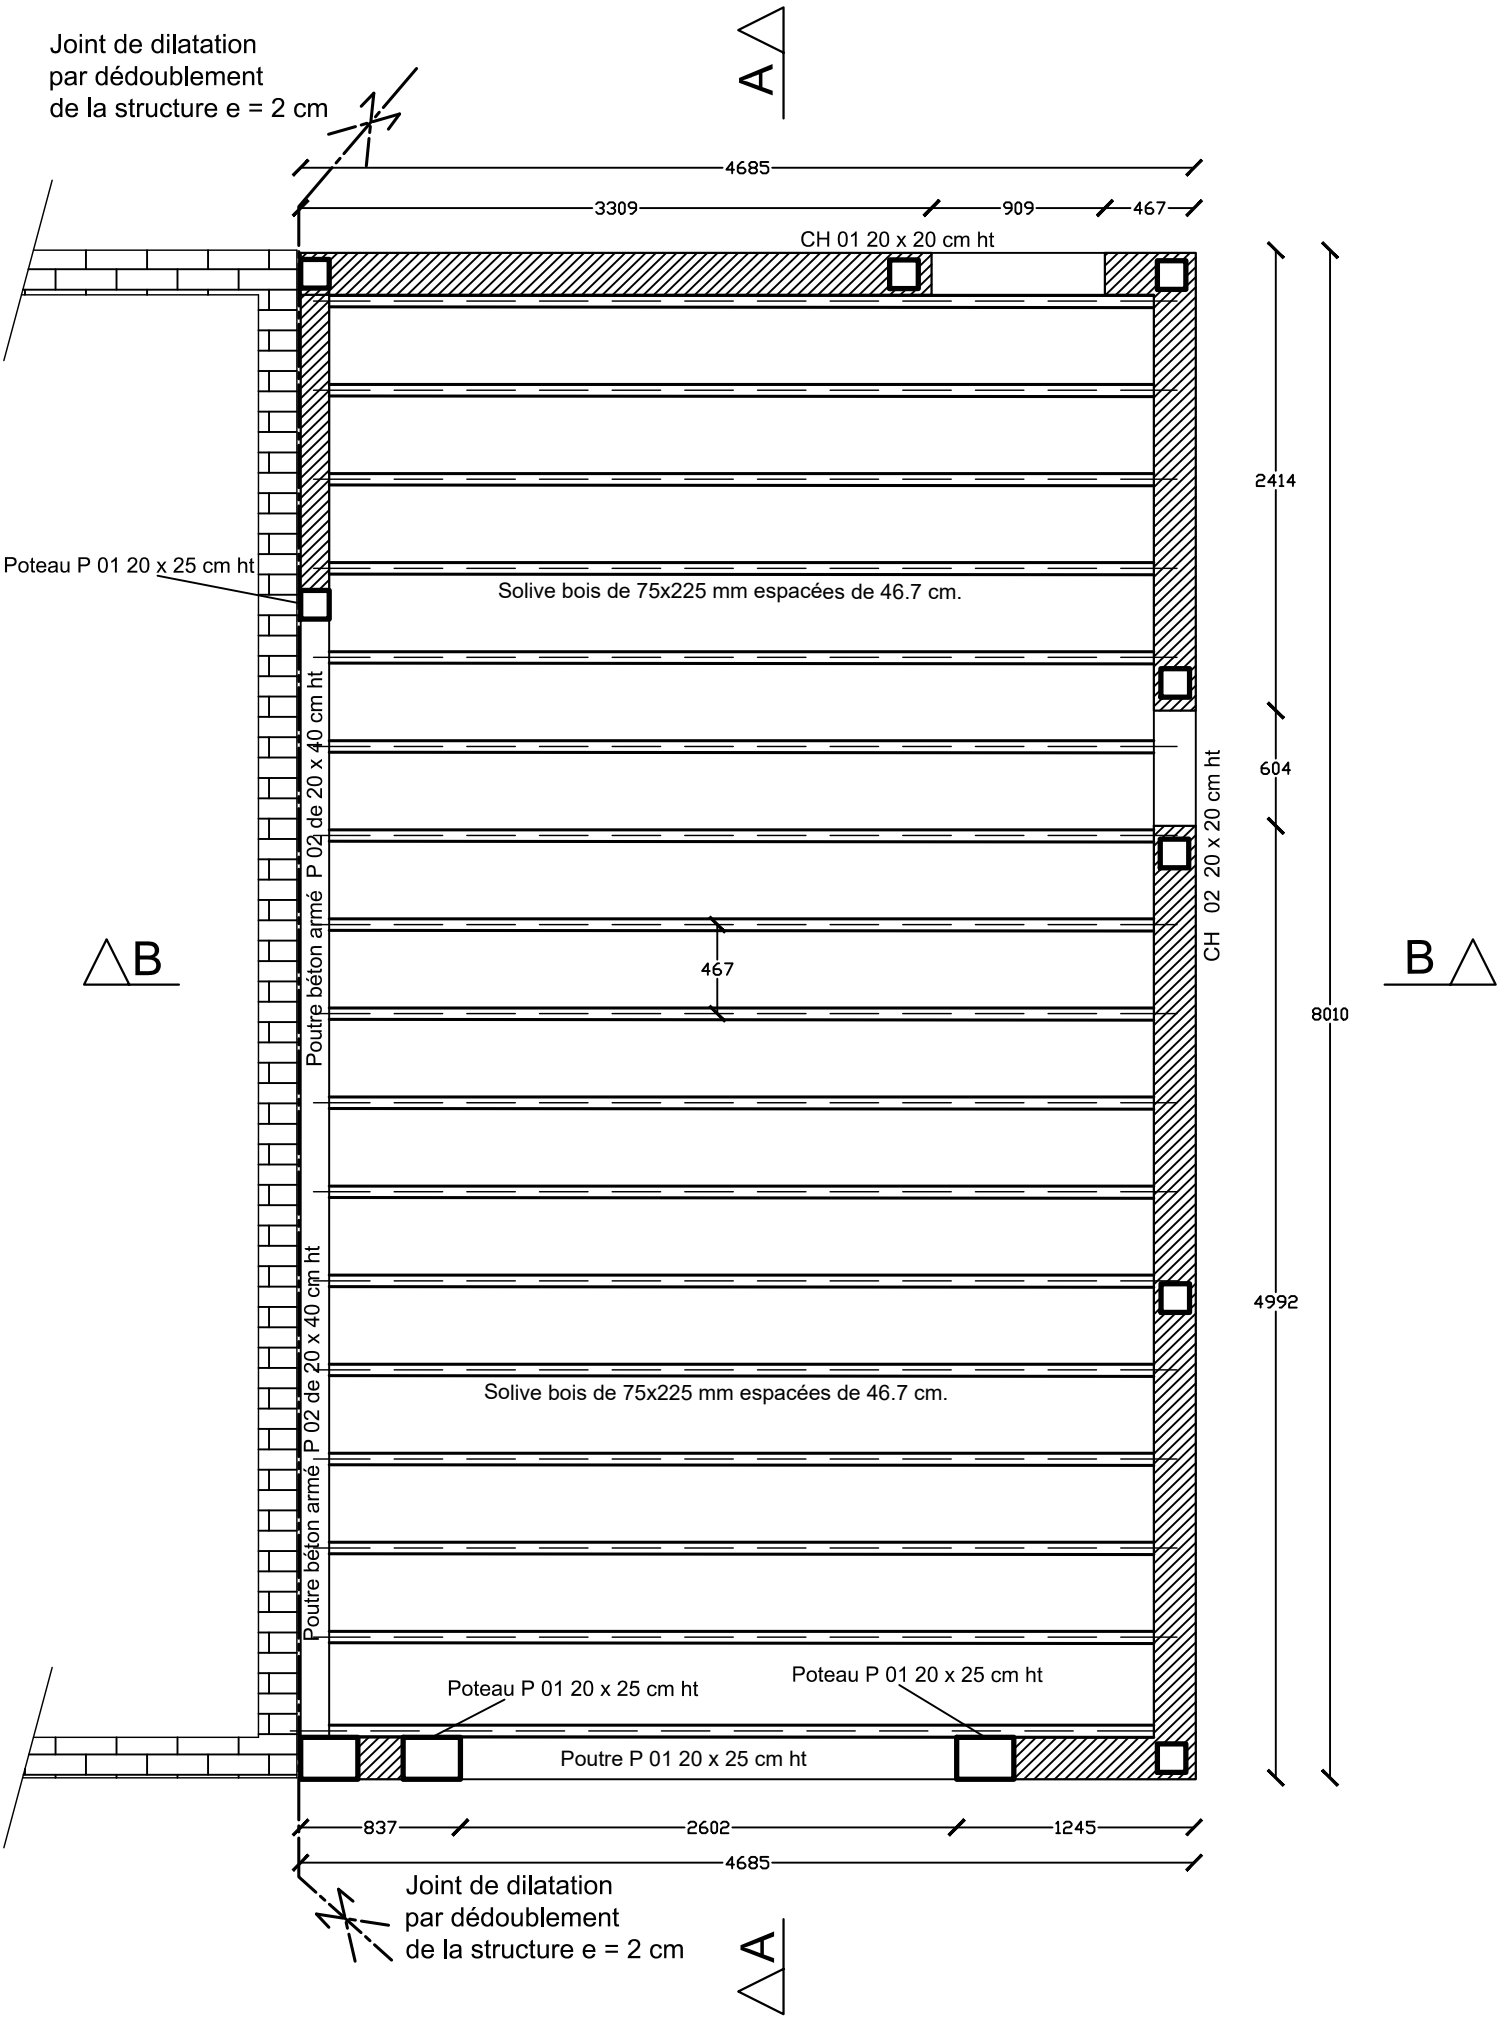


Maîtrise d'Ouvrage :
M et Me Tison Bock
38 Allée du Bois
59830 Wannehain.

BET STRUCTURE :
J.K.F. STRUCTURE
92 Bd du GLE du Gaulle
59100 Roubaix

Etude BA pour la création
d'une extension


Dossier d'Etude Structurelle :
PH RDC

Plan N° : GO 02
Ech : 1/50

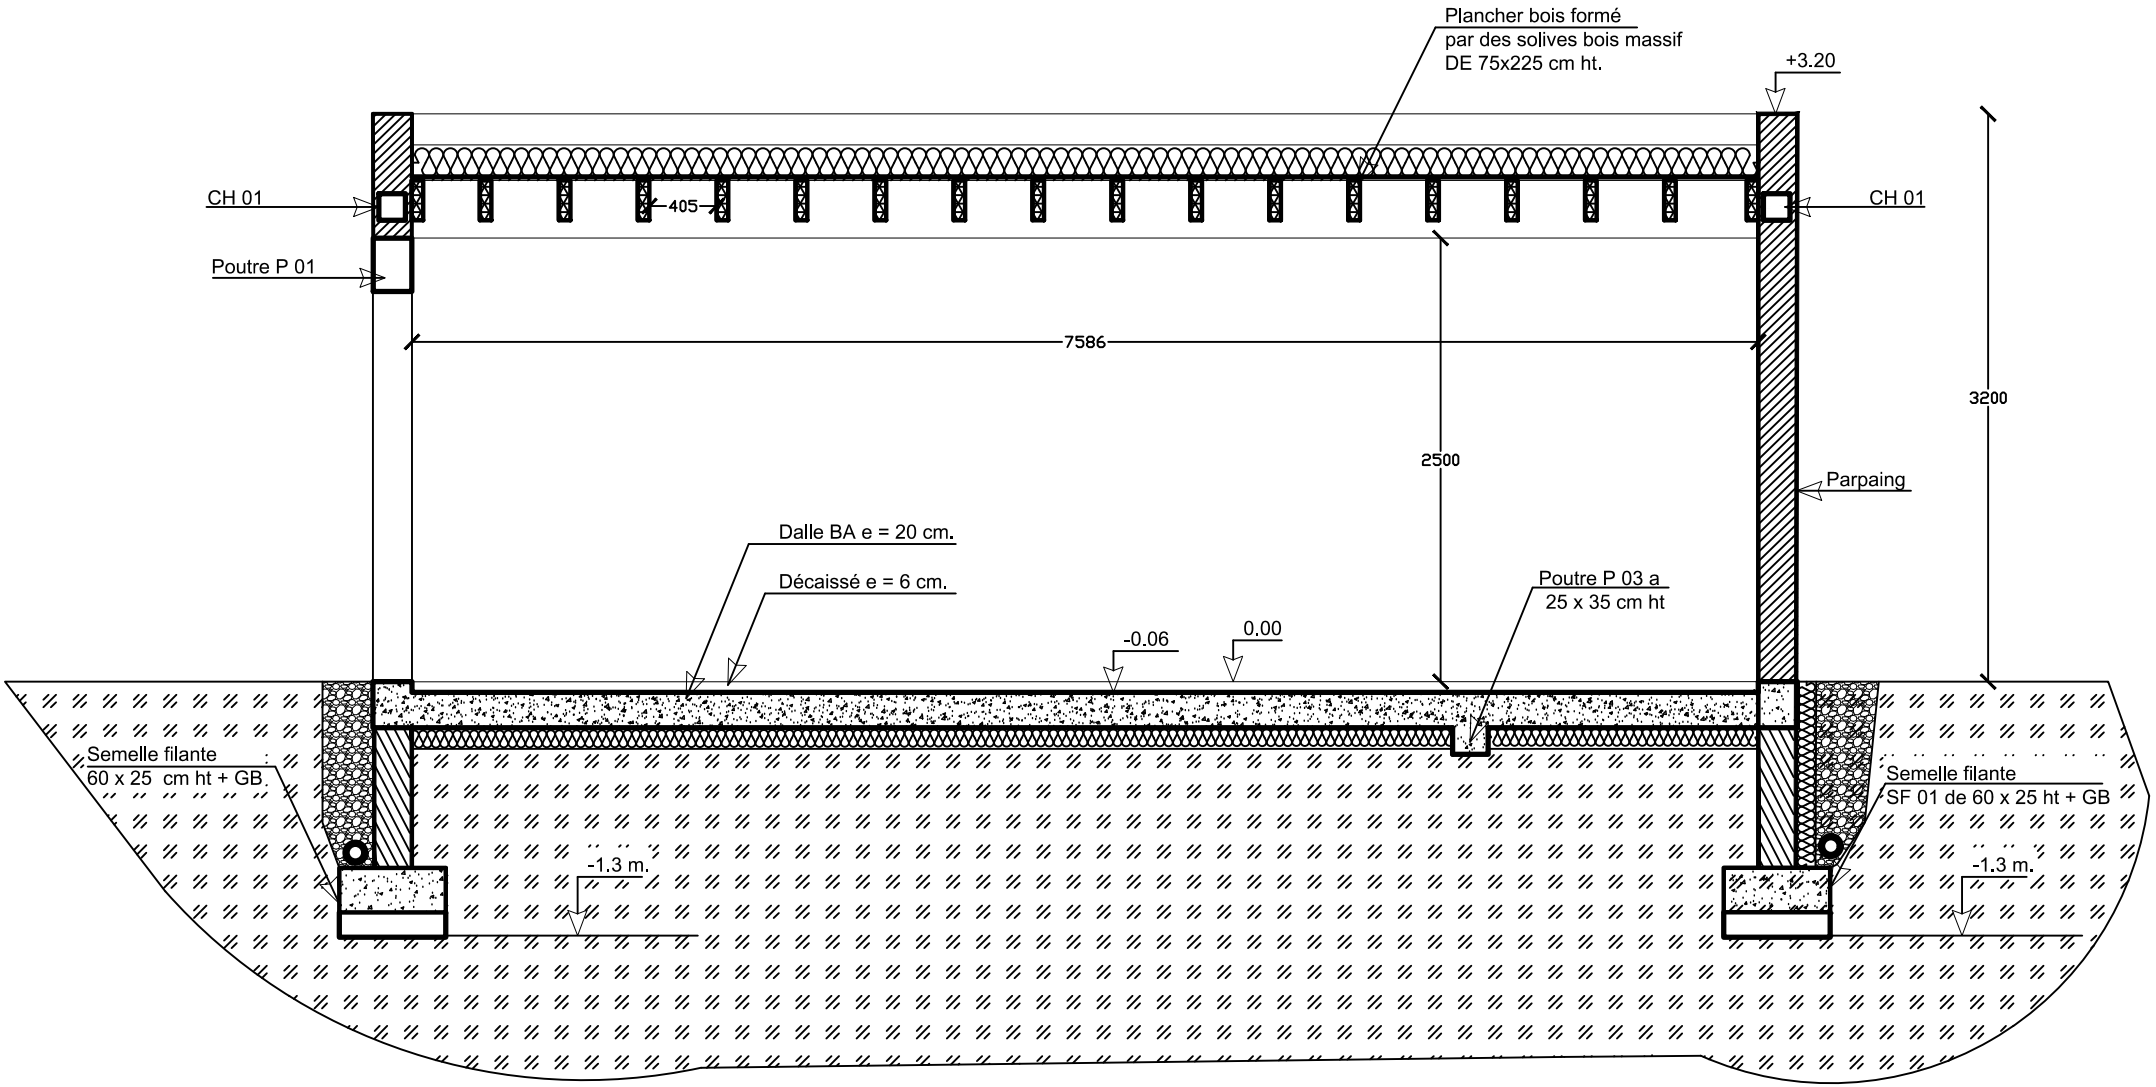

Coupe A-A.

Maîtrise d'Ouvrage : M et Me Tison Bock 38 Allée du Bois 59830 Wannehain.	**BET STRUCTURE :** J.K.F. STRUCTURE 92 Bd du GLE du Gaulle 59100 Roubaix	Etude BA pour la création d'une extension	**Dossier d'Etude Structurelle :** COUPE A-A	**Plan N° : GO 03** Ech : 1/50

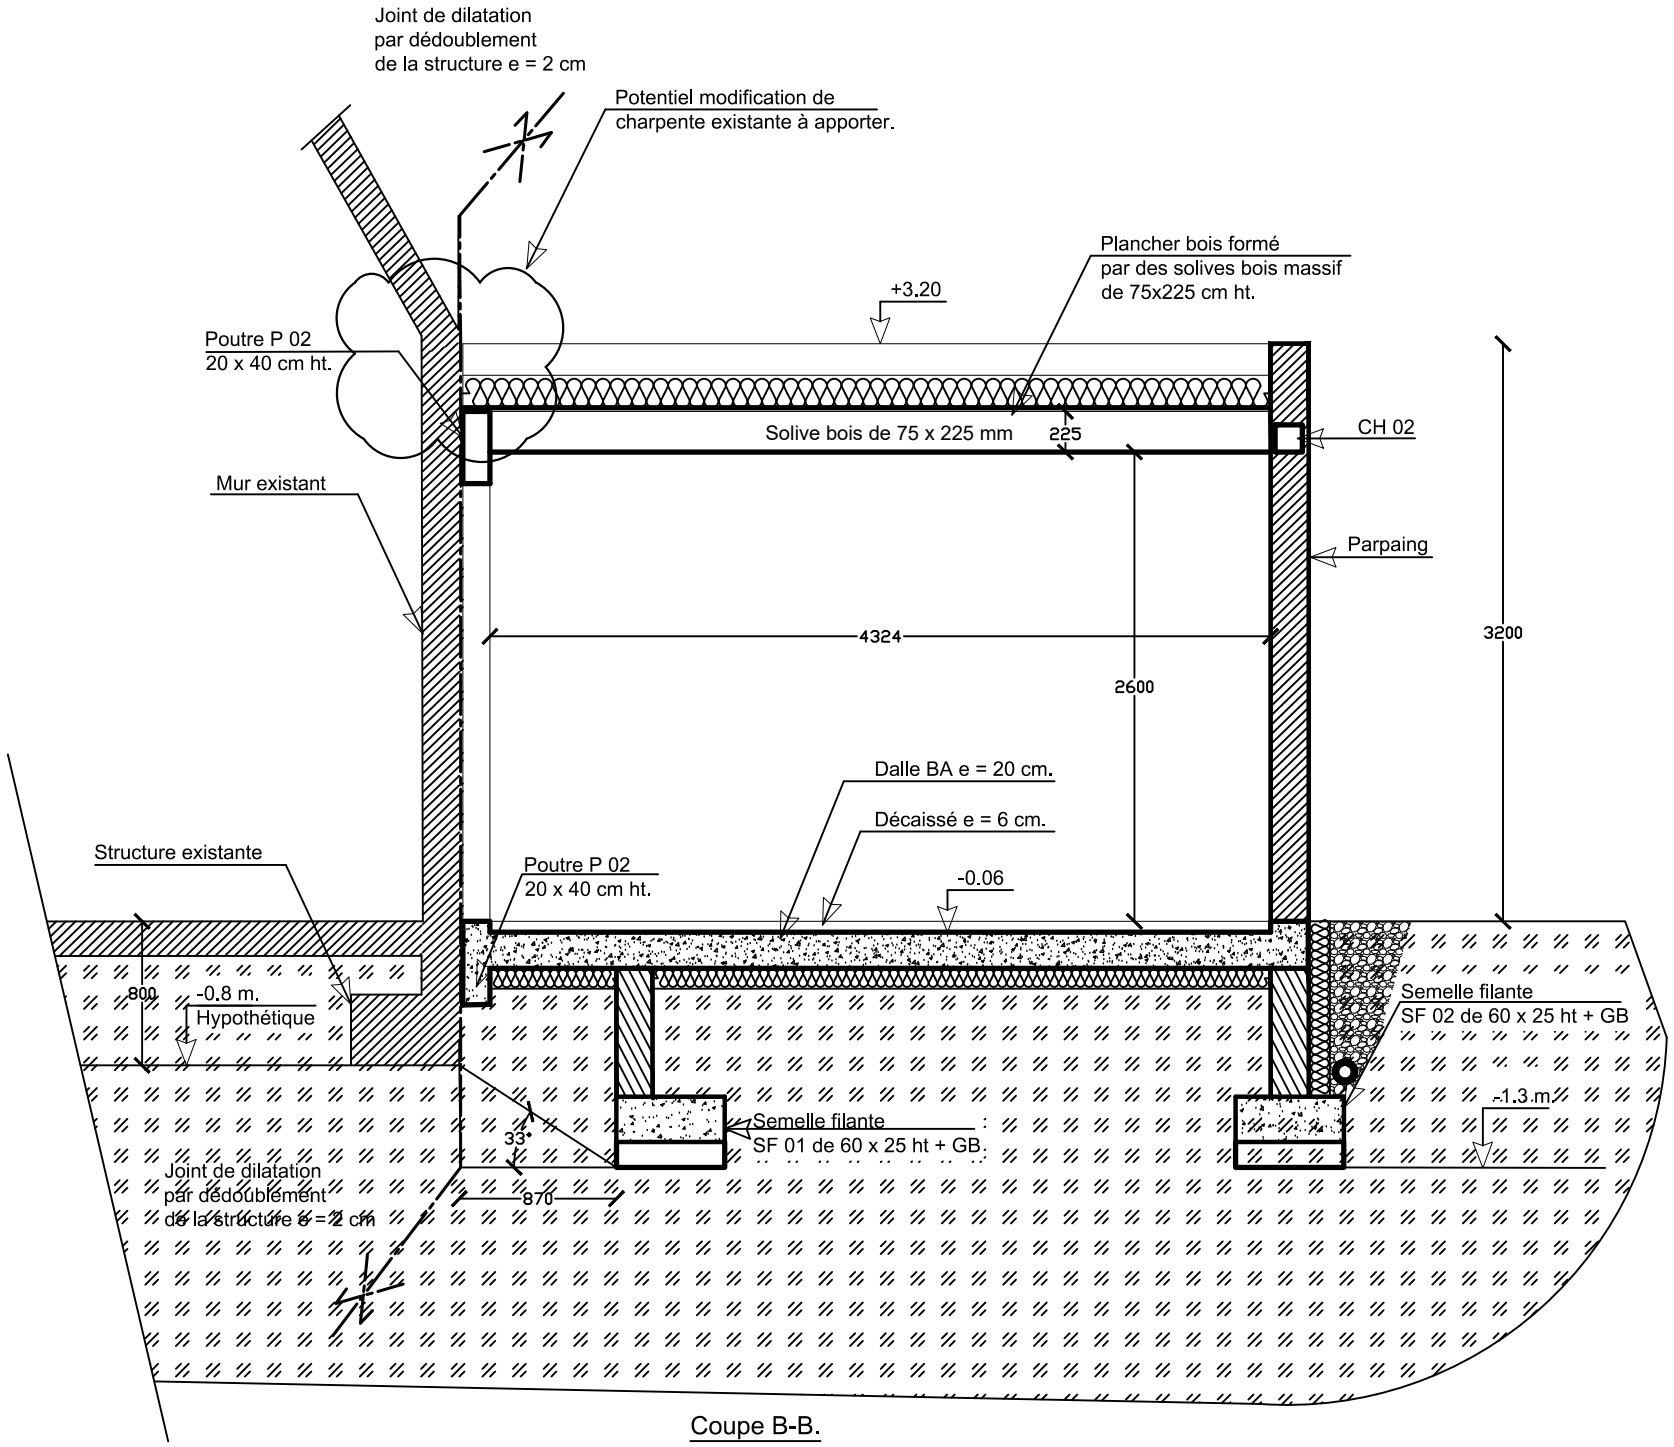

Coupe B-B.

CH 01: Chainage vertical BA 20 x 20 cm ht
CH 02: Chainage horizontal BA 20 x 20 cm ht
P 01 : Poteau BA 20 x 25 cm ht
P 01 : Poutre BA 20 x 25 cm ht
P 02 : Poutre BA 20 x 40 cm ht
P 03 a: Poutre BA 25 x 35 cm ht
P 03 b: Poutre BA 25 x 35 cm ht

Parpaing

Mur Brique existant

Hypothèses de calculs :

Zone sismique faible (zone 01)
bâtiment de catégorie I,
la structure n'est pas
soumise à une conception
parasismique.

Conformément à l'étude de sols,
les fondations sont réalisées par
des fondations superficielles, type :
semelle filante.
Zone de neige : A1
Zone du vent : zone 2



Taux de travail du sol : 10 T/m²

Maitrise d'Ouvrage :
M et Me Tison Bock
38 Allée du Bois
59830 Wannehain.

BET STRUCTURE :
J.K.F. STRUCTURE
92 Bd du GLE du Gaulle
59100 Roubaix

Etude BA pour la création
d'une extension

Dossier d'Etude Structurelle :
COUPE B-B

Plan N° : GO 04
Ech : 1/50