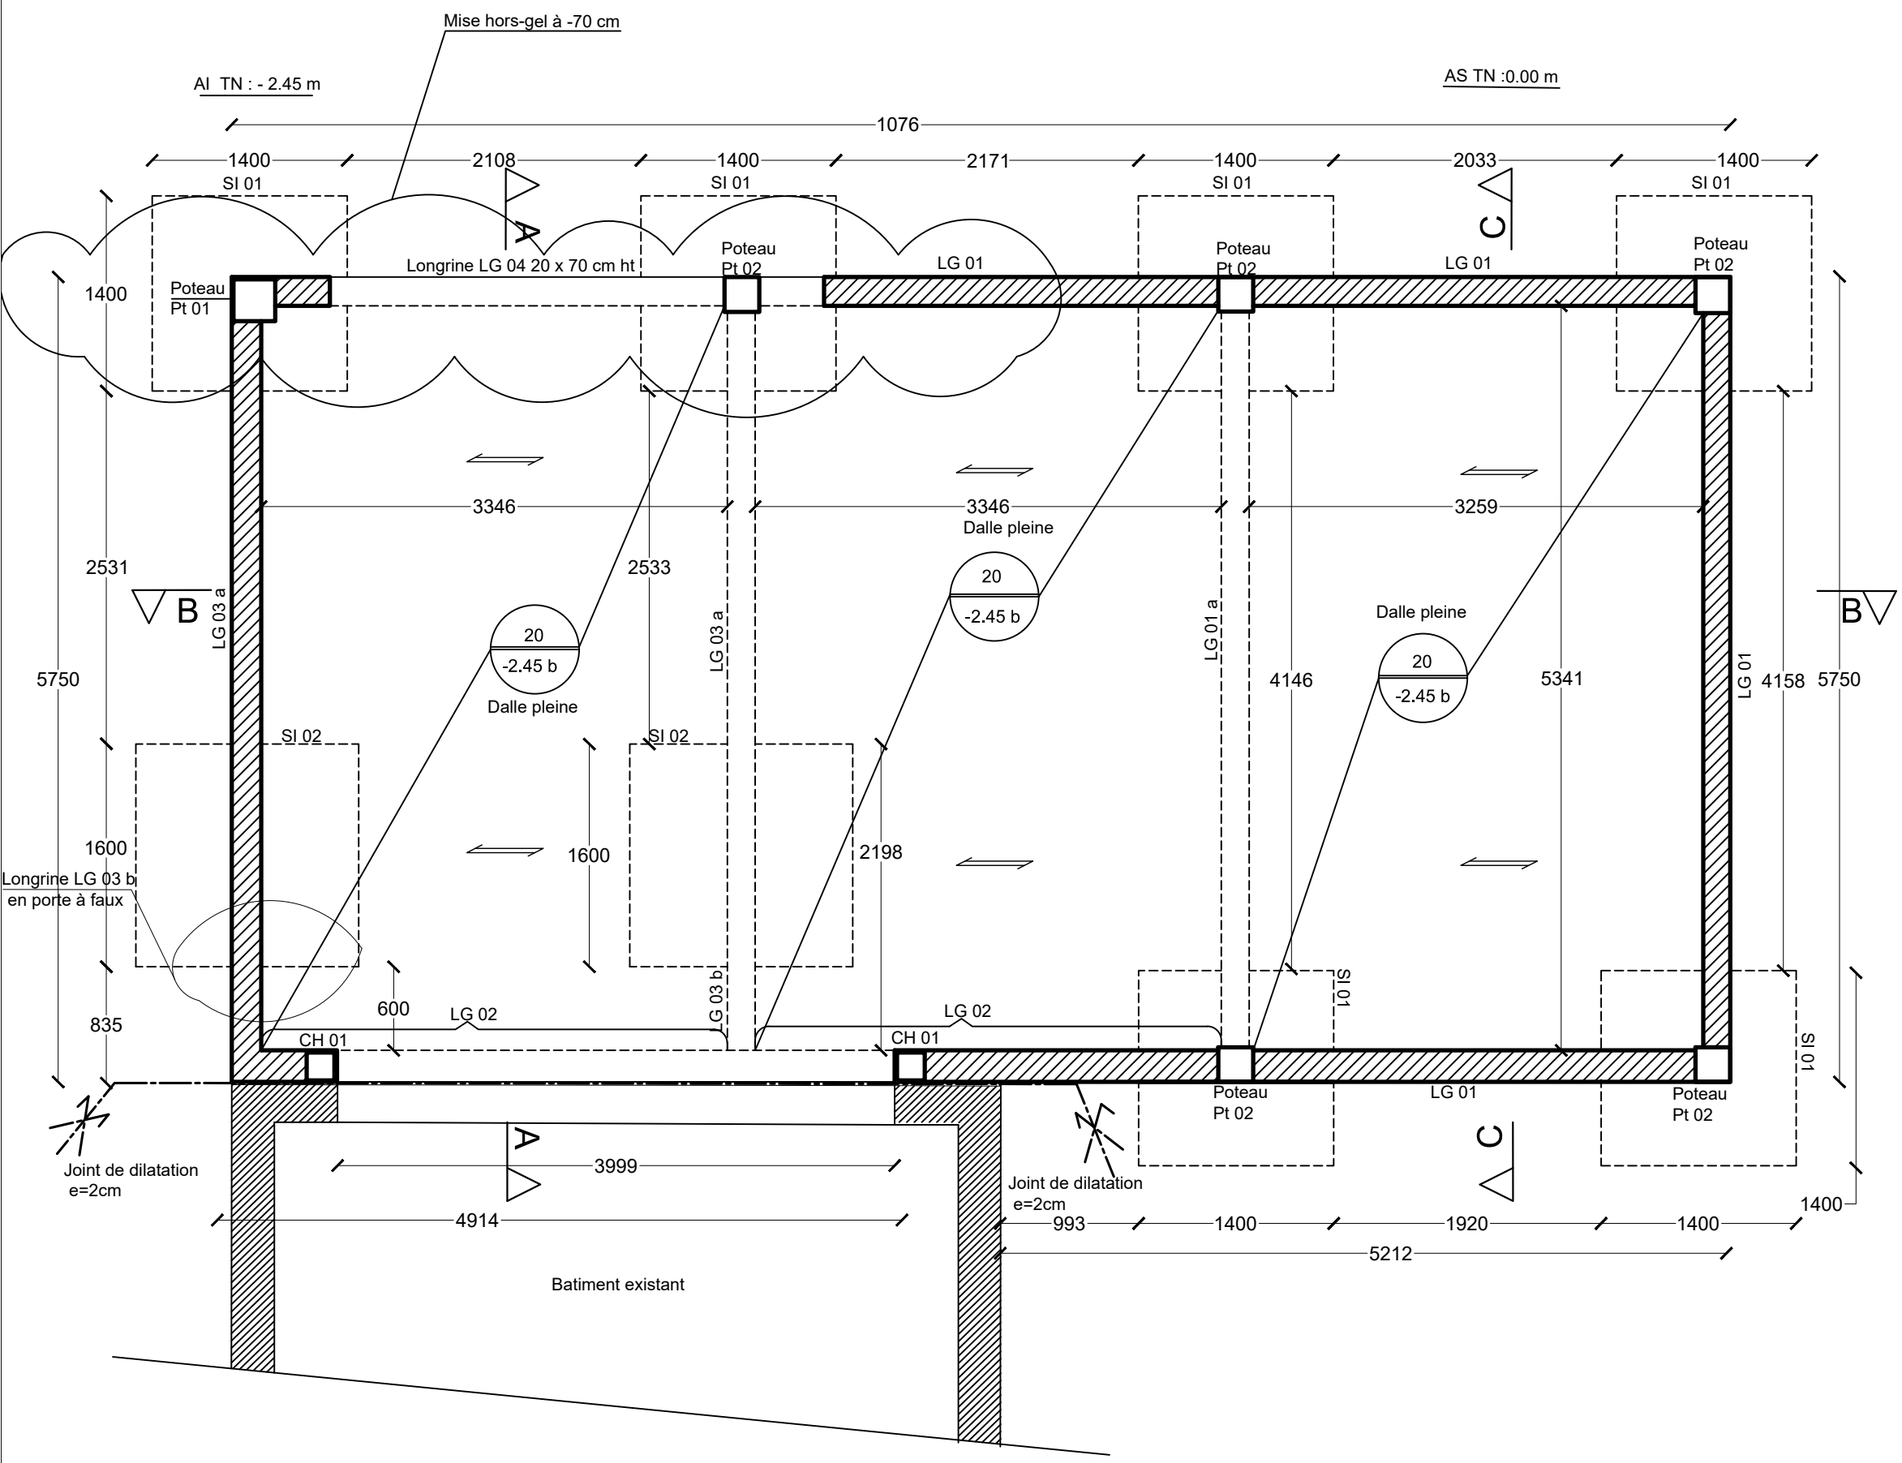


Plan de fondations

Maçonnerie BBM e =20 cm

Batiment existant

Sl 01 : Semelle Isolée de 140 x 140 cm ht
Sl 02 : Semelle Isolée de 160 x 160 cm ht
Pt 01 : Poteau BA 30 x 30 cm ht
Pt 02 : Poteau BA 25 x 25 cm ht
LG 01 : Longrine BA 20x 35 cm ht
LG 01 a :Longrine BA 20x 35 cm ht
LG 02 : Longrine BA 25 x 40 cm ht
LG 03 a : Longrine BA 25 x 40 cm ht
LG 03 b : Longrine BA 25 x 40 cm ht
P 01 a : Poutre BA 25 x 30 cm ht
P 01 b : Poutre BA 25 x 30 cm ht
P 02 a : Poutre BA 25 x 30 cm ht
P 02 b : Poutre BA 20 x 30 cm ht
P 03 : Poutre BA 25 x 30 cm ht
P 04 : Poutre BA 20 x 36 cm ht
P 05 : Poutre BA 20 x 30 cm ht
P 06 a : Poutre BA 30 x 25 cm ht
P 06 b : Poutre BA 30 x 25 cm ht
CH 01: Chainage vertical BA 20 x 20 cm ht
CH 02: Chainage horizontal BA 20 x 20 cm ht

Hypothèses de calculs :

Zone sismique (zone 01)
bâtiment de catégorie I,
la structure n'est pas soumise à une conception parasismique.

Zone de neige : A1


Zone du vent : zone 3

Conformément à l'étude de sols, les fondations sont réalisées par des semelles superficielles.

Charges d'exploitation Q = 1.5 Kn / m²

Carellage + chape = 130 kg/m²

Taux de travail du sol est de 1.74 bars

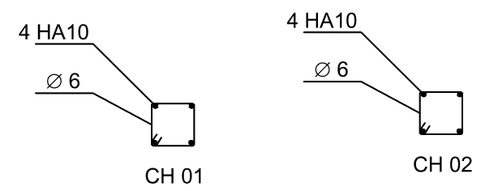


Maîtrise d'Ouvrage :
Mr et Mme BRICOUT
Avenue de Dunkerque
62520, Le Touquet-Paris-Plage.

BET STRUCTURE :
J.K.F. STRUCTURE
92 Bd du GLE du Gaulle
59100 Roubaix


Extension d'une habitation existante en R-1;RDC;Comble

Dossier d'Etude Structurelle :
Plan de fondations


Plan N° : GO 01
Ech : 1/75

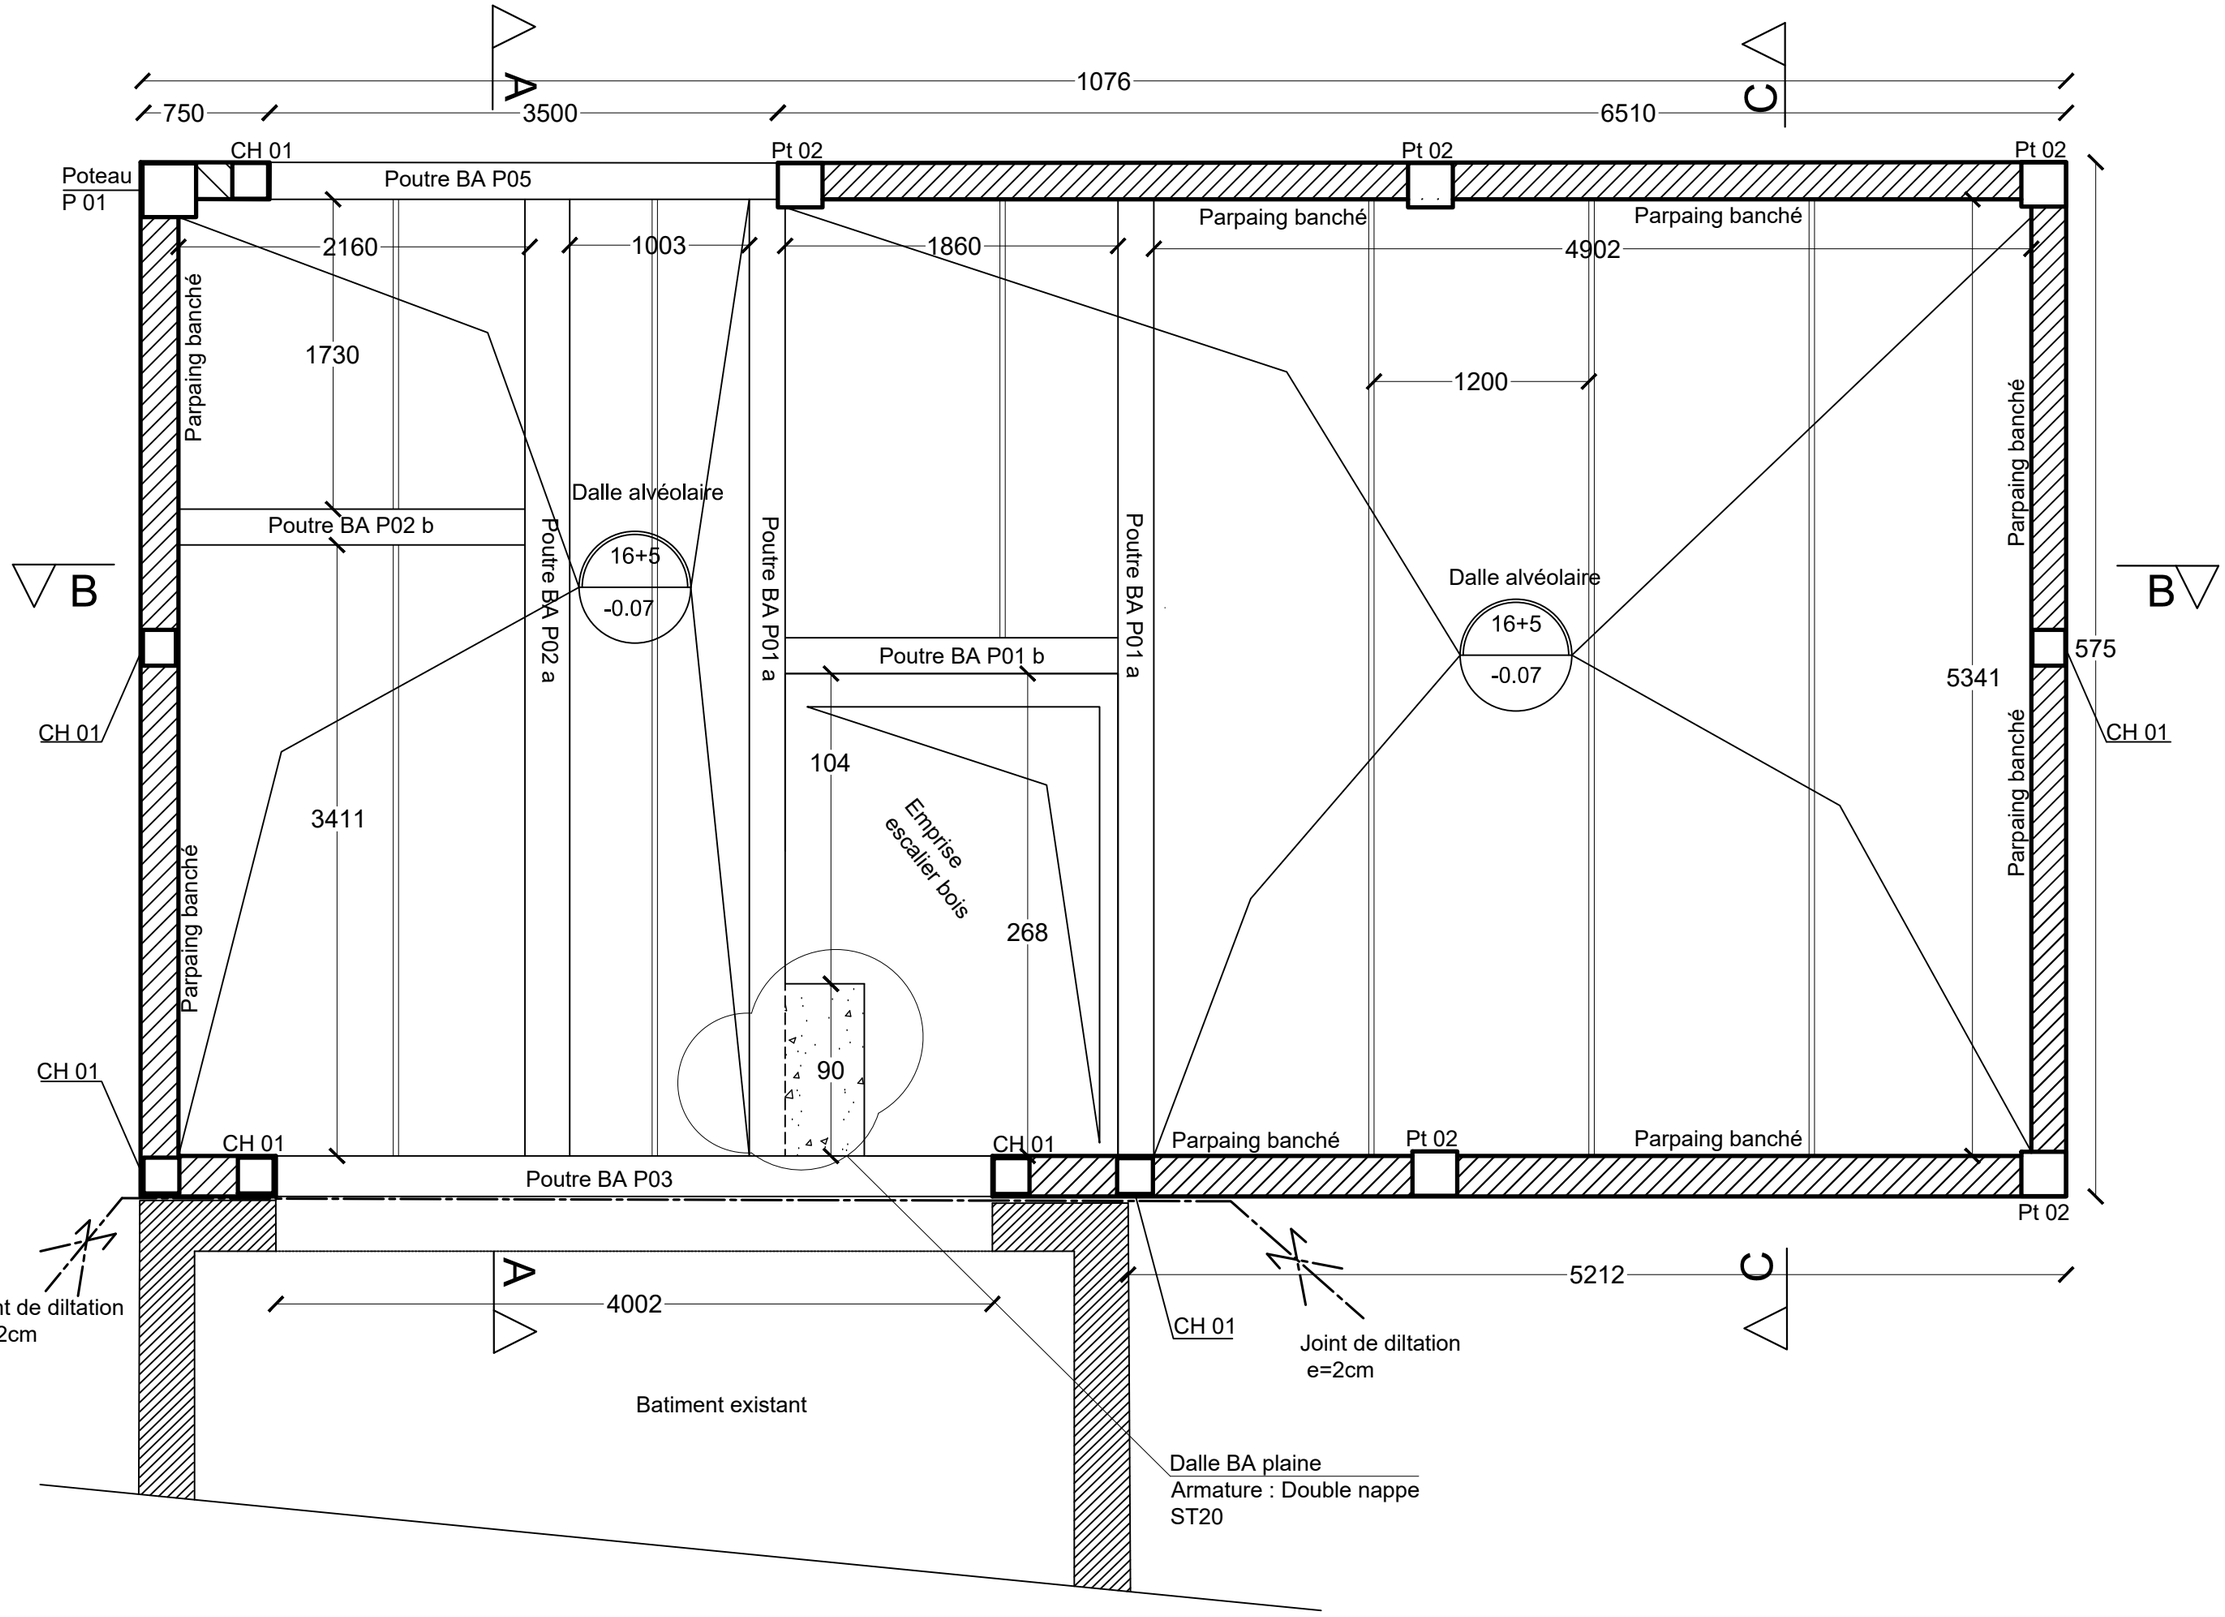


Maîtrise d'Ouvrage : Mr et Mme BRICOUT Avenue de Dunkerque 62520, Le Touquet-Paris-Plage.	**BET STRUCTURE :** J.K.F. STRUCTURE 92 Bd du GLE du Gaulle 59100 Roubaix	Extension d'une habitation existante en R-1;RDC;Comble	**Dossier d'Etude Structurelle :** Ph Sous-sol	**Plan N° : GO 02** Ech : 1/50

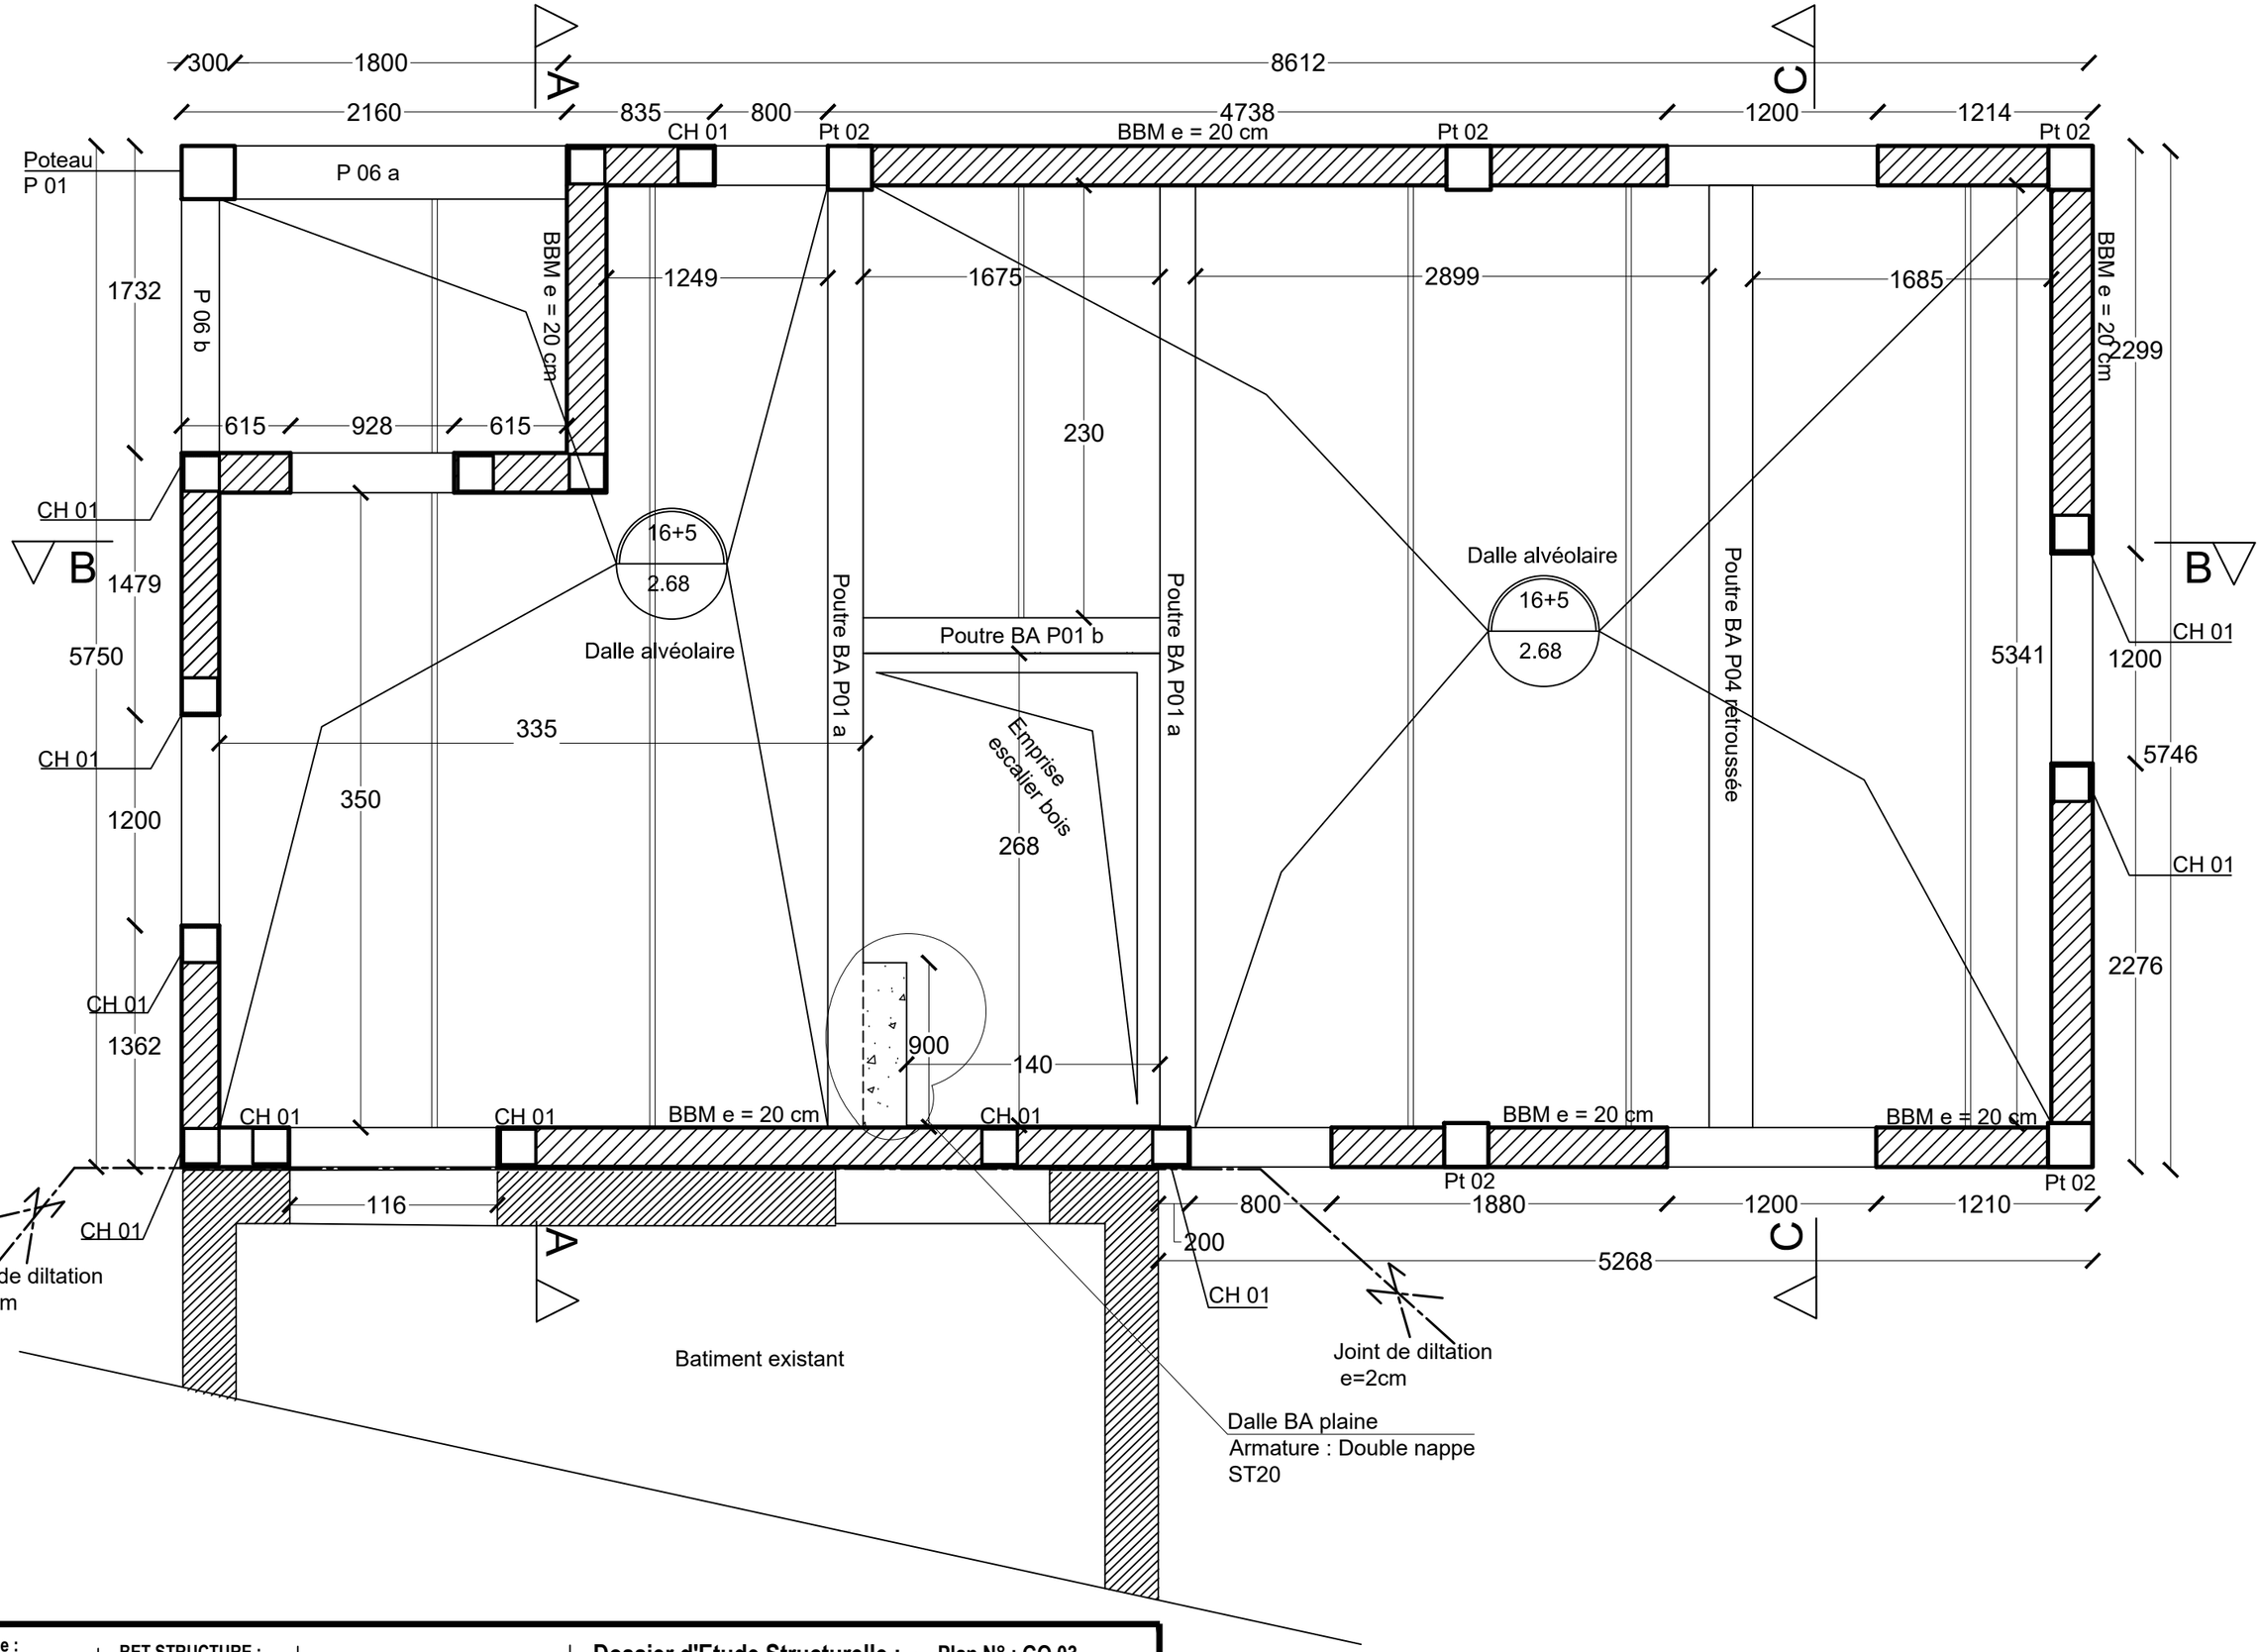

Maîtrise d'Ouvrage : Mr et Mme BRICOUT Avenue de Dunkerque 62520, Le Touquet-Paris-Plage.	**BET STRUCTURE :** J.K.F. STRUCTURE 92 Bd du GLE du Gaulle 59100 Roubaix	Extension d'une habitation existante en R-1;RDC;Comble	**Dossier d'Etude Structurelle :** Ph rdc	**Plan N° : GO 03** Ech : 1/50

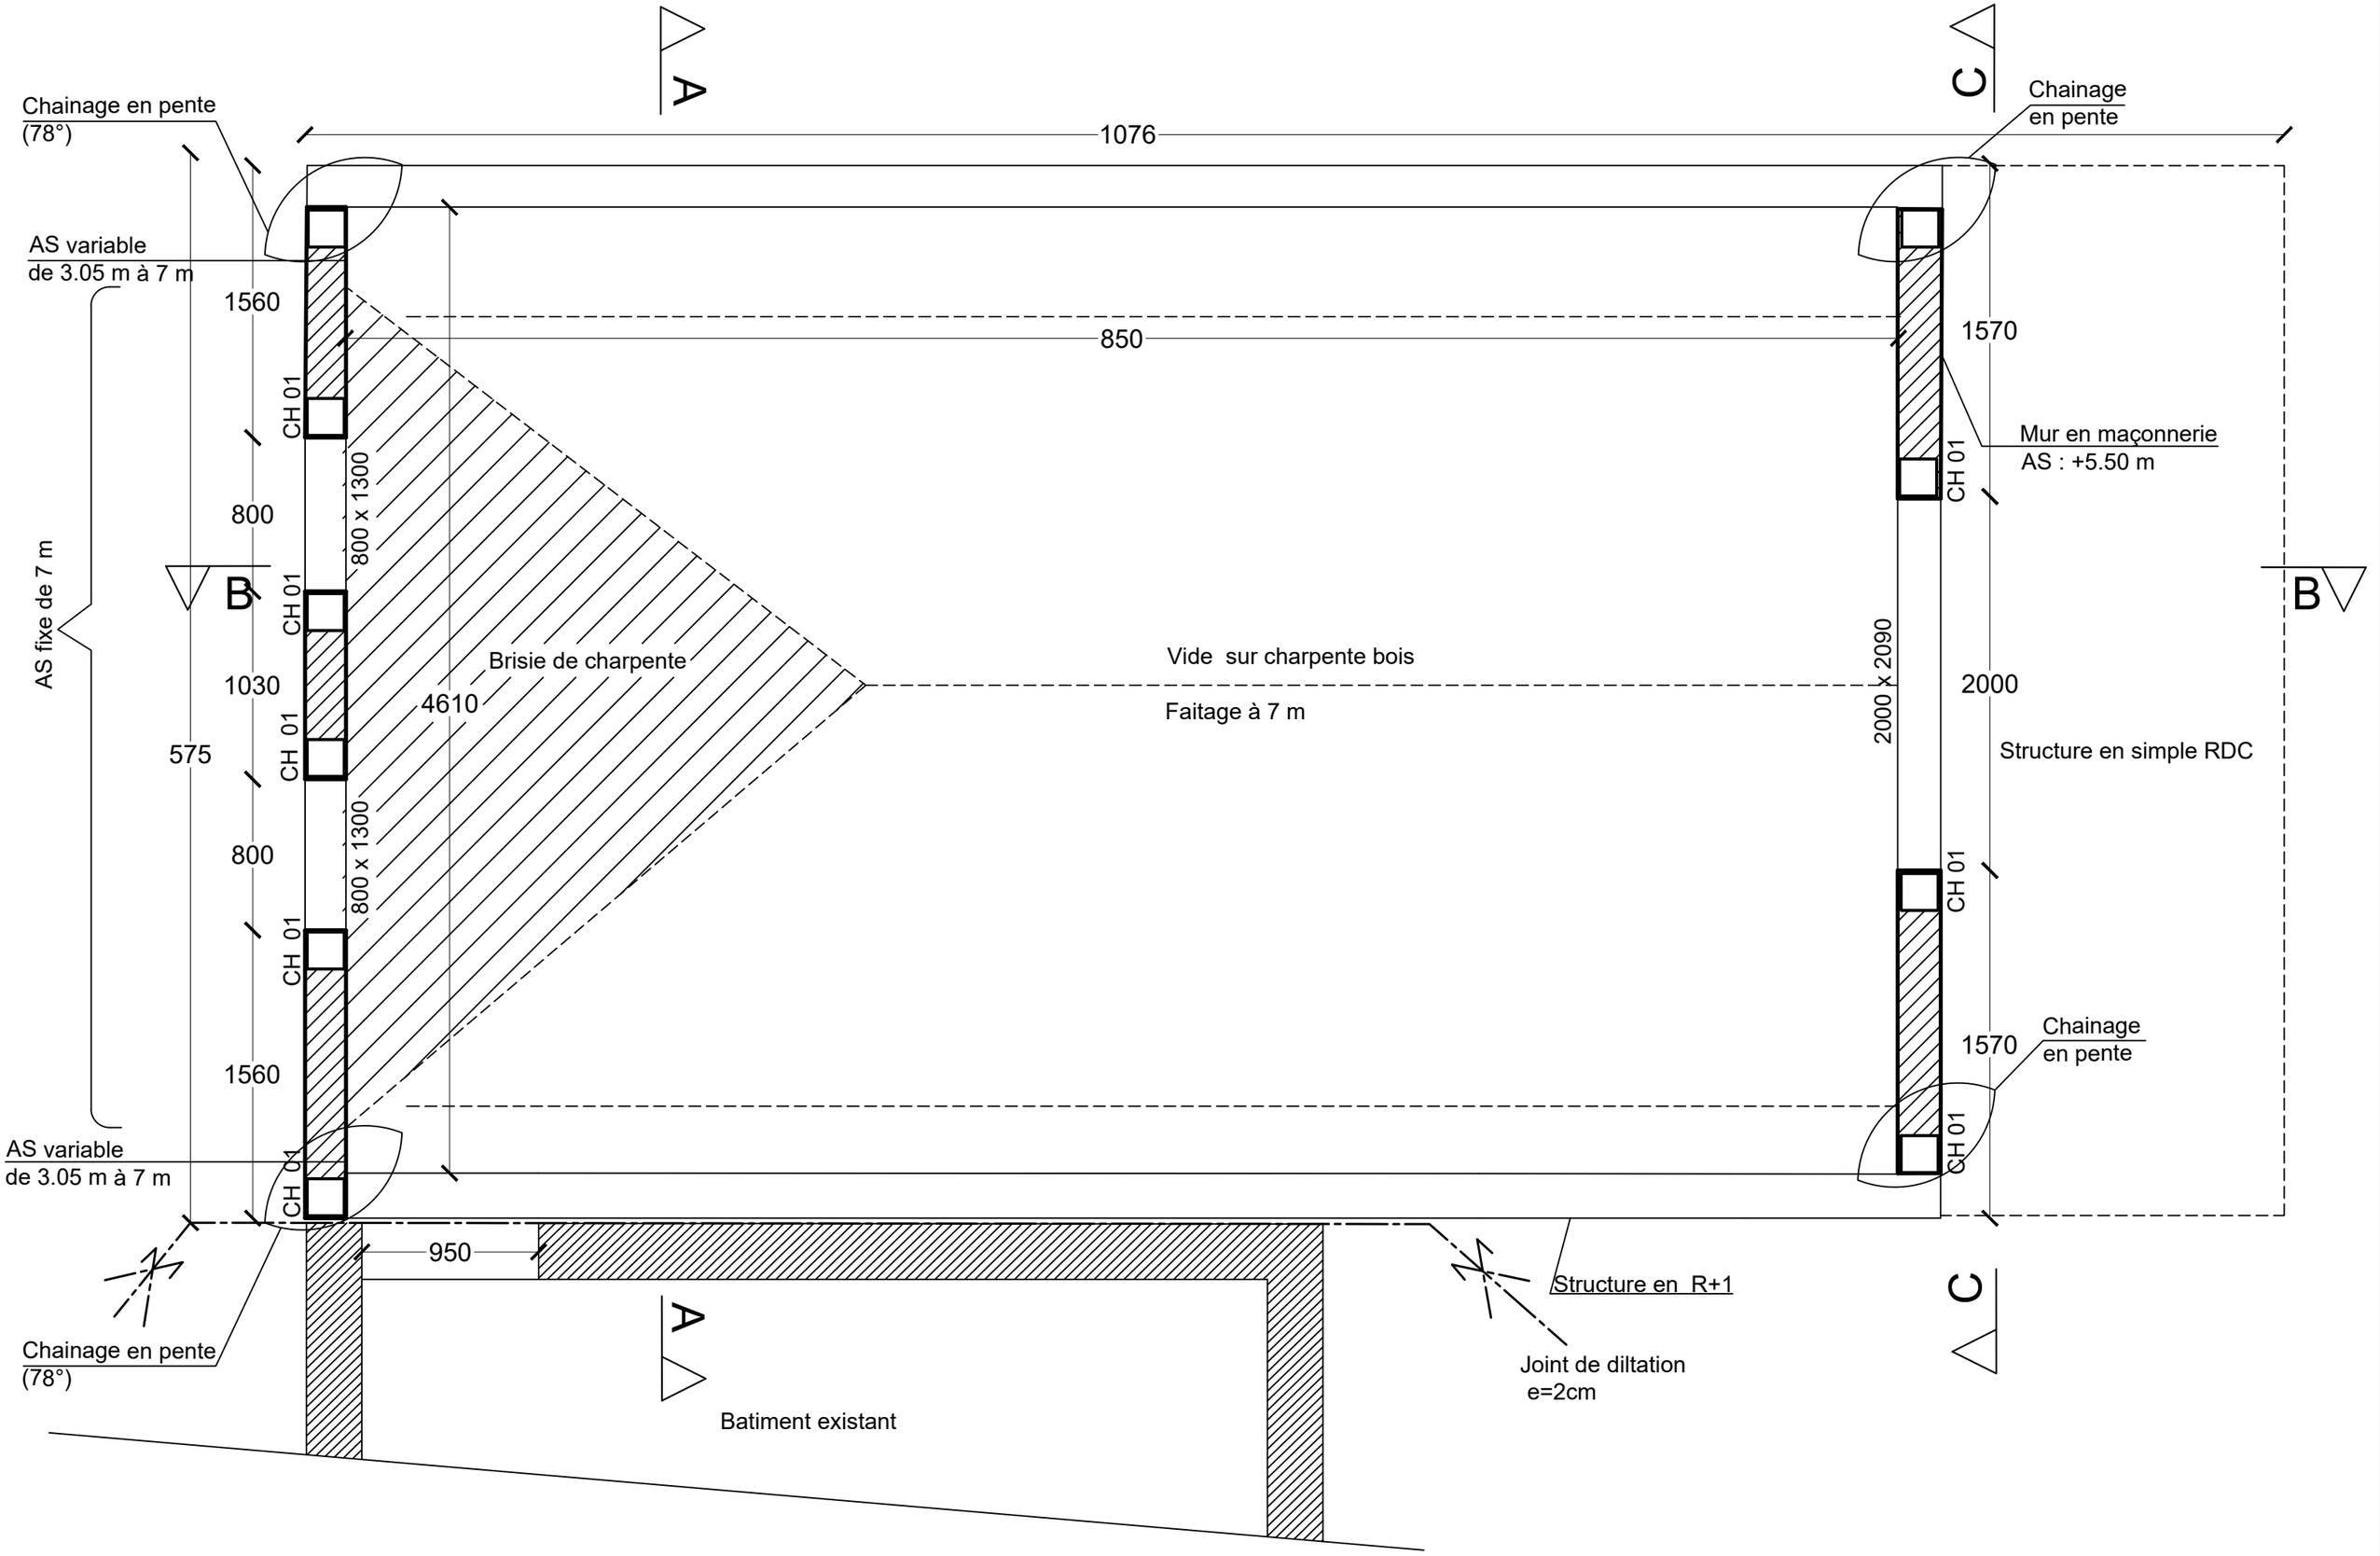


Maîtrise d'Ouvrage : Mr et Mme BRICOUT Avenue de Dunkerque 62520, Le Touquet-Paris-Plage.	**BET STRUCTURE :** J.K.F. STRUCTURE 92 Bd du GLE du Gaulle 59100 Roubaix	Extension d'une habitation existante en R-1;RDC;Comble	**Dossier d'Etude Structurelle :** Ph comble	**Plan N° : GO 04** Ech : 1/50

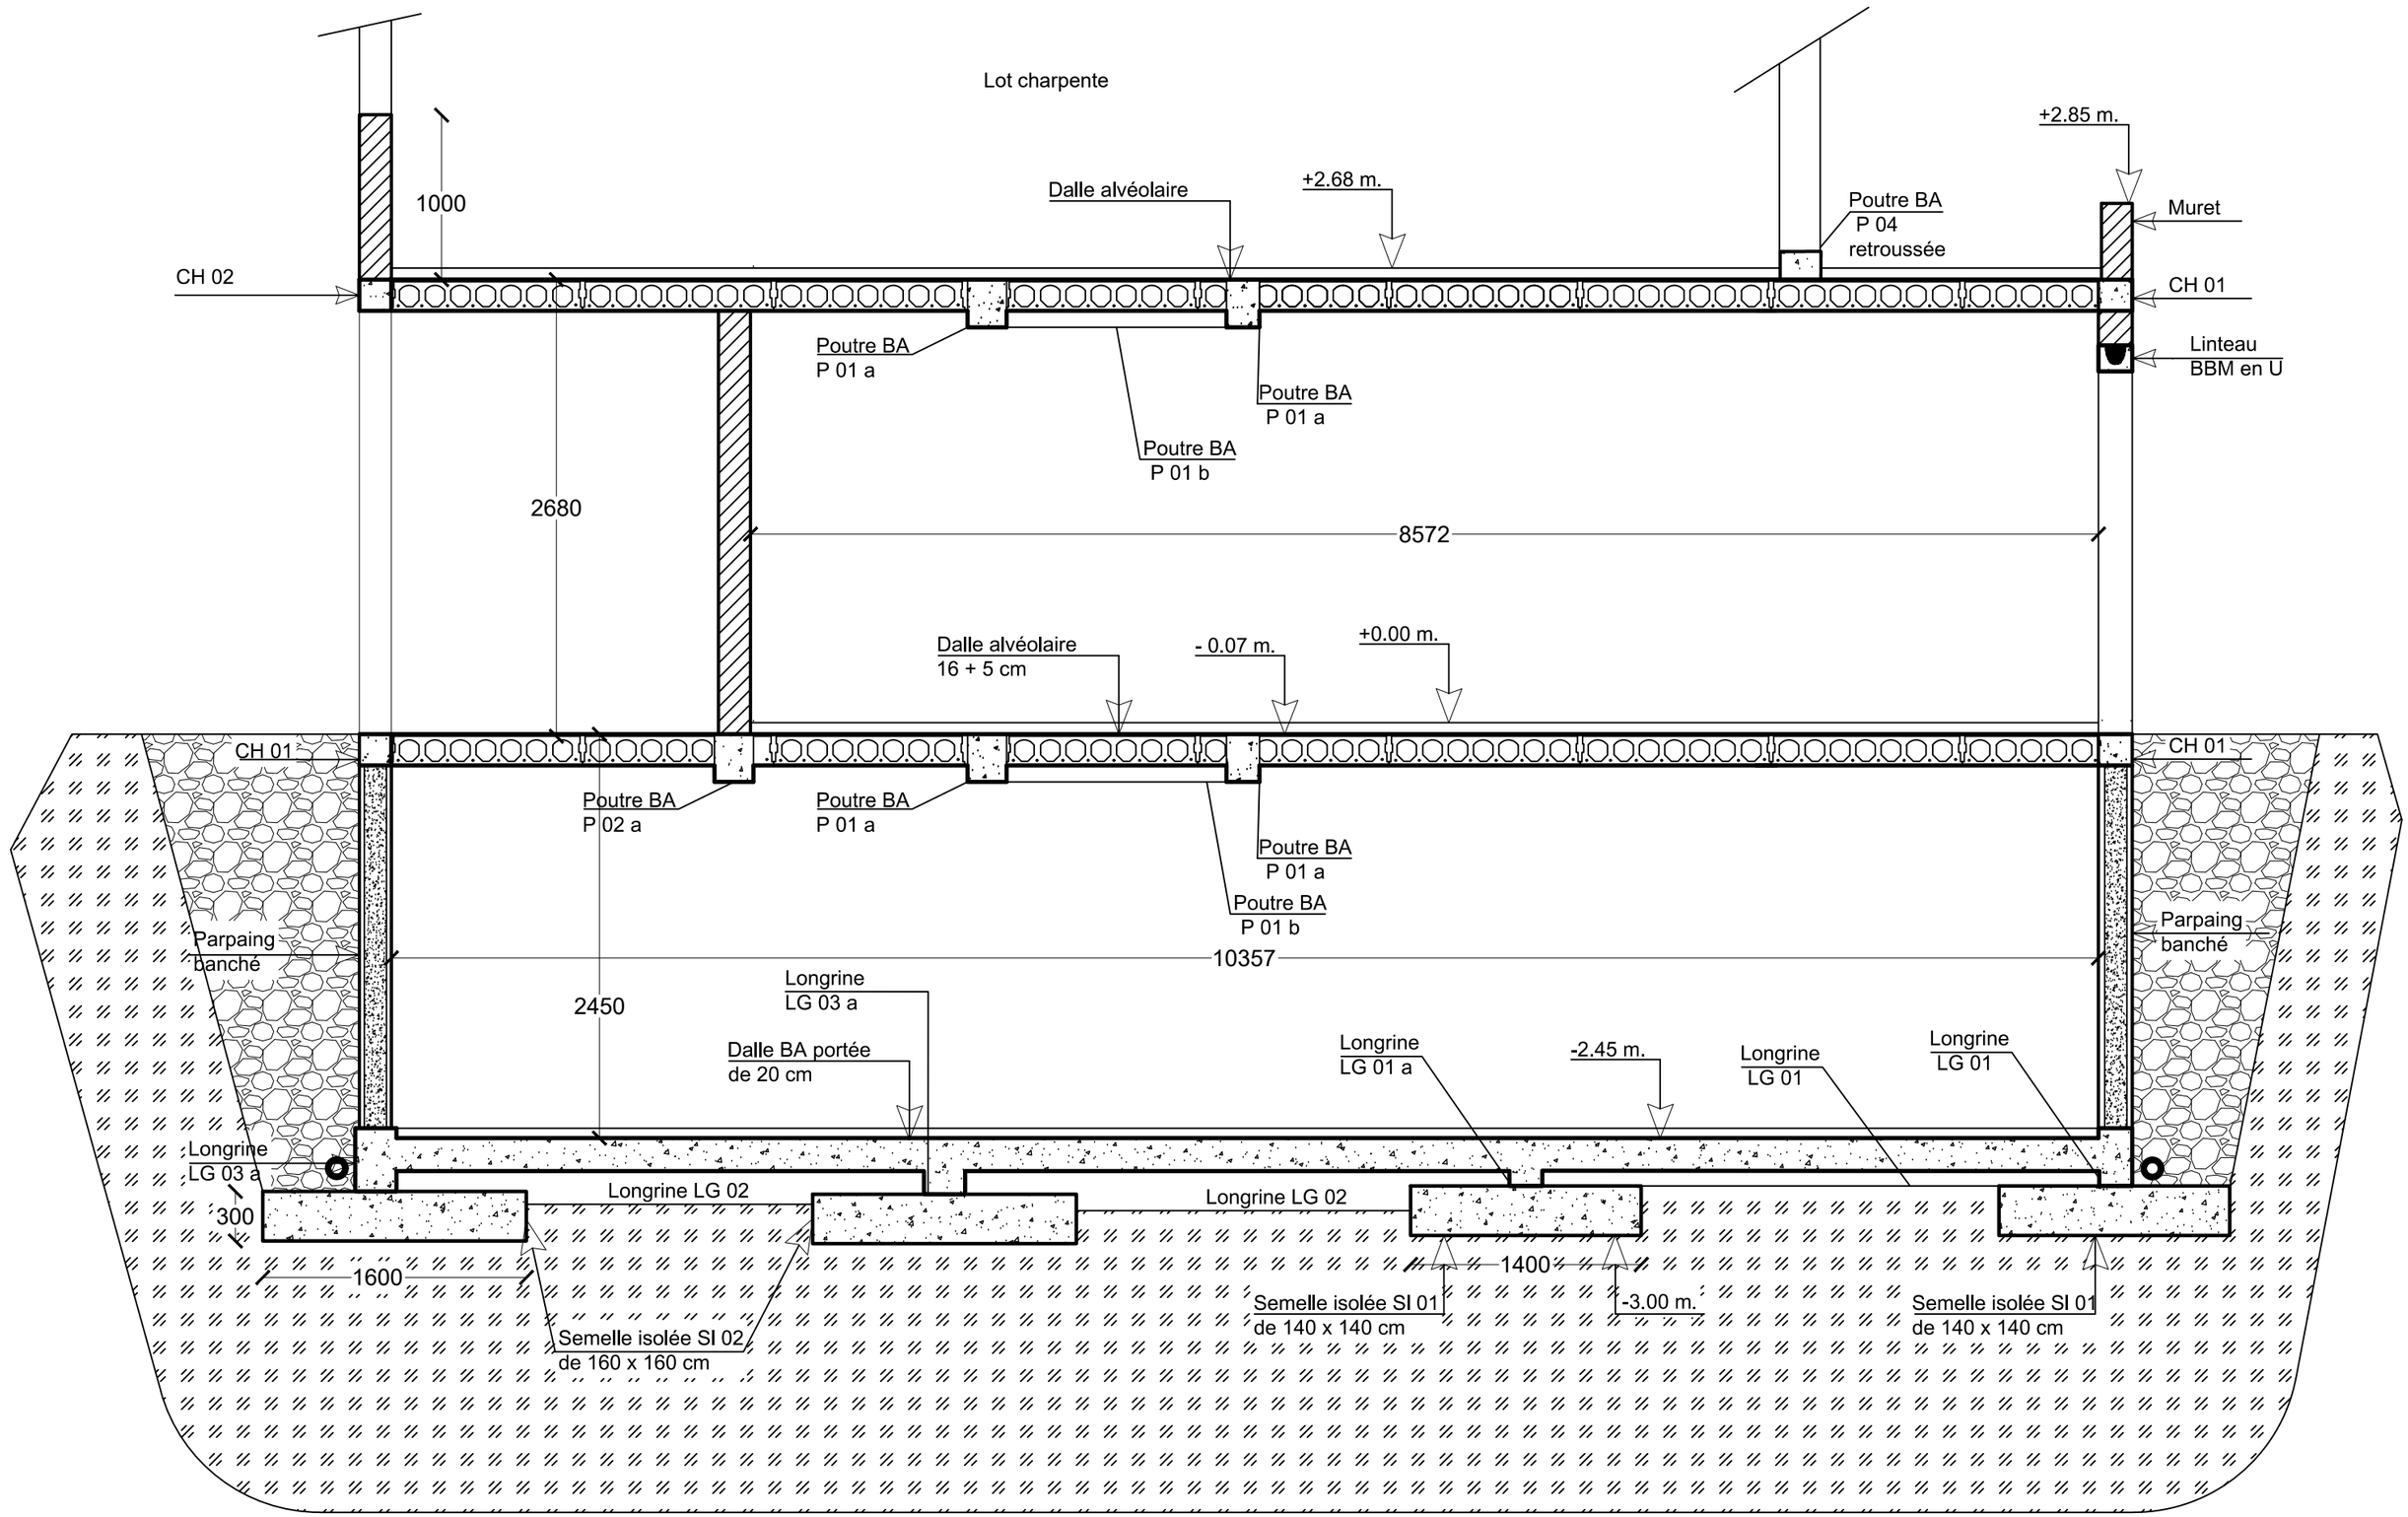

Coupe B-B

Maîtrise d'Ouvrage : Mr et Mme BRICOUT Avenue de Dunkerque 62520, Le Touquet-Paris-Plage.	**BET STRUCTURE :** J.K.F. STRUCTURE 92 Bd du GLE du Gaulle 59100 Roubaix	Extension d'une habitation existante en R-1;RDC;Comble	**Dossier d'Etude Structurelle :** Coupe B-B	**Plan N° : GO 05** Ech : 1/50

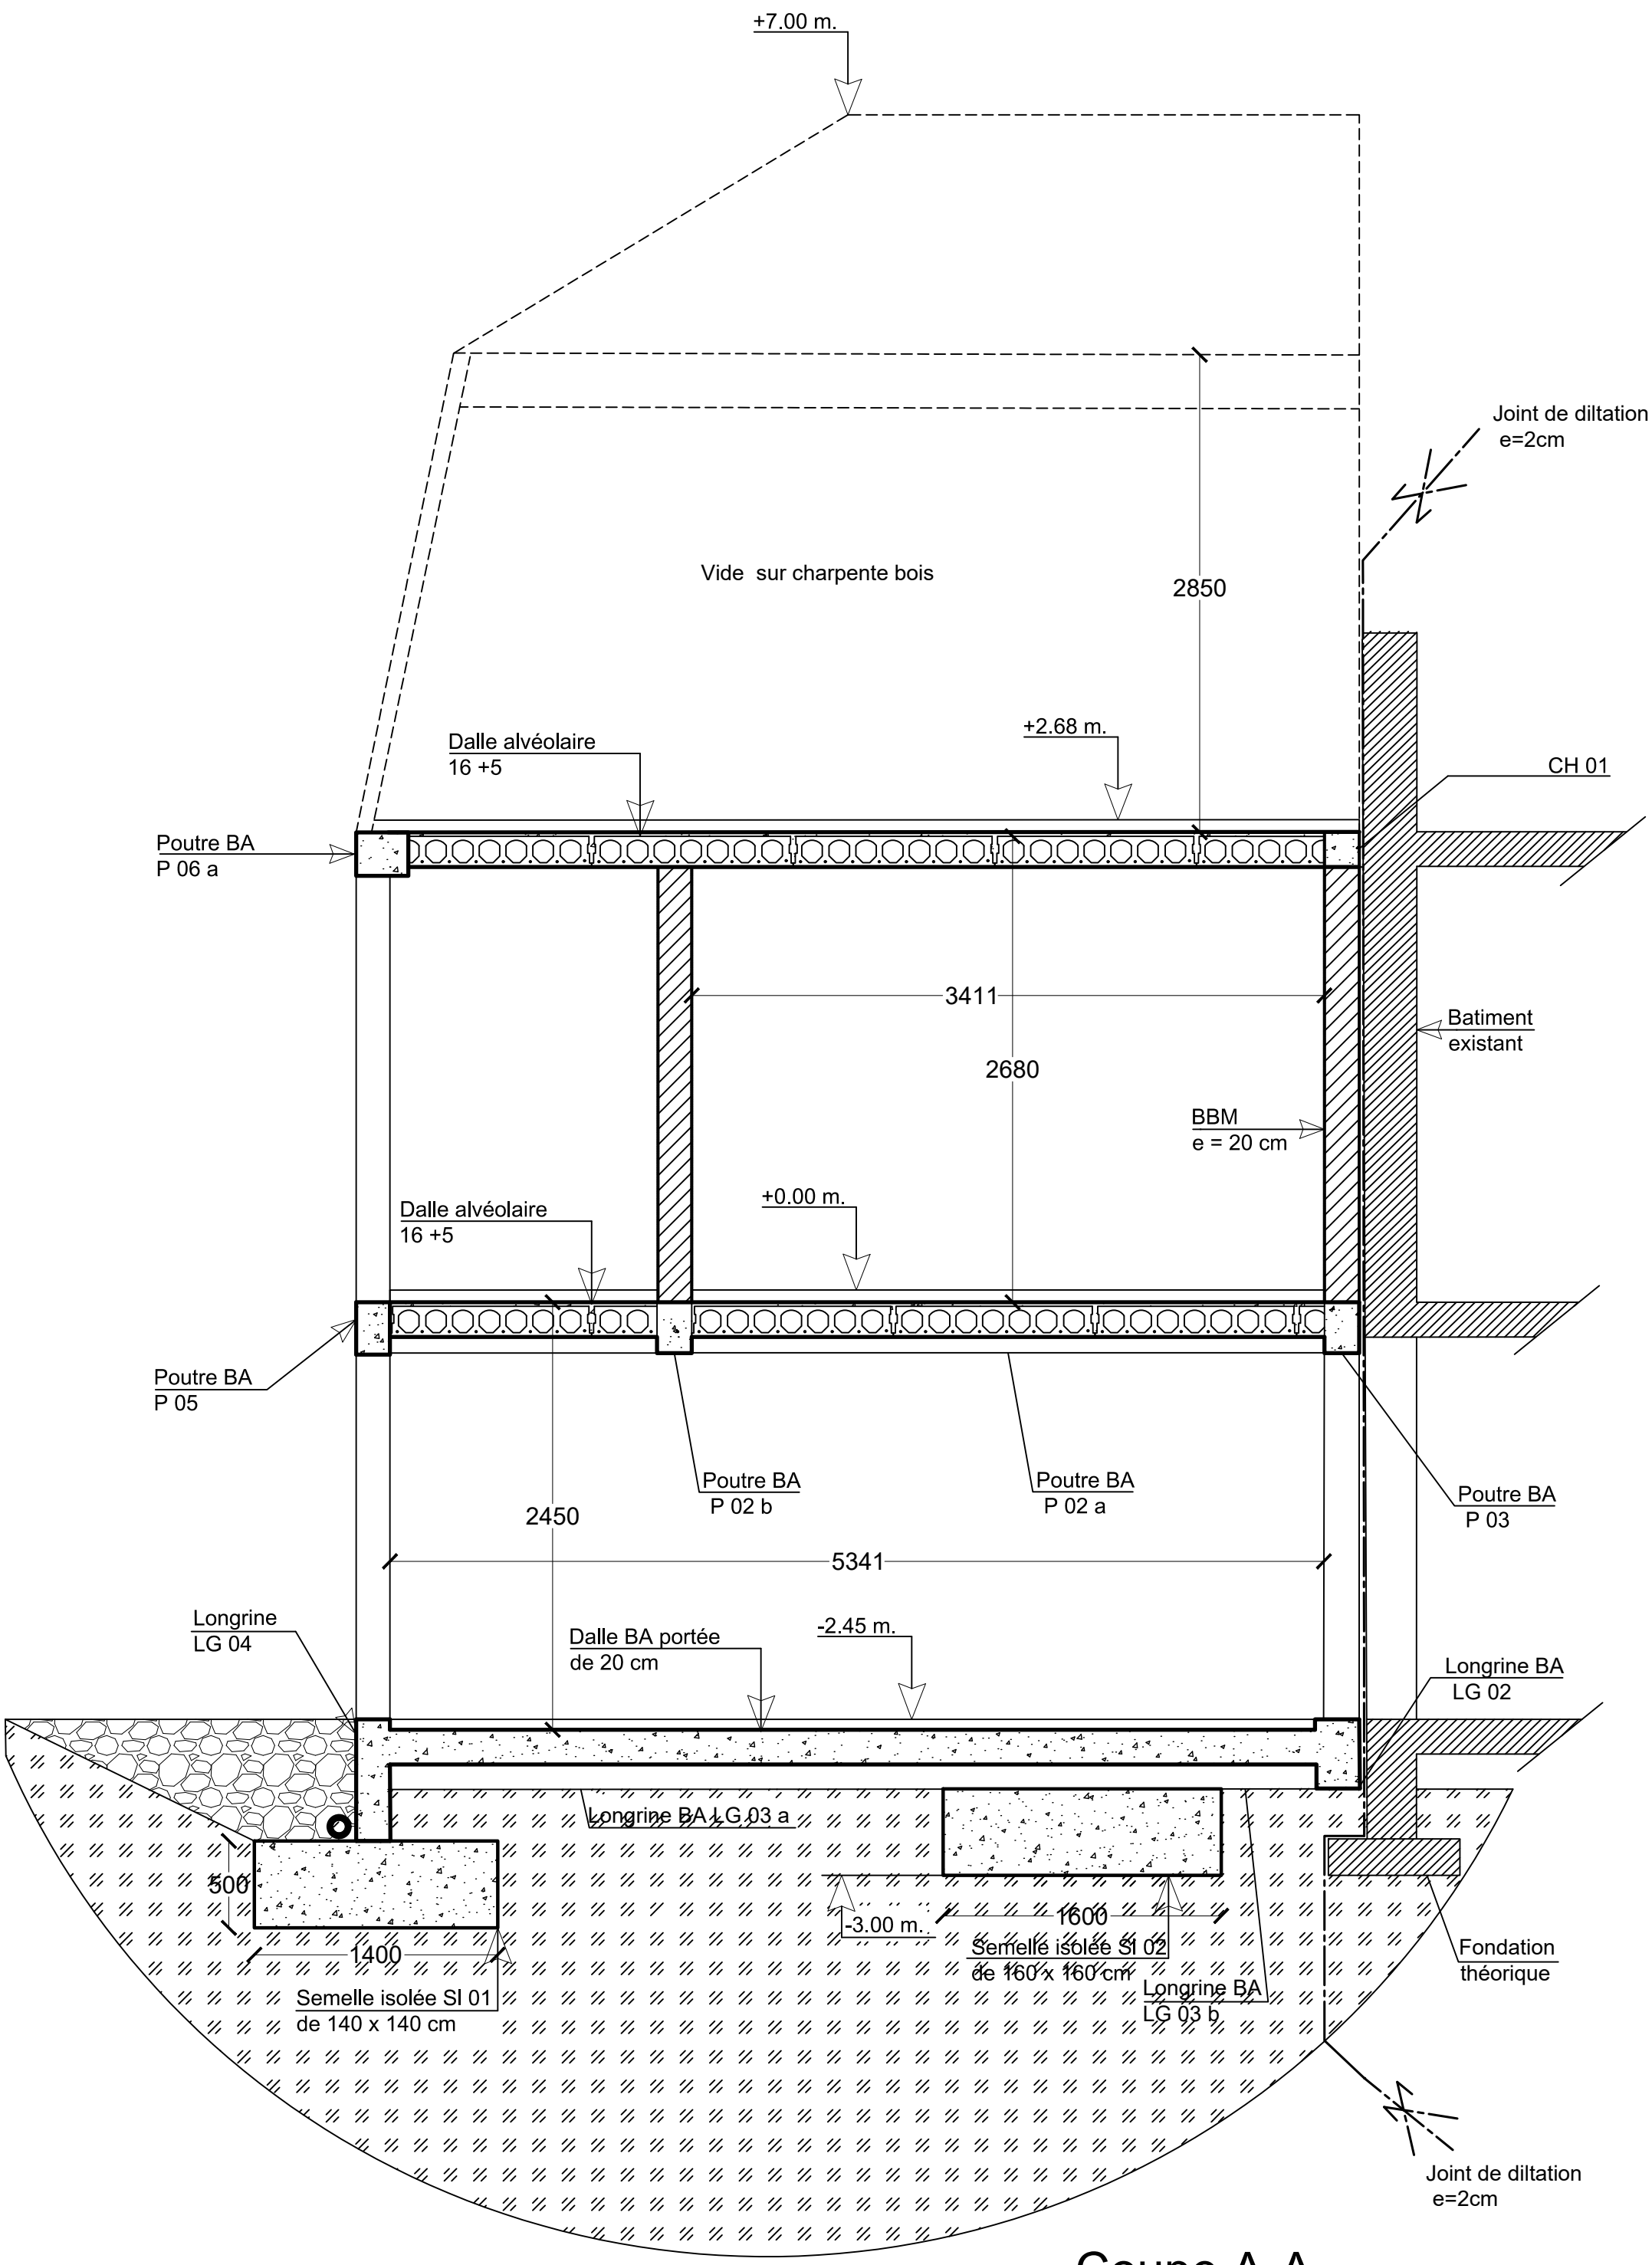

Coupe A-A


Maîtrise d'Ouvrage :
Mr et Mme BRICOUT
Avenue de Dunkerque
62520, Le Touquet-Paris-Plage.

BET STRUCTURE :
J.K.F. STRUCTURE
92 Bd du GLE du Gaulle
59100 Roubaix

Extension d'une habitation existante en R-1;RDC;Comble

Dossier d'Etude Structurelle :
Coupe A-A

Plan N° : GO 06
Ech : 1/50

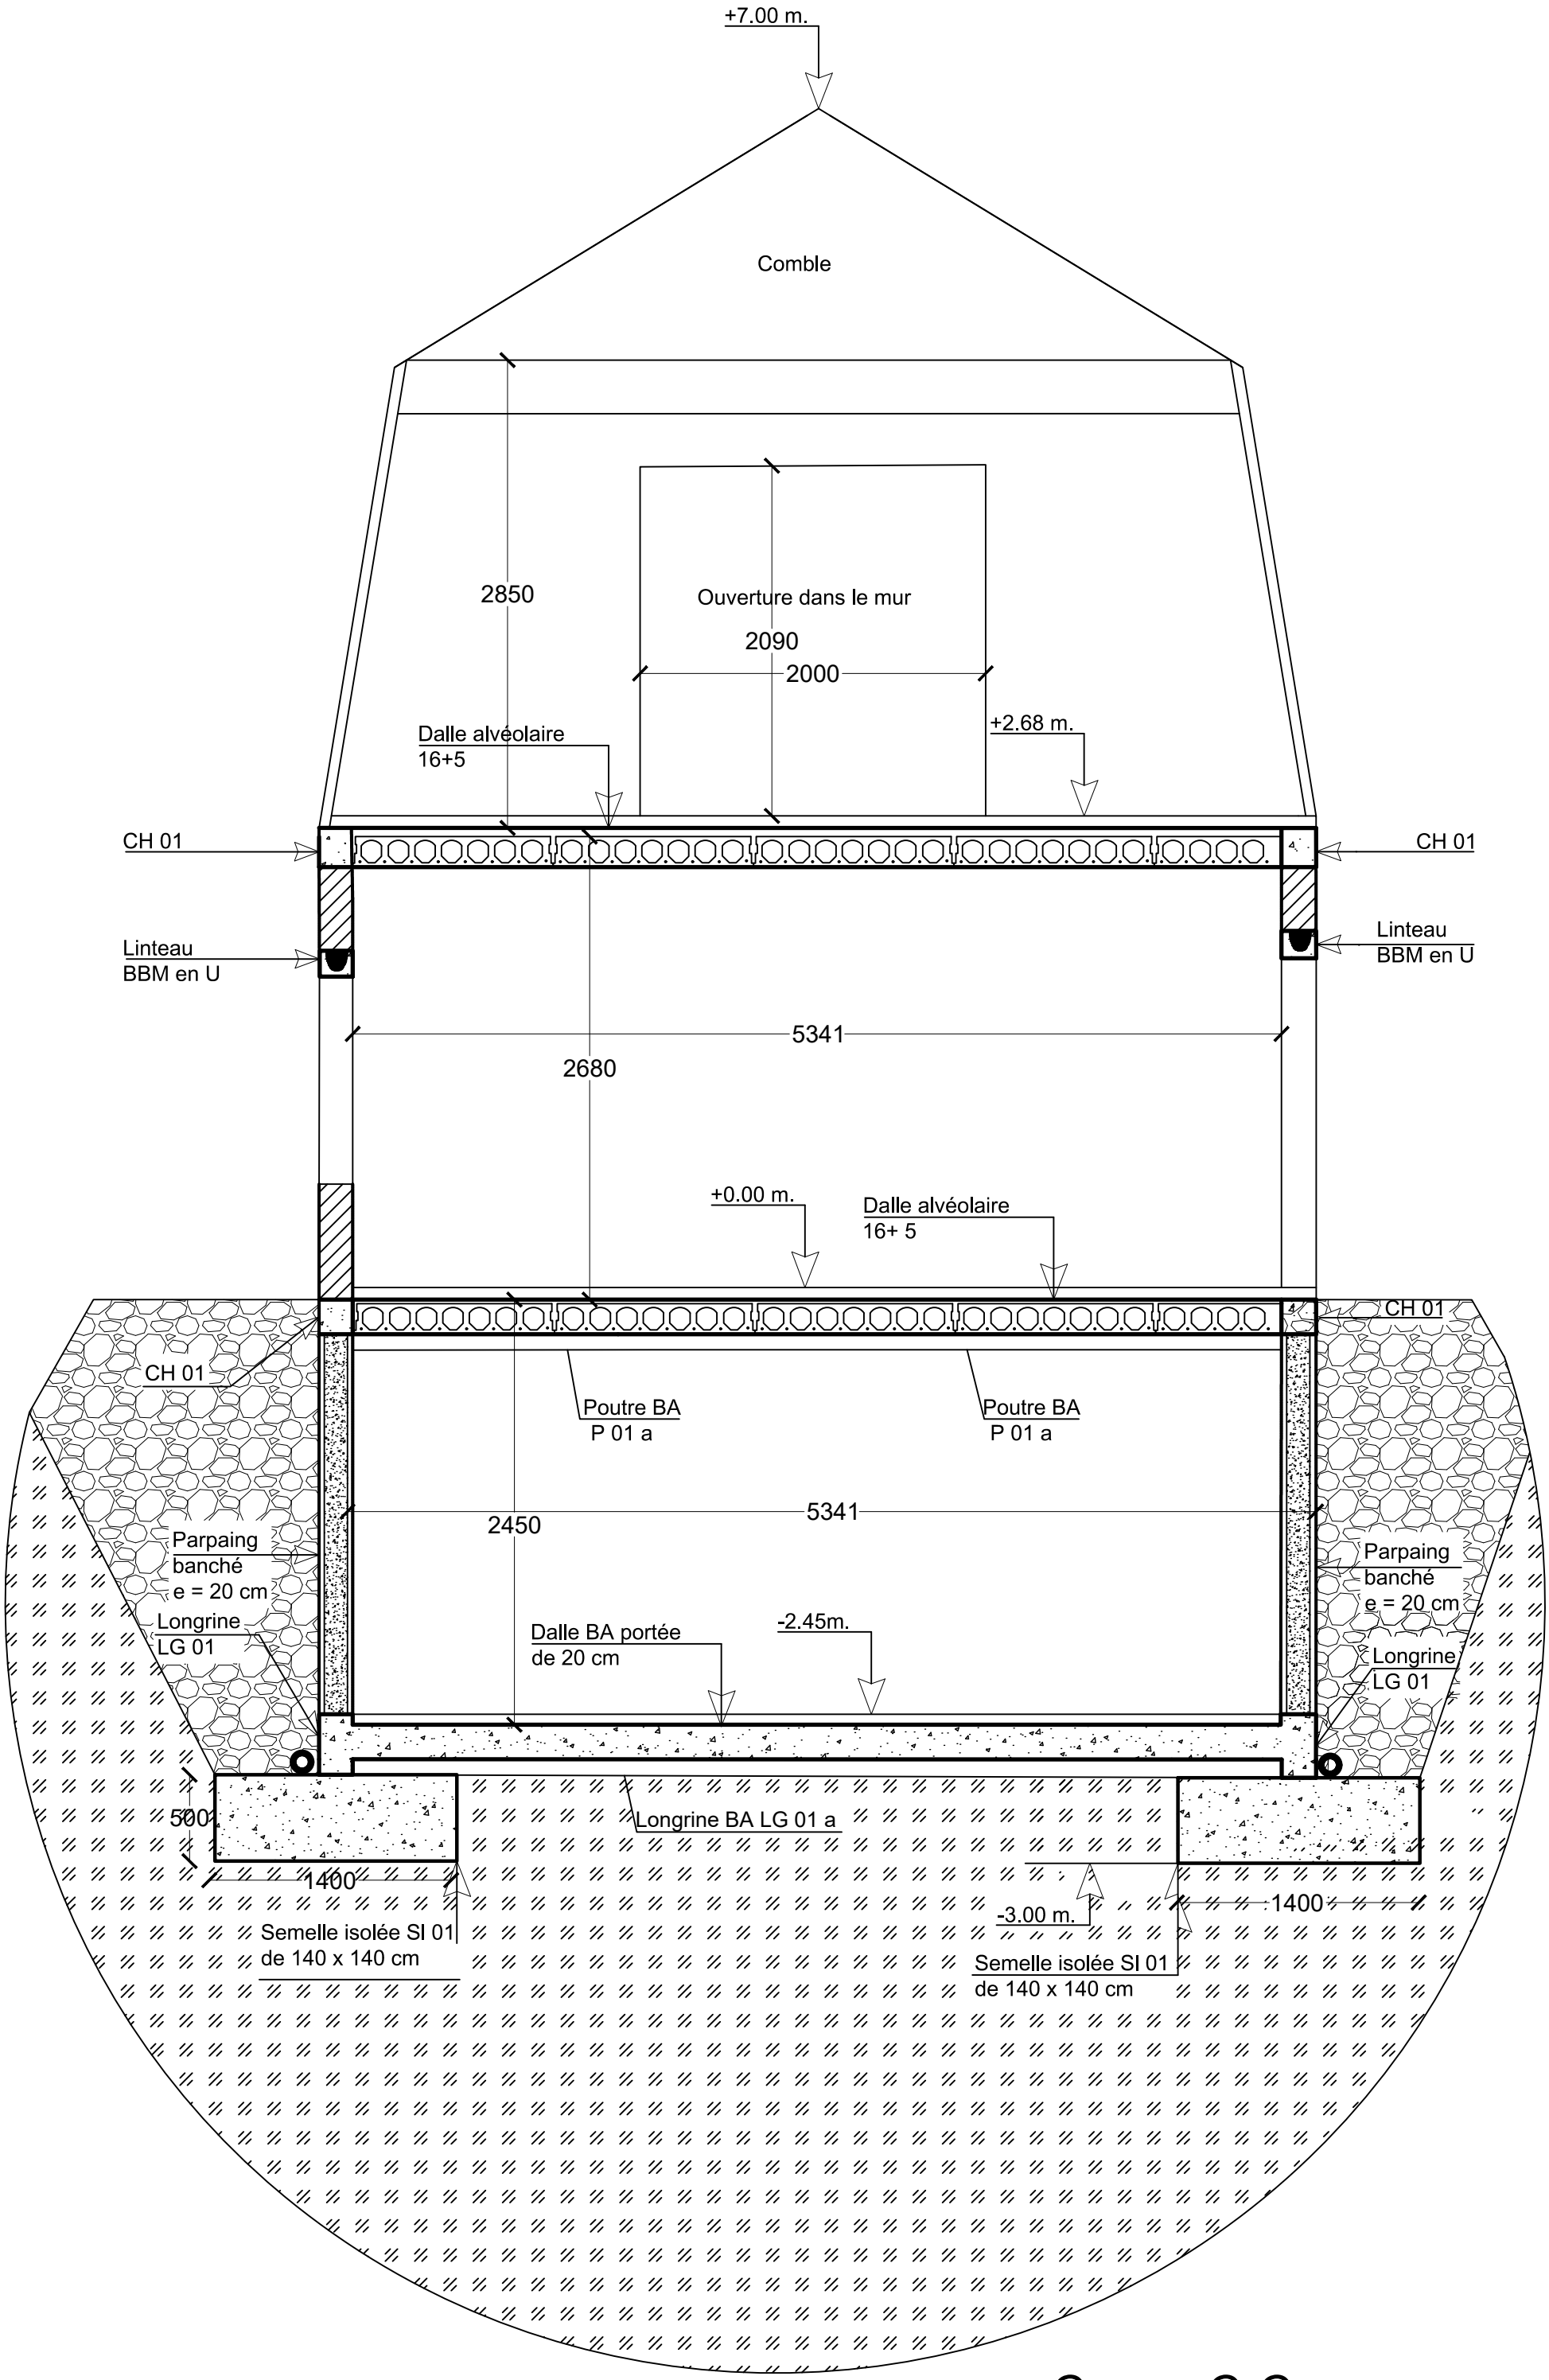

Coupe C-C


Maîtrise d'Ouvrage :
Mr et Mme BRICOUT
Avenue de Dunkerque
62520, Le Touquet-Paris-Plage.

BET STRUCTURE :
J.K.F. STRUCTURE
92 Bd du GLE du Gaulle
59100 Roubaix

Extension d'une habitation existante en R-1;RDC;Comble


Dossier d'Etude Structurelle :
Coupe C-C

Plan N° : GO 07
Ech : 1/50

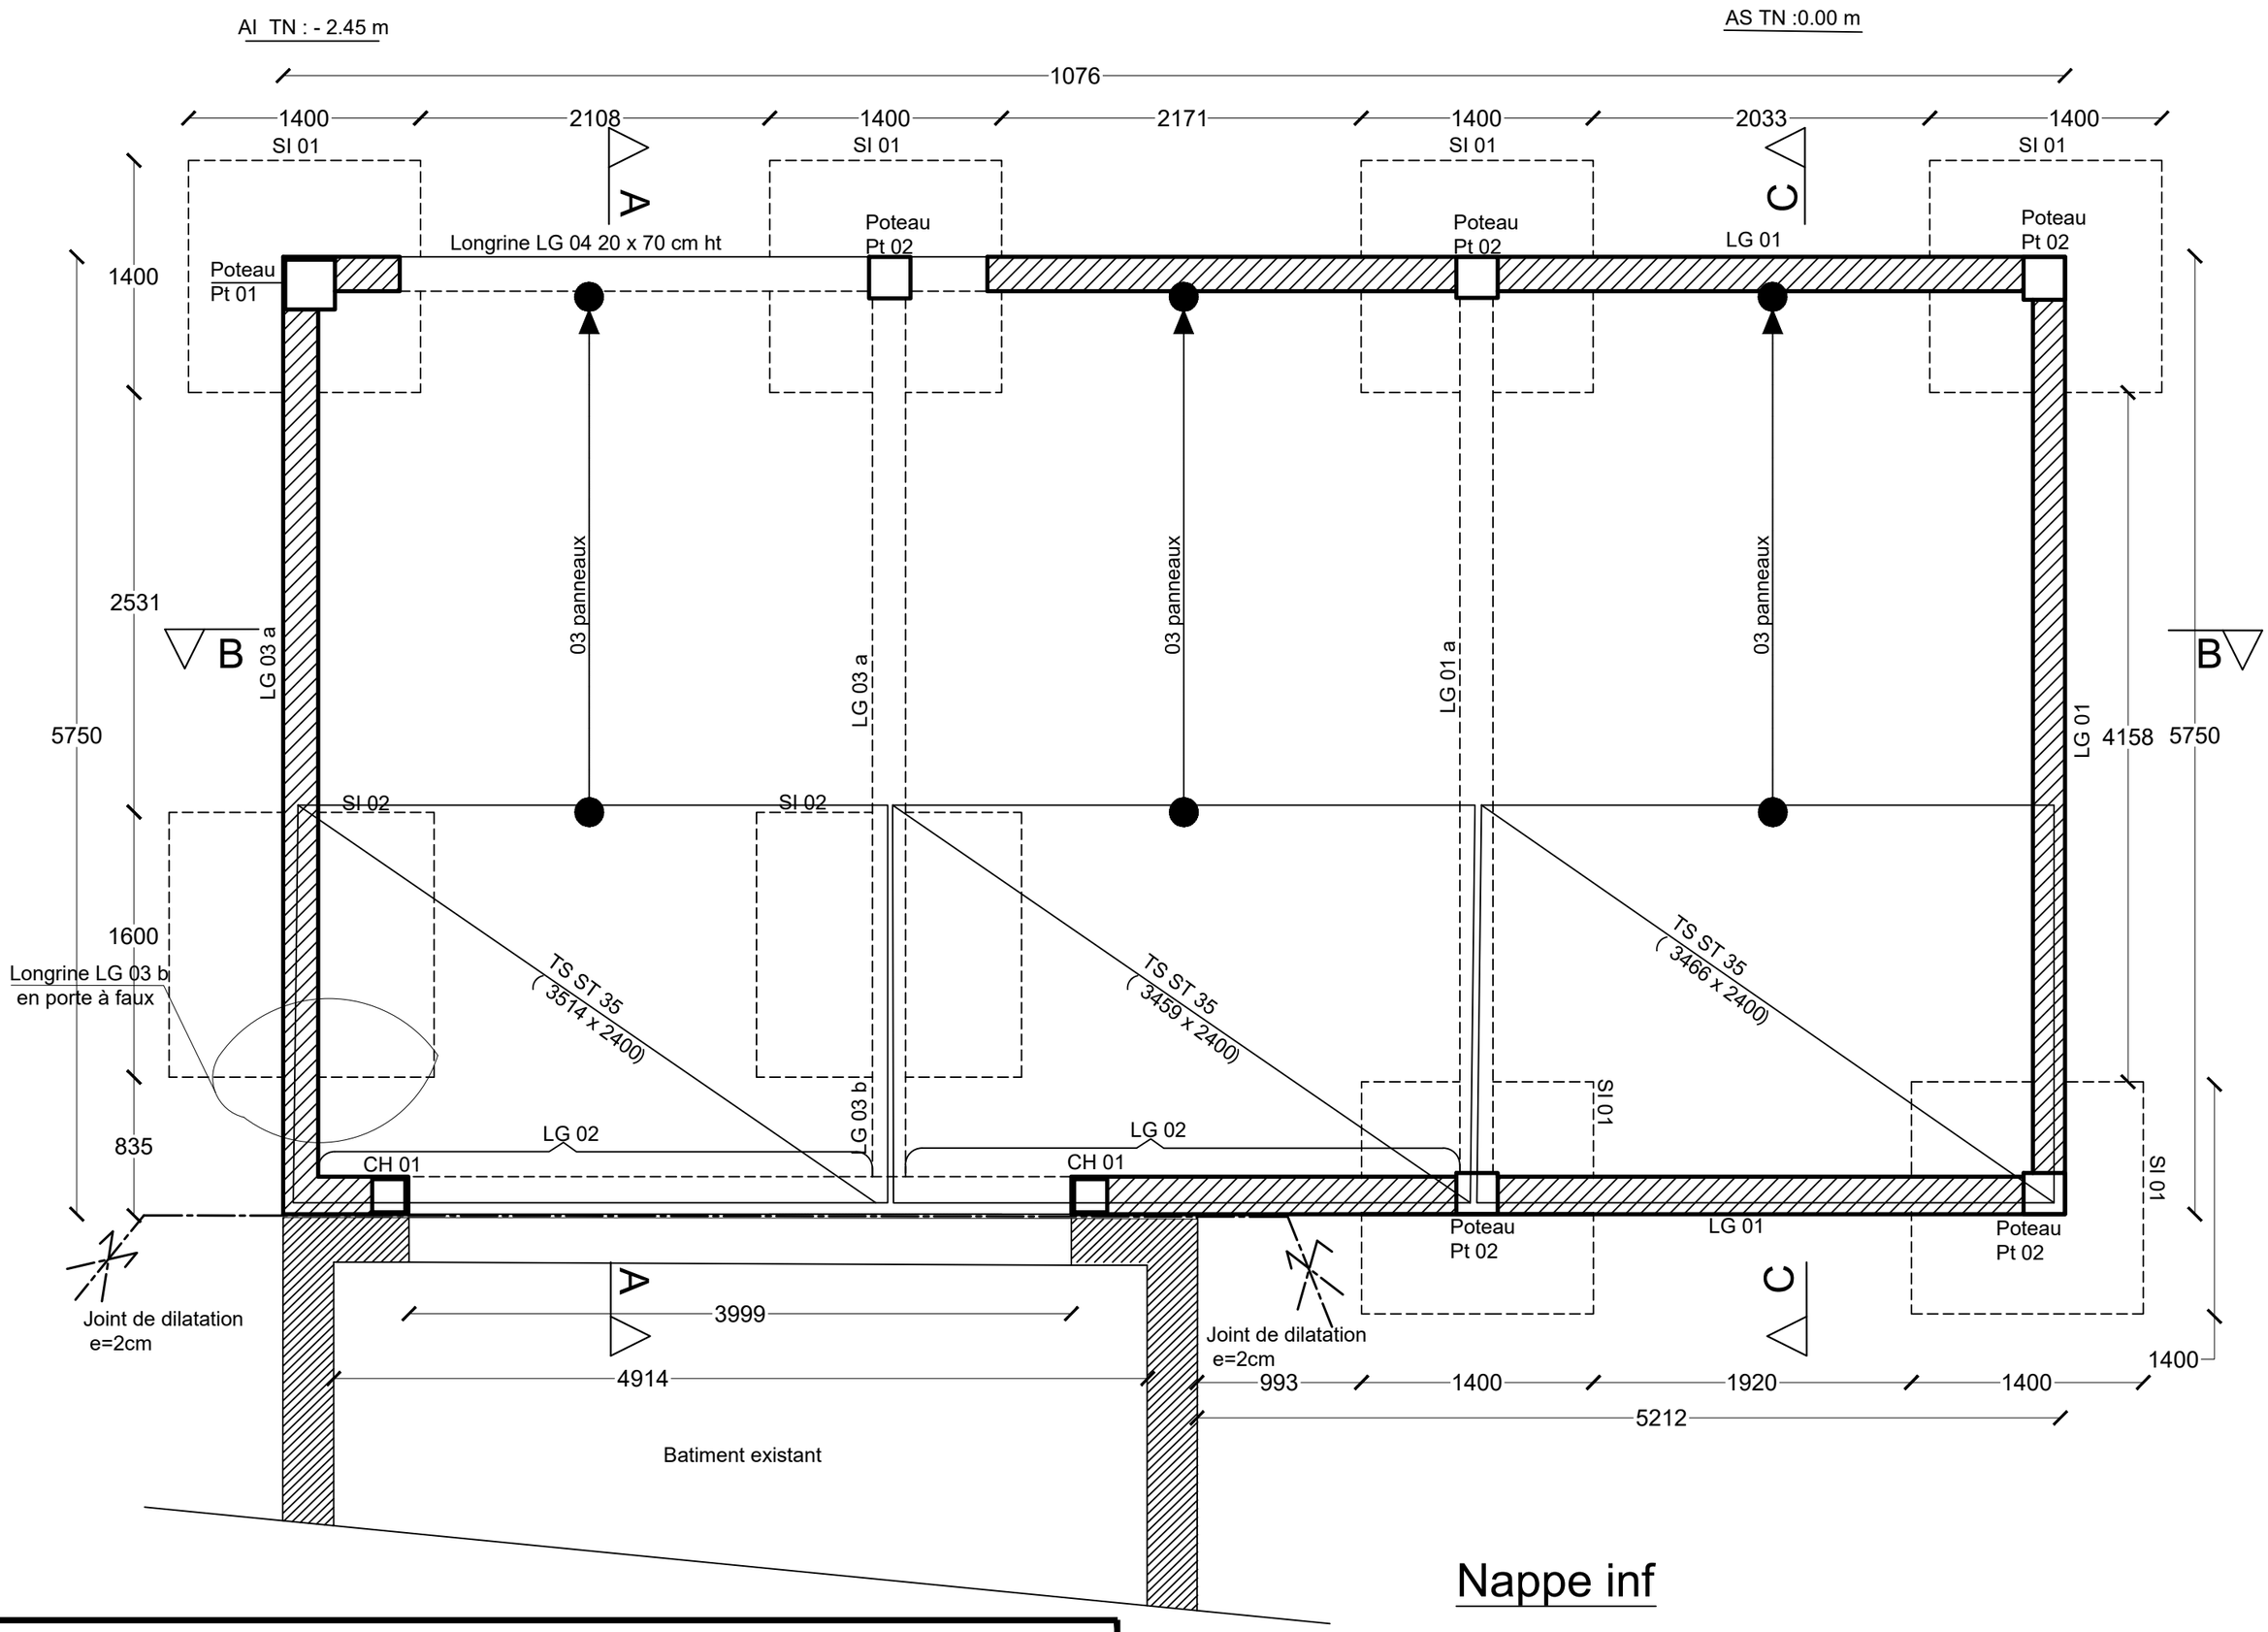

Nappe inf

Maîtrise d'Ouvrage : Mr et Mme BRICOUT Avenue de Dunkerque 62520, Le Touquet-Paris-Plage.	**BET STRUCTURE :** J.K.F. STRUCTURE 92 Bd du GLE du Gaulle 59100 Roubaix	Extension d'une habitation existante en R-1;RDC;Comble	**Dossier d'Etude Structurelle :** Feraillage dalle BA Nappe inférieure	**Plan N° : GO 08** Ech : 1/50

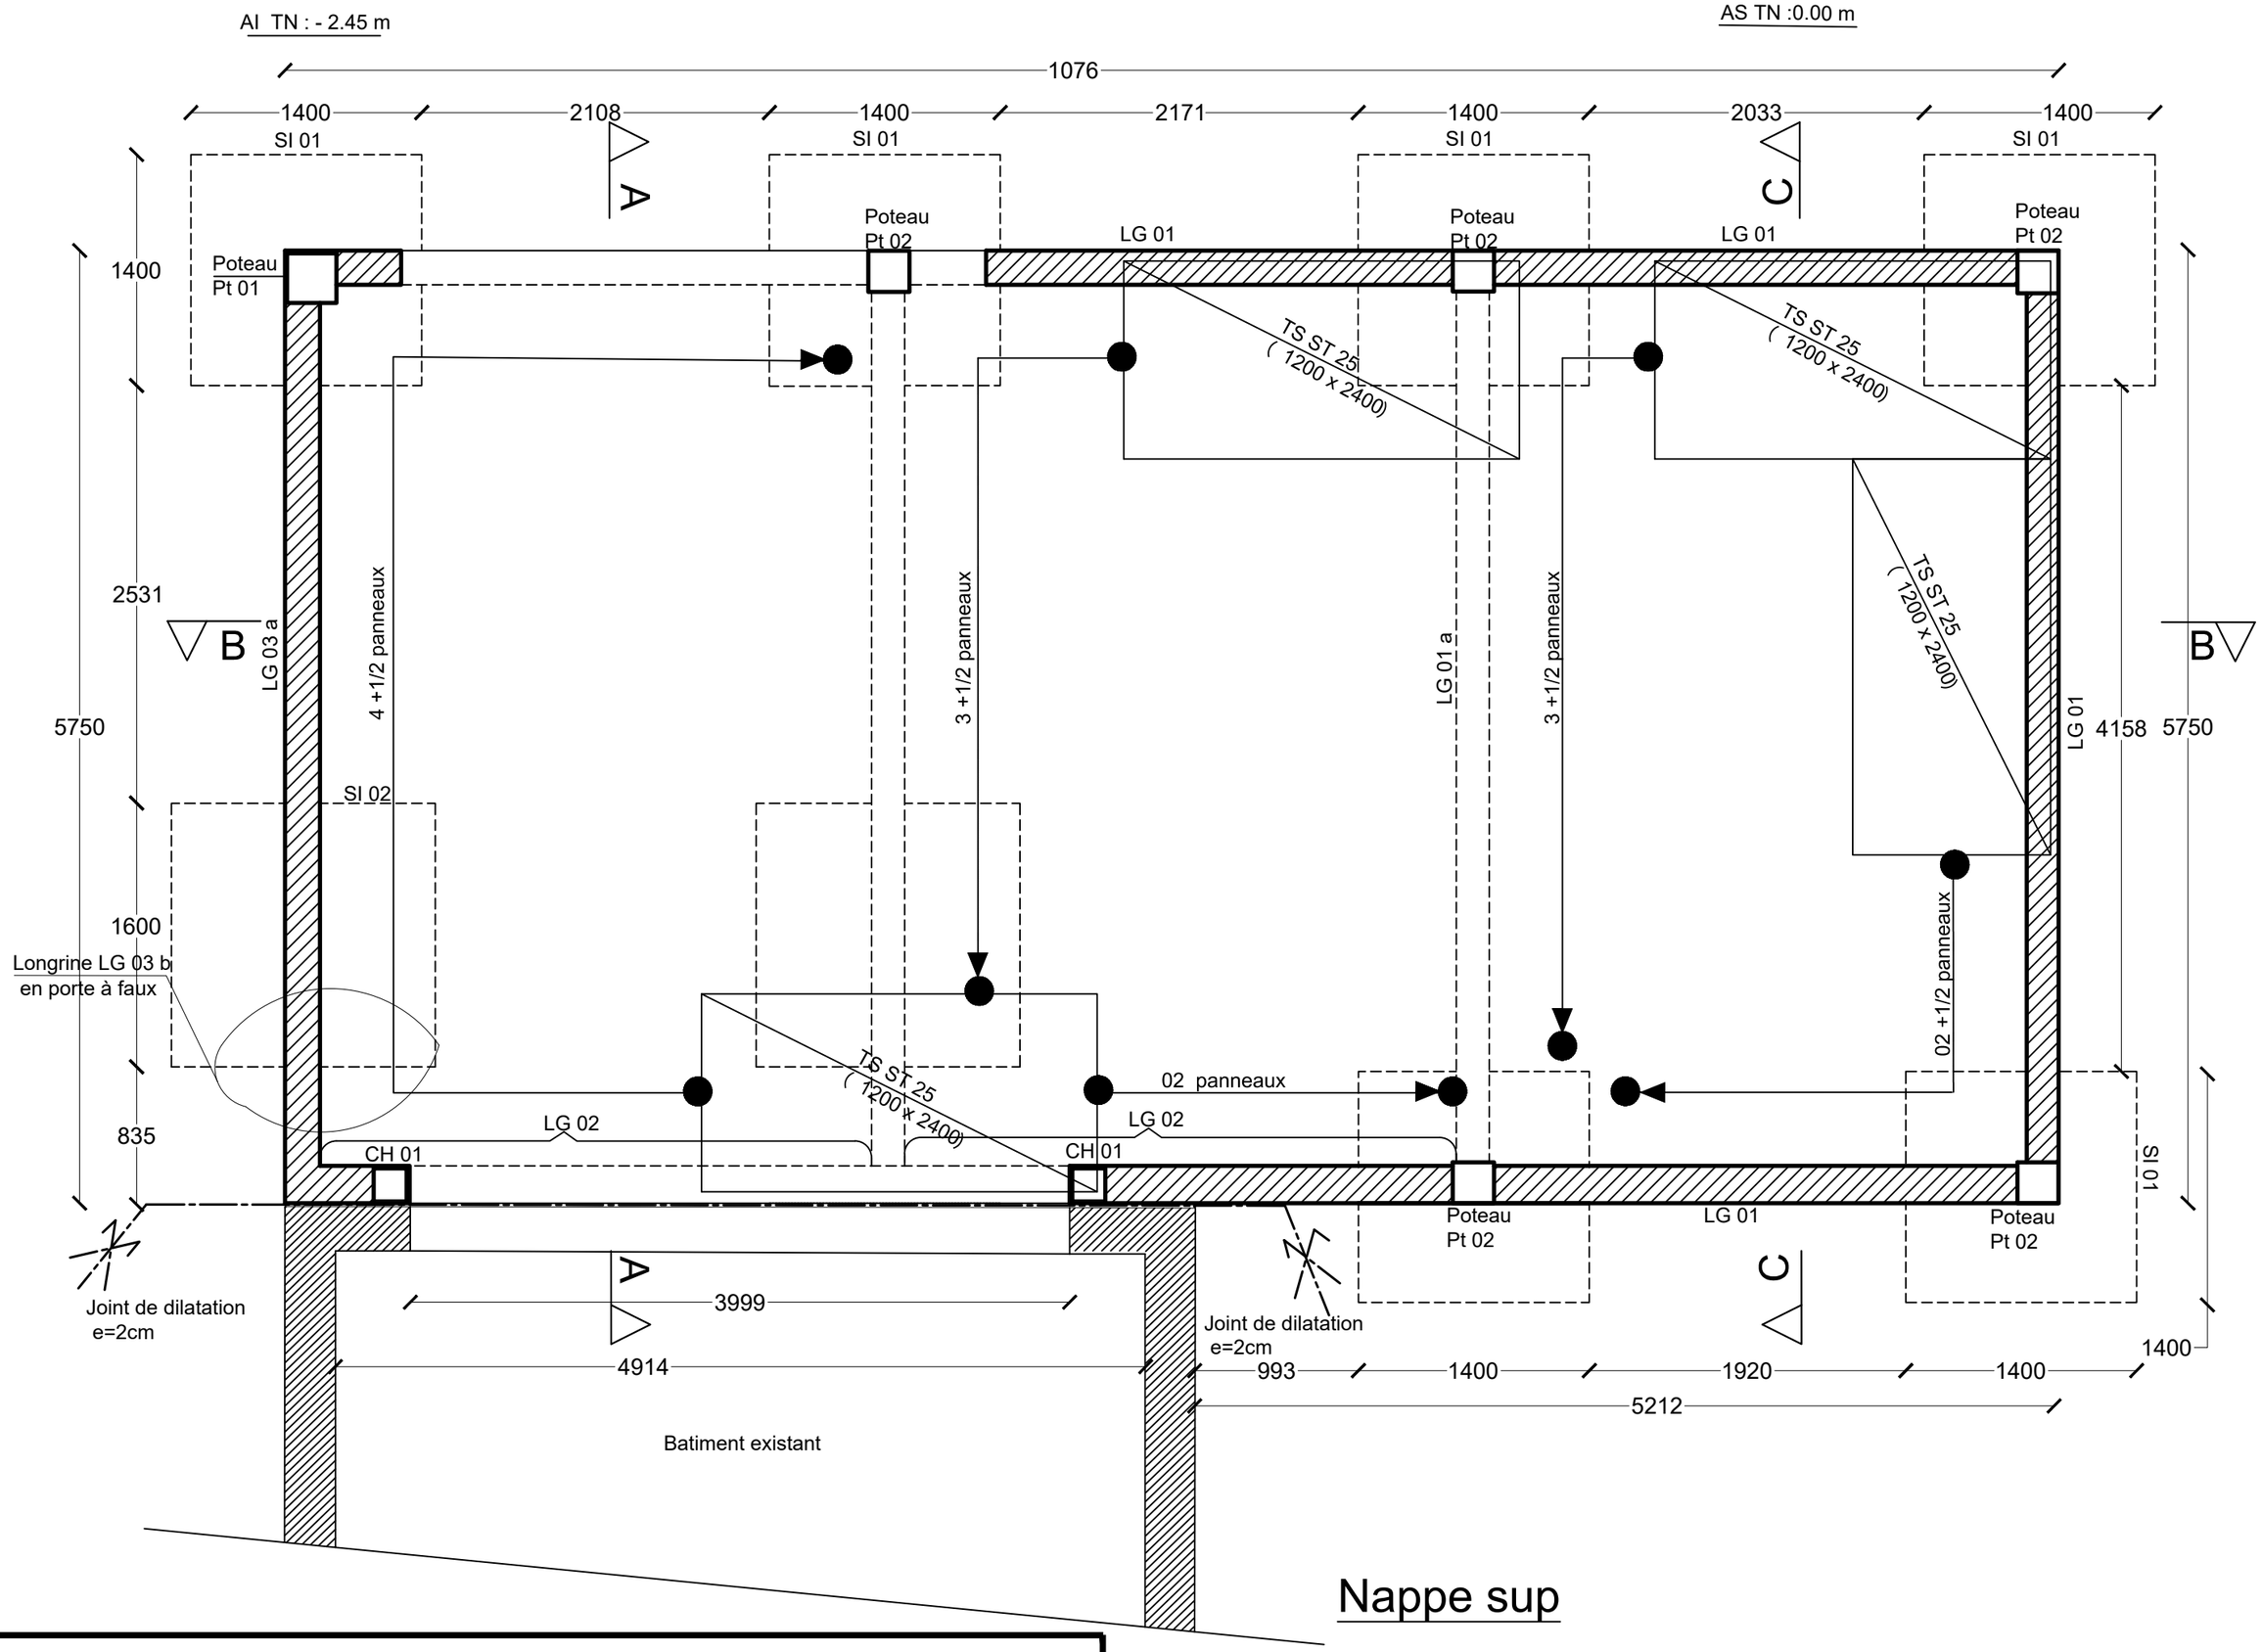

Maîtrise d'Ouvrage :
Mr et Mme BRICOUT
Avenue de Dunkerque
62520, Le Touquet-Paris-Plage.

BET STRUCTURE :
J.K.F. STRUCTURE
92 Bd du GLE du Gaulle
59100 Roubaix

Extension d'une habitation existante en R-1;RDC;Comble

Dossier d'Etude Structurelle :
Feraillage dalle BA
Nappe supérieure

Plan N° : GO 09
Ech : 1/50