
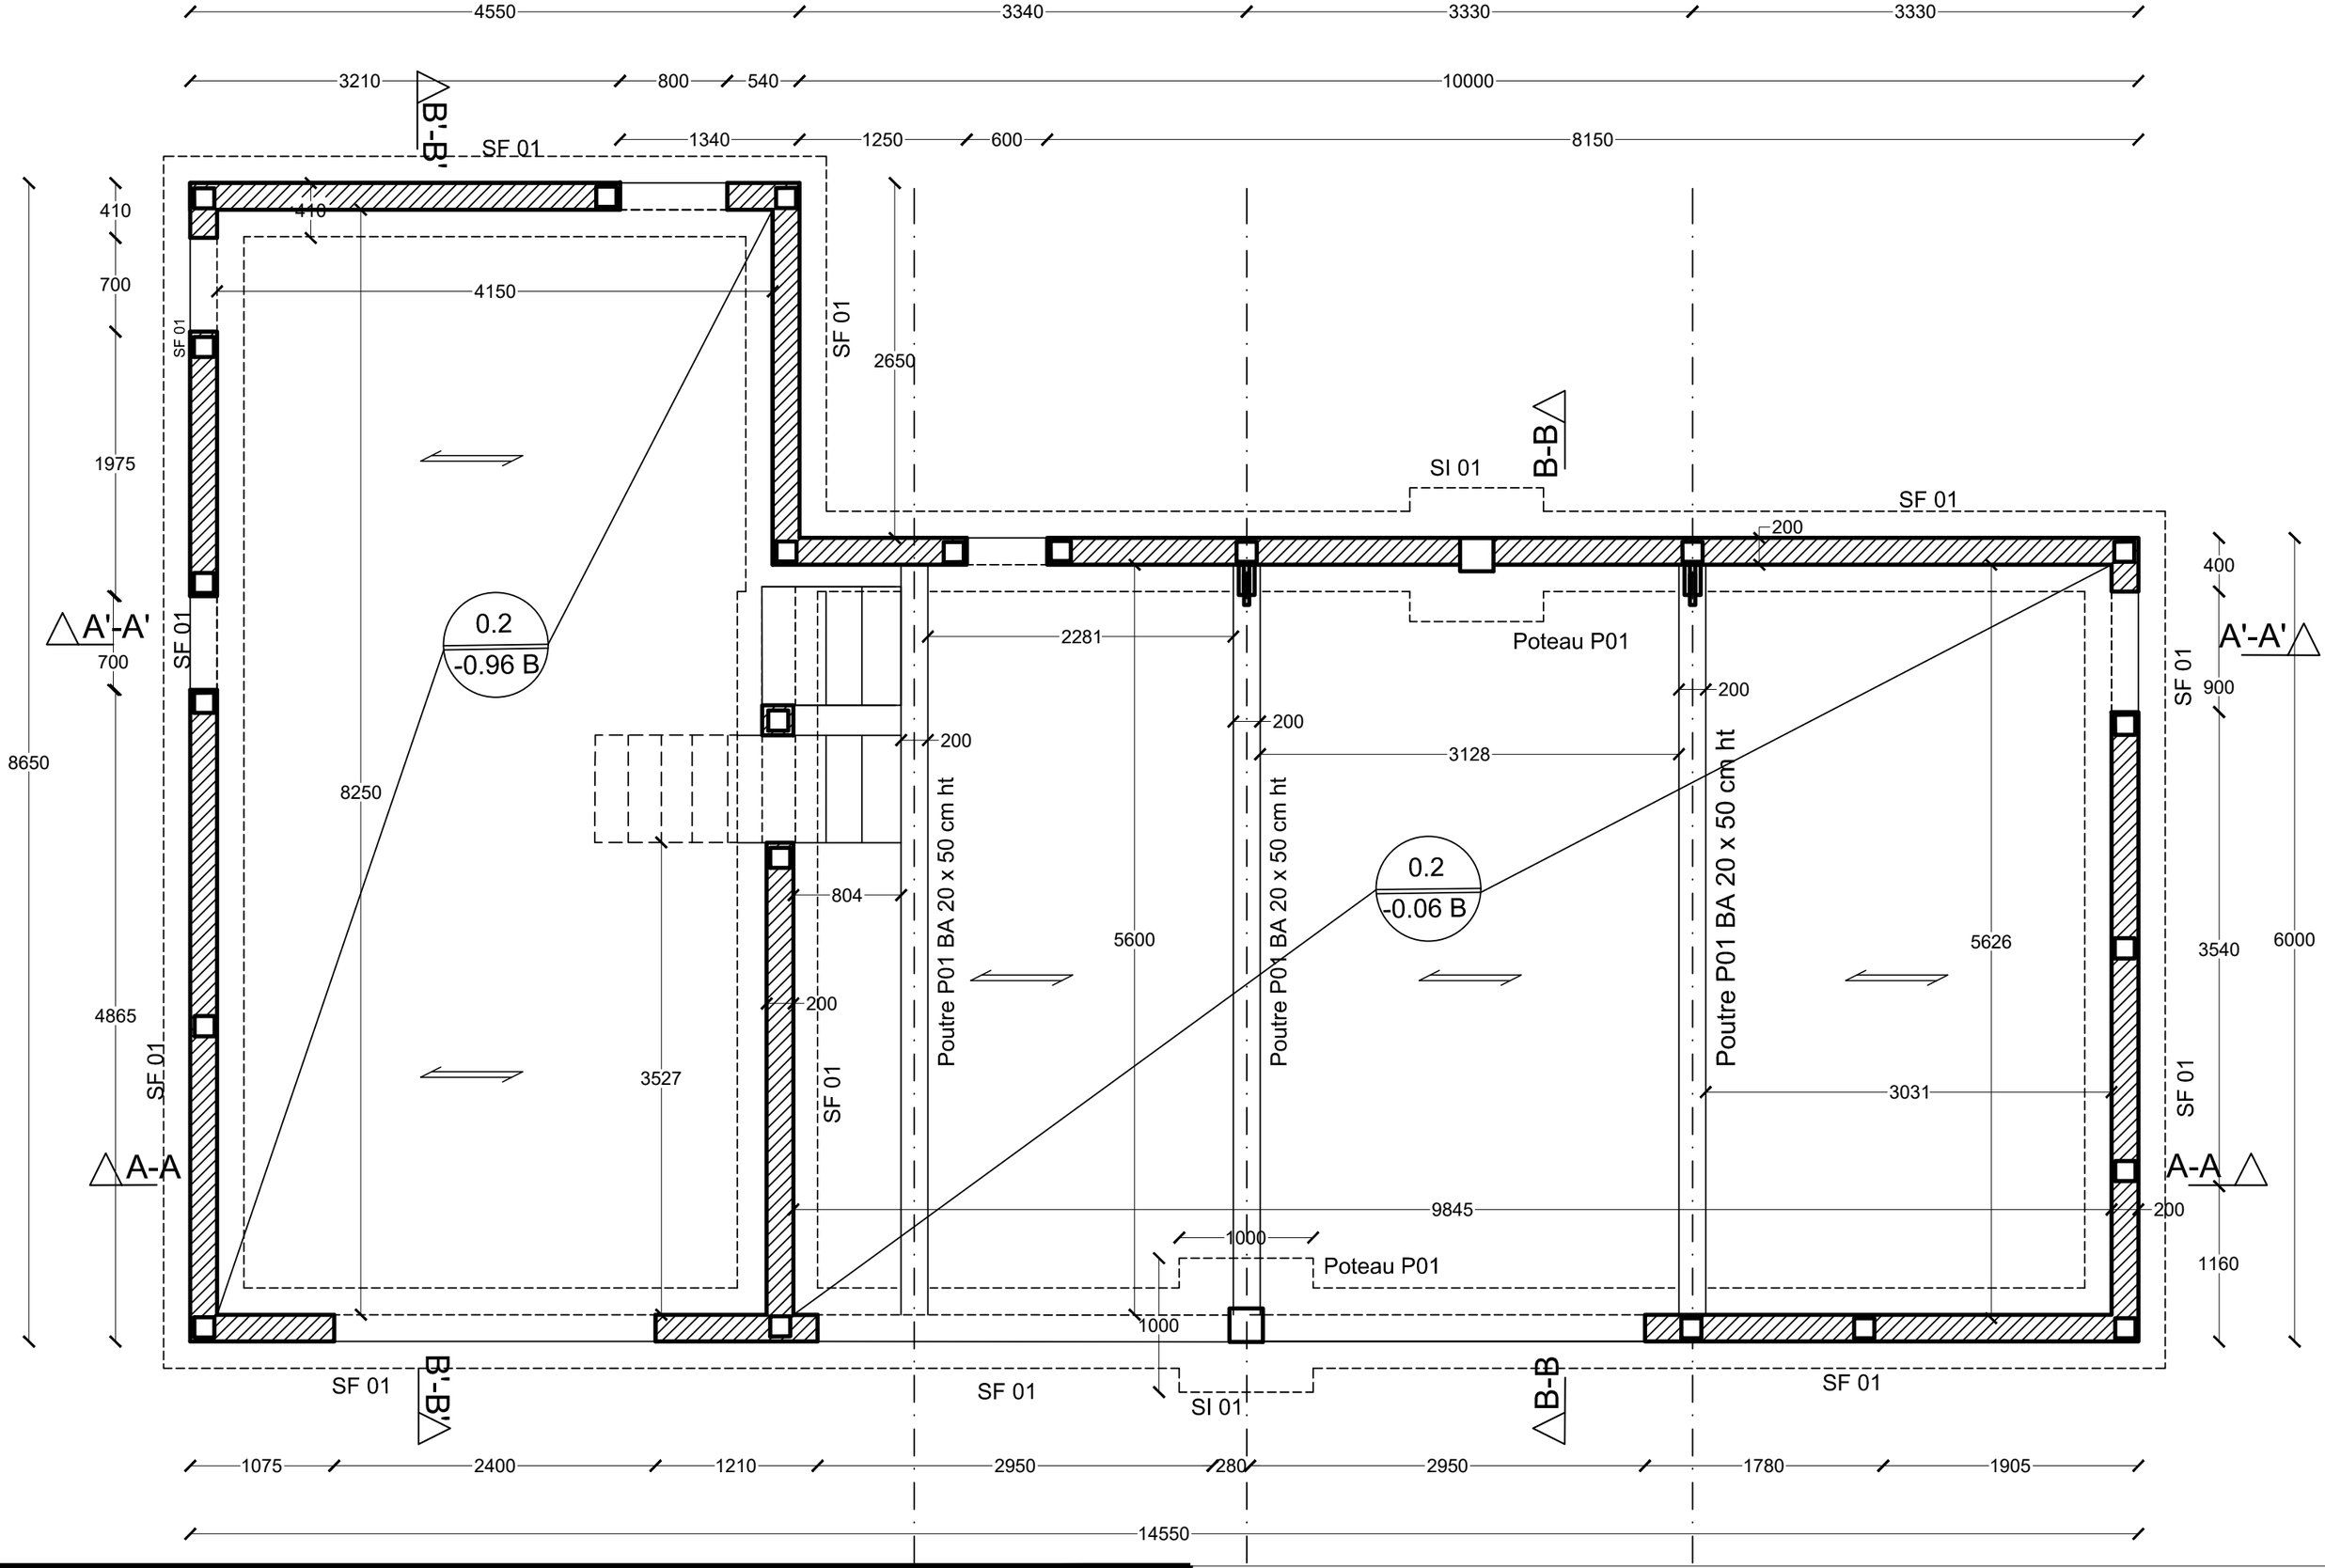


Maîtrise d'Ouvrage : Mme Roux Ghisdlaine 64 Route de Quend 80120 Fort Mahone Plage	**BET STRUCTURE :** J.K.F. STRUCTURE 92 Bd du GLE du Gaulle 59100 Roubaix	Etude d'exécution d'une maison individuelle	**Dossier d'Etude Structurelle :** Plan de fondations	**Plan N° : GO 01** Ech : 1/50

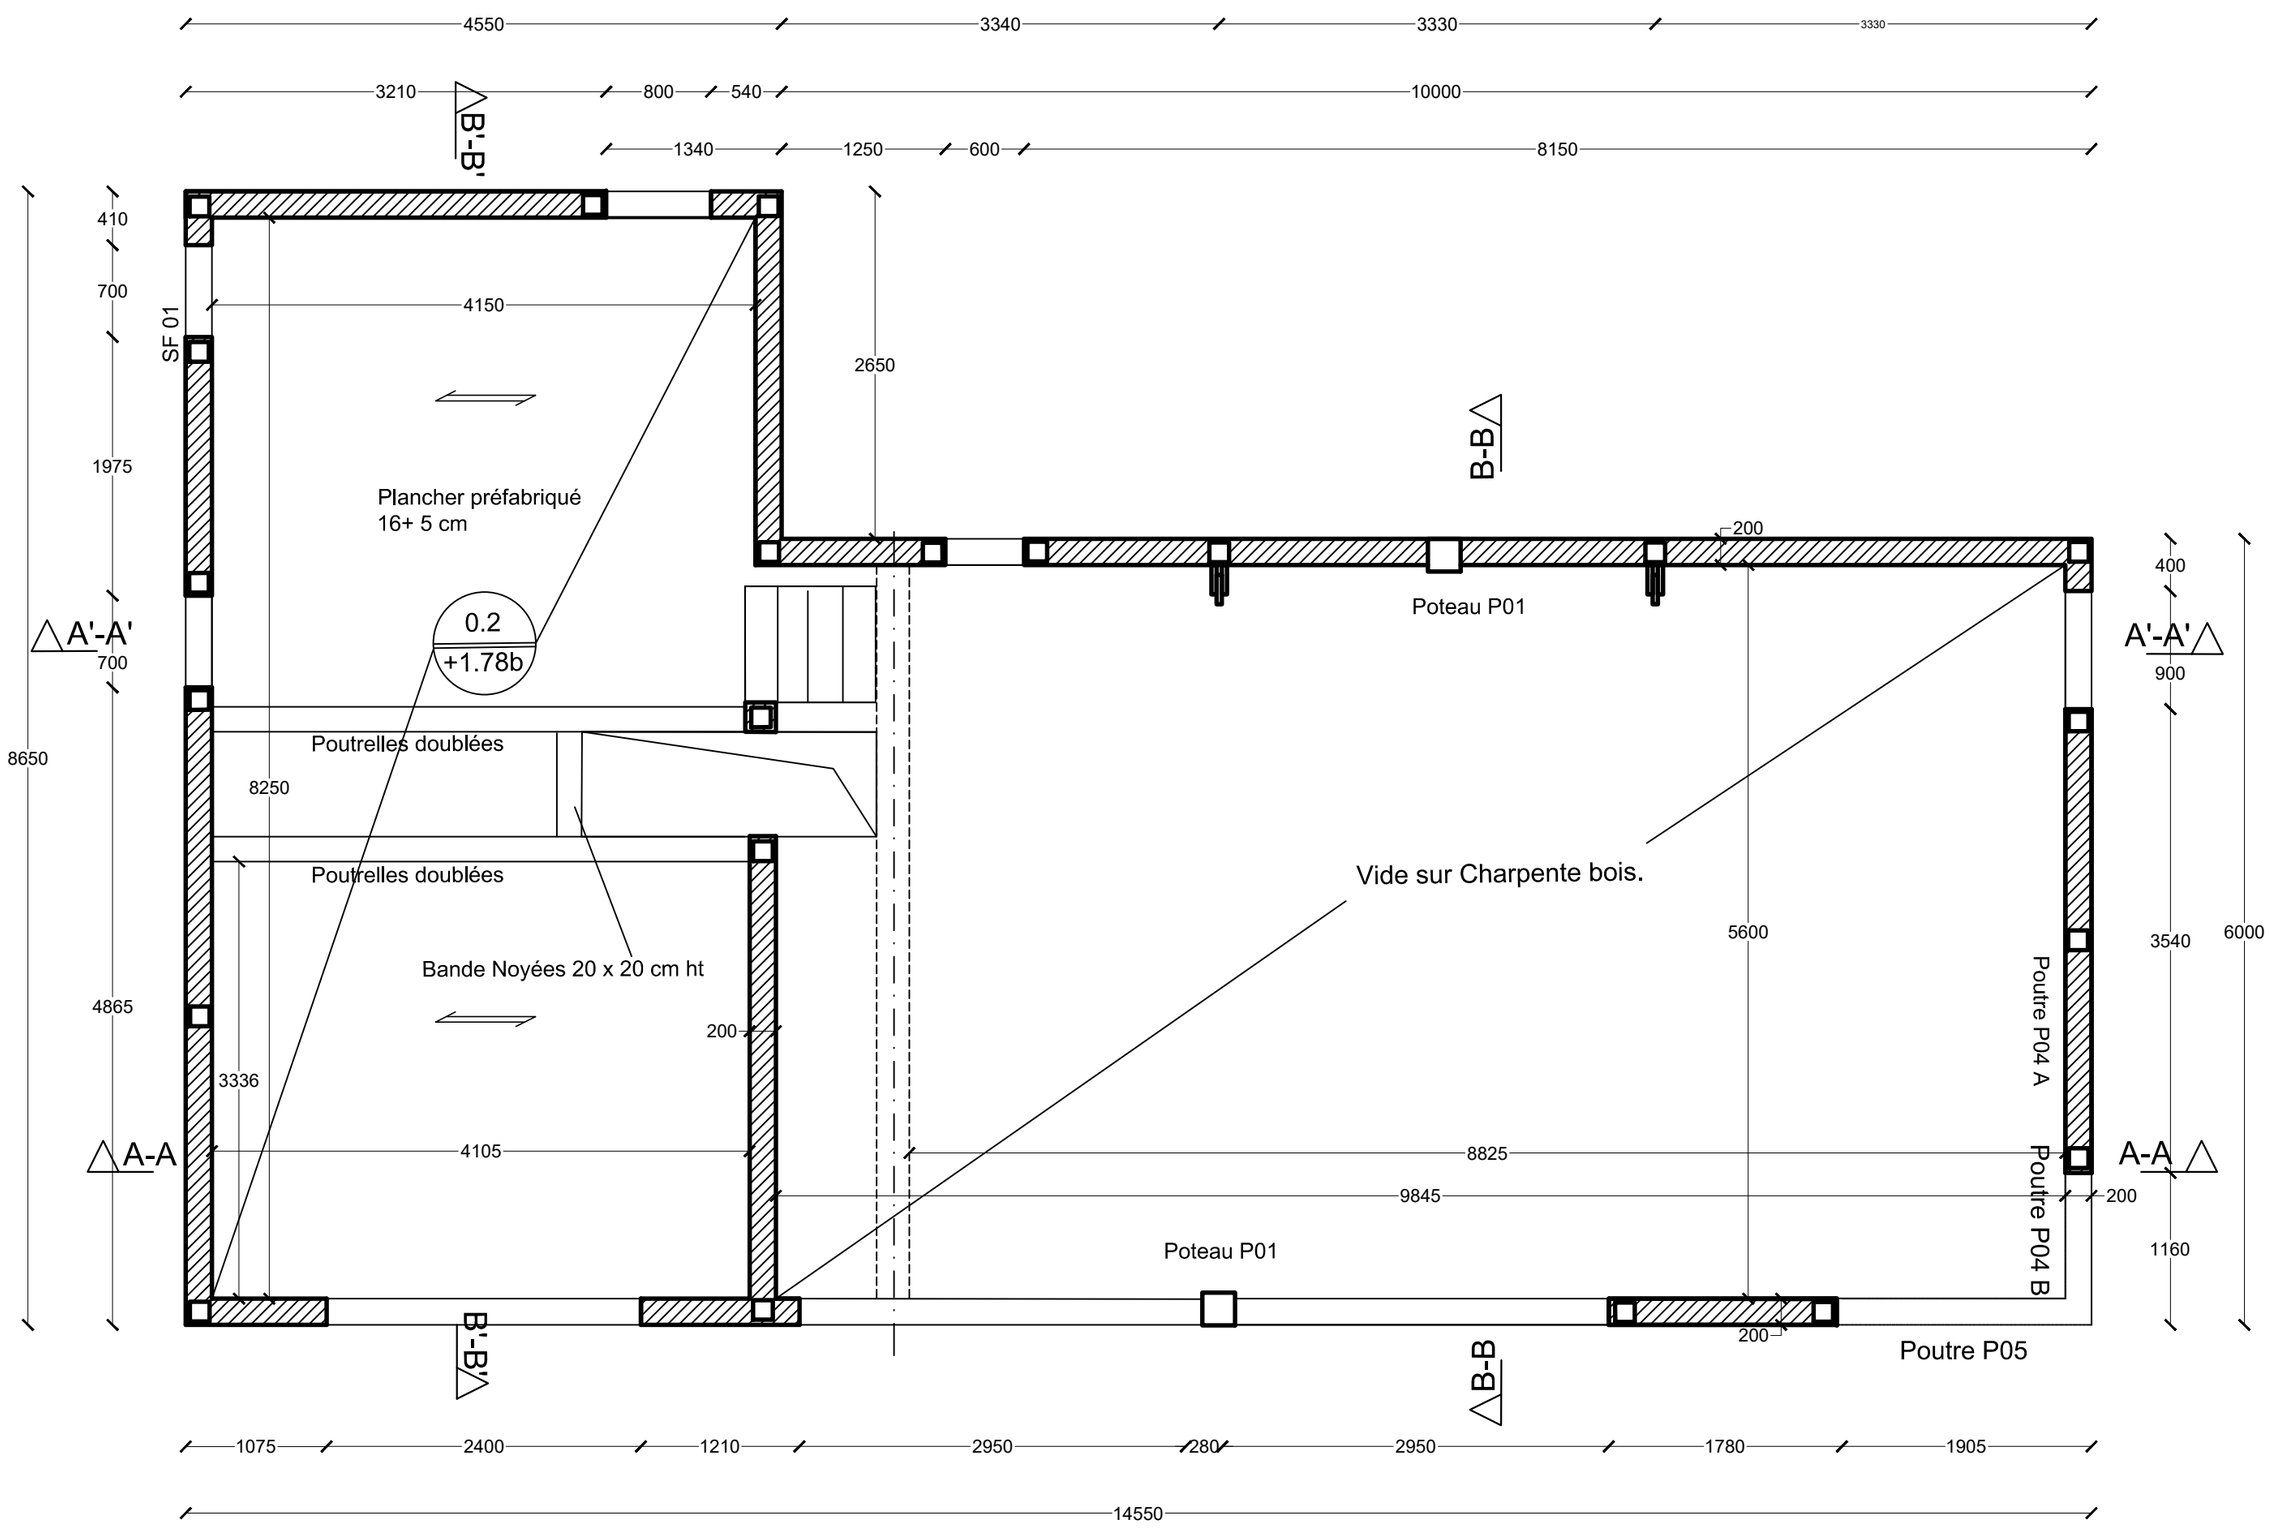


Maîtrise d'Ouvrage :
Mme Roux Ghisdlaine
64 Route de Quend
80120 Fort Mahone Plage

BET STRUCTURE :
J.K.F. STRUCTURE
92 Bd du GLE du Gaulle
59100 Roubaix

Etude d'exécution d'une maison individuelle


Dossier d'Etude Structurelle :
PH RDC

Plan N° : GO 02
Ech : 1/50

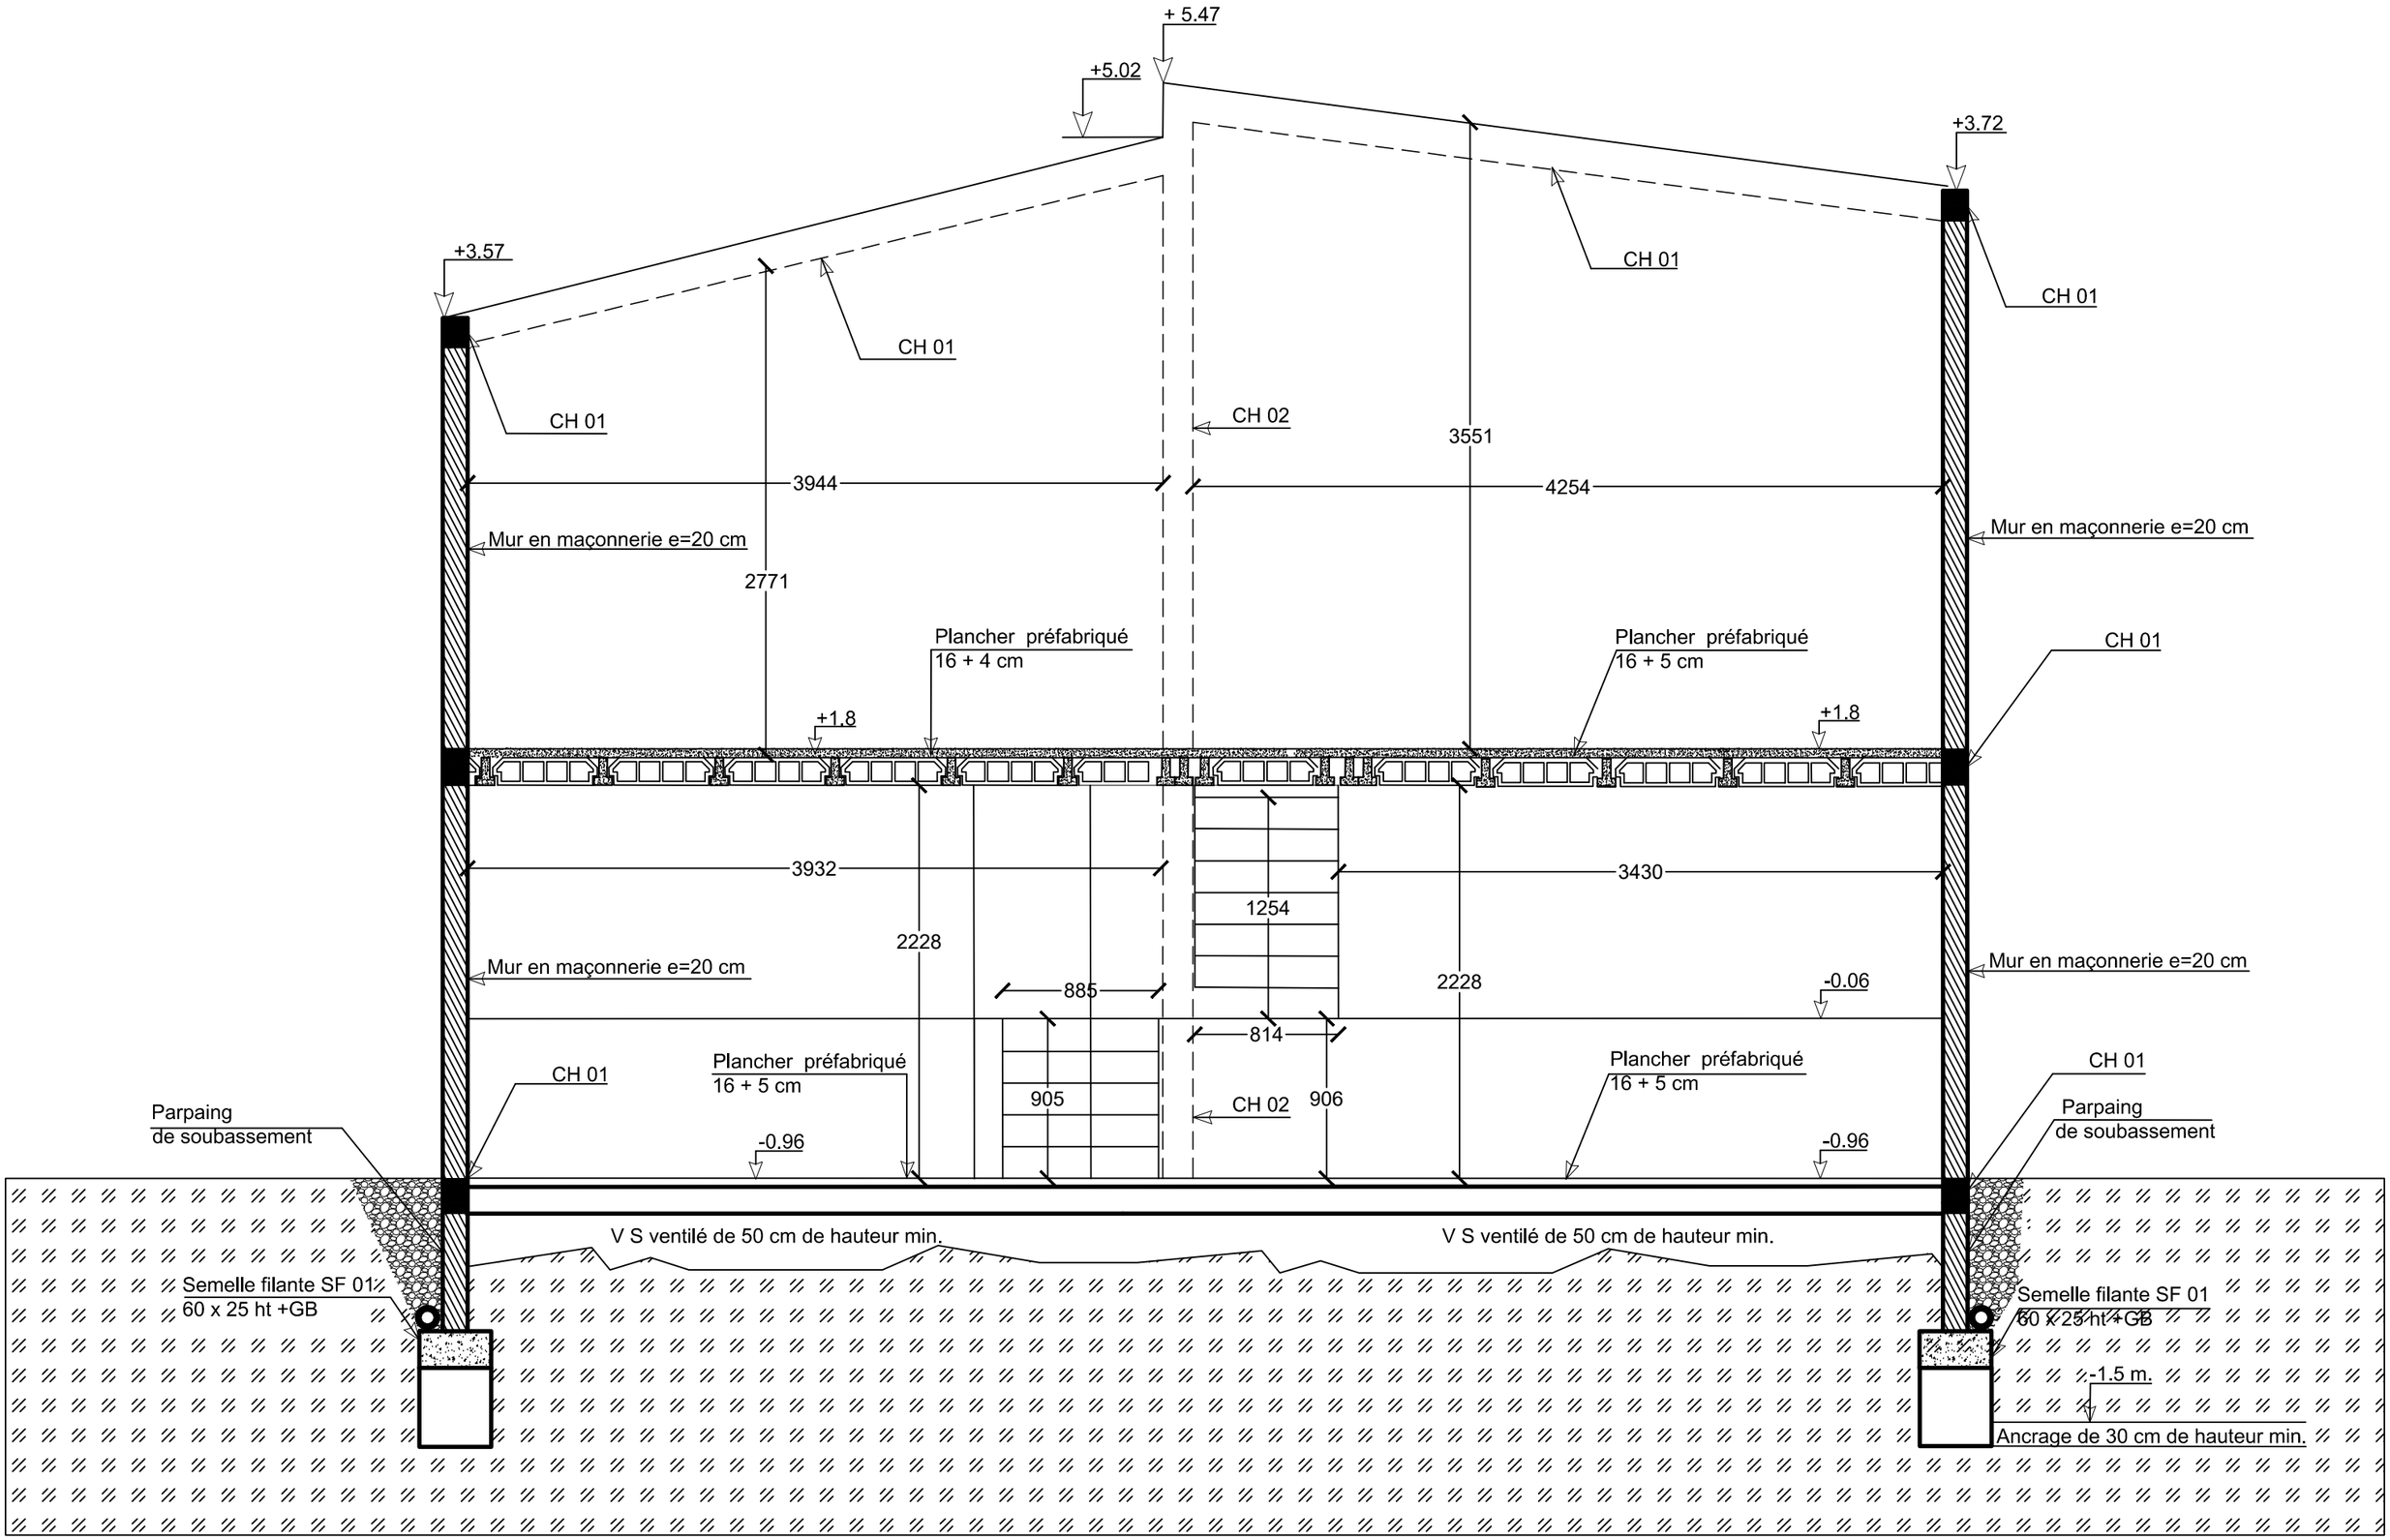


COUPE B'-B'

Maîtrise d'Ouvrage : Mme Roux Ghisdlaine 6 Route de Quend 80120 Fort Mahone Plage.	**BET STRUCTURE :** J.K.F. STRUCTURE 92 Bd du GLE du Gaulle 59100 Roubaix	Etude d'exécution d'une maison individuelle.	**Dossier d'Etude Structurelle :** COUPE B'-B'	**Plan N° : GO 03** Ech : 1/50

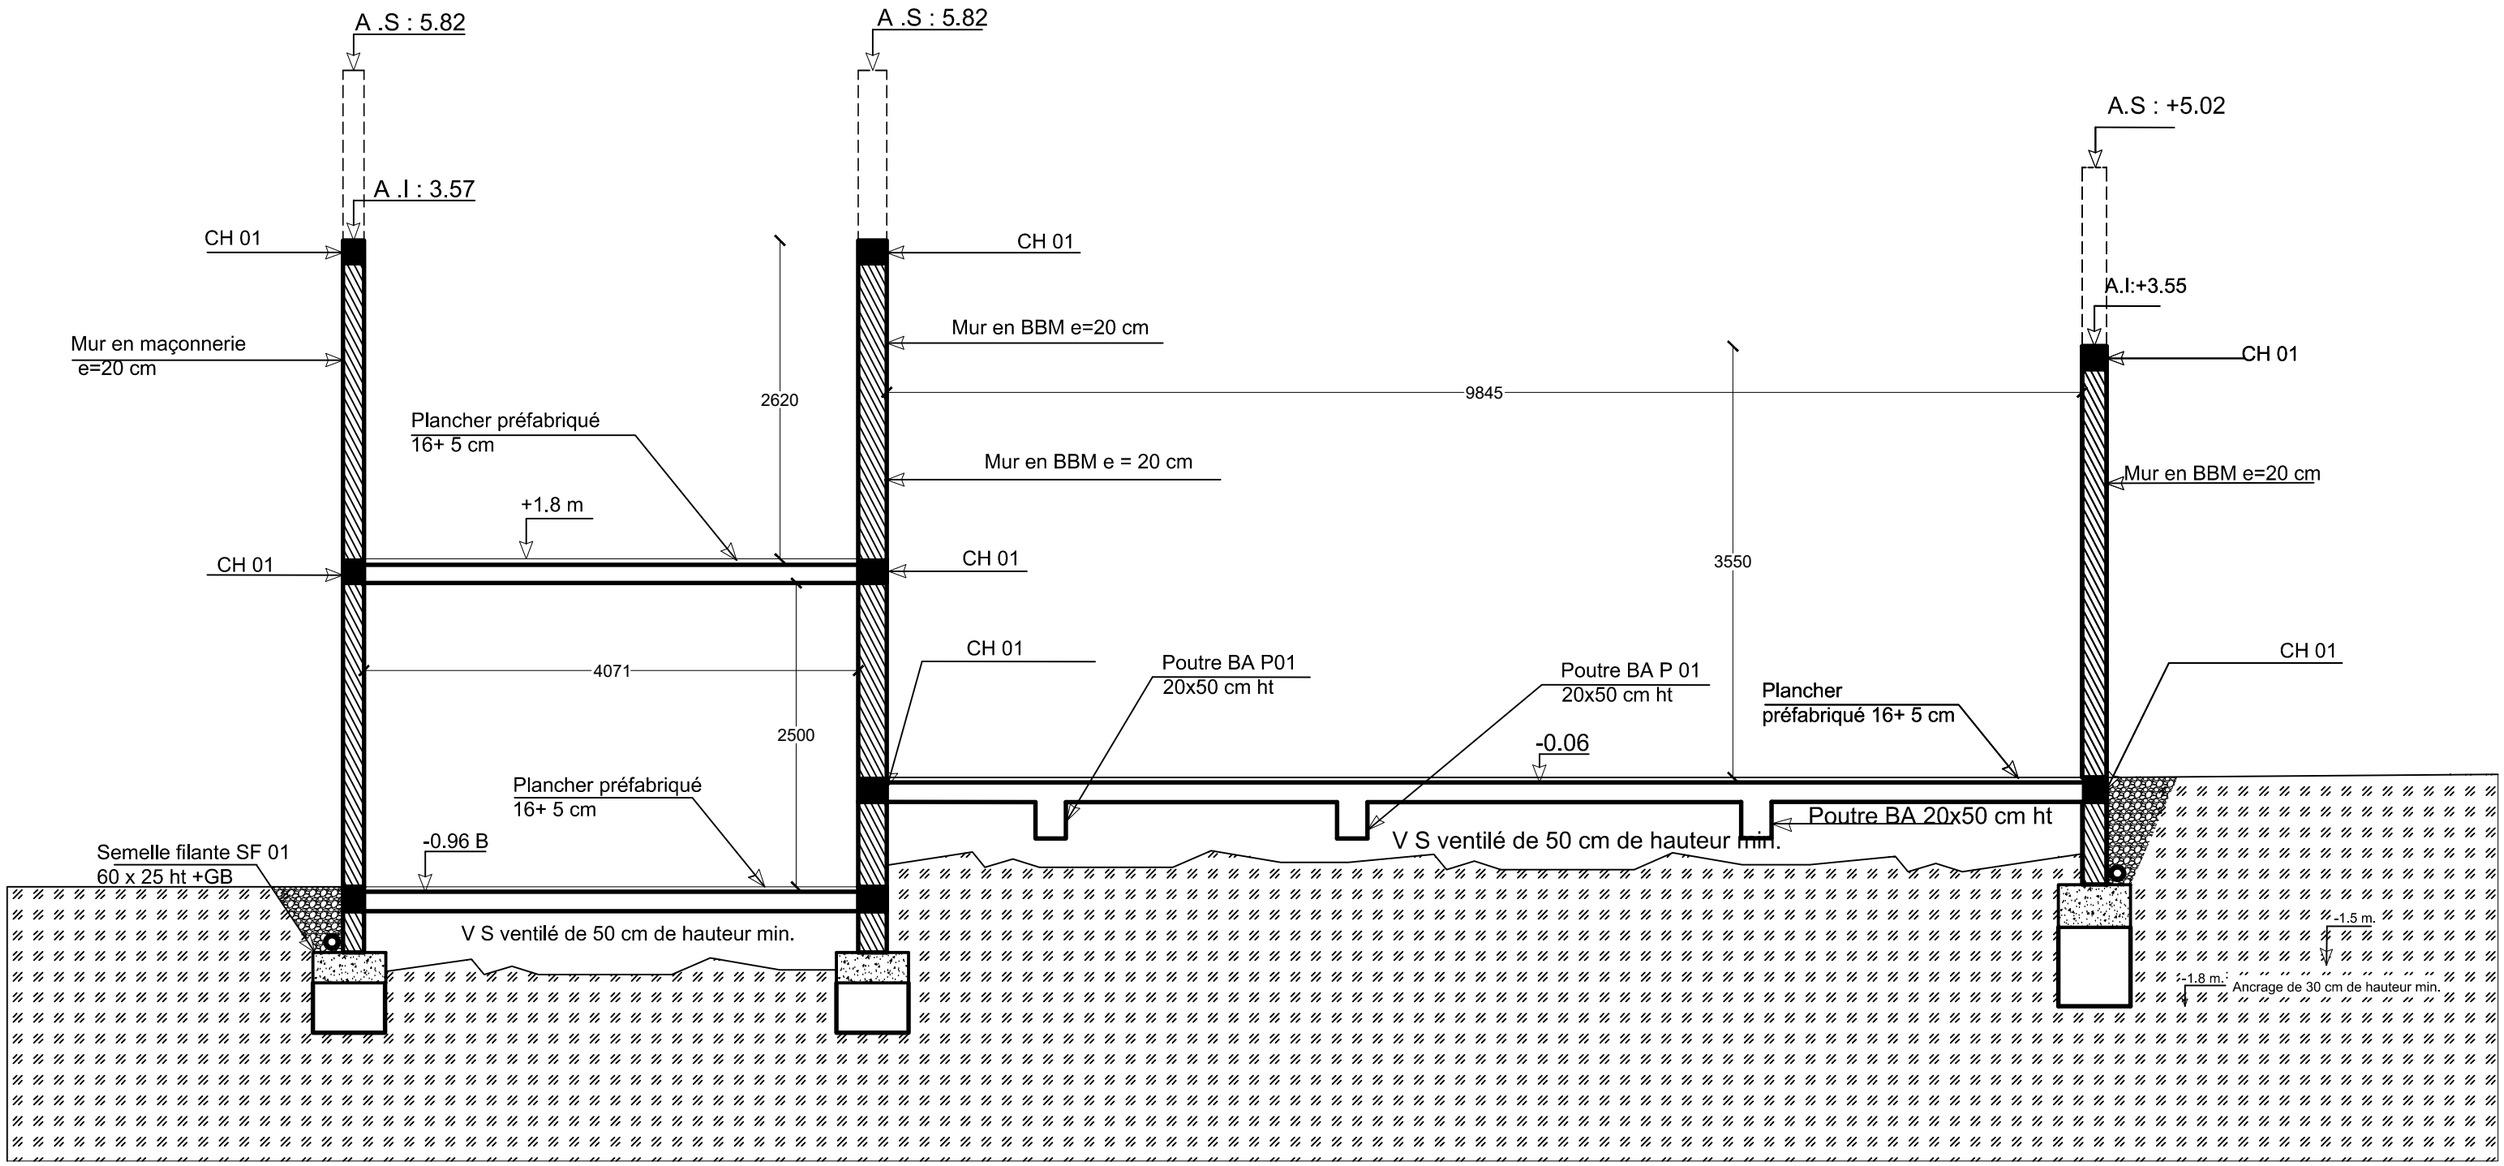

Coupes A-A

Maîtrise d'Ouvrage : Mme Roux Ghisdlaine 6 Route de Quend 80120 Fort Mahone Plage.	**BET STRUCTURE :** J.K.F. STRUCTURE 92 Bd du GLE du Gaulle 59100 Roubaix	Etude d'exécution d'une maison individuelle.	**Dossier d'Etude Structurelle :** COUPE A-A	**Plan N° : GO 04** Ech : 1/50

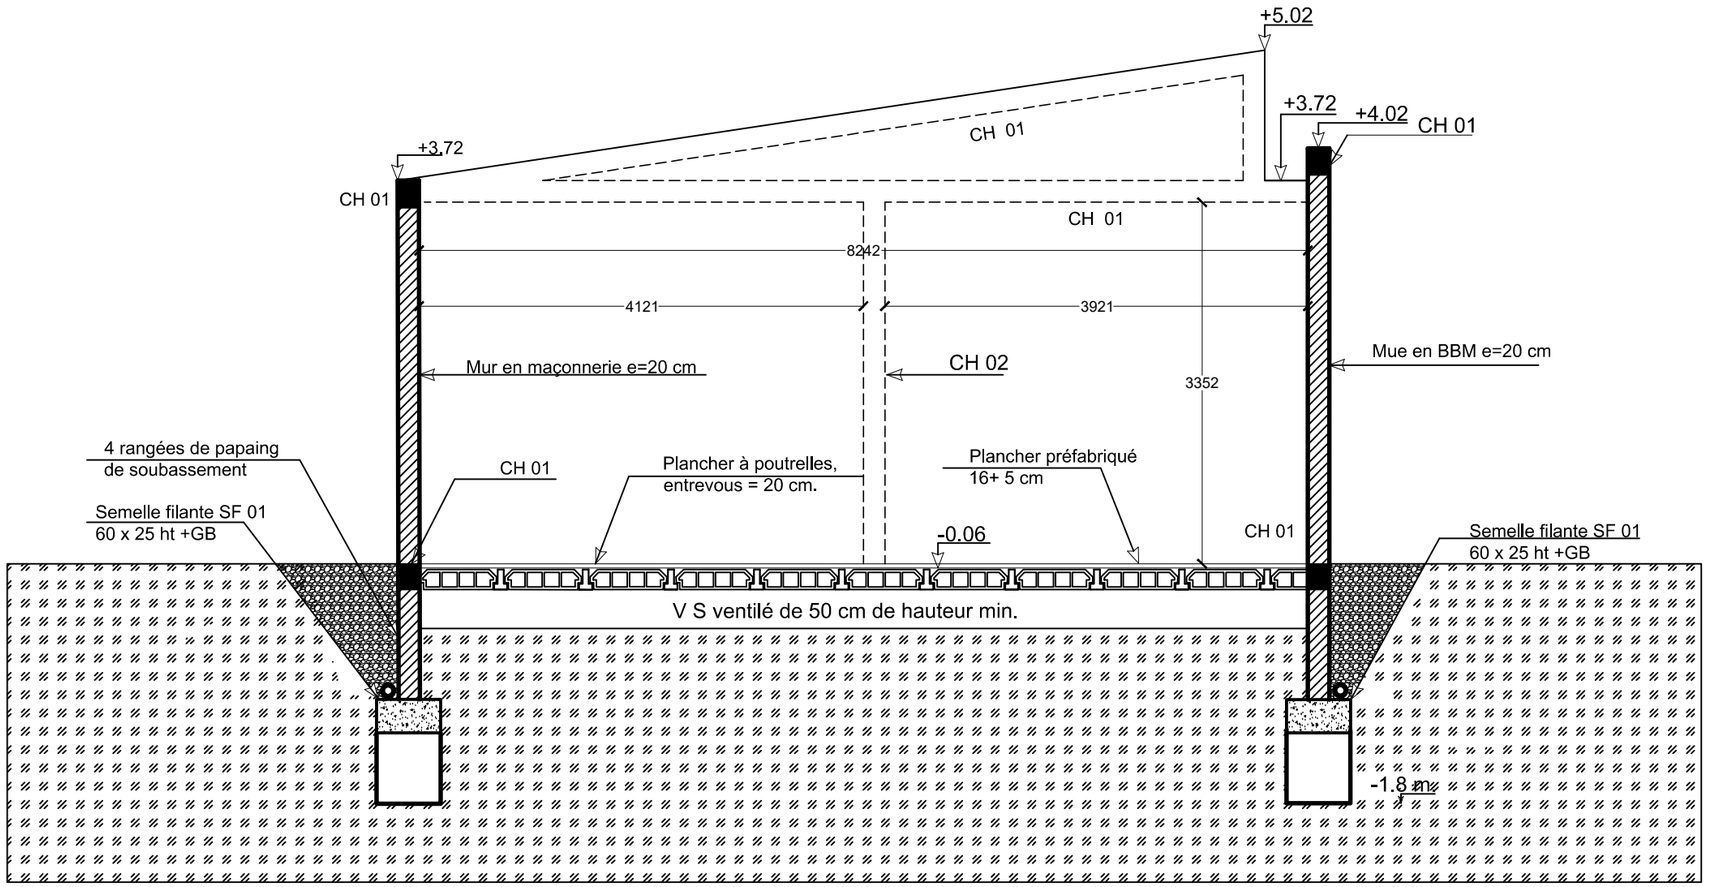


COUPE B-B

Poteau BA P 01 de 25 x 25 cm

Mur BBM (parpaing) e = 20 cm


Hypothèses de calculs :

Zone sismique faible (zone 01) bâtiment de catégorie I, la structure n'est pas soumise à une conception parasismique.

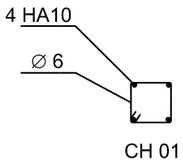

Zone de neige : A1

Zone du vent : zone 2

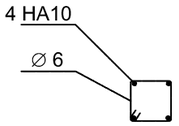

Conformément à l'étude de sols, les fondations sont réalisées par des fondations superficielles, type : semelle filante.

Charges d'exploitation Q = 1.5 Kn / m²

P01 : poteau BA de 25 x 25 cm hauteur 3.72 m.

SF 01 : Semelle Filante 60 x 25 cm ht.

Taux de travail du sol : 12 T/m²

CH 01 : Chaînage horizontal 20x20 cm

CH 01 : Chaînage vertical 20x20 cm

Maîtrise d'Ouvrage :
Mme Roux Ghisdlaine
6 Route de Quend
80120 Fort Mahone Plage.

BET STRUCTURE :
J.K.F. STRUCTURE
92 Bd du GLE du Gaulle
59100 Roubaix


Etude d'exécution d'une maison individuelle.

Dossier d'Etude Structurelle :

COUPE B-B

Plan N° : GO 05

Ech : 1/100

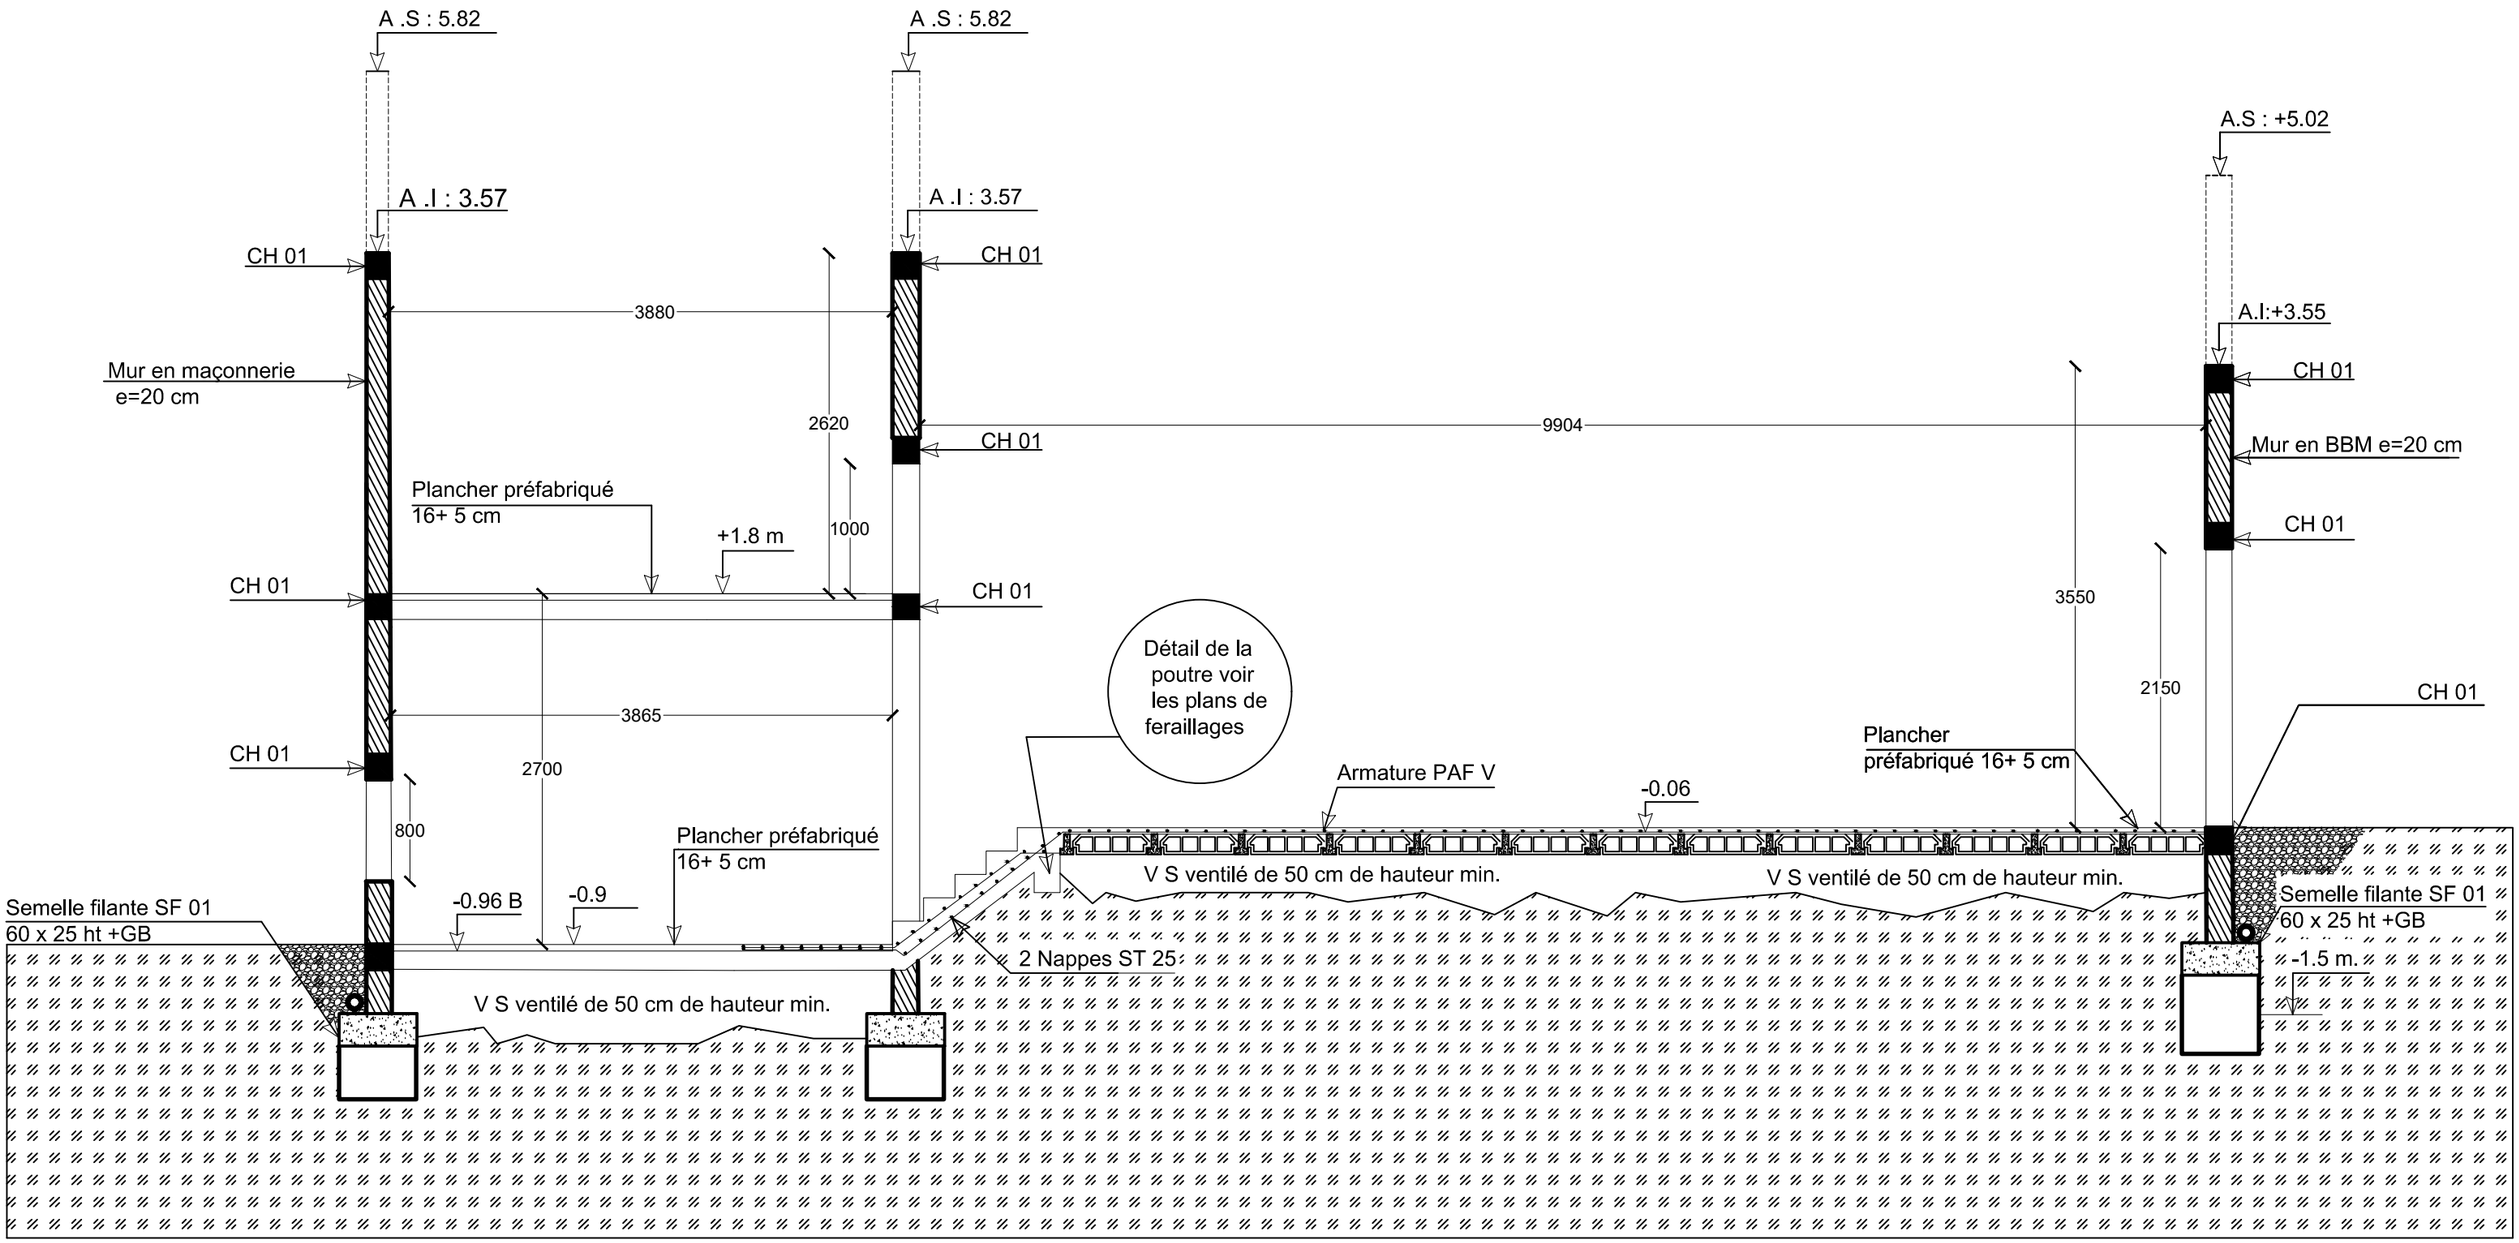

COUPE A'-A'

Maîtrise d'Ouvrage : Mme Roux Ghisdlaine 6 Route de Quend 80120 Fort Mahone Plage.	**BET STRUCTURE :** J.K.F. STRUCTURE 92 Bd du GLE du Gaulle 59100 Roubaix	Etude d'exécution d'une maison individuelle.	**Dossier d'Etude Structurelle :** COUPE A'-A'	**Plan N° : GO 06** Ech : 1/50