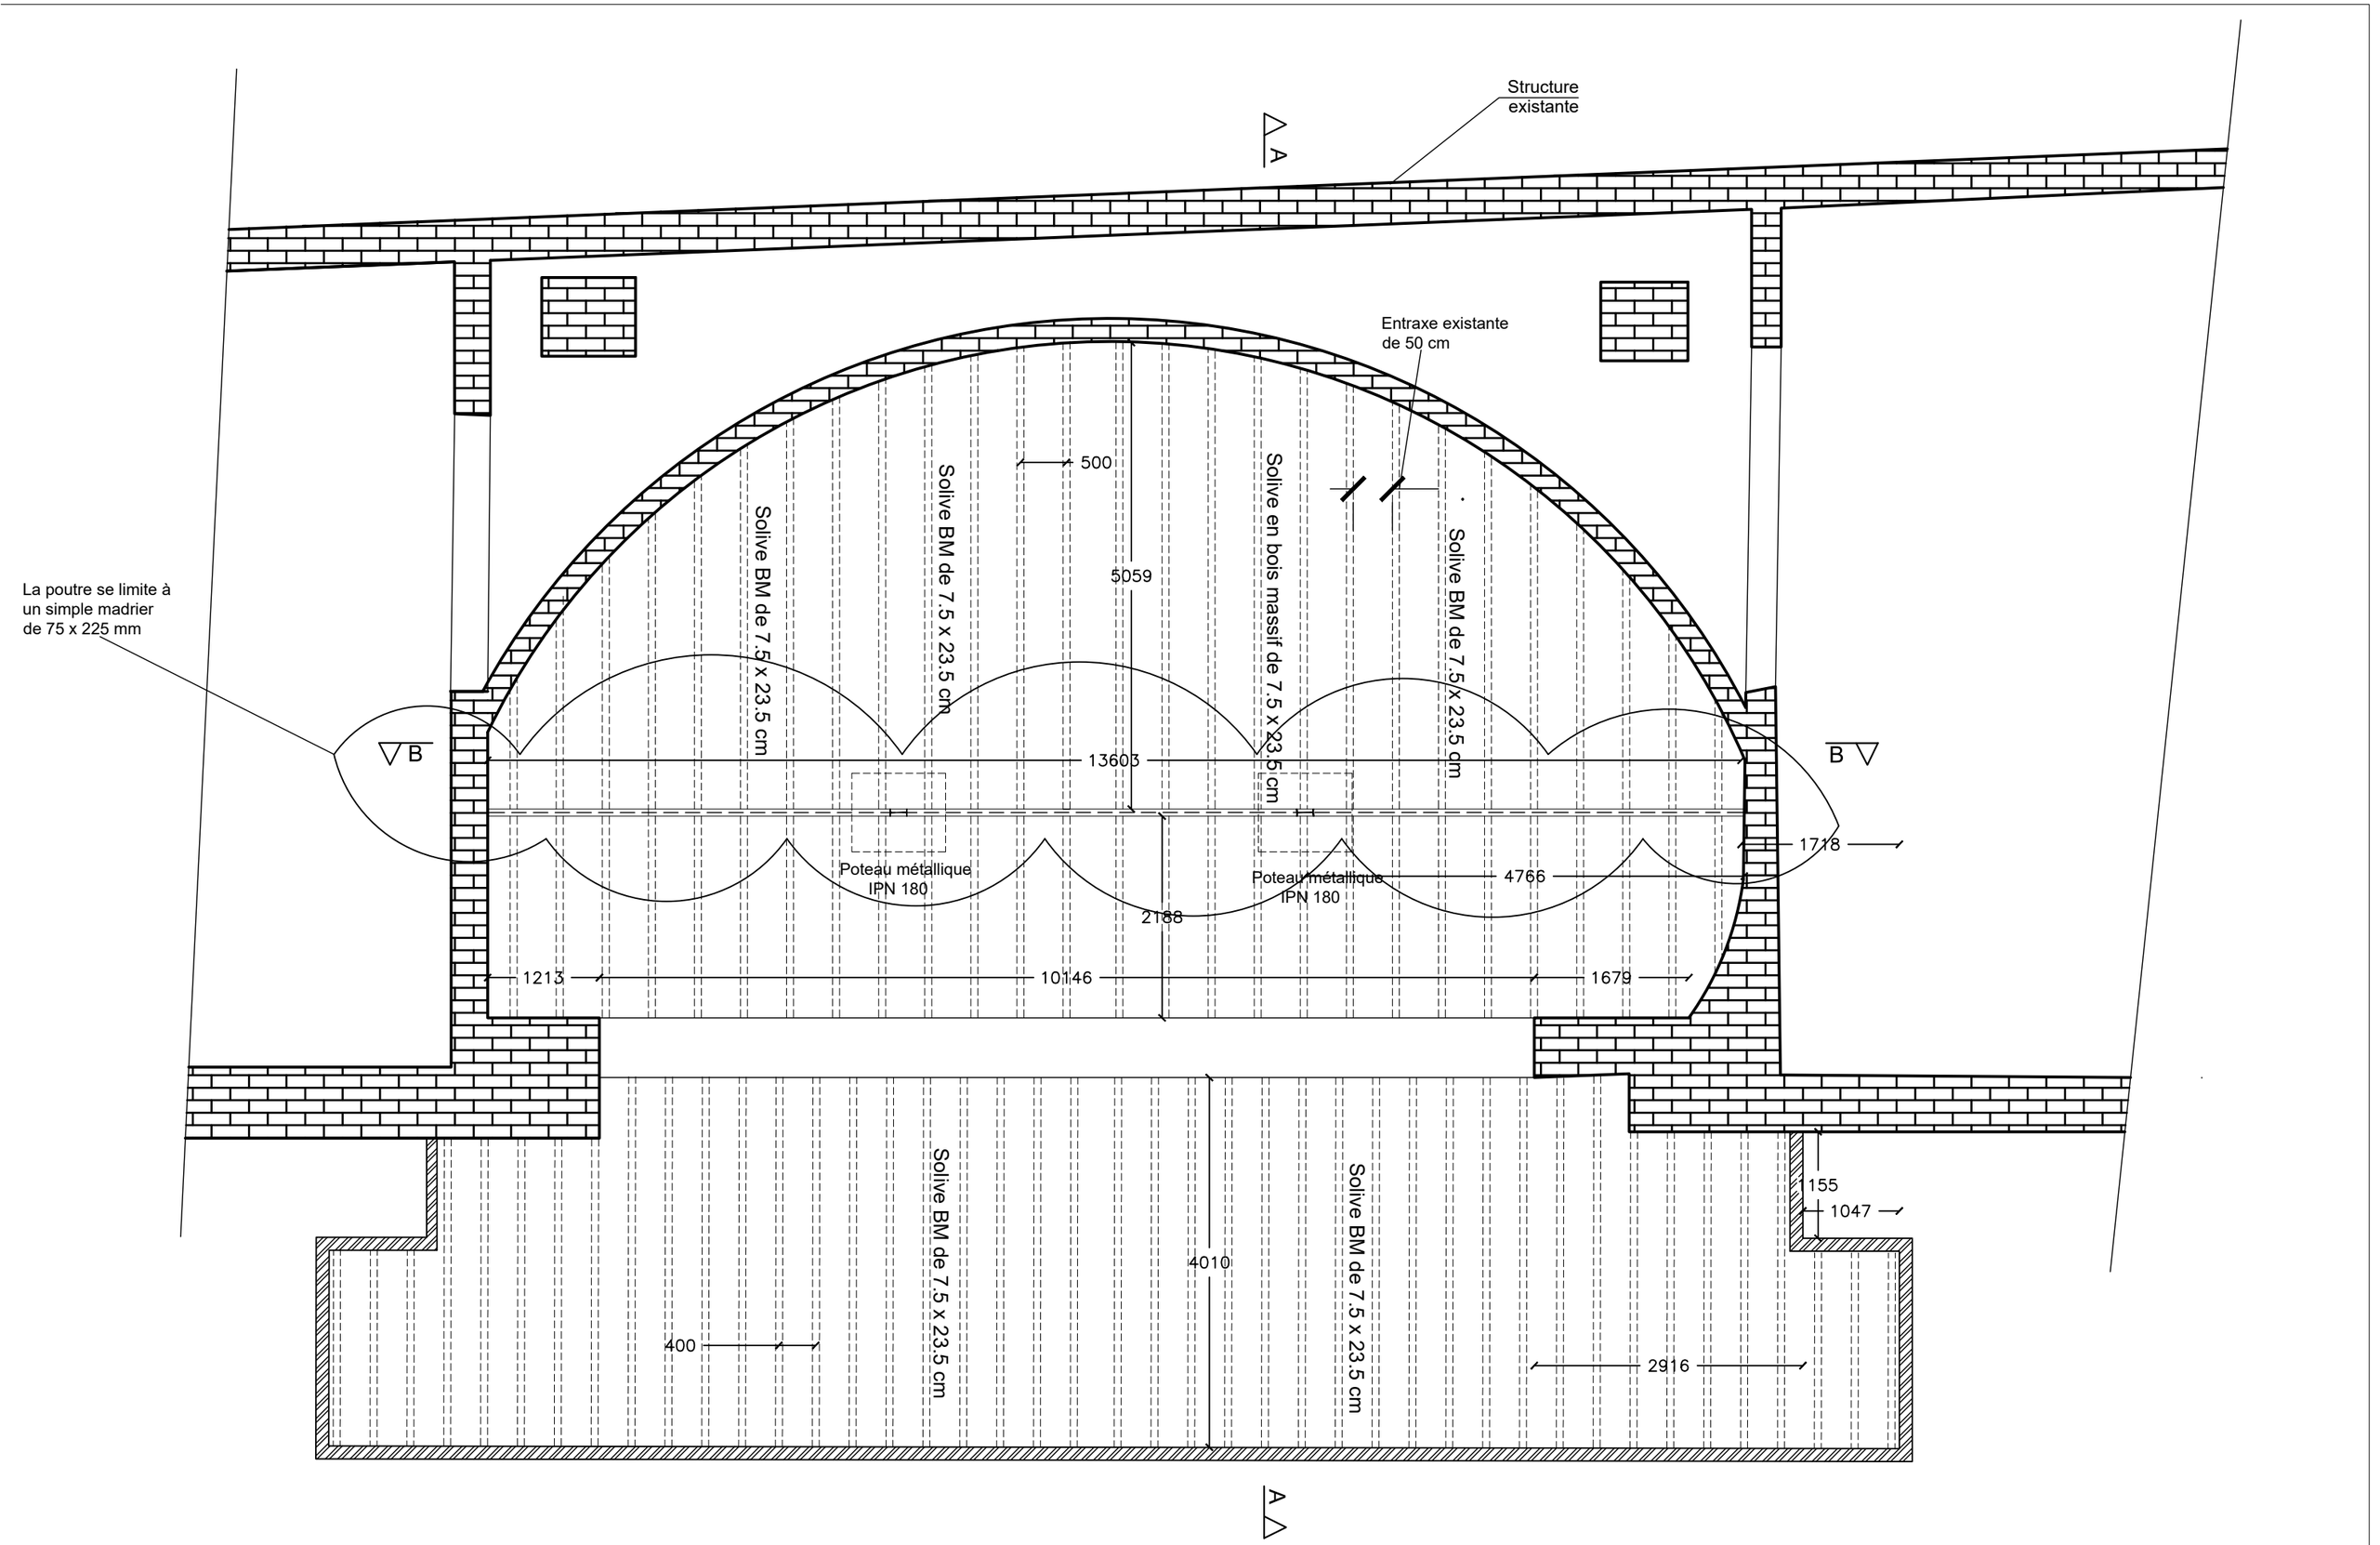


Plancher haut sous sol existant.


Maîtrise d'Ouvrage :
Mairie de Roubaix
17 Grand Place
59 100 Roubaix

BET STRUCTURE :
J.K.F. STRUCTURE
92 Bd du GLE du Gaulle
59100 Roubaix

Etude de la charge d'exploitation admissible pour la scene de la salle watremez

Dossier d'Etude Structurelle :
Plancher haut sous-sol existant

Plan N° : GO 01
Ech : 1/75

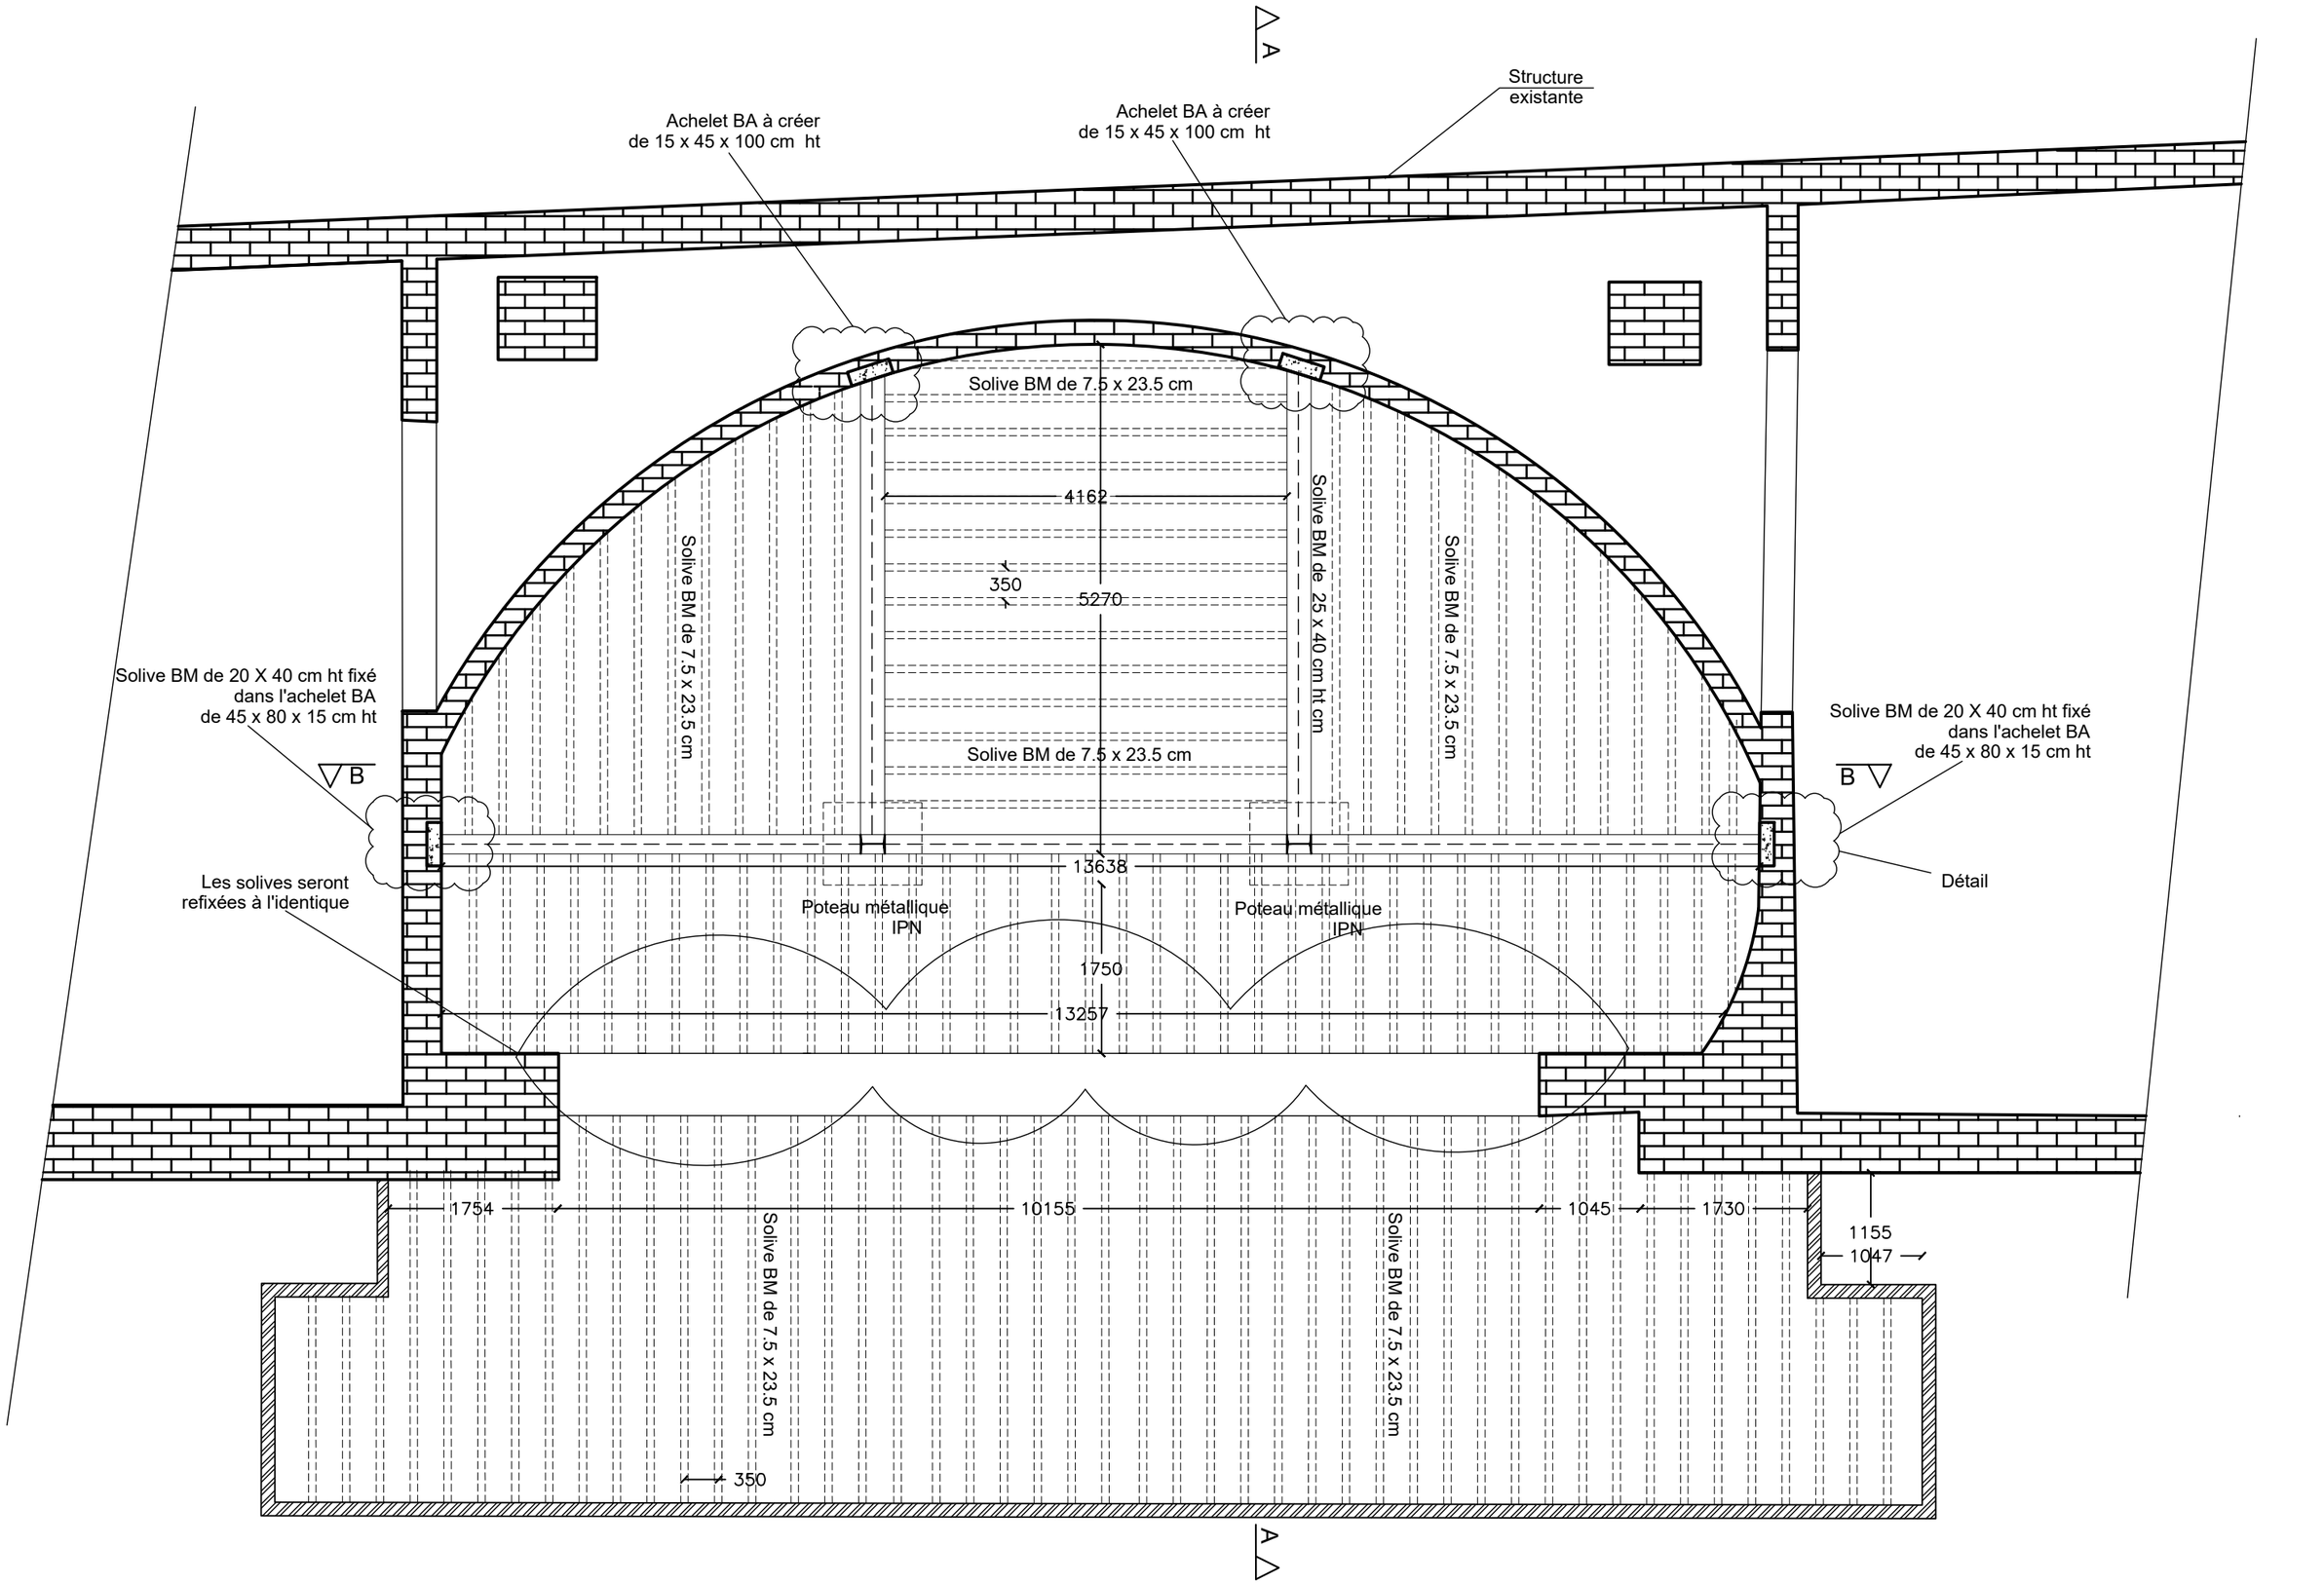

Plancher haut sous sol projet.


Maîtrise d'Ouvrage :
Mairie de Roubaix
17 Grand Place
59 100 Roubaix

BET STRUCTURE :
J.K.F. STRUCTURE
92 Bd du GLE du Gaulle
59100 Roubaix

Etude de la charge d'exploitation admissible pour la scene de la salle watremez

Dossier d'Etude Structurelle :
Plancher haut sous-sol projet

Plan N° : GO 02
Ech : 1/75

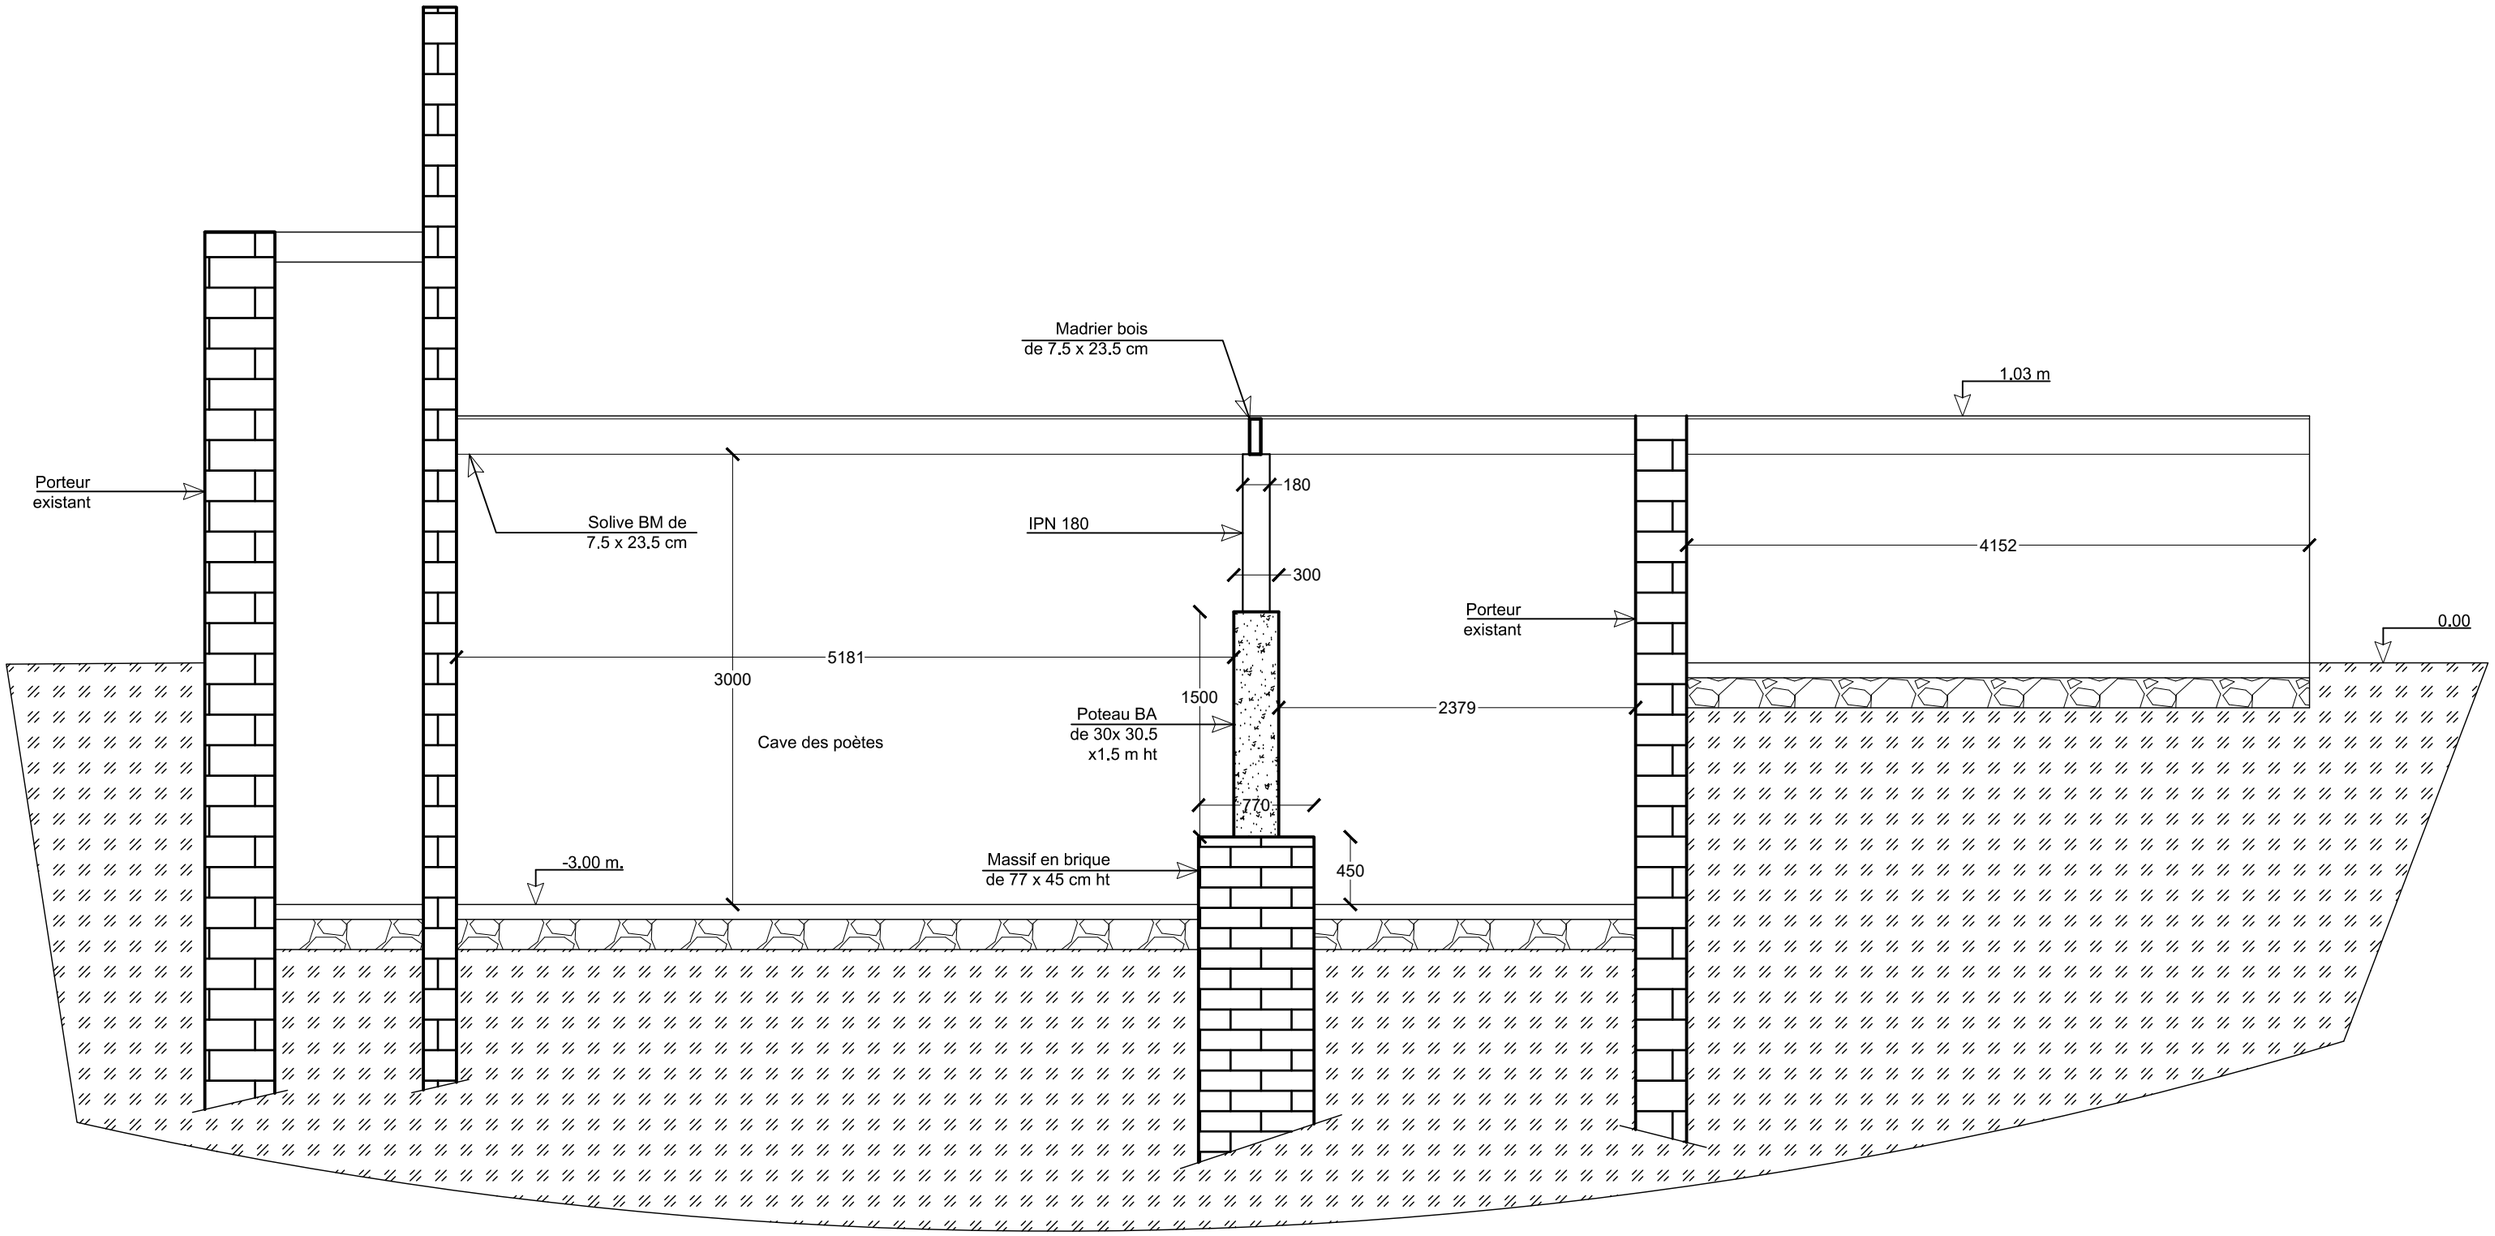

Coupe A-A existant


Maîtrise d'Ouvrage :
Mairie de Roubaix
17 Grand Place
59 100 Roubaix

BET STRUCTURE :
J.K.F. STRUCTURE
92 Bd du GLE du Gaulle
59100 Roubaix

Etude de la charge d'exploitation admissible pour la scene de la salle watremez

Dossier d'Etude Structurelle :
Coupe A-A existant

Plan N° : GO 03
Ech : 1/75

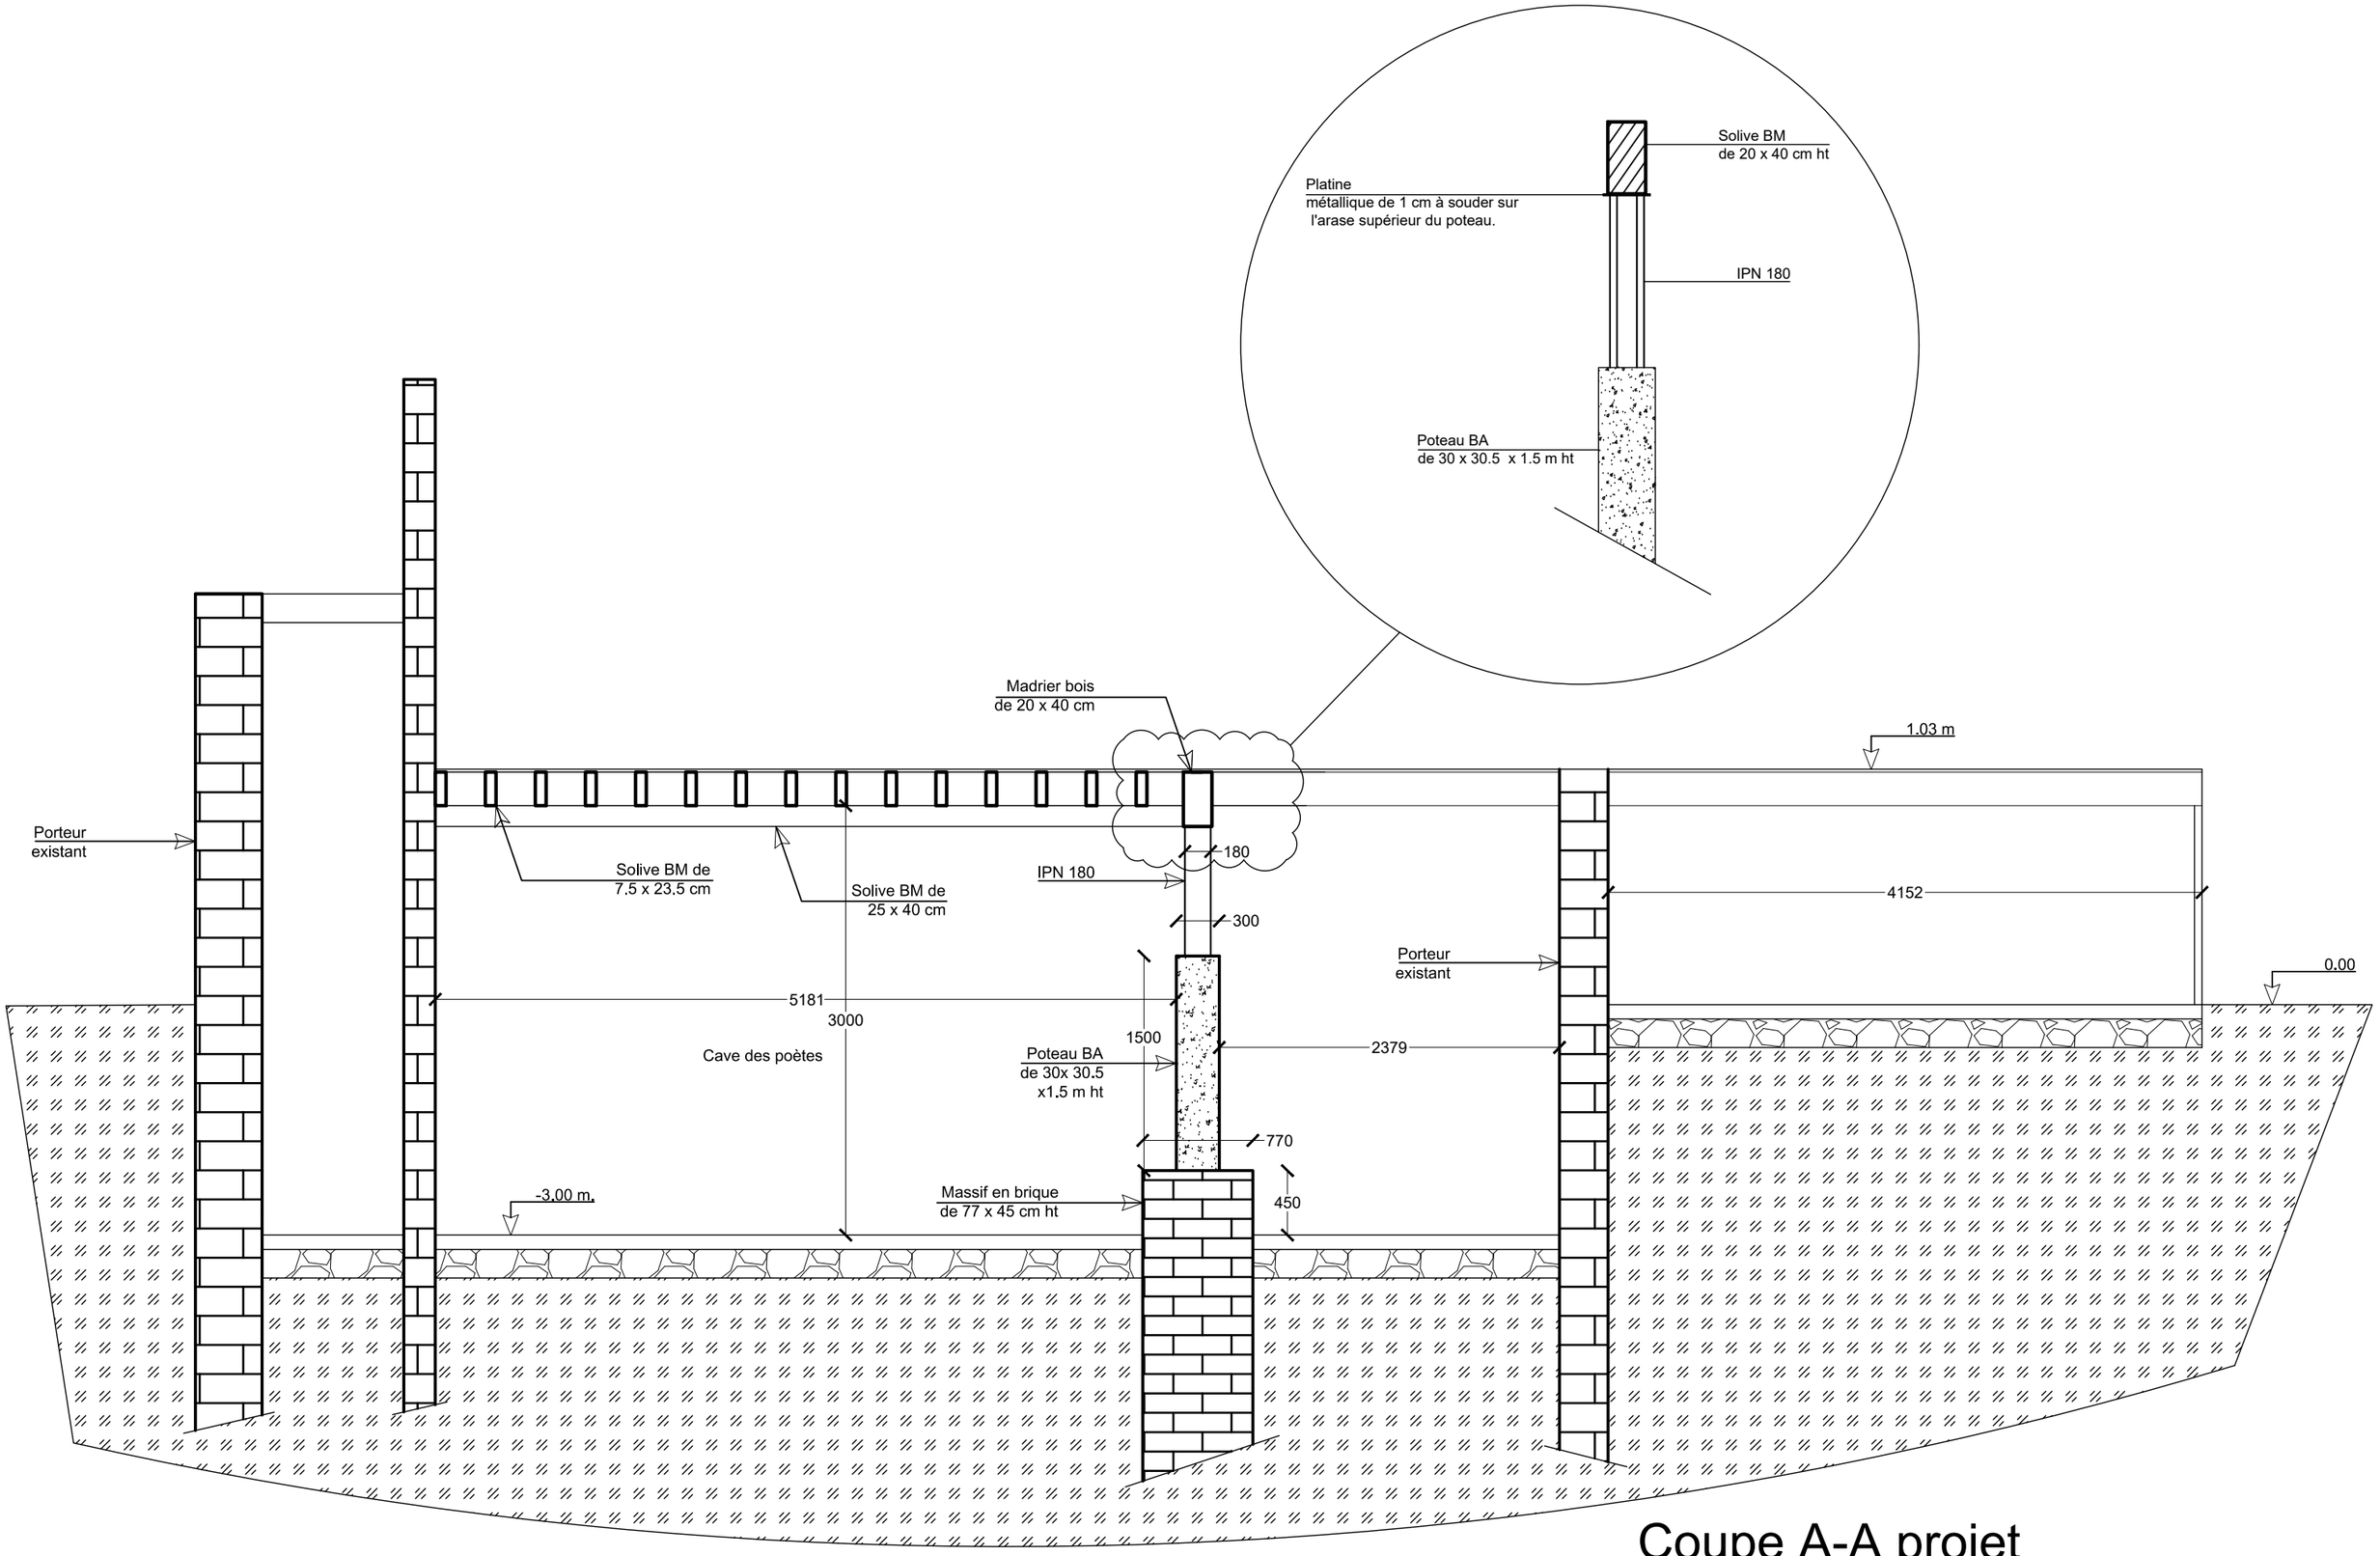

Coupe A-A projet


Maîtrise d'Ouvrage :
Mairie de Roubaix
17 Grand Place
59 100 Roubaix

BET STRUCTURE :
J.K.F. STRUCTURE
92 Bd du GLE du Gaulle
59100 Roubaix

Etude de la charge d'exploitation admissible pour la scene de la salle watremez

Dossier d'Etude Structurelle :
Coupe A-A projet

Plan N° : GO 04
Ech : 1/75

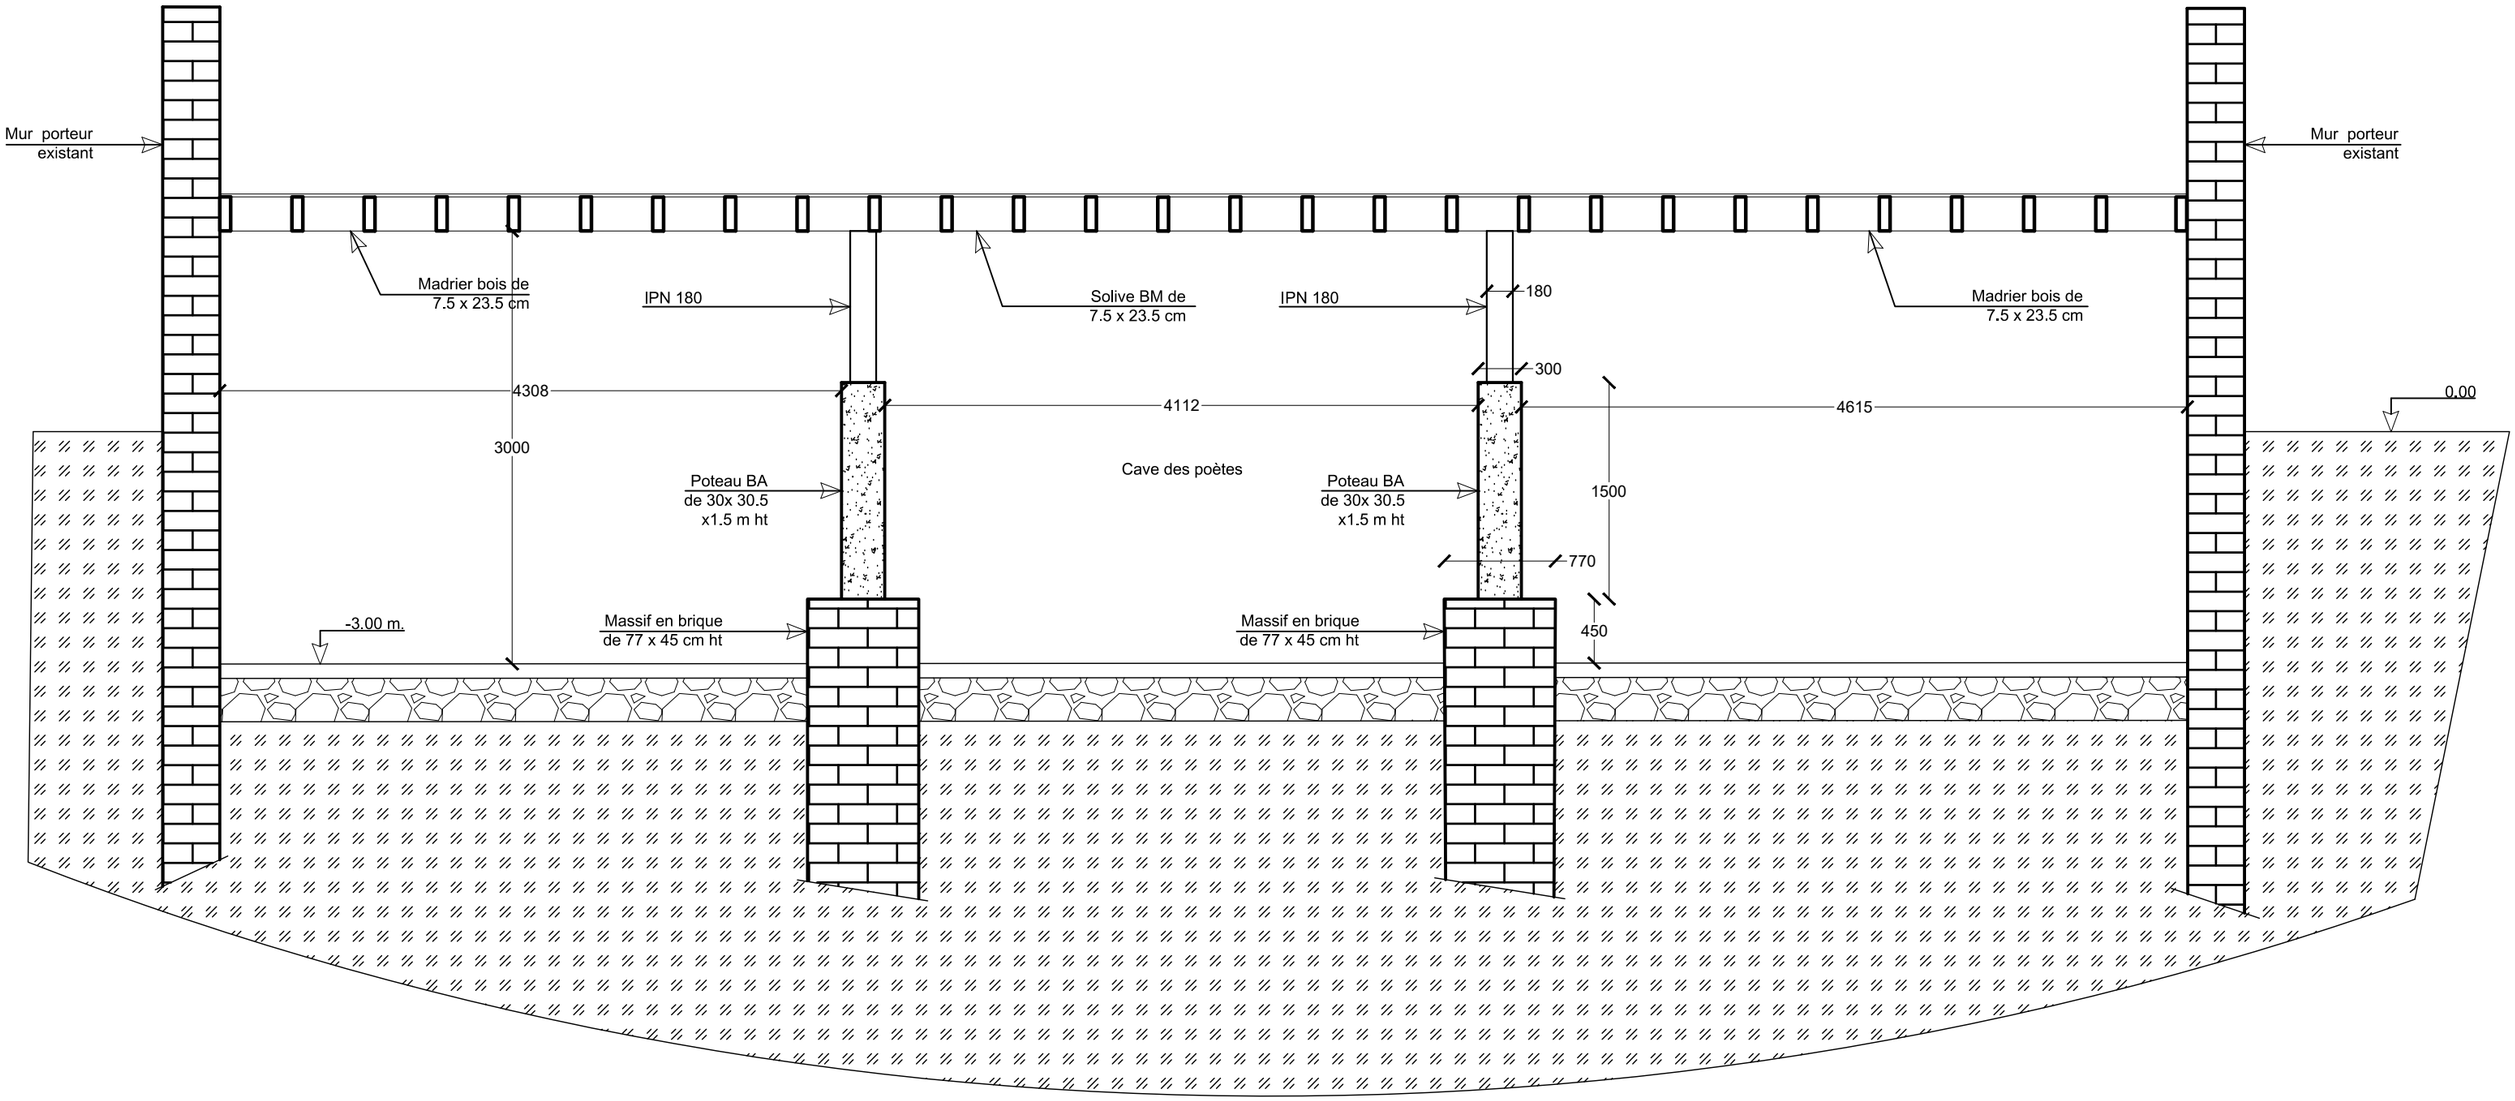

Coupe B-B existant


Maîtrise d'Ouvrage :
Mairie de Roubaix
17 Grand Place
59 100 Roubaix

BET STRUCTURE :
J.K.F. STRUCTURE
92 Bd du GLE du Gaulle
59100 Roubaix

Etude de la charge d'exploitation admissible pour la scene de la salle watremez

Dossier d'Etude Structurelle :
Coupe B-B existant

Plan N° : GO 05
Ech : 1/75

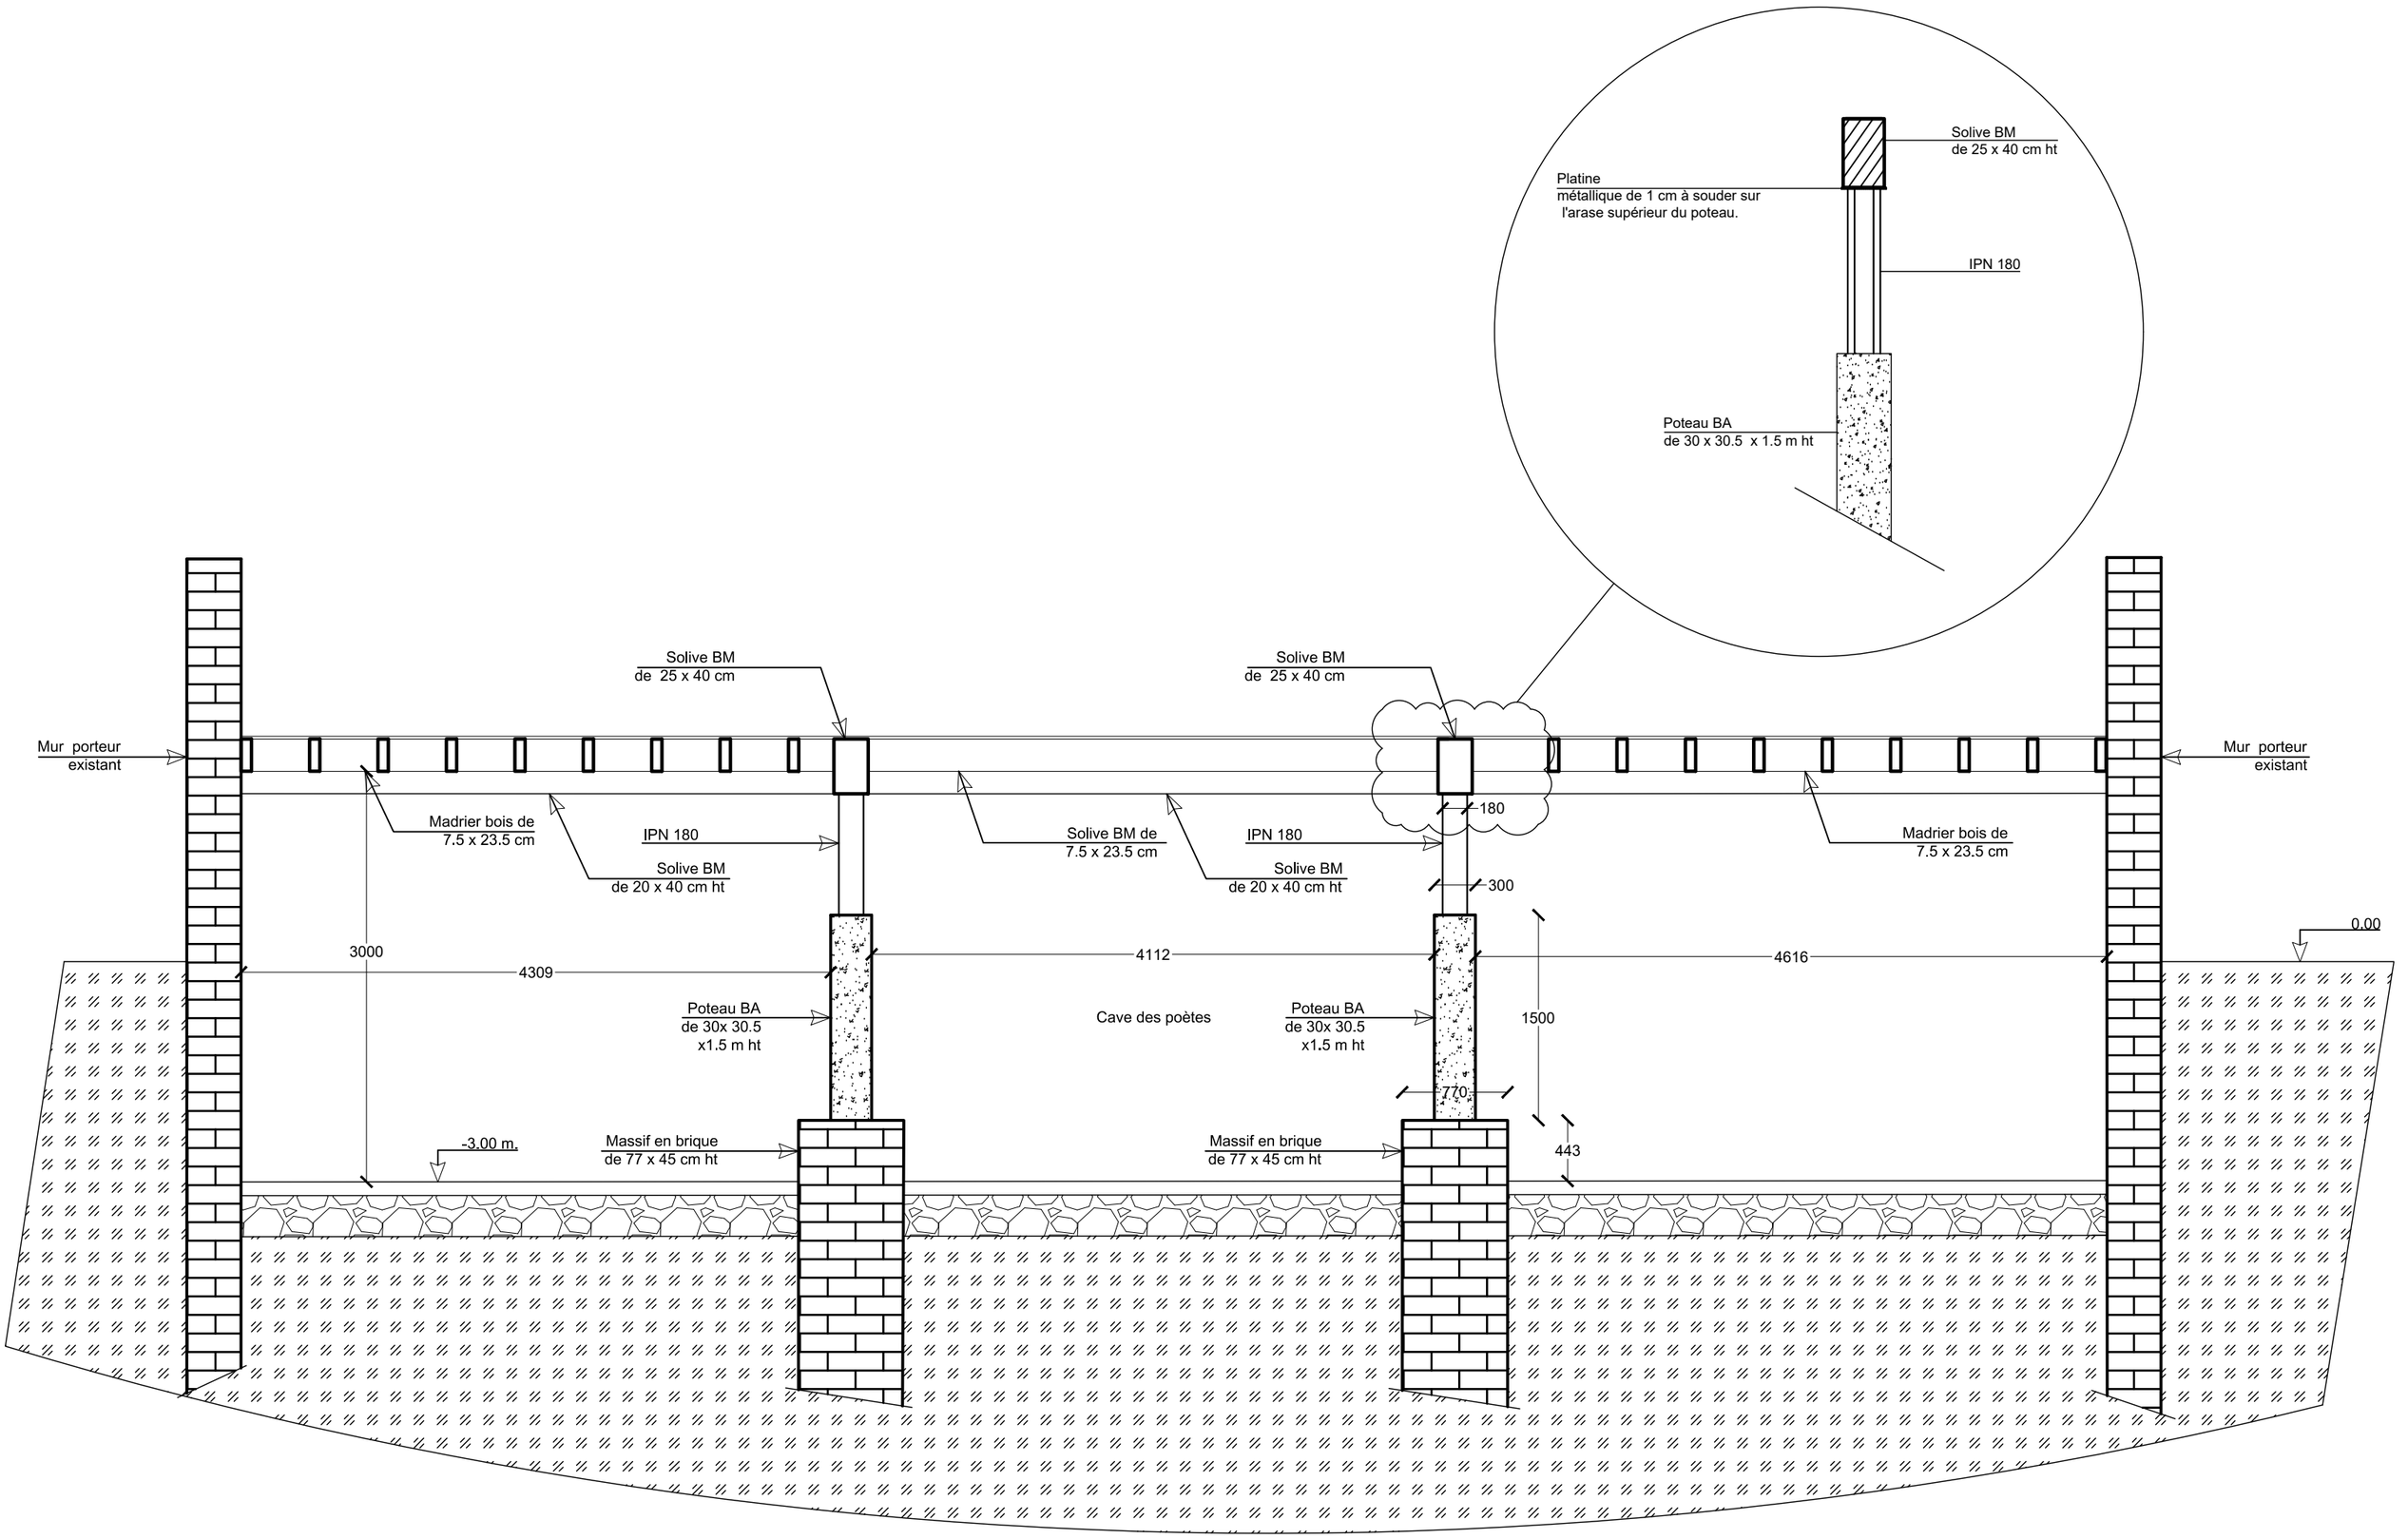

Coupe B-B projet

Maîtrise d'Ouvrage :
Mairie de Roubaix
17 Grand Place
59 100 Roubaix

BET STRUCTURE :
J.K.F. STRUCTURE
92 Bd du GLE du Gaulle
59100 Roubaix


Etude de la charge d'exploitation admissible pour la scene de la salle watremez

Dossier d'Etude Structurelle :
Coupe B-B projet

Plan N° : GO 06
Ech : 1/75

Ferraillage achelets :

10 HA 10 + 3 étriés Ø 6 mm.
Avec un enrobage
de 2 cm minimum sur
les quatre faces.

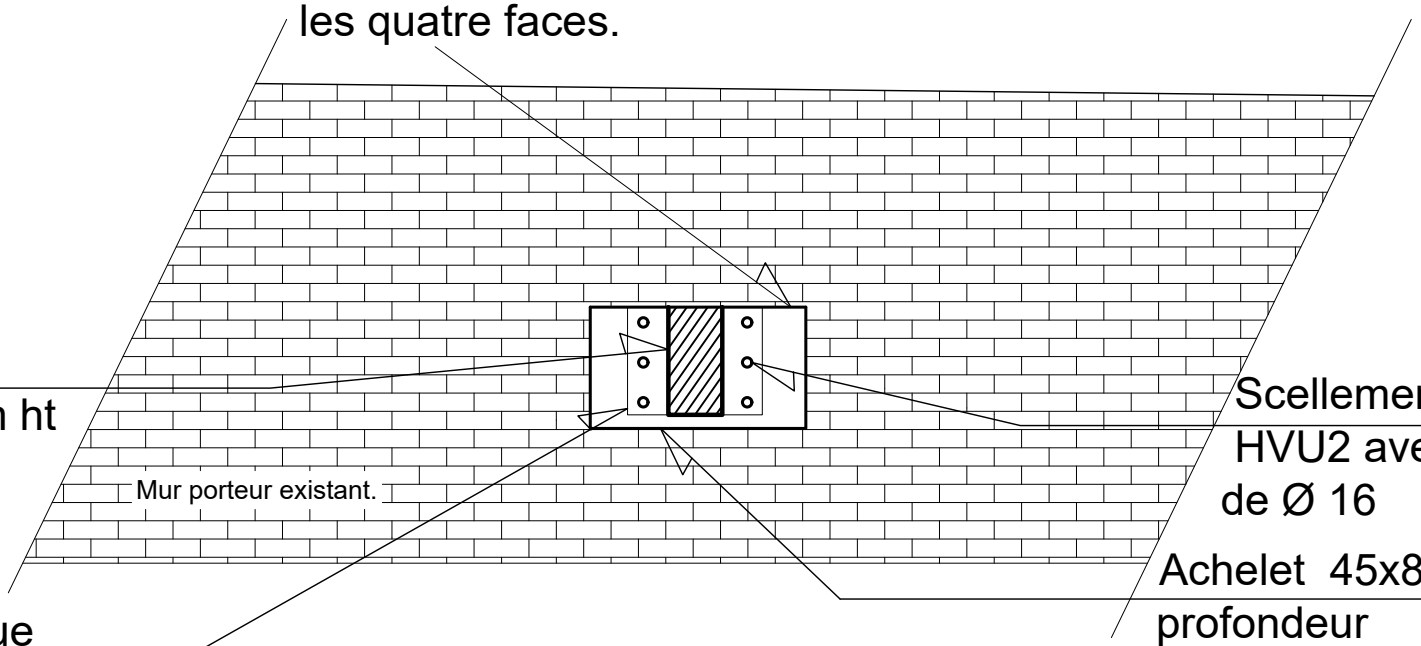

Solive BM
de 20 x 40 cm ht

Scellement chimique
HVU2 avec des tiges filetées
de Ø 16

Achelet 45x80x15 cm de
profondeur
en BA à créer dans le
mur existant.

Platine métallique
de 40 x 50 x 0.8 cm formée
par une épaisseur de 8 mm

Détail

Maîtrise d'Ouvrage :
Mairie de Roubaix
17 Grand Place
59 100 Roubaix

BET STRUCTURE :
J.K.F. STRUCTURE
92 Bd du GLE du Gaulle
59100 Roubaix

Etude de la charge d'exploitation
admissible pour la scene
de la salle watremez

Dossier d'Etude Structurelle :

Détail

Plan N° : GO 06

Ech : 1/75