

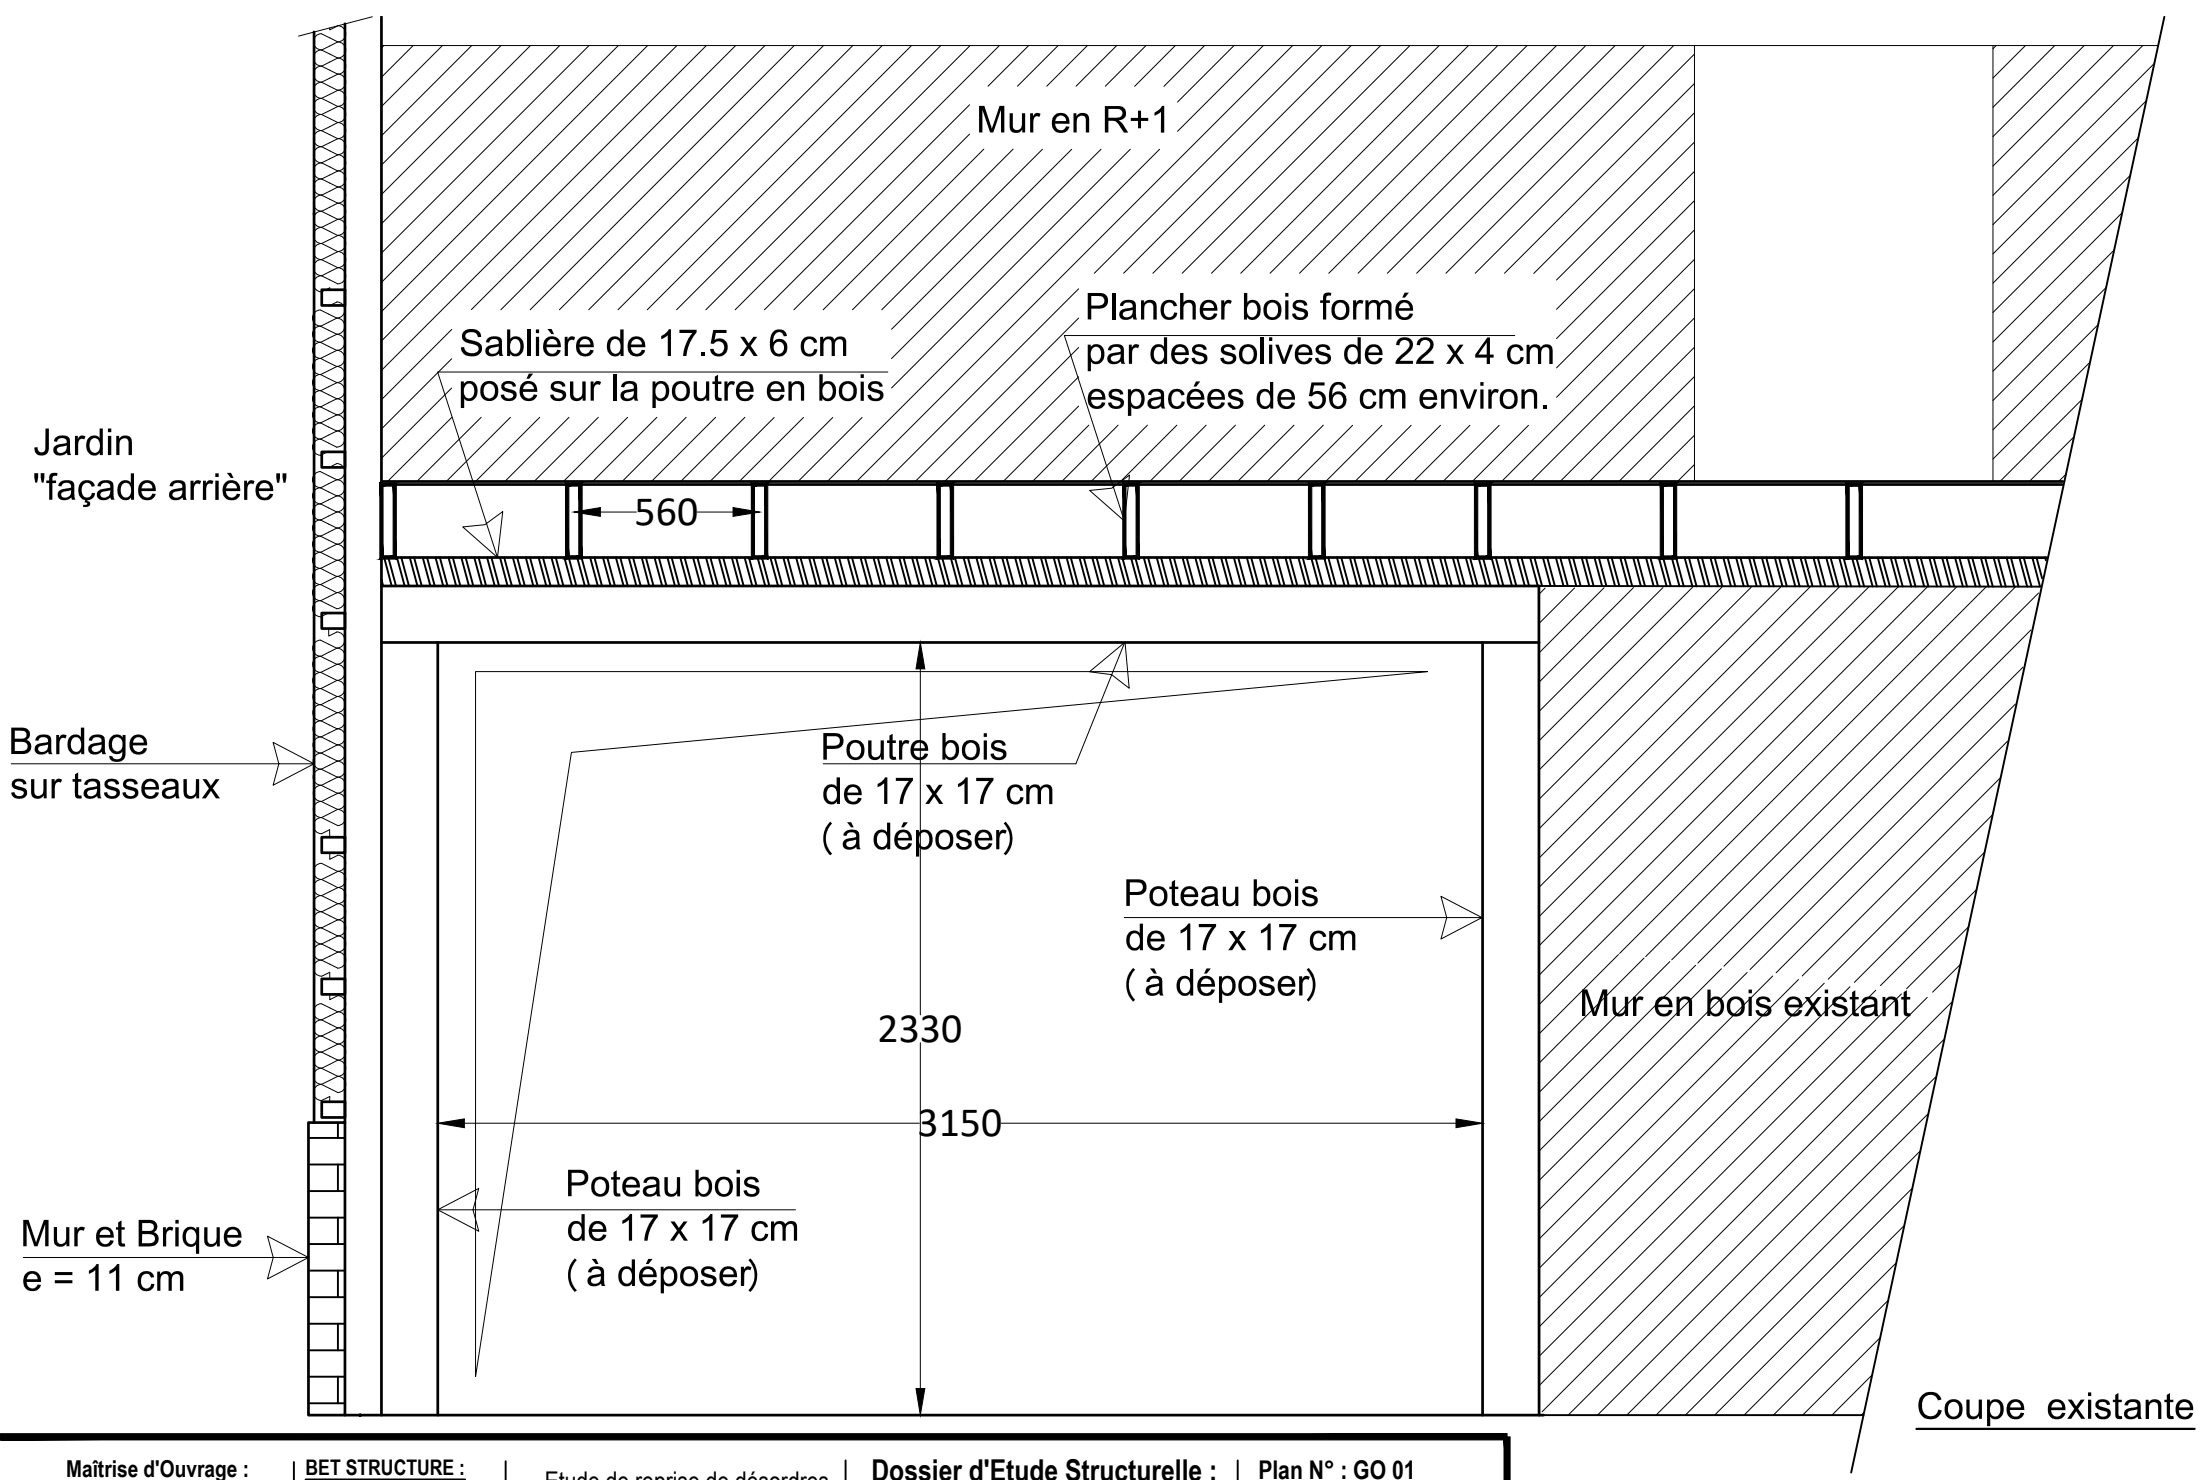


Maîtrise d'Ouvrage :	BET STRUCTURE :		Dossier d'Etude Structurelle :	Plan N° : GO 01
Mme Slaouni 87 rue de Nancy 59100 Roubaix	J.K.F. STRUCTURE 92 Bd du GLE du Gaulle 59100 Roubaix	Etude de reprise de désordres d'une ouverture déjà réalisée.	Coupe existante sur ouverture	Ech : 1/50

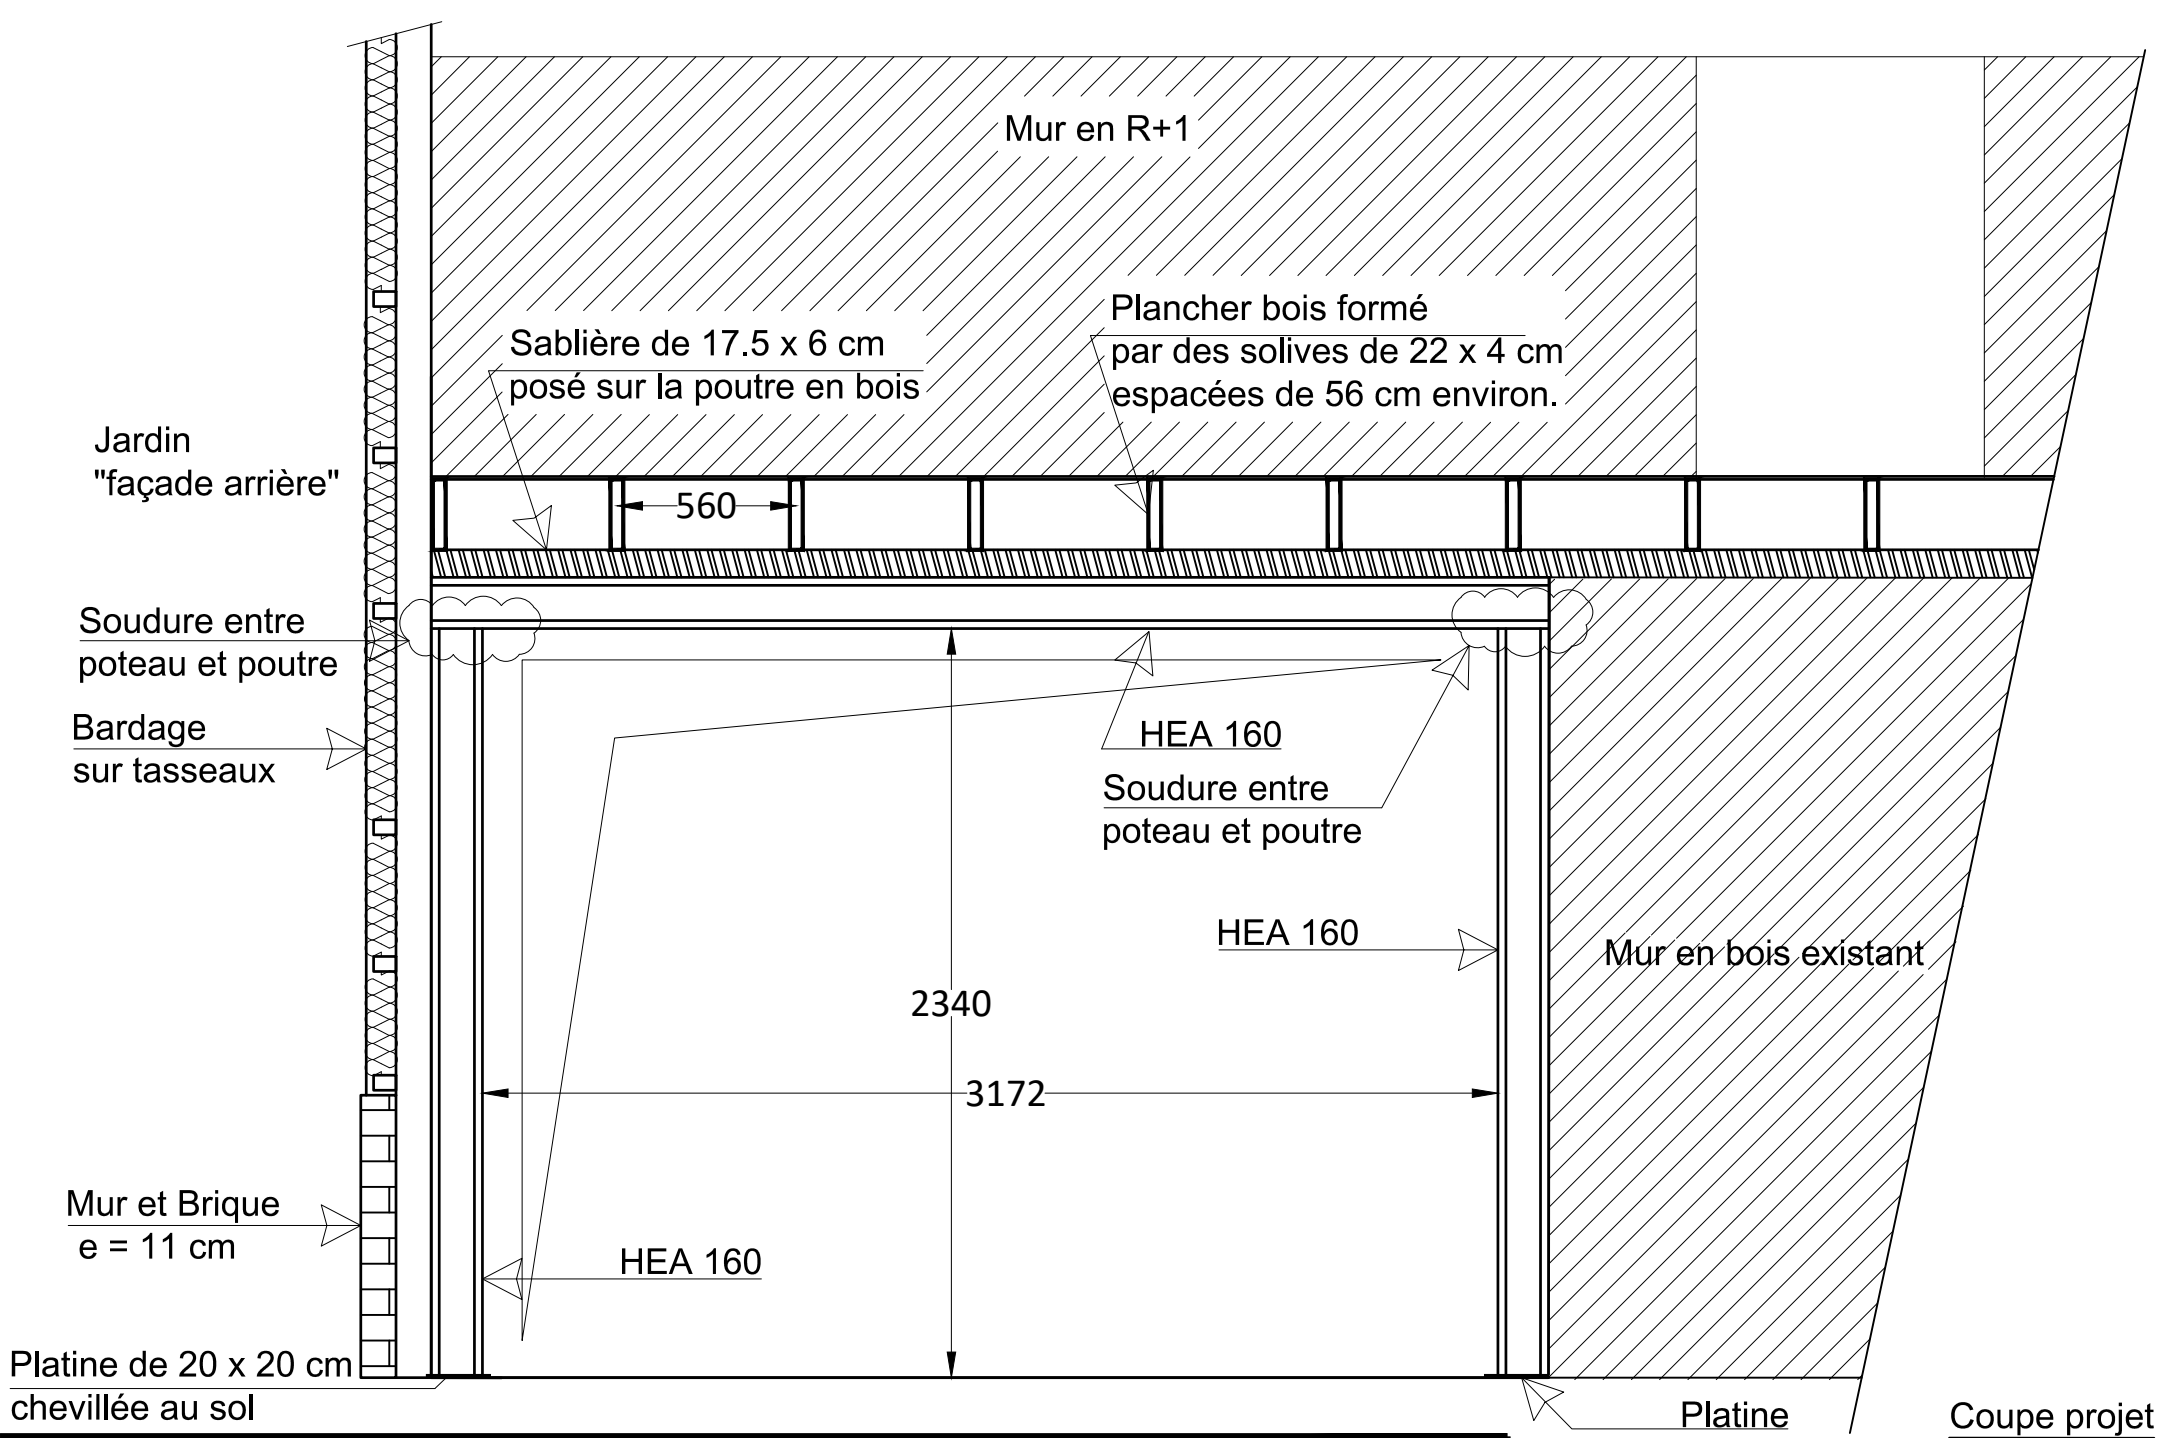


Coupe projet

Maîtrise d'Ouvrage :	BET STRUCTURE :		Dossier d'Etude Structurelle :	Plan N° : GO 02
Mme Slaouni 87 rue de Nancy 59100 Roubaix	J.K.F. STRUCTURE 92 Bd du GLE du Gaulle 59100 Roubaix	Etude de reprise de désordres d'une ouverture déjà réalisée.	Coupe projet sur ouverture	Ech : 1/50

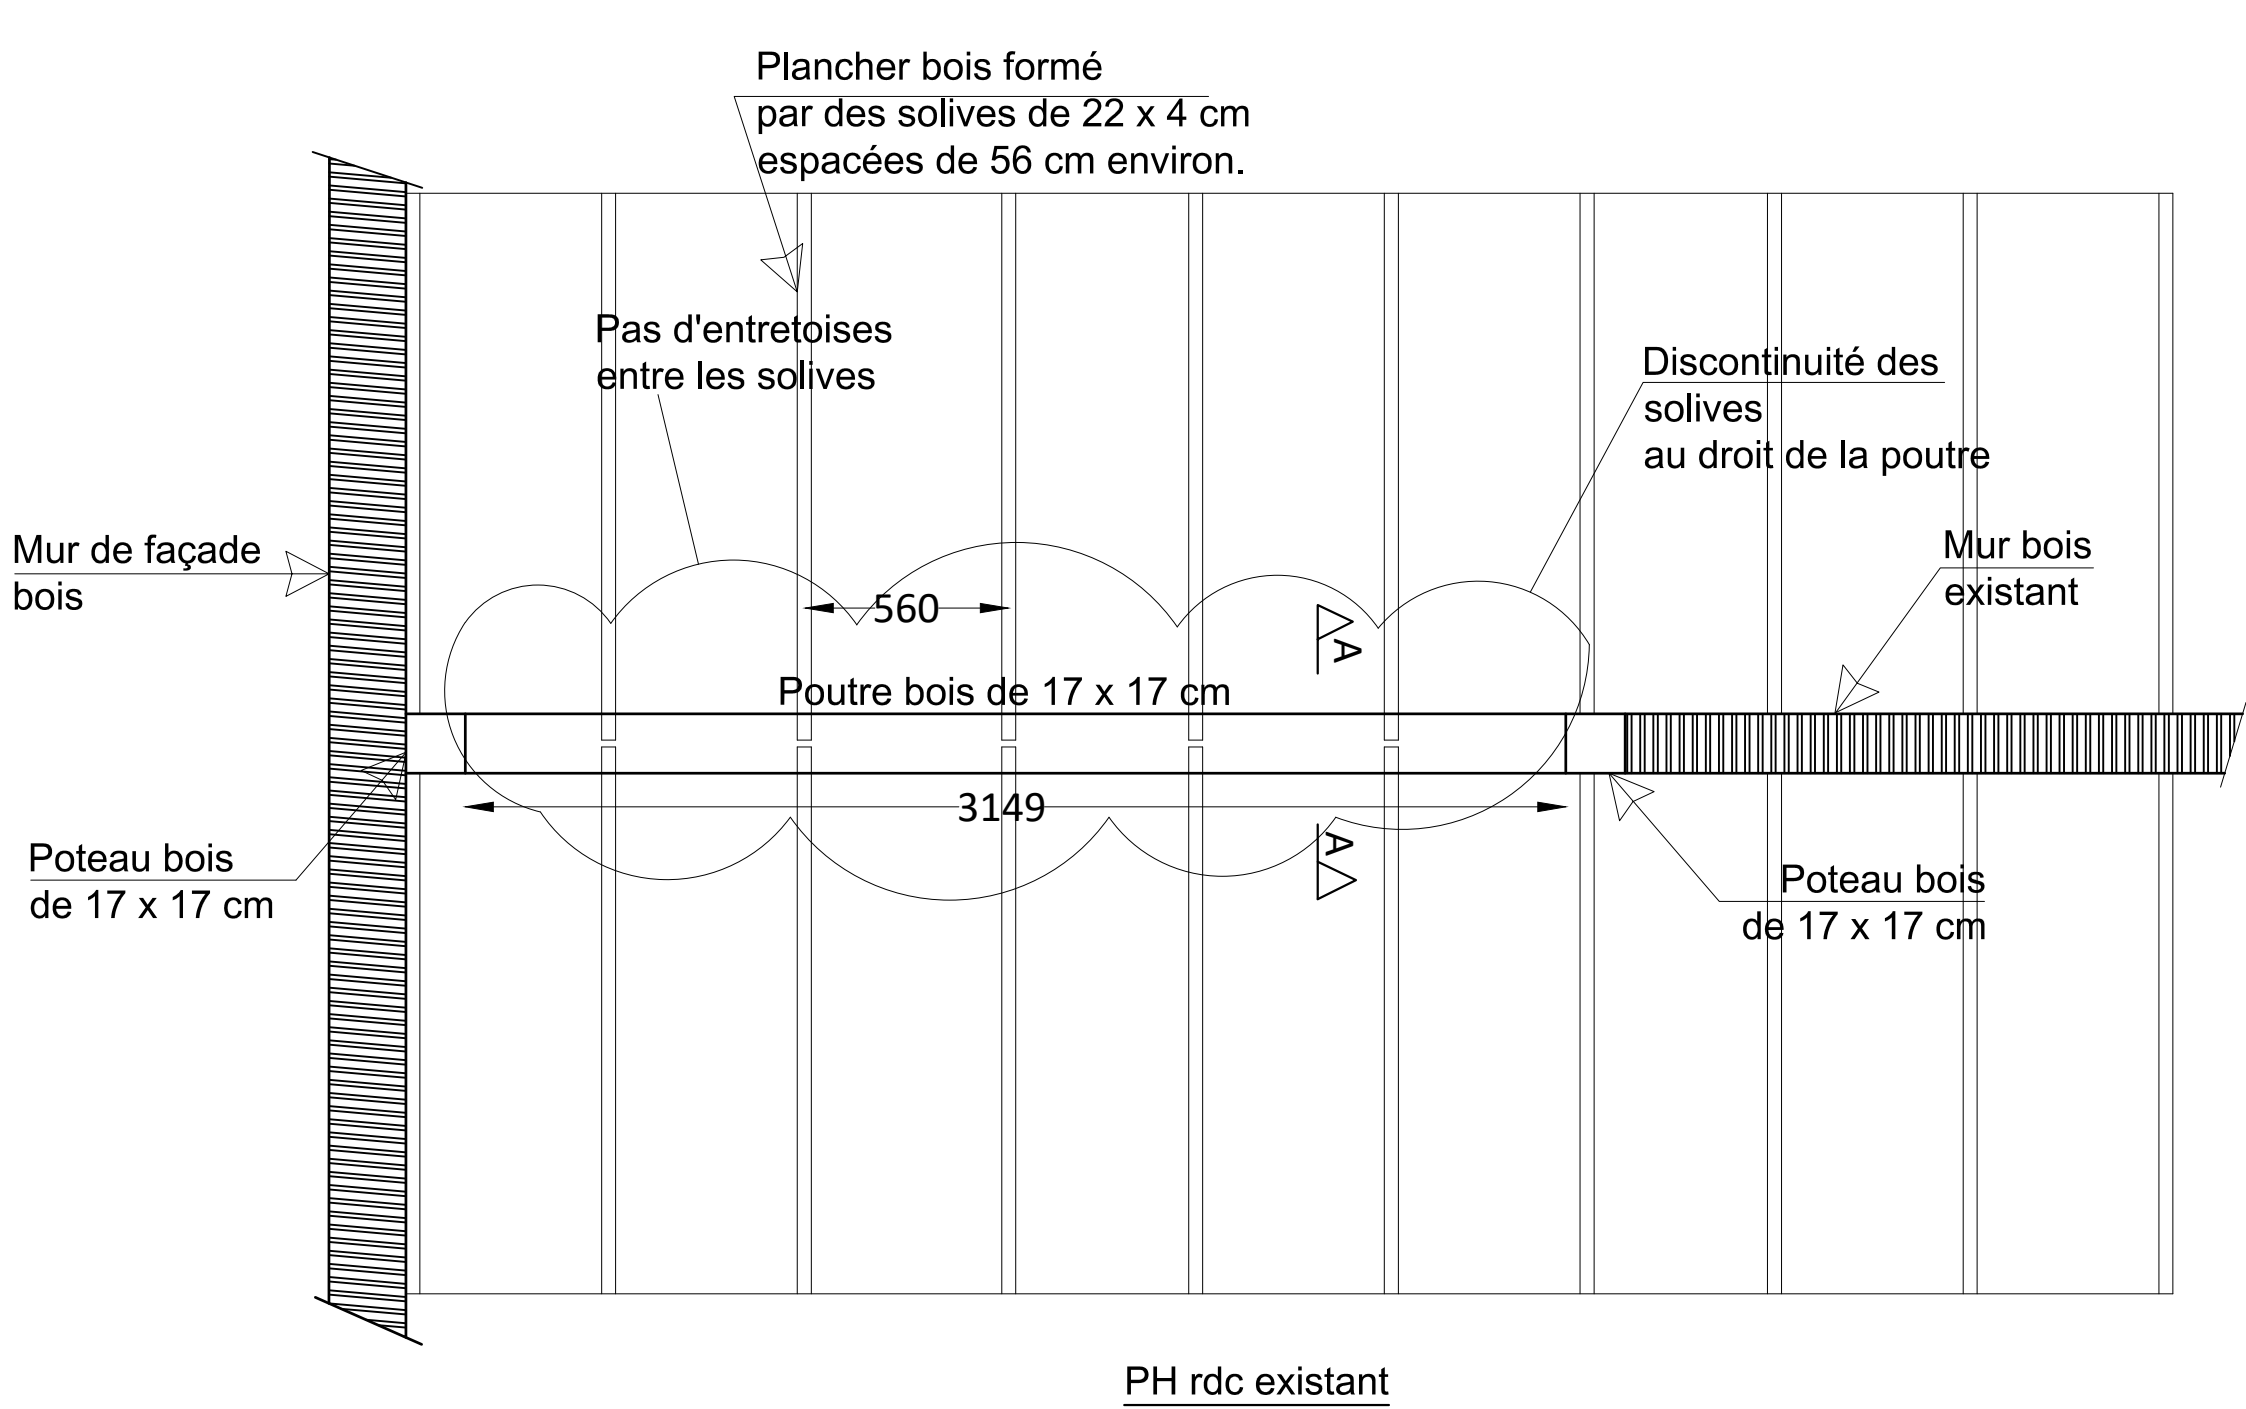


PH rdc existant

Maîtrise d'Ouvrage :	BET STRUCTURE :		Dossier d'Etude Structurelle :	Plan N° : GO 03
Mme Slaouni 87 rue de Nancy 59100 Roubaix	J.K.F. STRUCTURE 92 Bd du GLE du Gaulle 59100 Roubaix	Etude de reprise de désordres d'une ouverture déjà réalisée.	PH rdc existant	Ech : 1/50

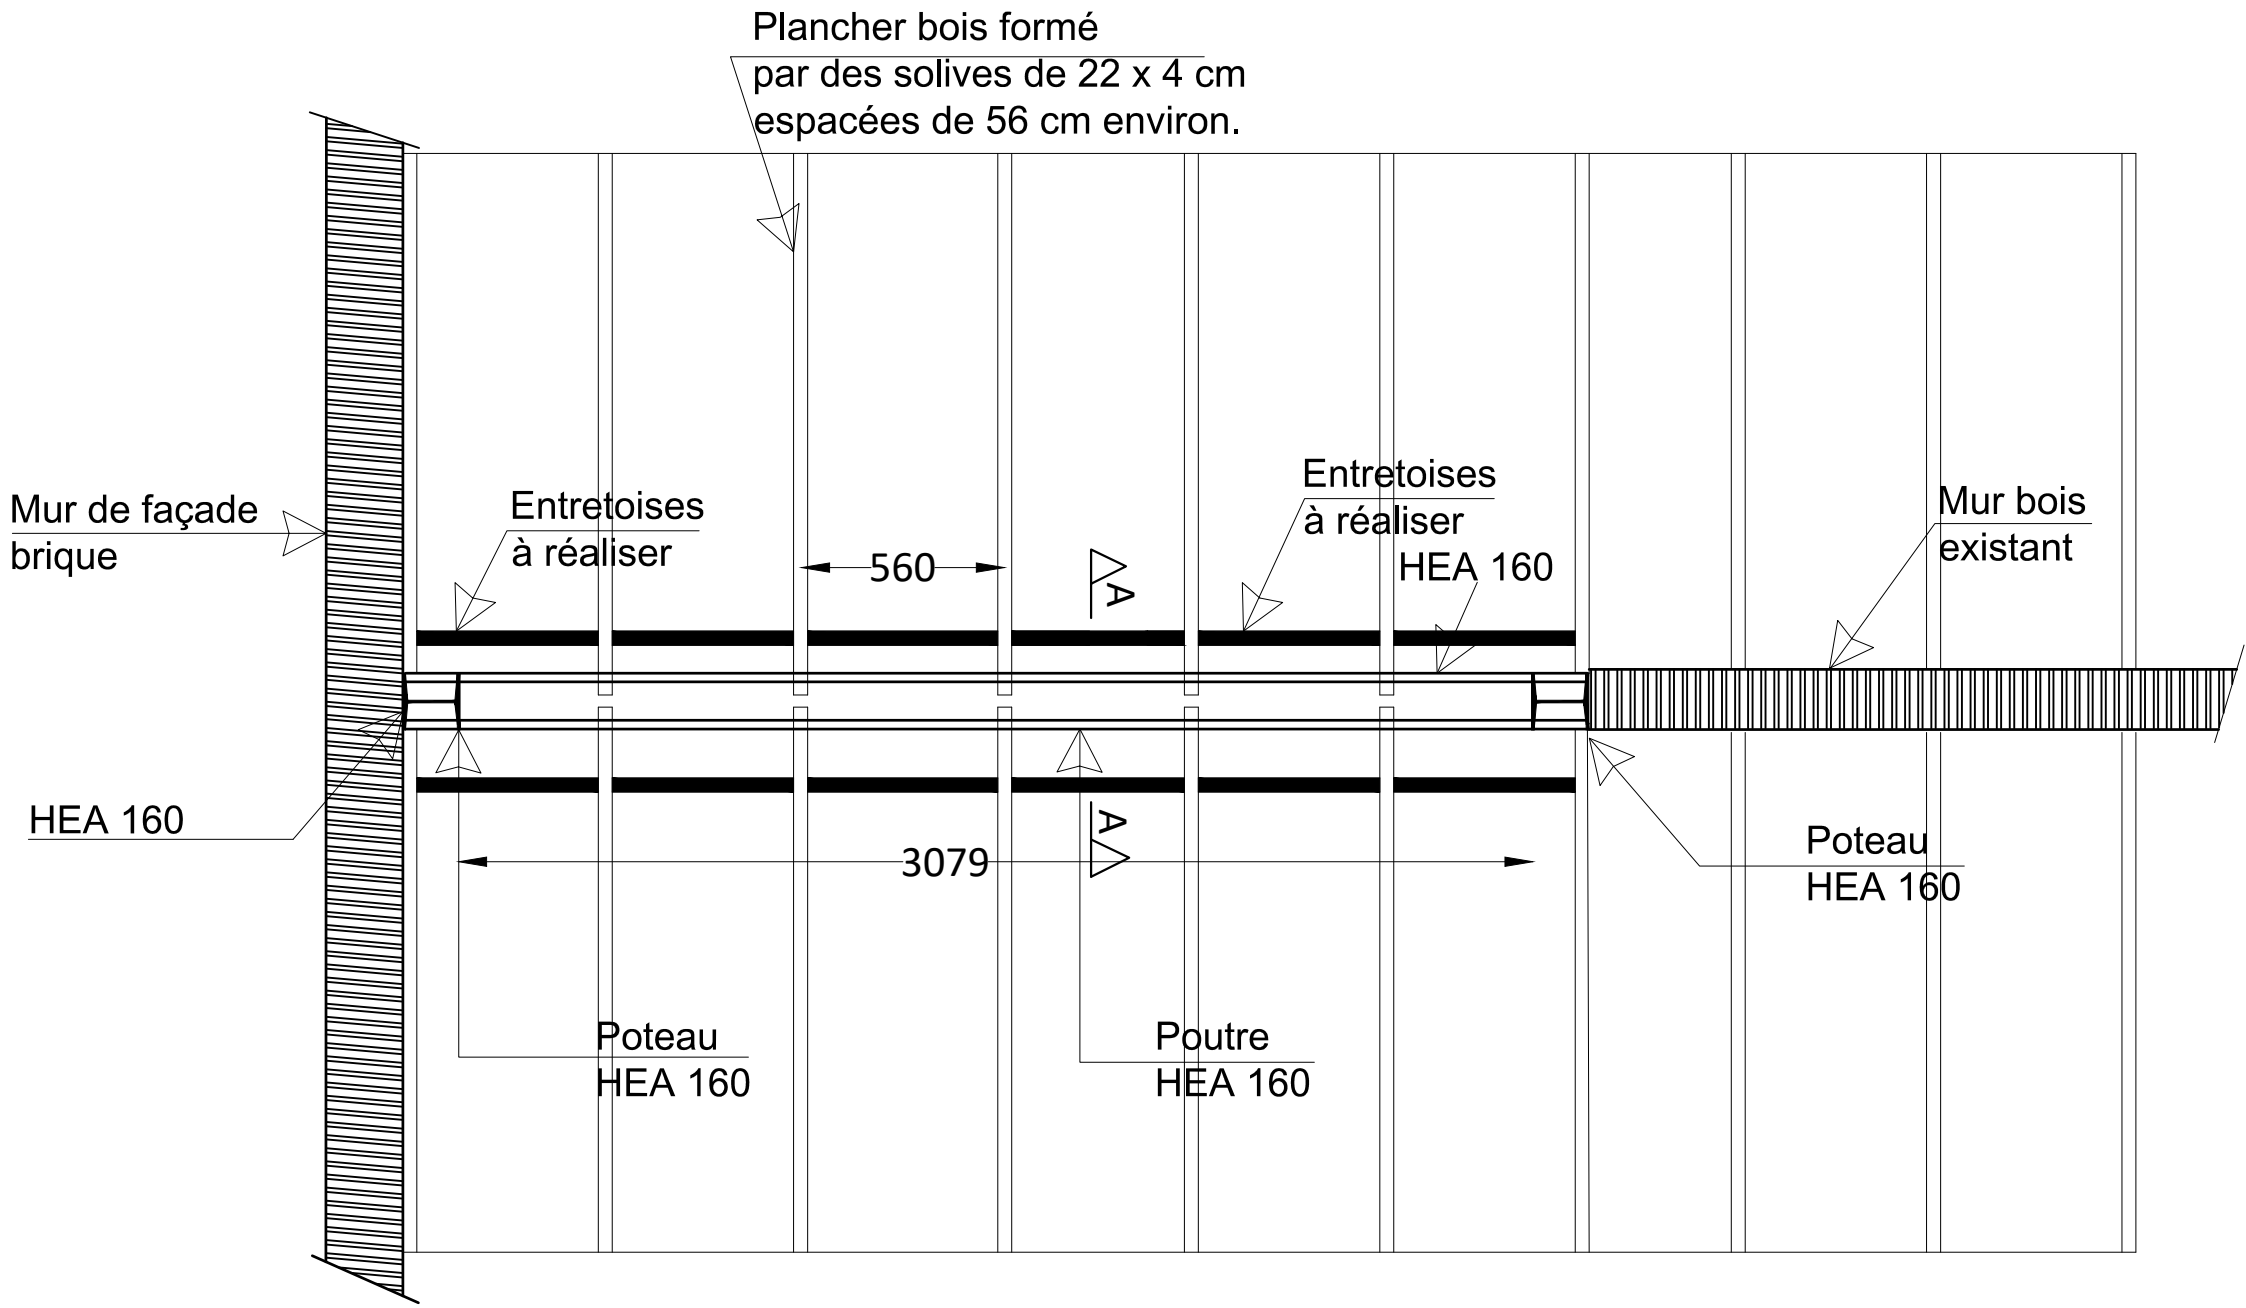

PH rdc projet

Maîtrise d'Ouvrage : Mme Slaouni 87 rue de Nancy 59100 Roubaix	**BET STRUCTURE :** J.K.F. STRUCTURE 92 Bd du GLE du Gaulle 59100 Roubaix	Etude de reprise de désordres d'une ouverture déjà réalisée.	**Dossier d'Etude Structurelle :** PH rdc projet	**Plan N° : GO 04** Ech : 1/50

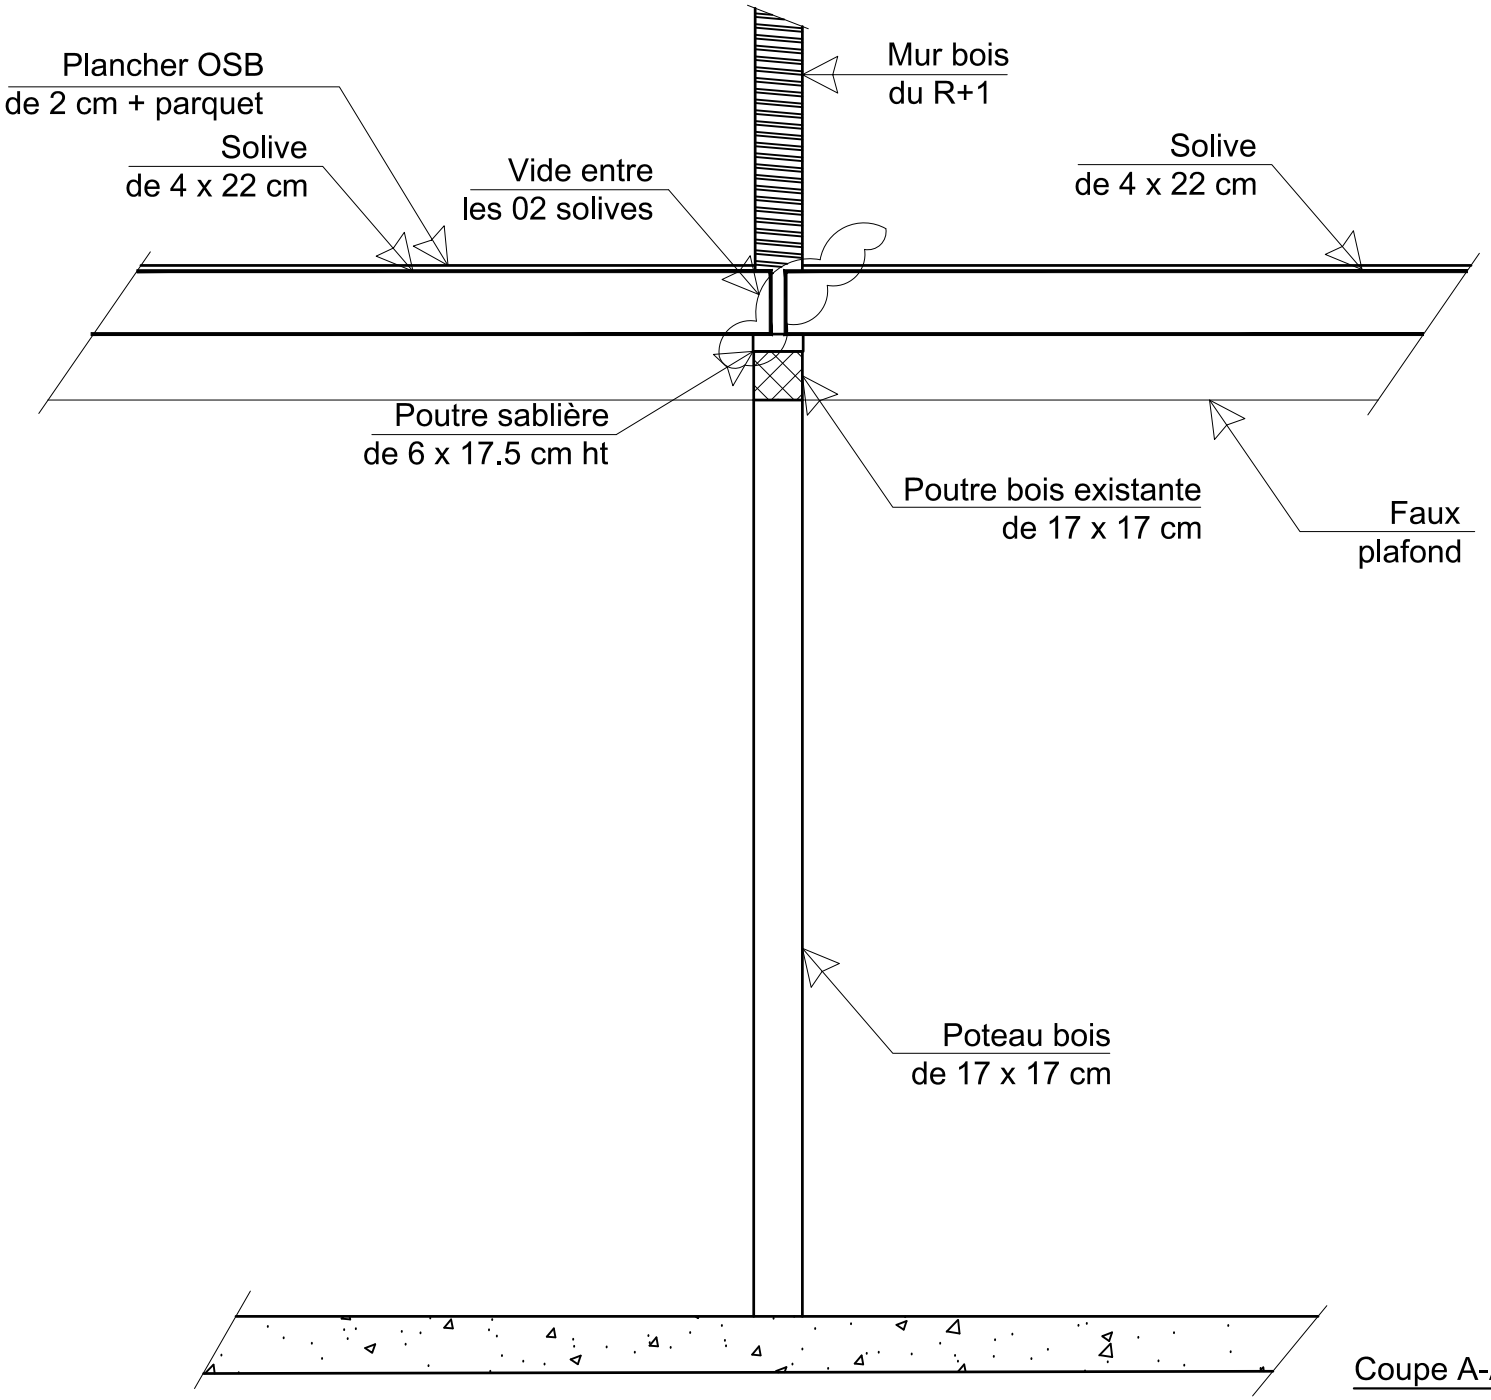

Coupe A-A existante


Maîtrise d'Ouvrage :
Mme Slaouni
87 rue de Nancy
59100 Roubaix

BET STRUCTURE :
J.K.F. STRUCTURE
92 Bd du GLE du Gaulle
59100 Roubaix

Etude de reprise de désordres d'une ouverture déjà réalisée.

Dossier d'Etude Structurelle :
Coupe A-A existant

Plan N° : GO 05
Ech : 1/50

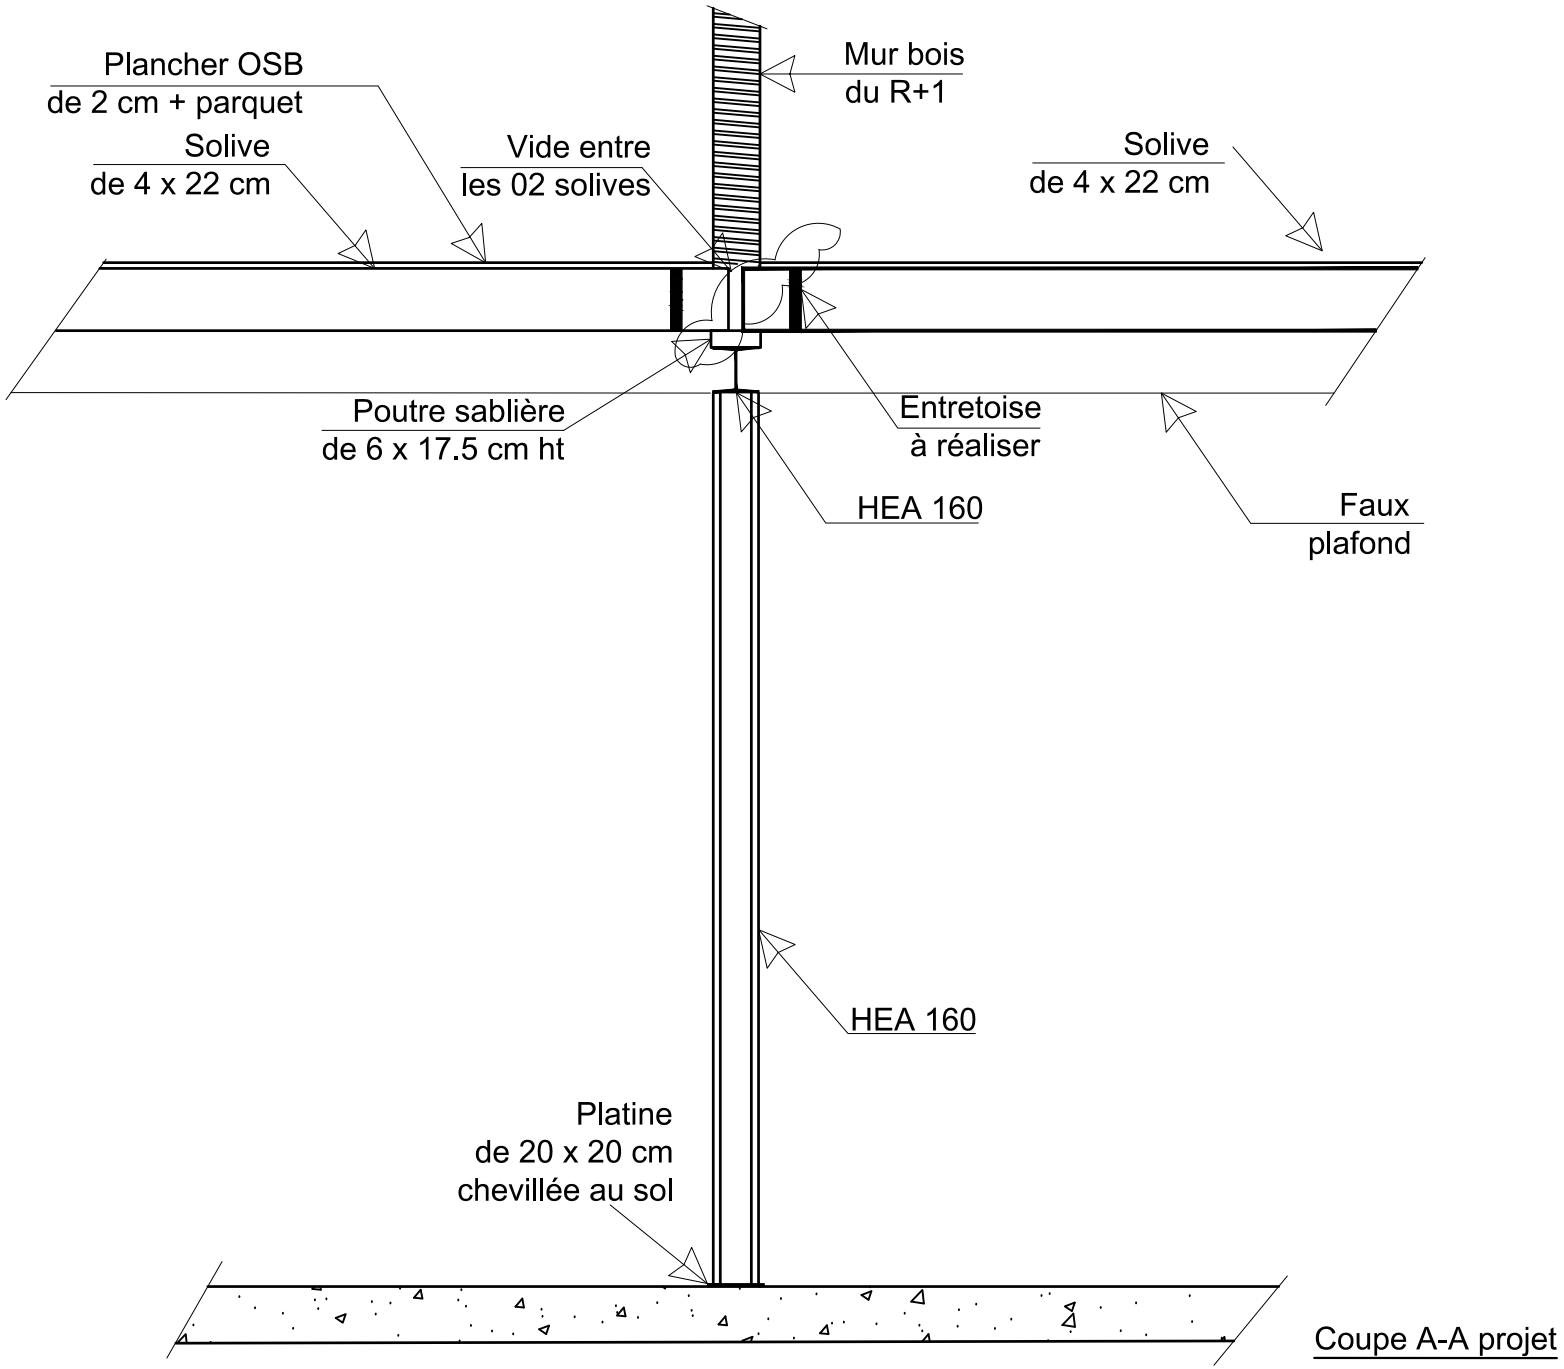

Coupe A-A projet

Maîtrise d'Ouvrage :
Mme Slaouni
87 rue de Nancy
59100 Roubaix

BET STRUCTURE :
J.K.F. STRUCTURE
92 Bd du GLE du Gaulle
59100 Roubaix

Etude de reprise de désordres d'une ouverture déjà réalisée

Dossier d'Etude Structurelle :
Coupe A-A projet

Plan N° : GO 06
Ech : 1/50