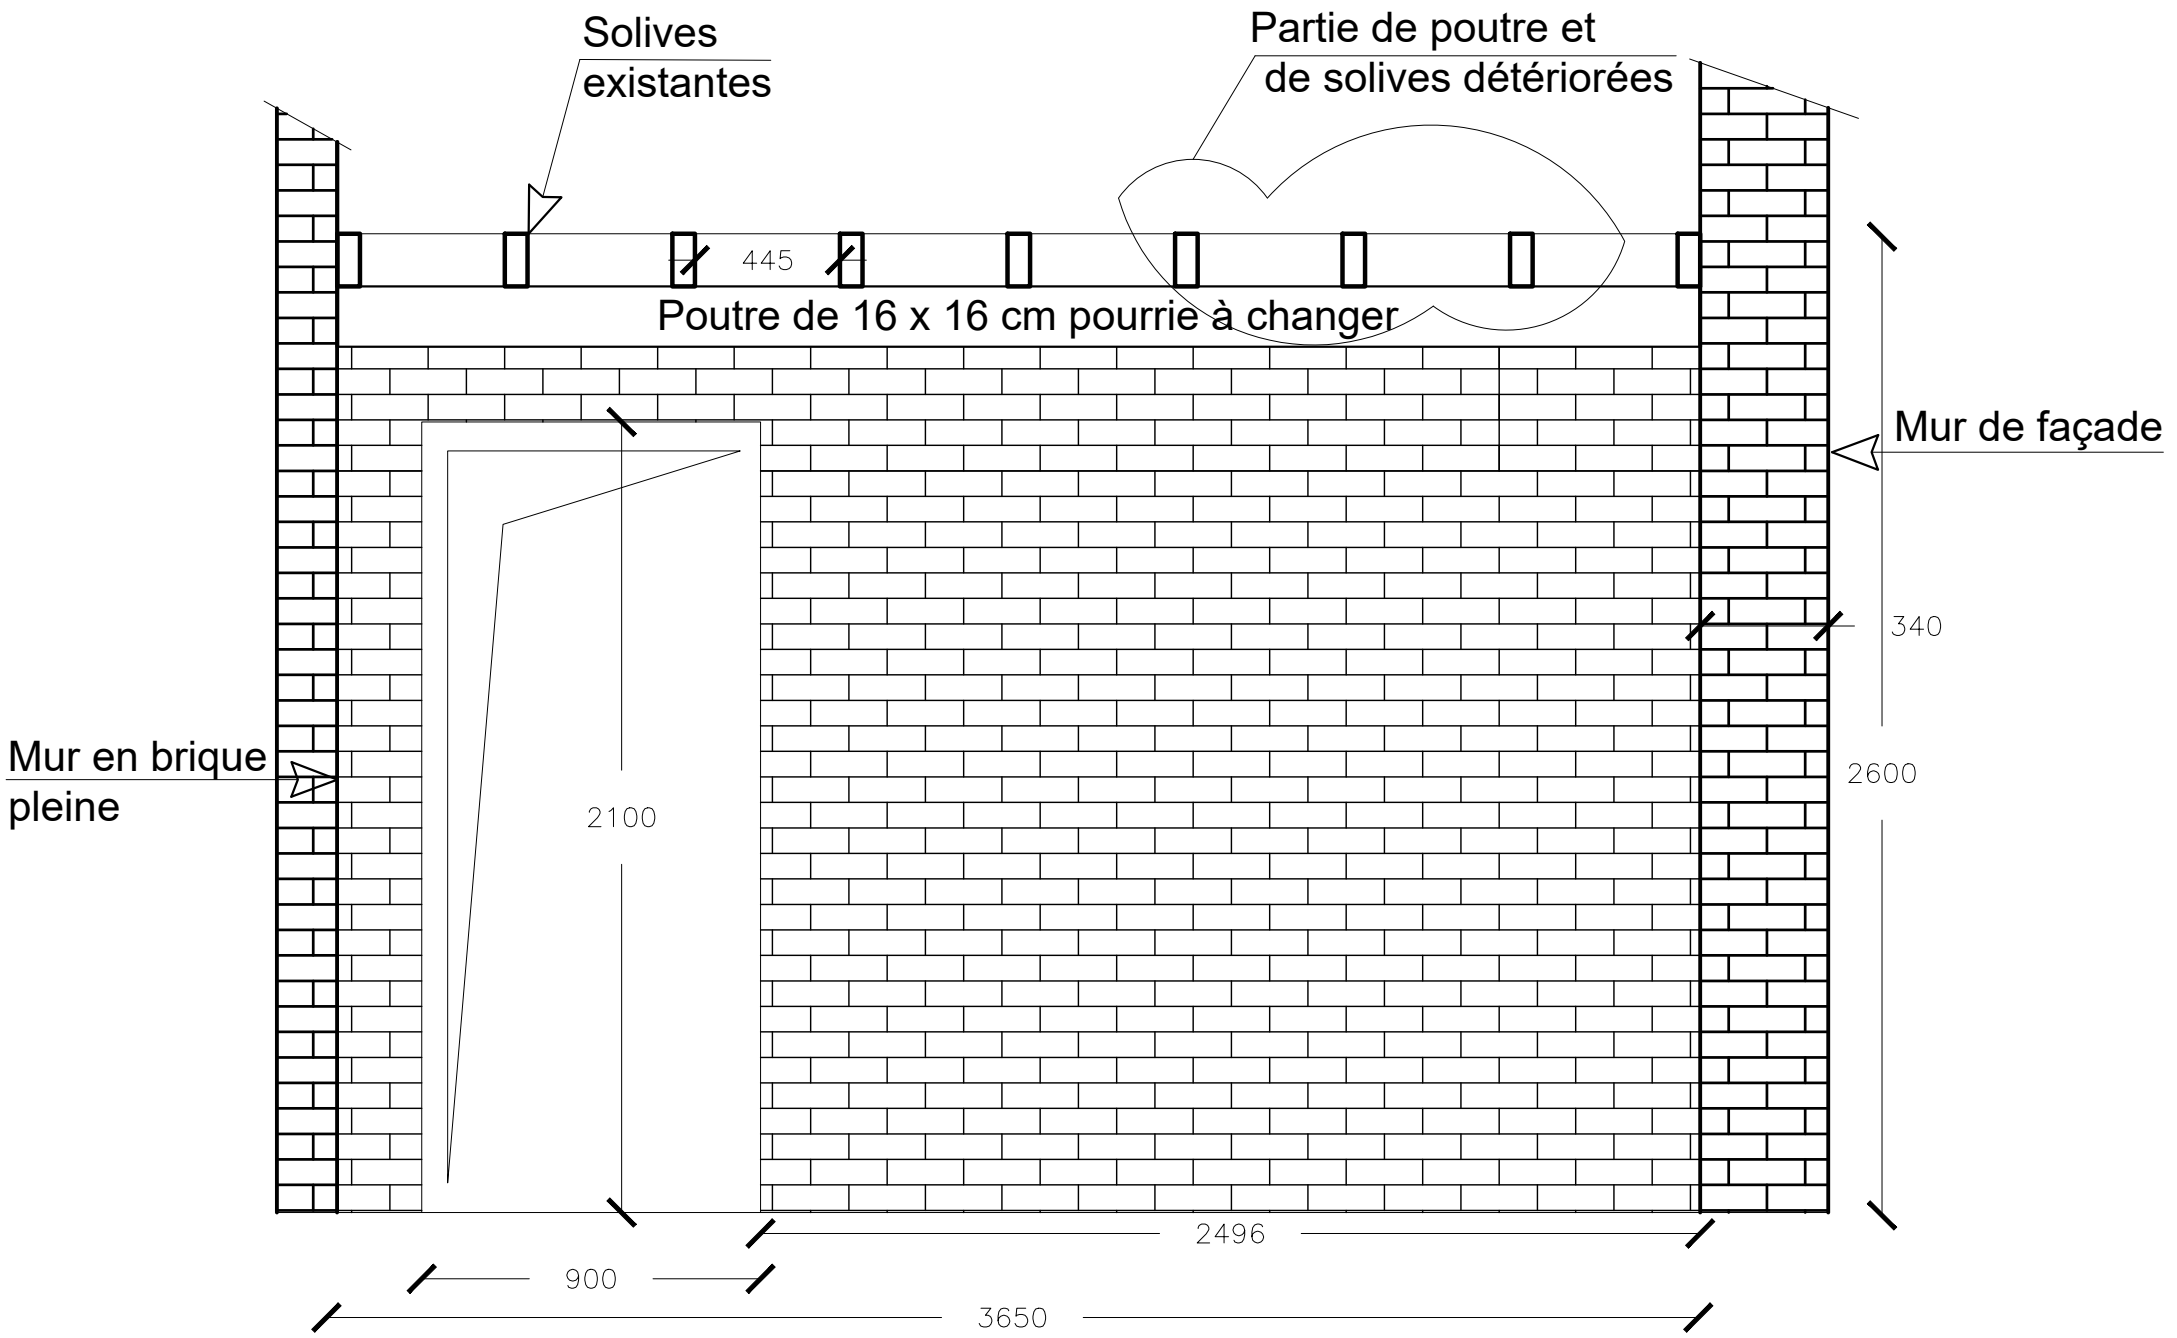



**Maîtrise de l'Ouvrage :**
Syndicat des copropriétaires
M Gissot Mathieu
121 Rue d'Arras
59000 Lille

**BET STRUCTURE :**
J.K.F. STRUCTURE
92 Bd du GLE du Gaulle
59100 Roubaix


Reprise d'une structure bois dégradée

**Dossier Etude Béton Armé**

**Vue de face actuelle**

**Plan N° : GO 01**

**Ech : 1/20**

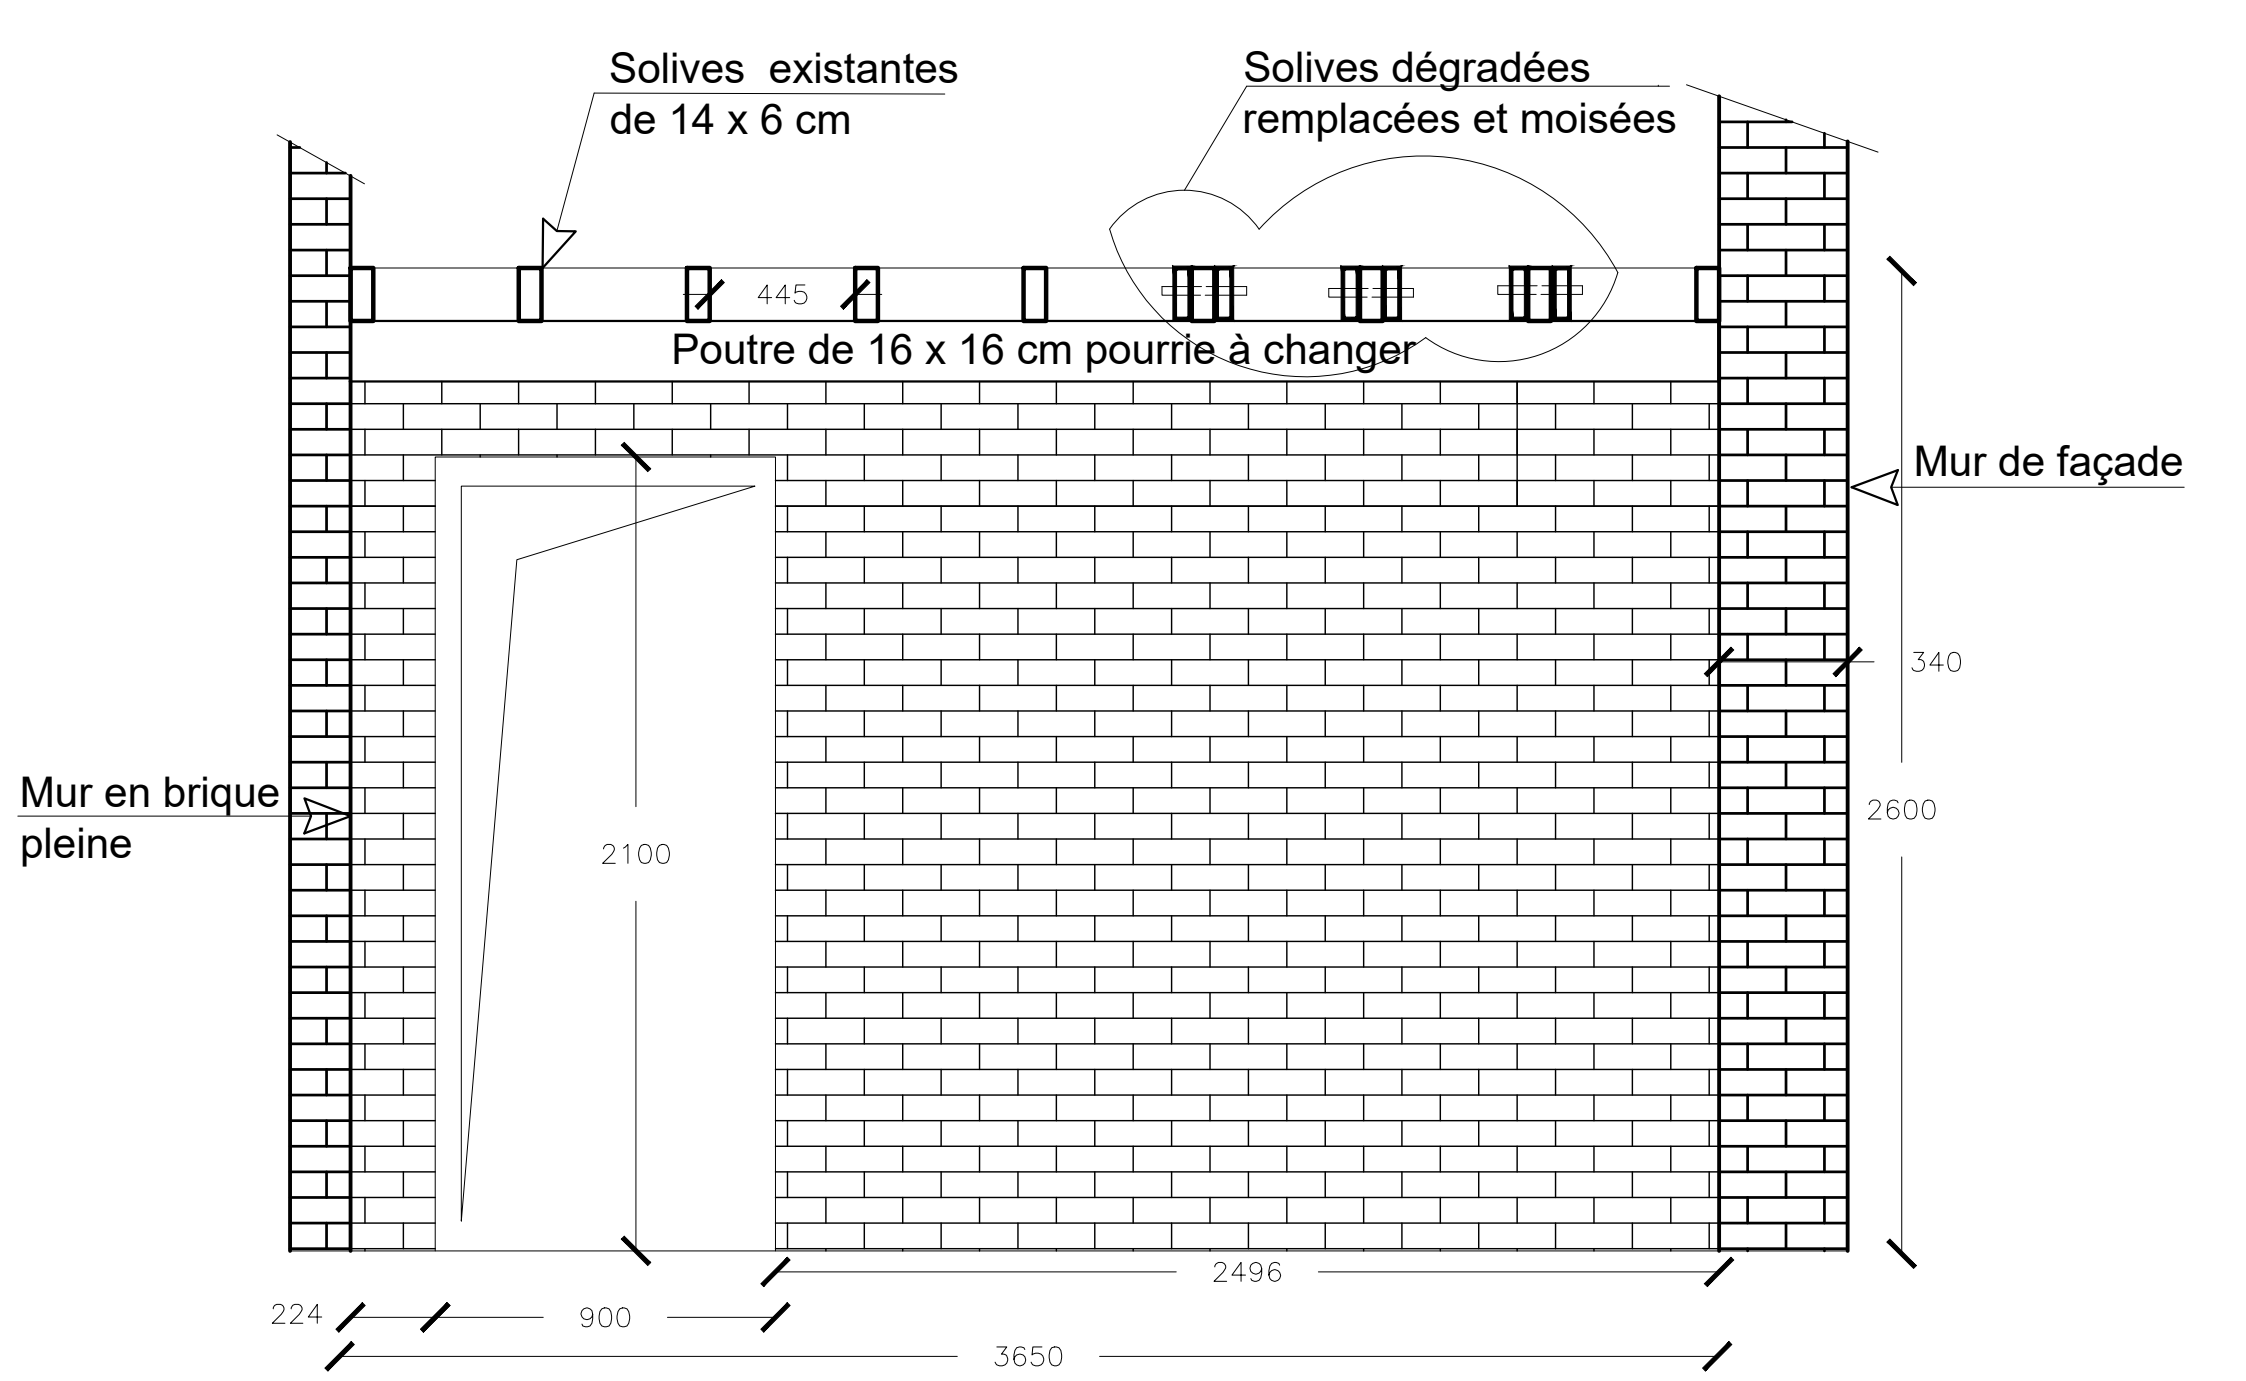


**Maîtrise de l'Ouvrage :**
Syndicat des copropriétaires
M Gissot Mathieu
121 Rue d'Arras
59000 Lille

**BET STRUCTURE :**
J.K.F. STRUCTURE
92 Bd du GLE du Gaulle
59100 Roubaix


Reprise d'une structure bois dégradée

**Dossier Etude Béton Armé**

**Vue de face projet**

**Plan N° : GO 02**

**Ech : 1/20**

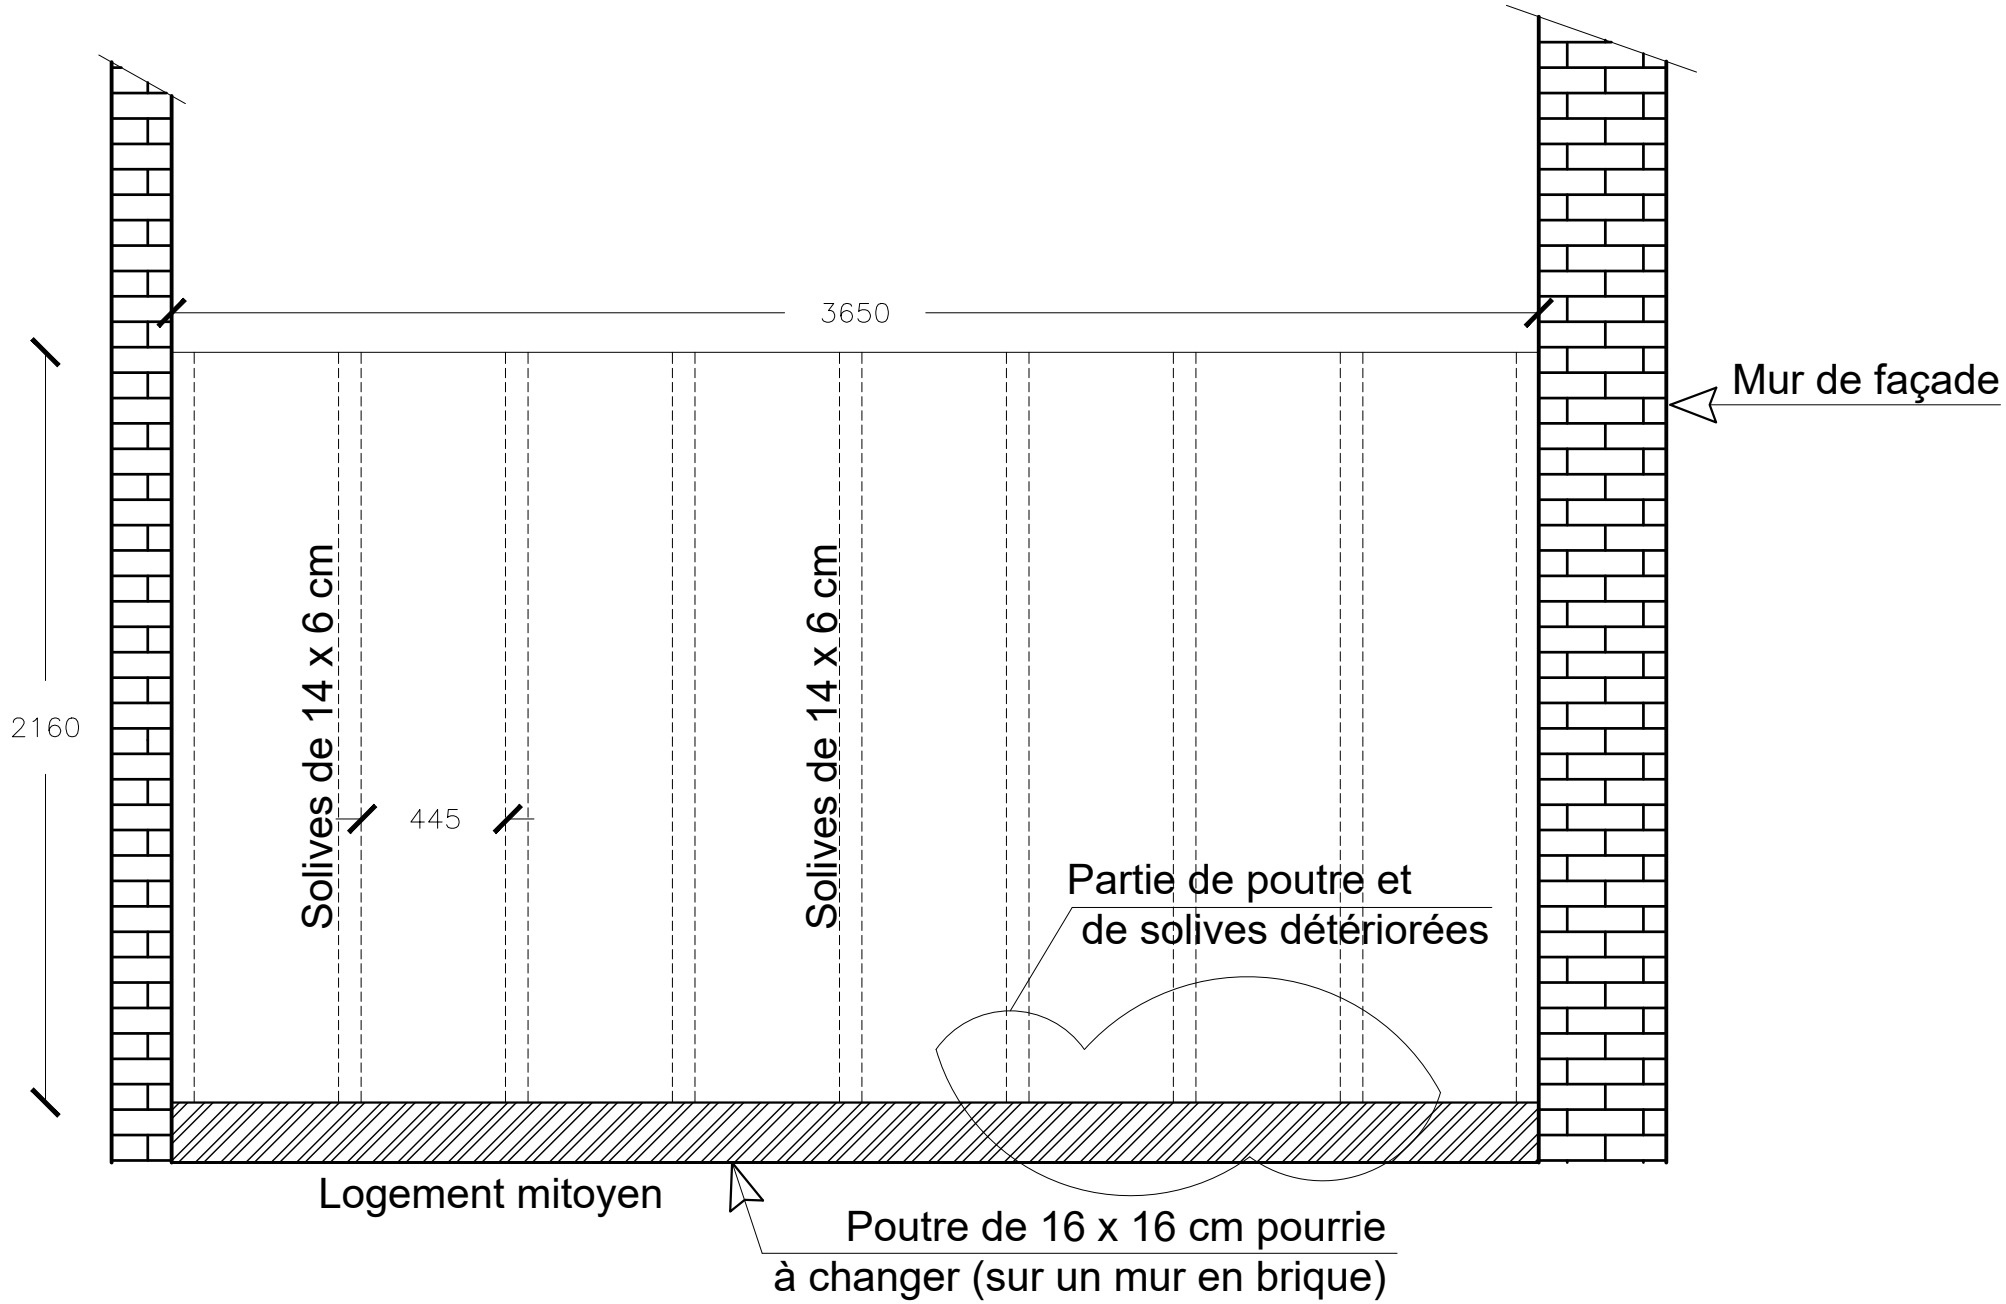


**Maîtrise de l'Ouvrage :**
Syndicat des copropriétaires
M Gissot Mathieu
121 Rue d'Arras
59000 Lille

**BET STRUCTURE :**
J.K.F. STRUCTURE
92 Bd du GLE du Gaulle
59100 Roubaix


Reprise d'une structure bois dégradée

**Dossier Etude Béton Armé**

**Vue en plan existant**

**Plan N° : GO 03**

**Ech : 1/15**

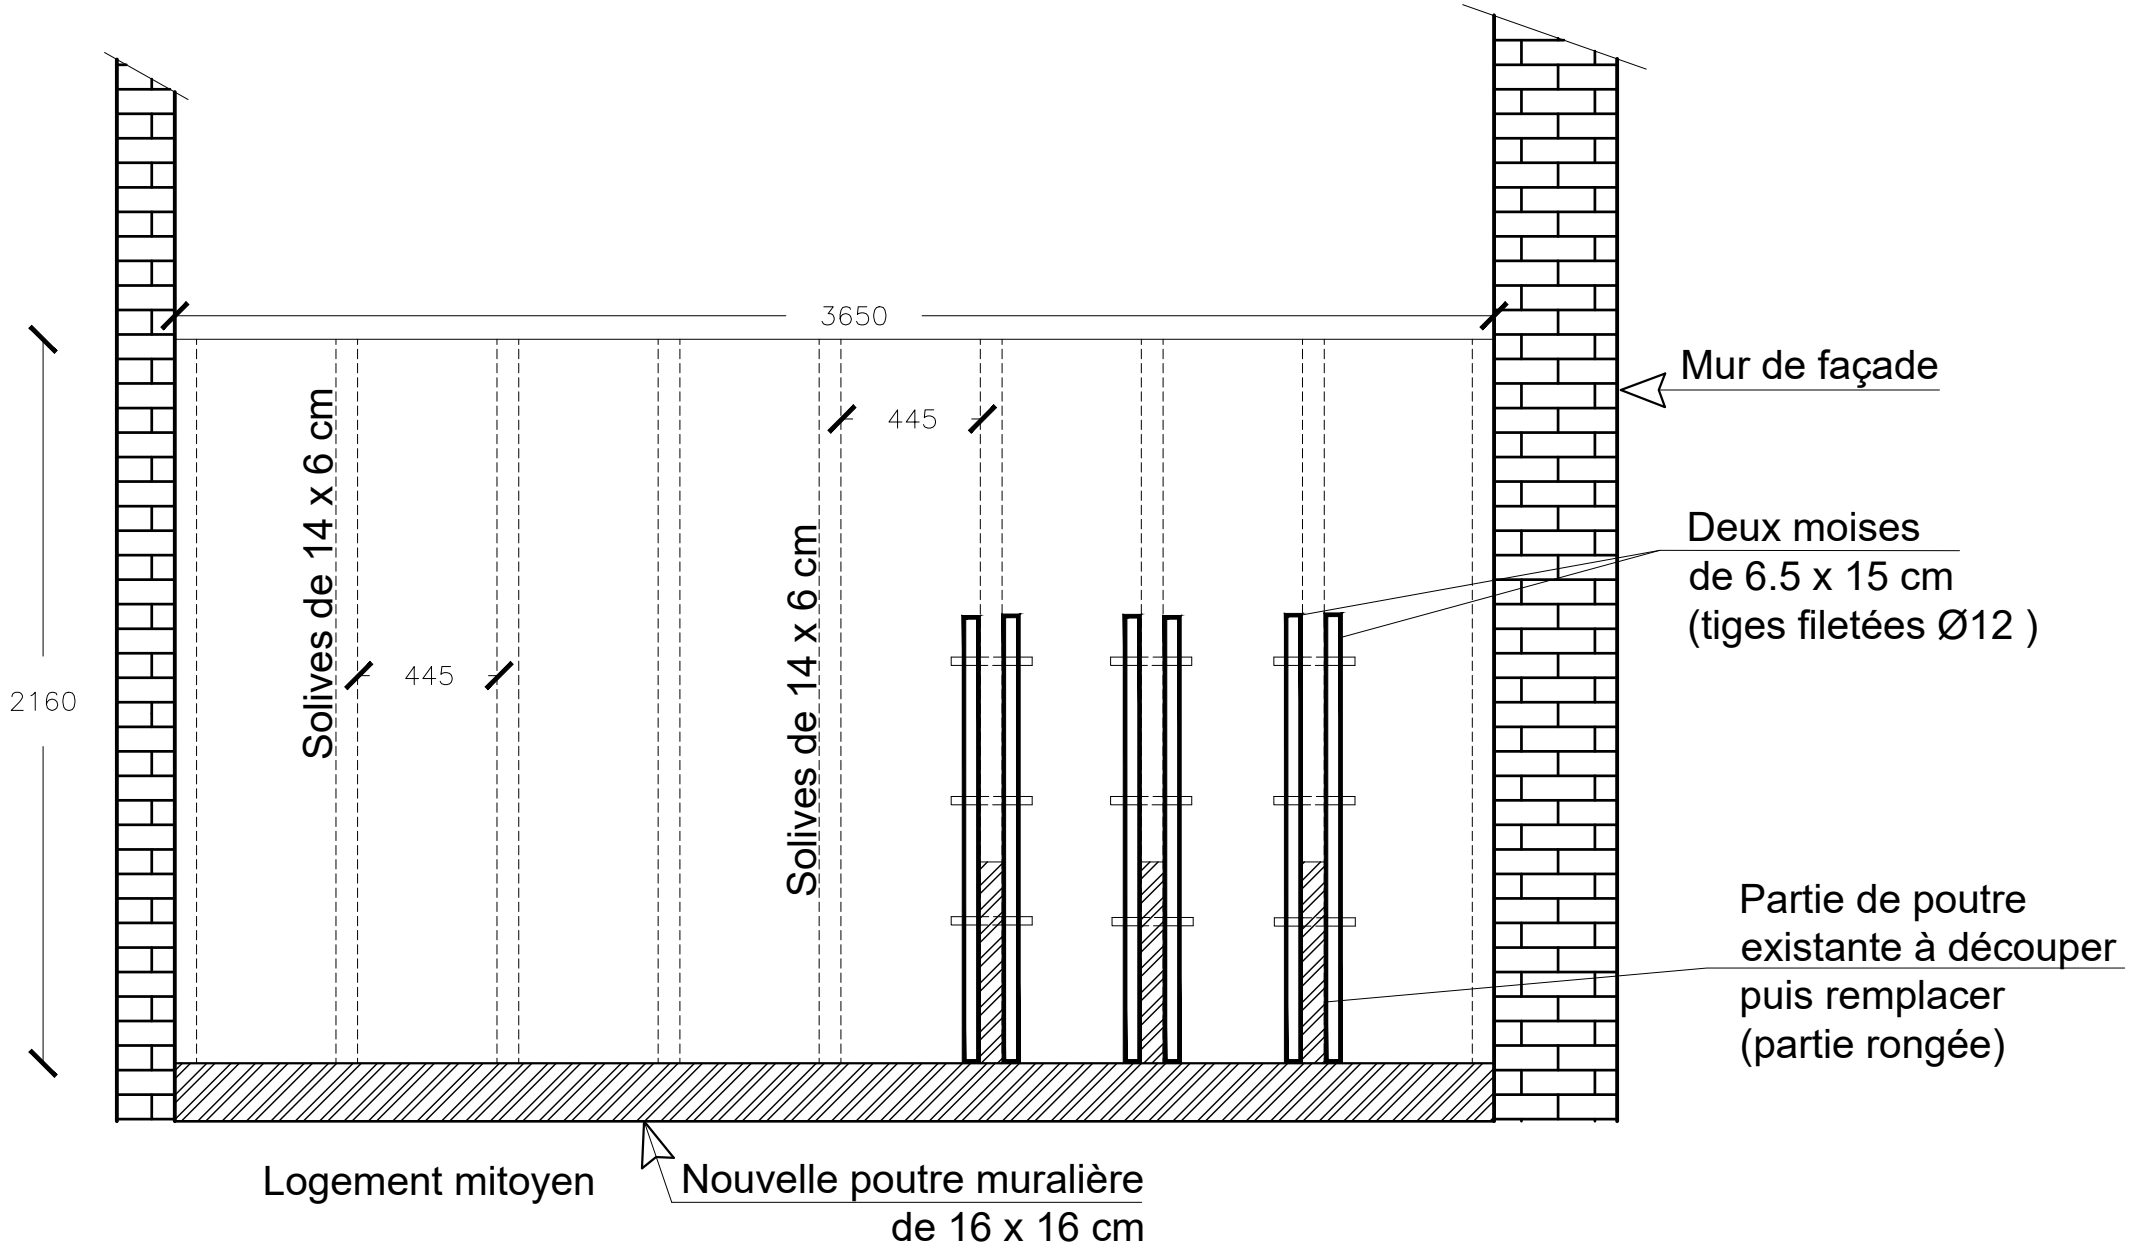


**Maîtrise de l'Ouvrage :**
Syndicat des copropriétaires
M Gissot Mathieu
121 Rue d'Arras
59000 Lille

**BET STRUCTURE :**
J.K.F. STRUCTURE
92 Bd du GLE du Gaulle
59100 Roubaix

Reprise d'une structure bois dégradée

**Dossier Etude Béton Armé**

**Vue en plan projet**

**Plan N° : GO 04**

**Ech : 1/15**