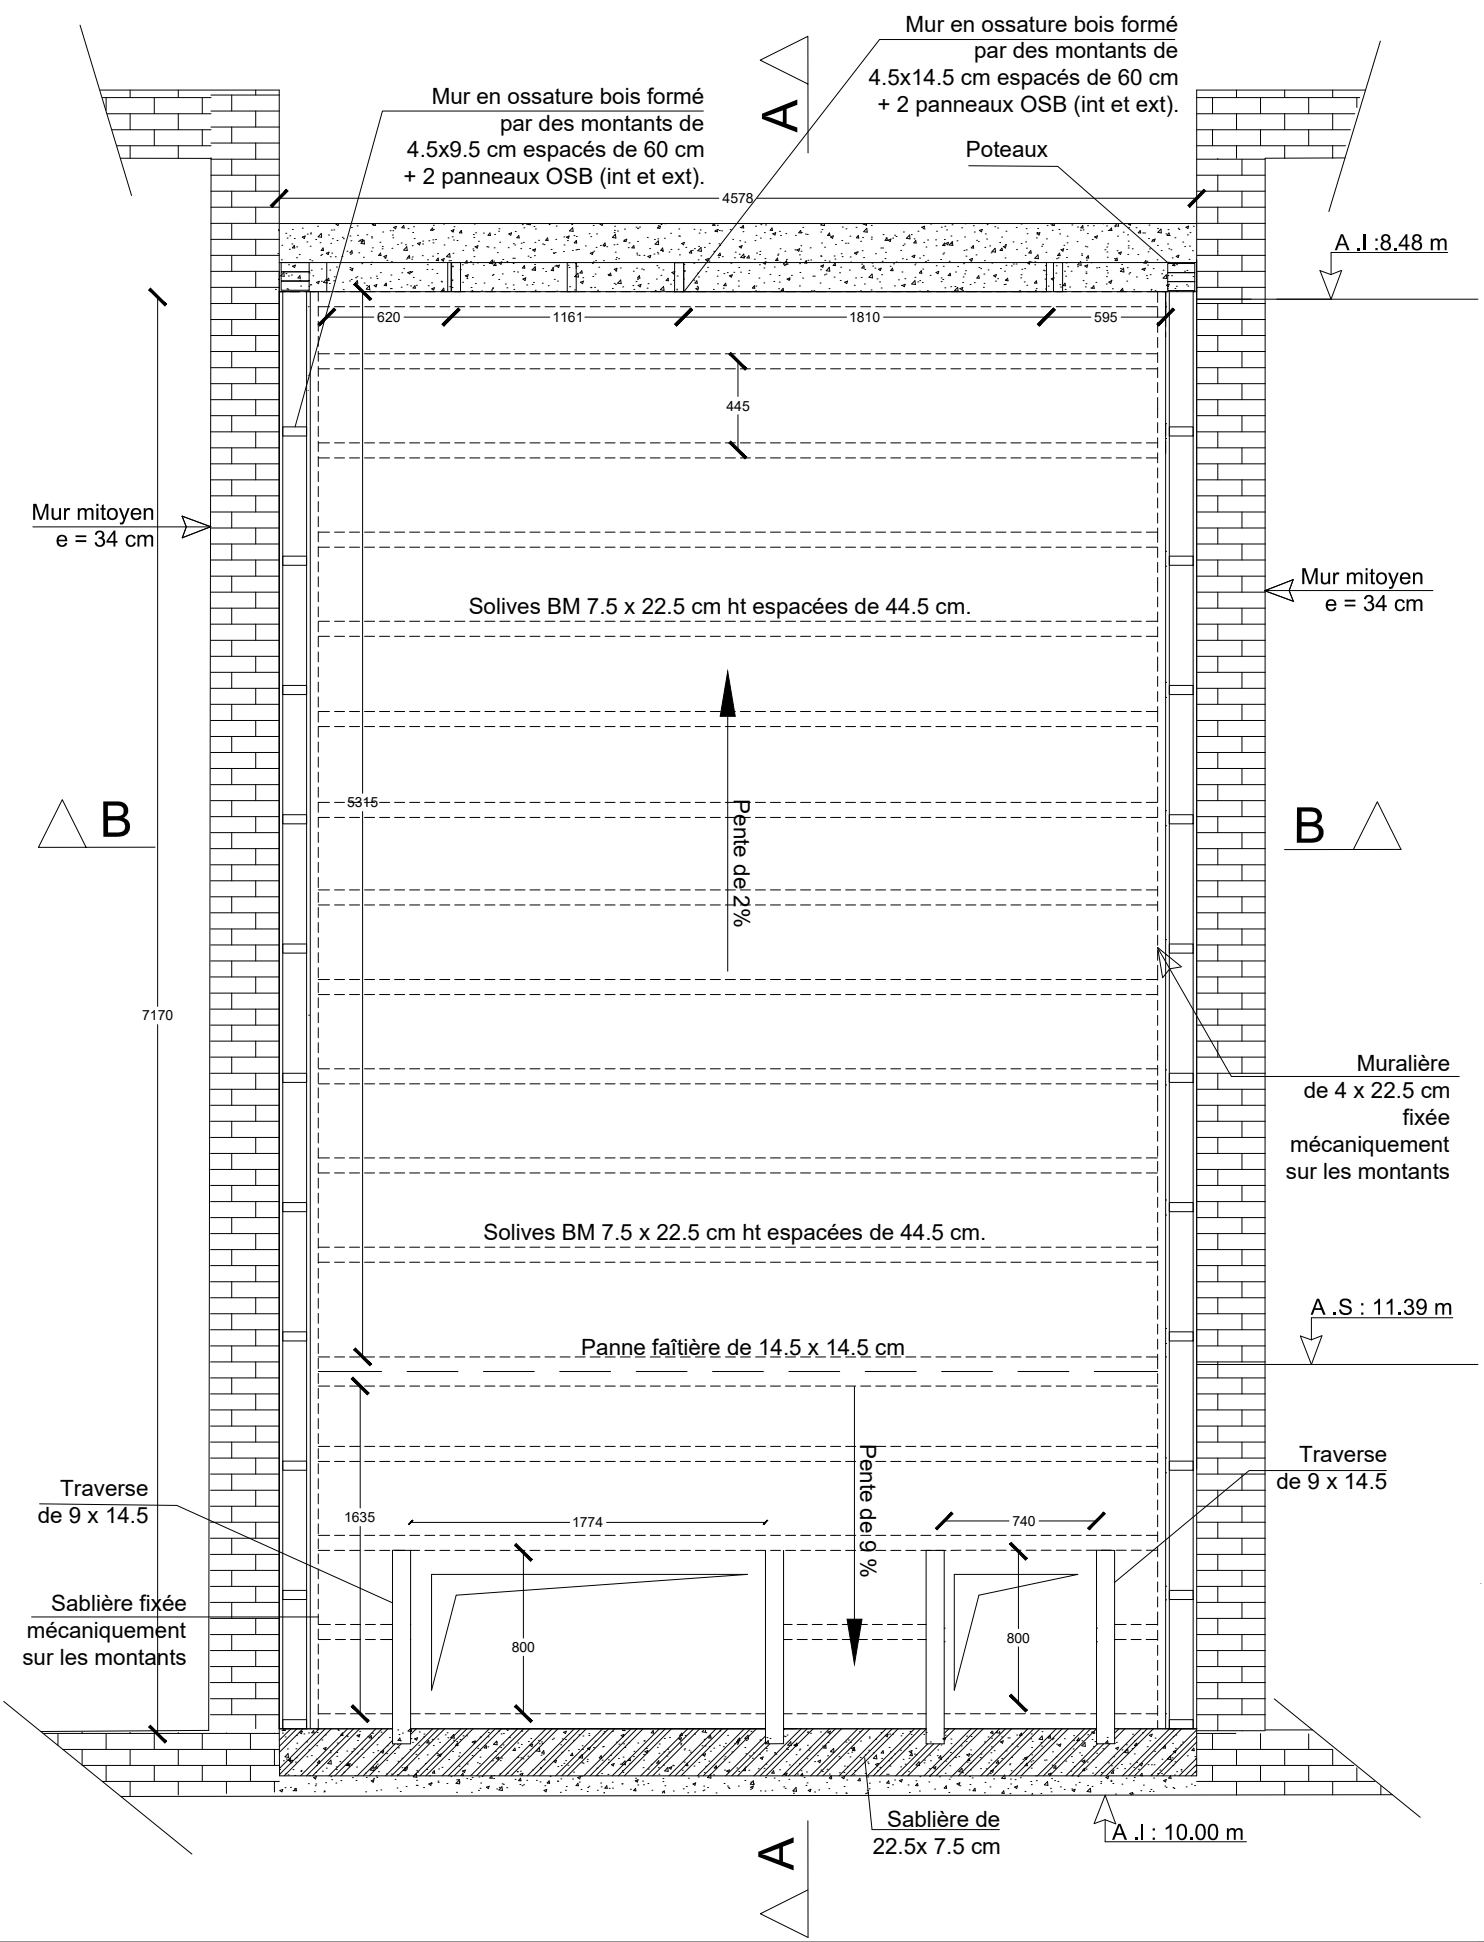



Maîtrise d'Ouvrage :
Mme Joséphine et M Quentin
24,Rue Denis du péage
59800 Lille
Parcelle CK 0034 .

BET STRUCTURE :
J.K.F. STRUCTURE
92 Bd du GLE du Gaulle
59100 Roubaix

Surélévation d'une maison mitoyenne.

Dossier d'Etude Structurelle :
Vue en plan projet
PH R+3 "Sur élevation"

Plan N° : GO 01
Ech : 1/50

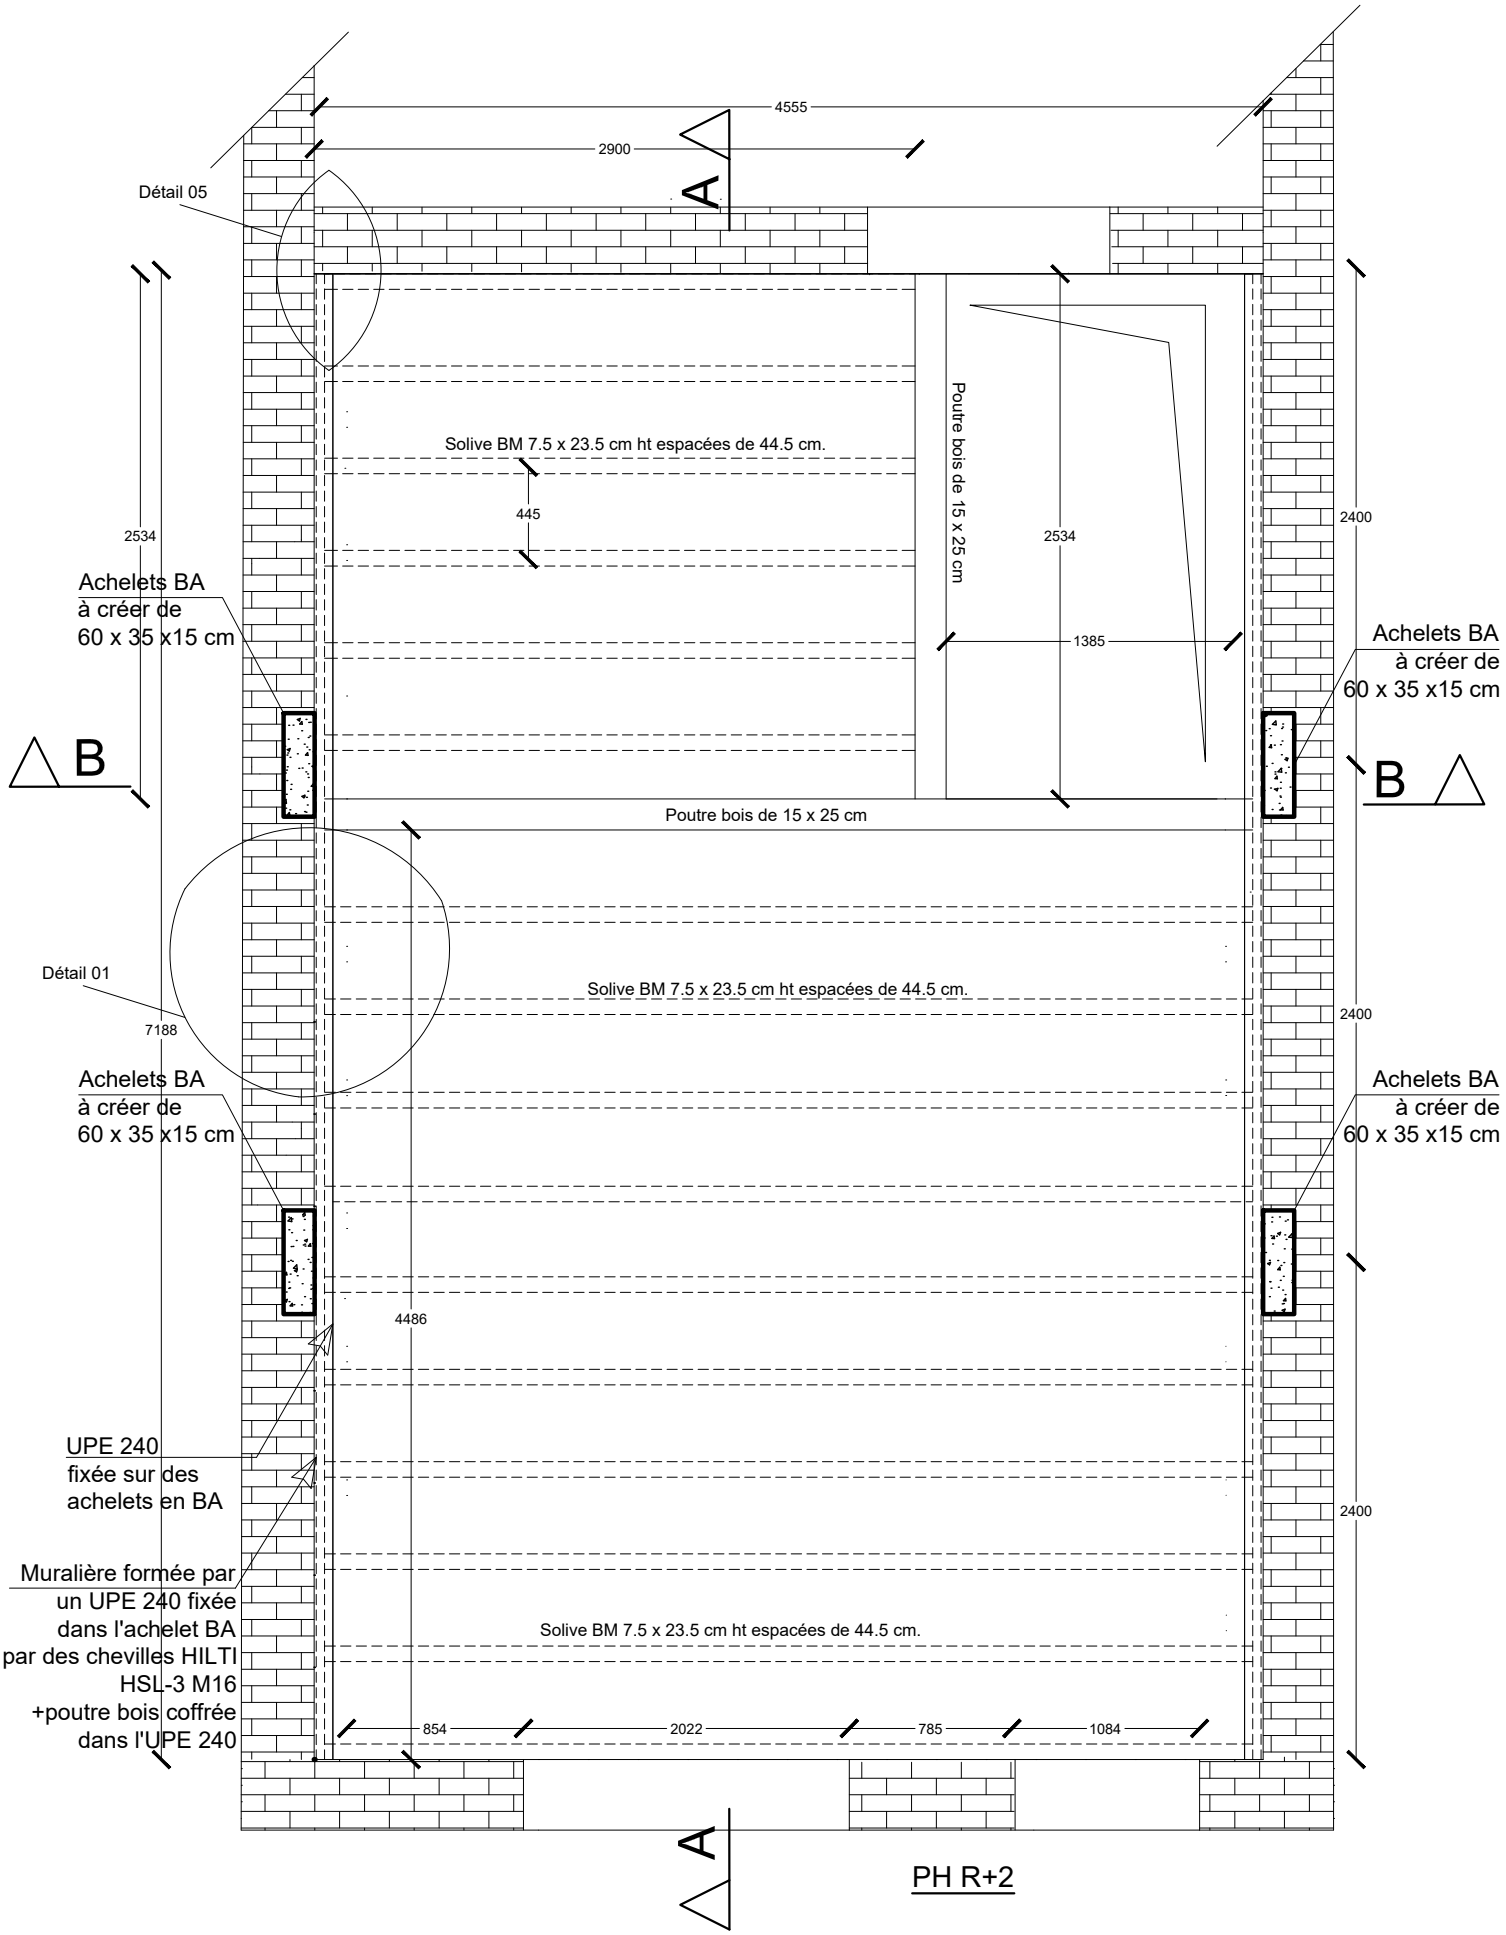

PH R+2


Maîtrise d'Ouvrage :
Mme Joséphine et M Quentin
24,Rue Denis du péage
59800 Lille
Parcelle CK 0034 .

BET STRUCTURE :
J.K.F. STRUCTURE
92 Bd du GLE du Gaulle
59100 Roubaix

Surélévation d'une maison mitoyenne.

Dossier d'Etude Structurelle :
PH R+2

Plan N° : GO 02
Ech : 1/50

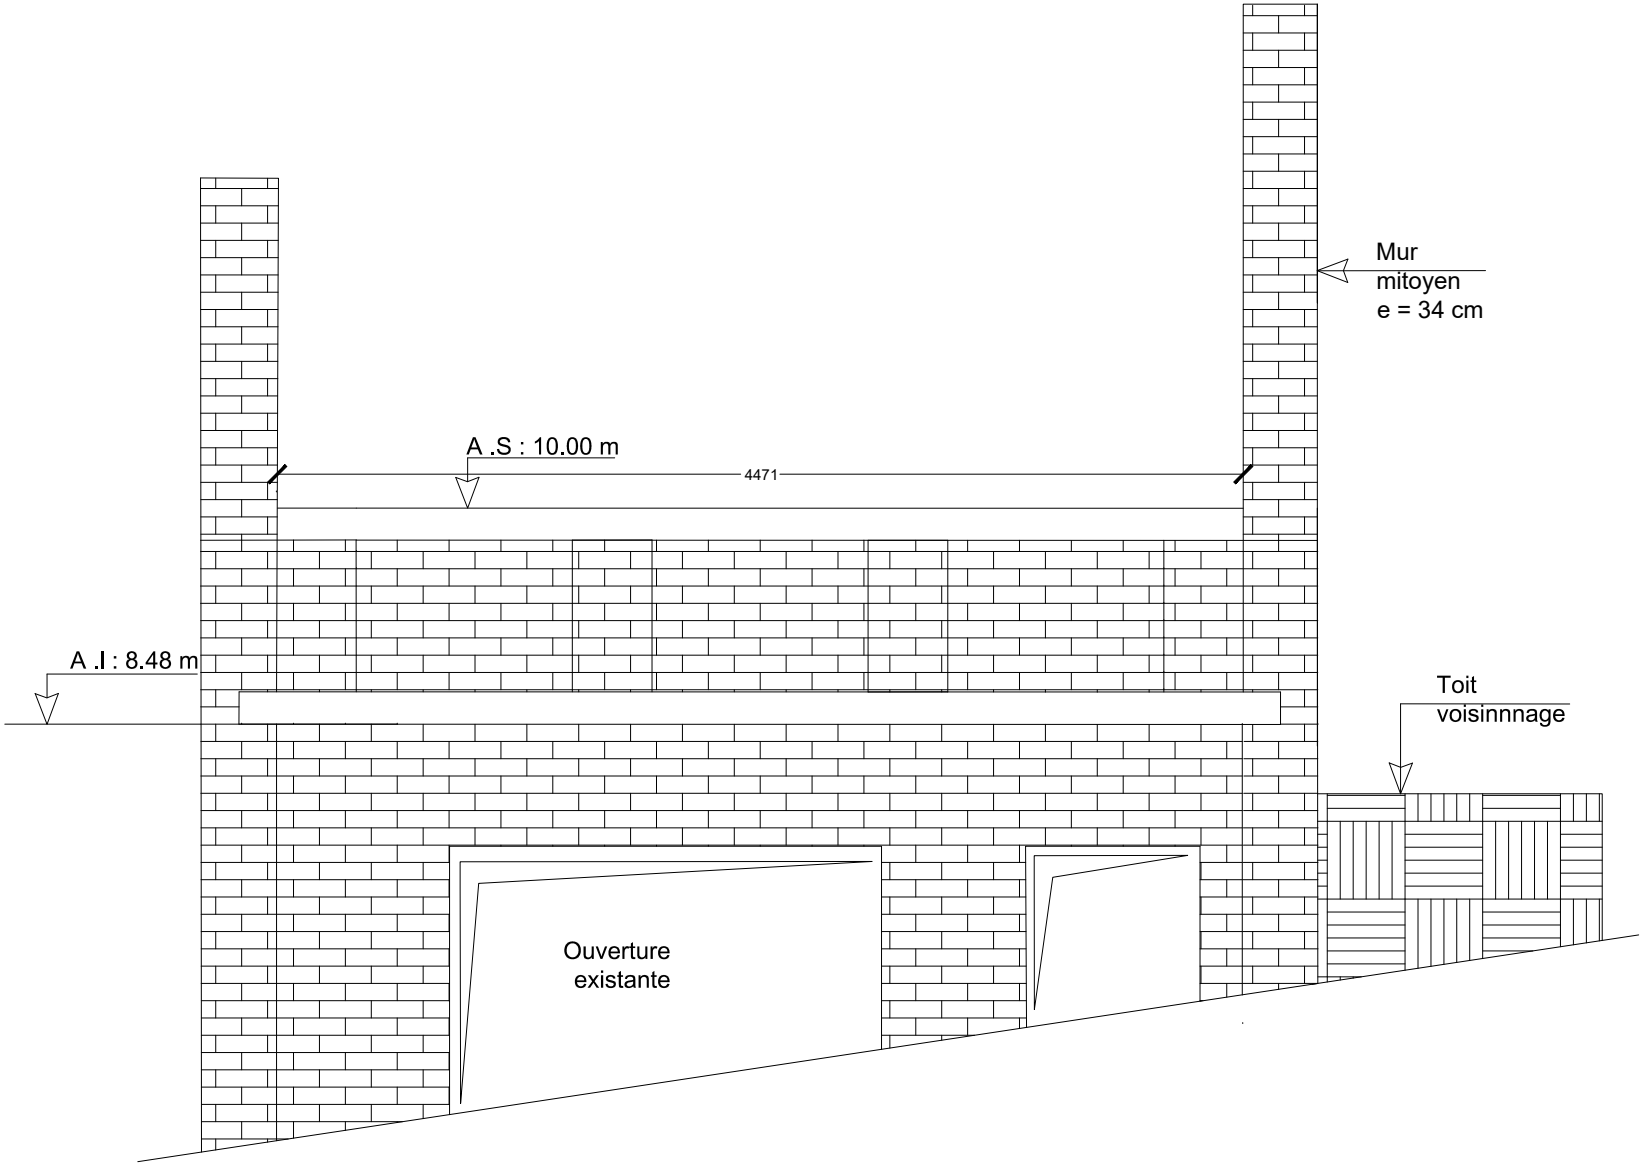

Façade sur rue existante


Maîtrise d'Ouvrage :
Mme Joséphine et M Quentin
24,Rue Denis du péage
59800 Lille
Parcelle CK 0034 .

BET STRUCTURE :
J.K.F. STRUCTURE
92 Bd du GLE du Gaulle
59100 Roubaix

Surélévation d'une maison mitoyenne.

Dossier d'Etude Structurelle :
Façade sur rue existante

Plan N° : GO 03
Ech : 1/35

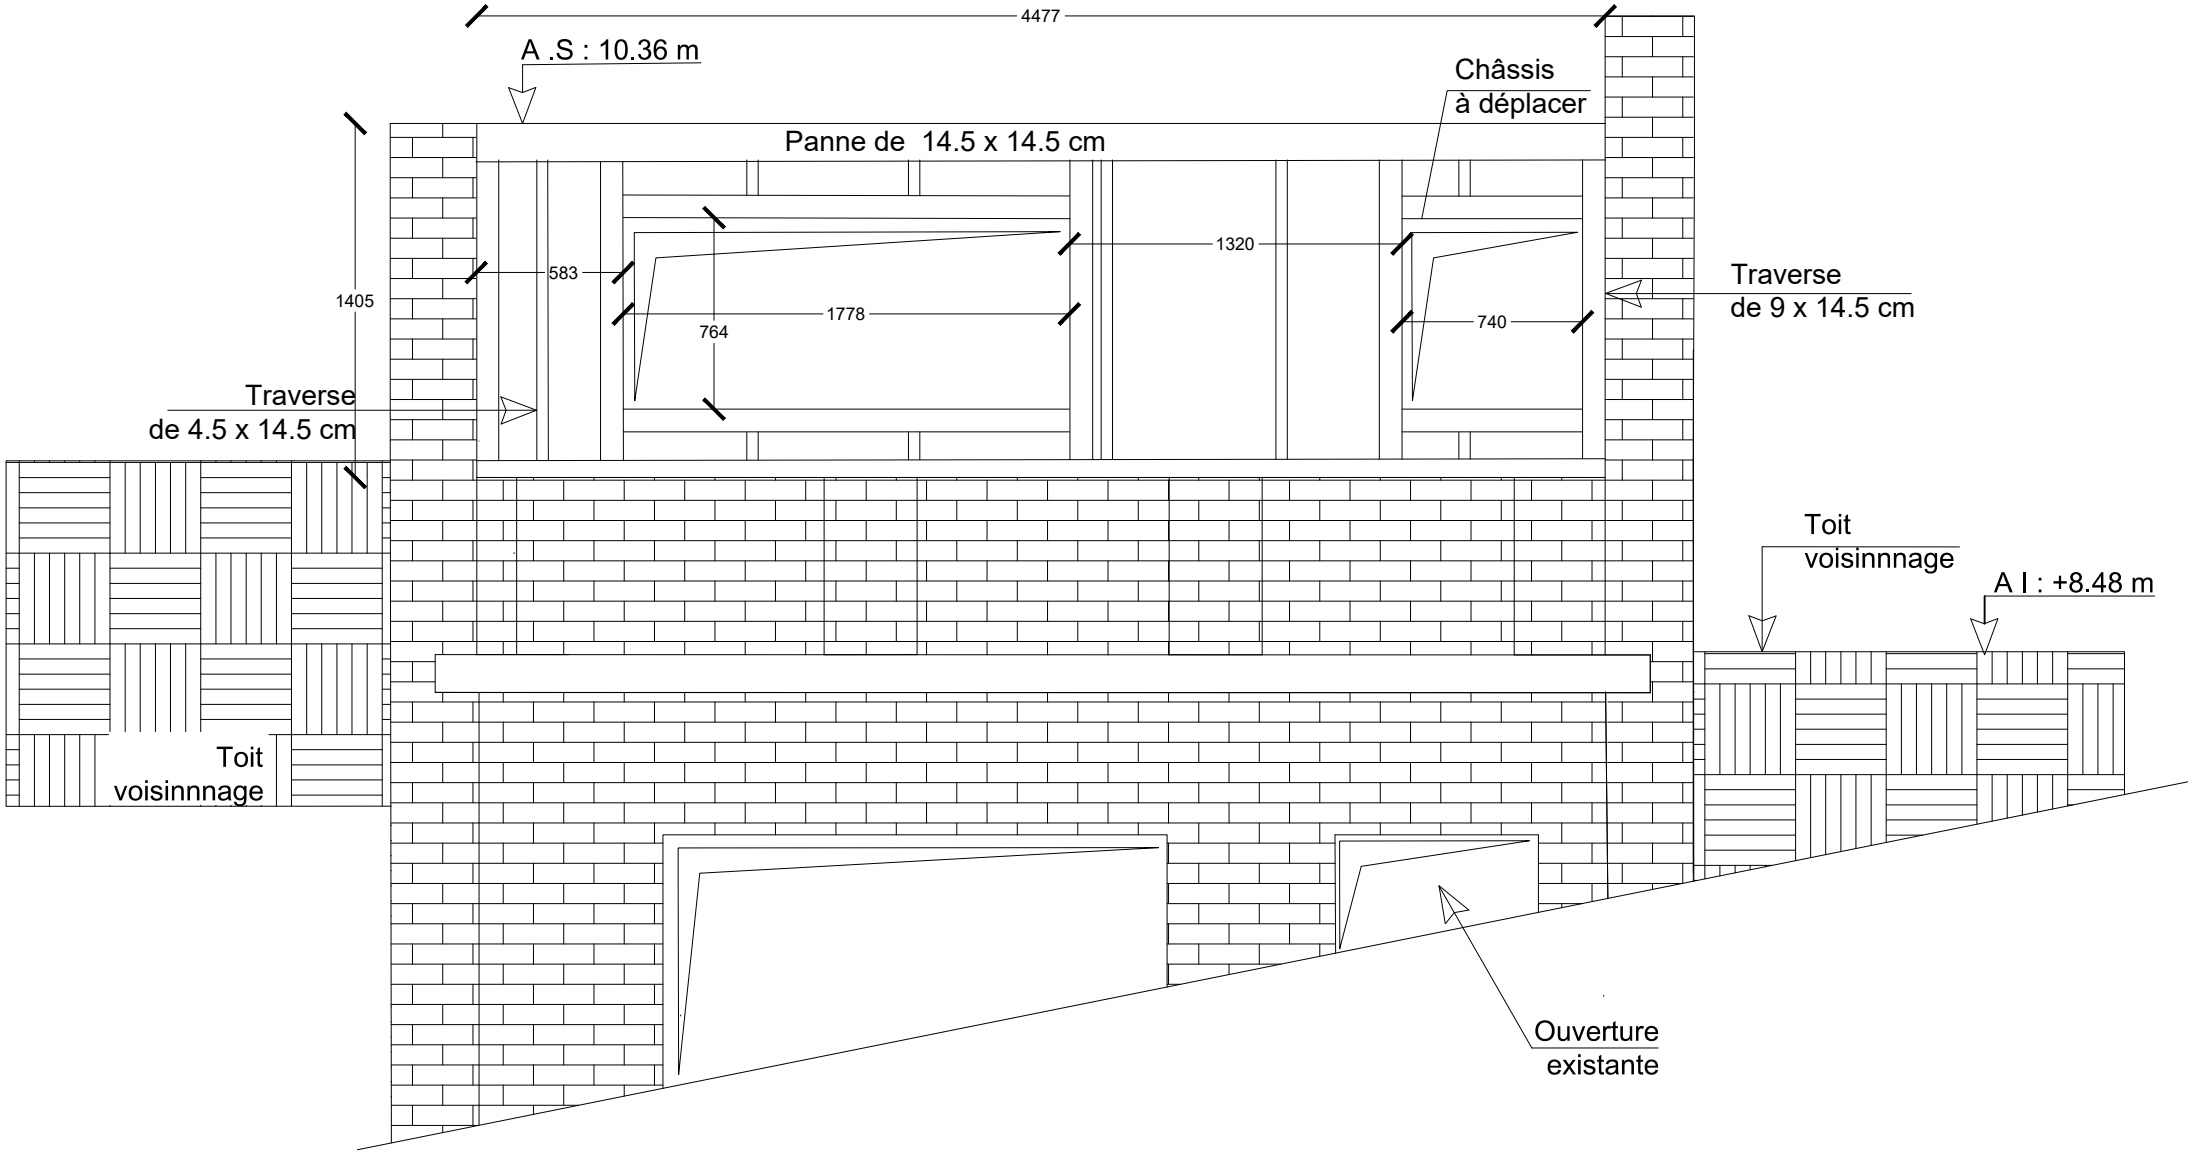

Façade sur rue projet


Maîtrise d'Ouvrage :
Mme Joséphine et M Quentin
24,Rue Denis du péage
59800 Lille
Parcelle CK 0034 .

BET STRUCTURE :
J.K.F. STRUCTURE
92 Bd du GLE du Gaulle
59100 Roubaix

Surélévation d'une maison mitoyenne.

Dossier d'Etude Structurelle :
Façade sur rue projet

Plan N° : GO 04
Ech :1/30

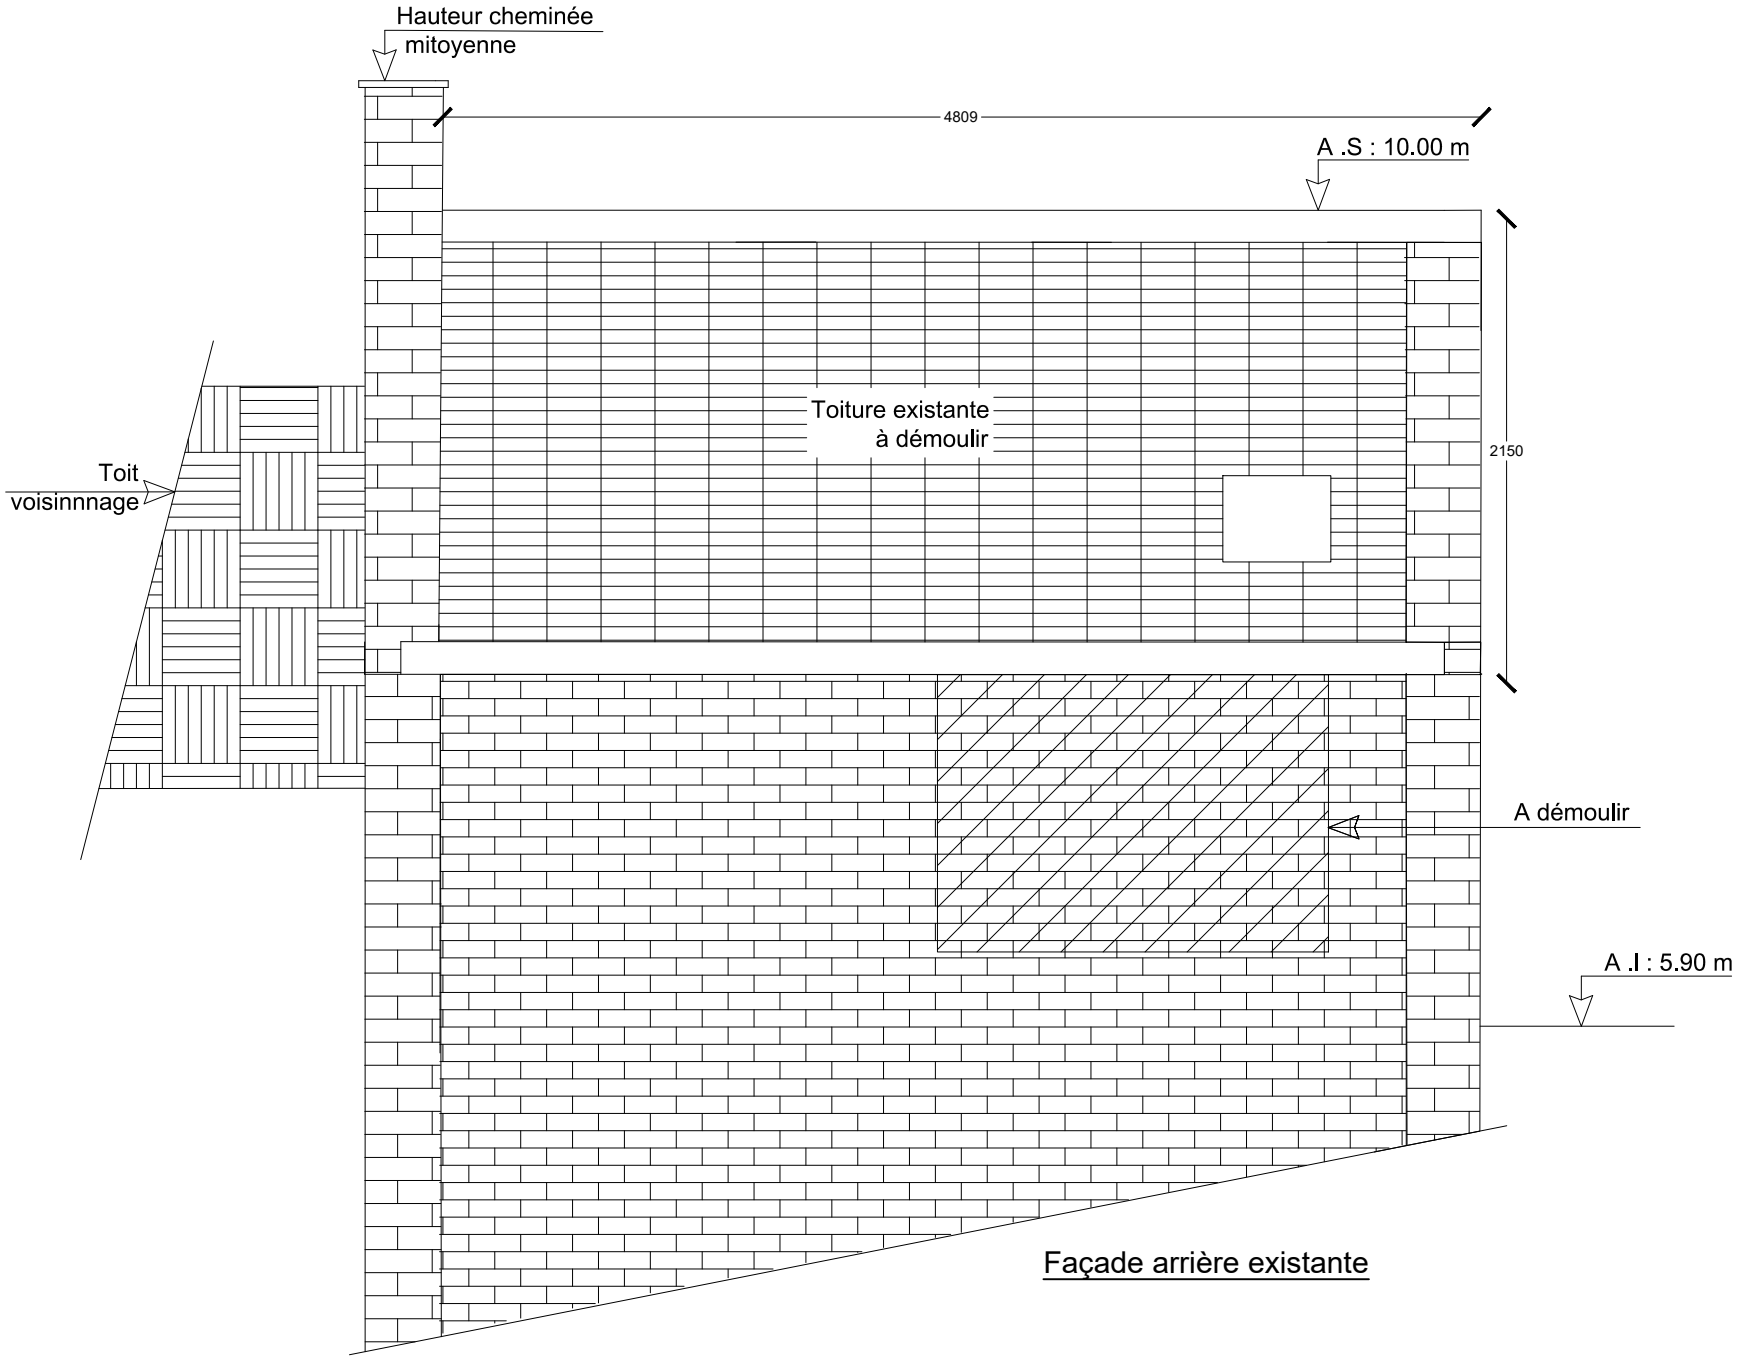

Façade arrière existante


Maîtrise d'Ouvrage :
Mme Joséphine et M Quentin
24,Rue Denis du péage
59800 Lille
Parcelle CK 0034 .

BET STRUCTURE :
J.K.F. STRUCTURE
92 Bd du GLE du Gaulle
59100 Roubaix

Surélévation d'une maison mitoyenne.

Dossier d'Etude Structurelle :
Façade arrière existante

Plan N° : GO 05
Ech : 1/35

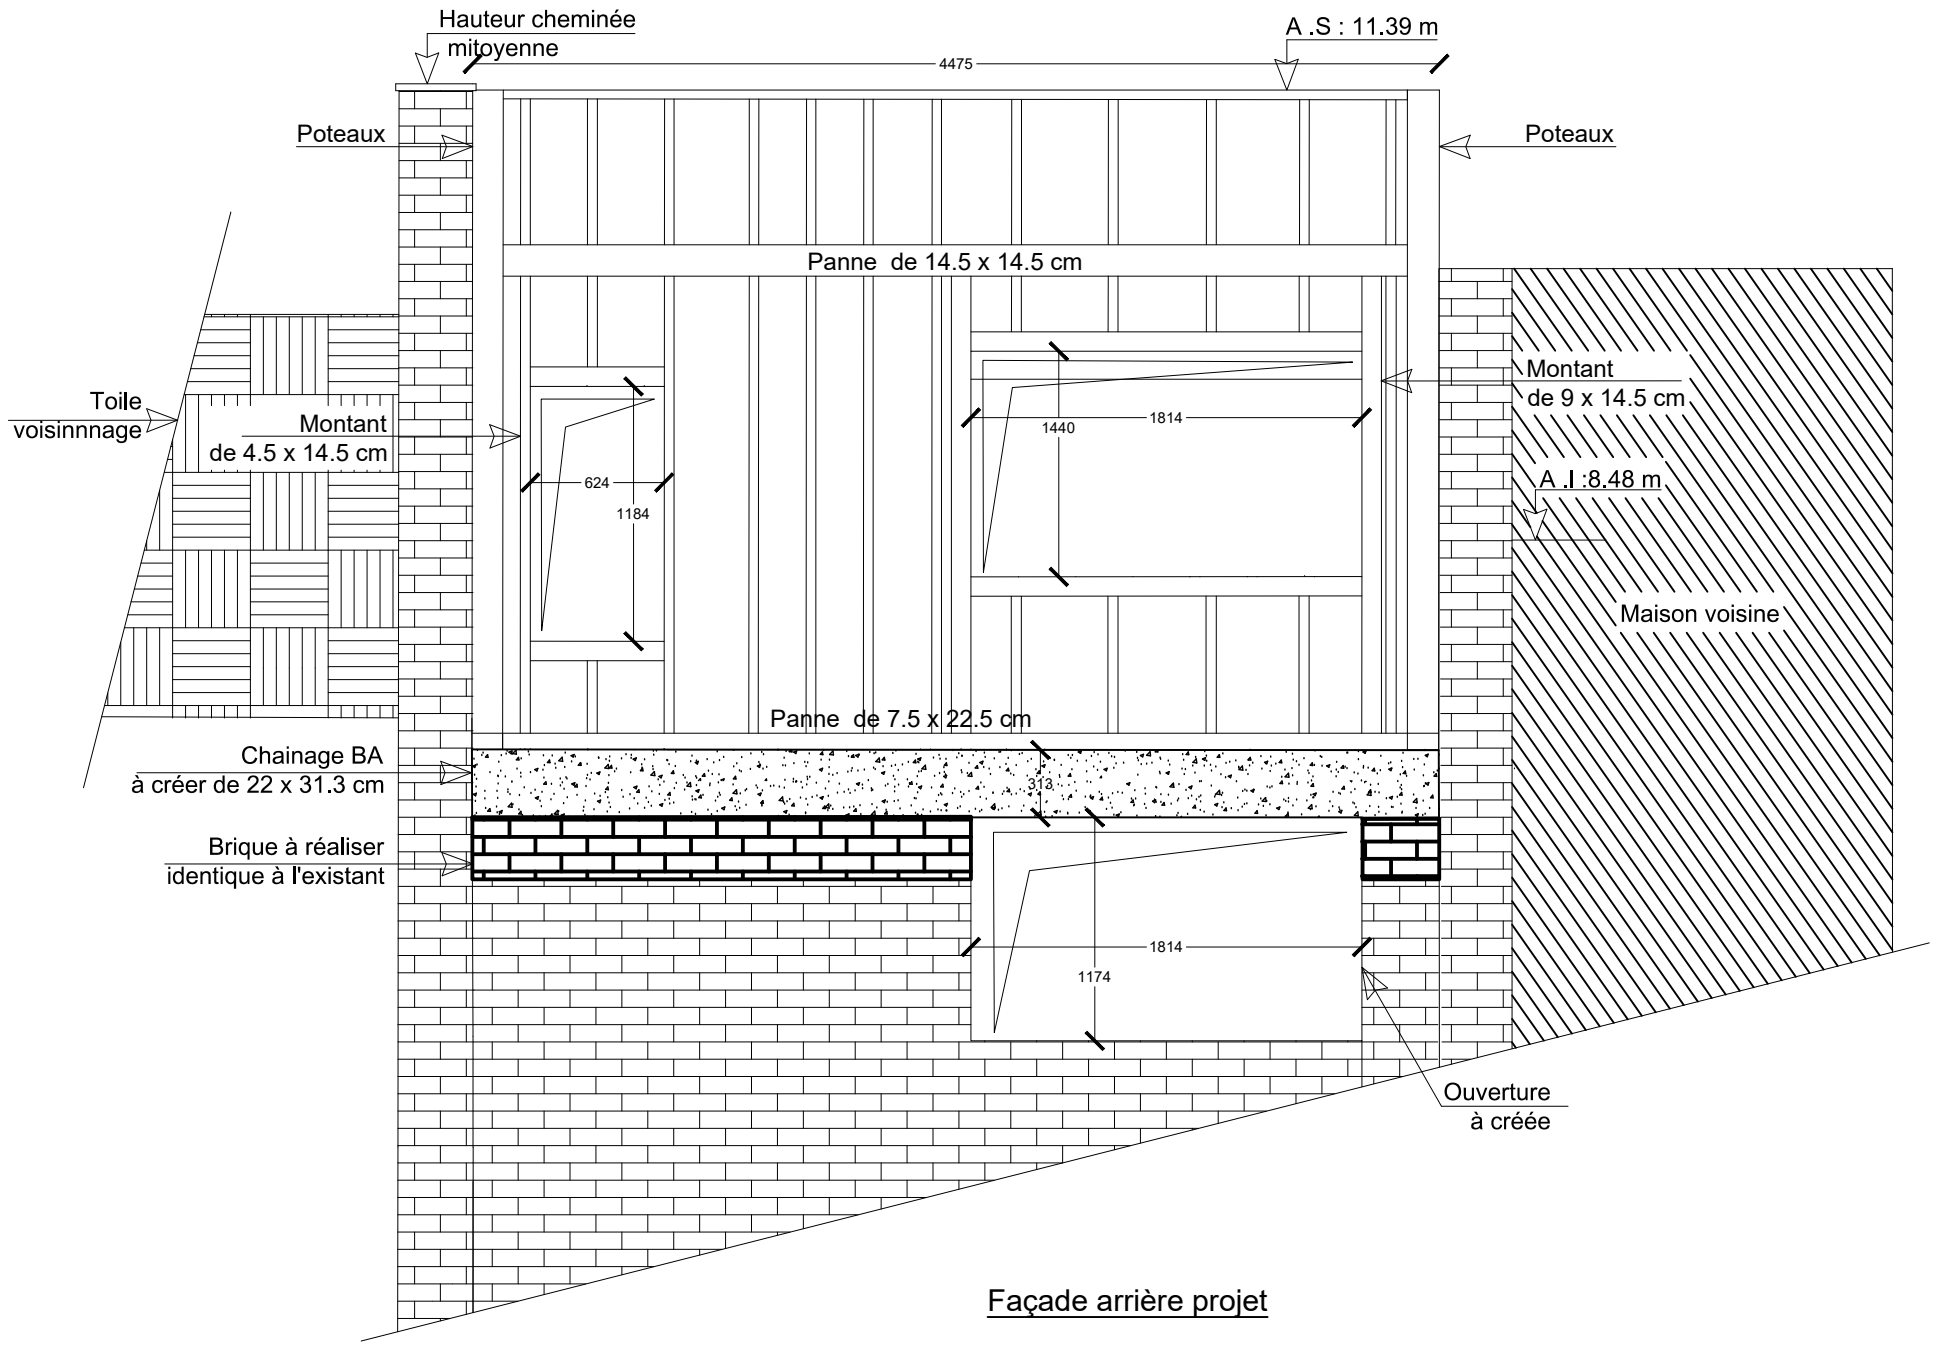

Façade arrière projet


Maîtrise d'Ouvrage :
Mme Joséphine et M Quentin
24,Rue Denis du péage
59800 Lille
Parcelle CK 0034 .

BET STRUCTURE :
J.K.F. STRUCTURE
92 Bd du GLE du Gaulle
59100 Roubaix

Surélévation d'une maison mitoyenne.

Dossier d'Etude Structurelle :
Façade arrière projet

Plan N° : GO 06
Ech : 1/35

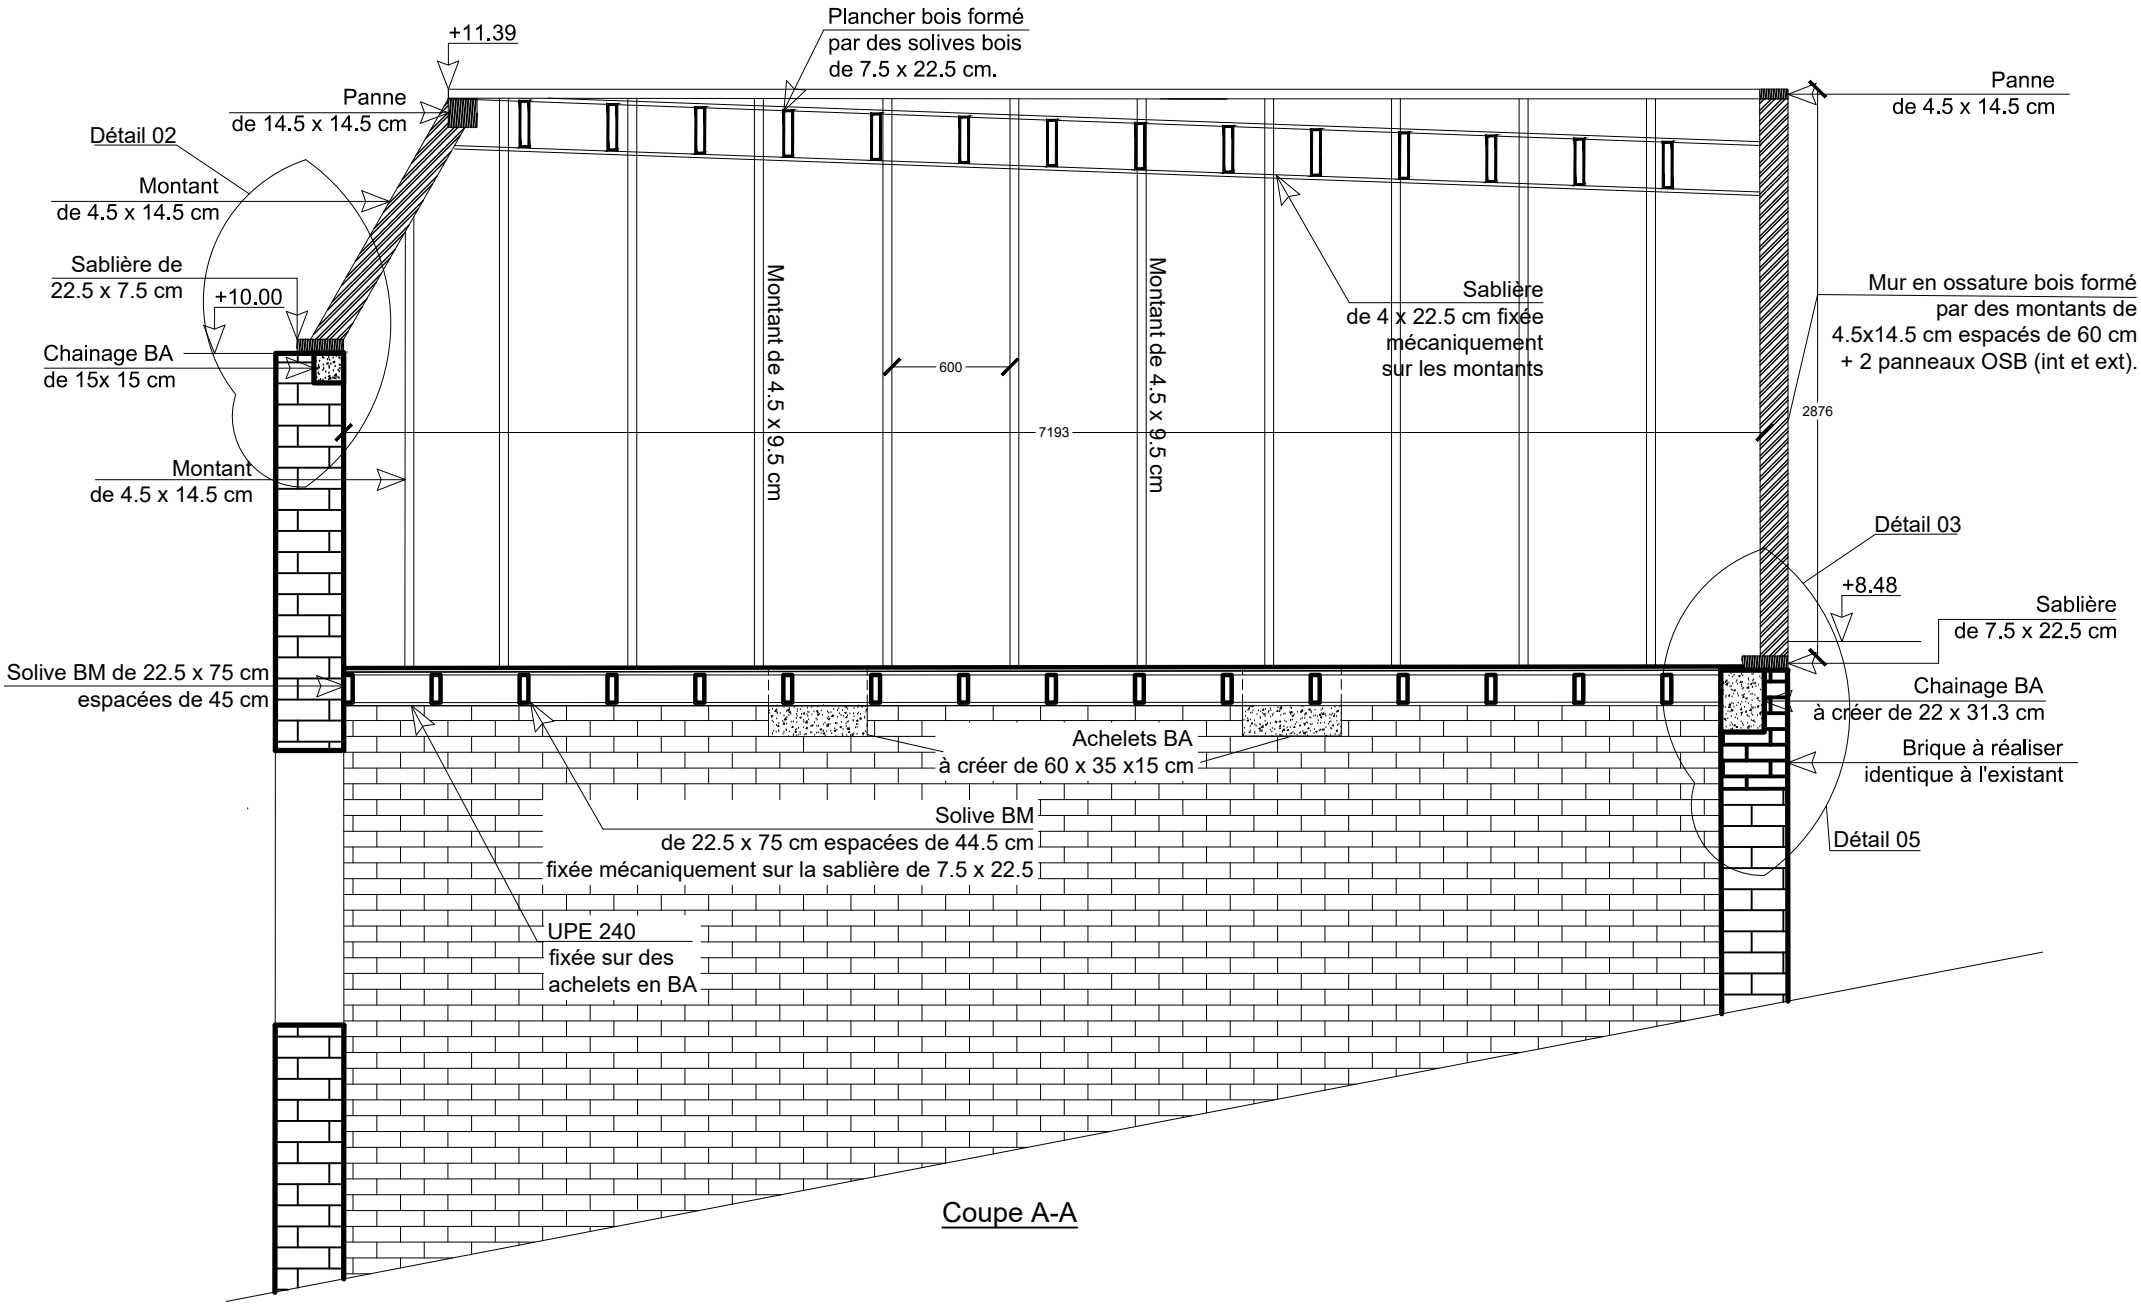

Coupe A-A


Maîtrise d'Ouvrage :
Mme Joséphine et M Quentin
24,Rue Denis du péage
59800 Lille,Parcelle CK 0034 .

BET STRUCTURE :
J.K.F. STRUCTURE
92 Bd du GLE du Gaulle
59100 Roubaix

Surélévation d'une maison mitoyenne.

Dossier d'Etude Structurelle :
Coupe A-A

Plan N° : GO 07
Ech : 1/35

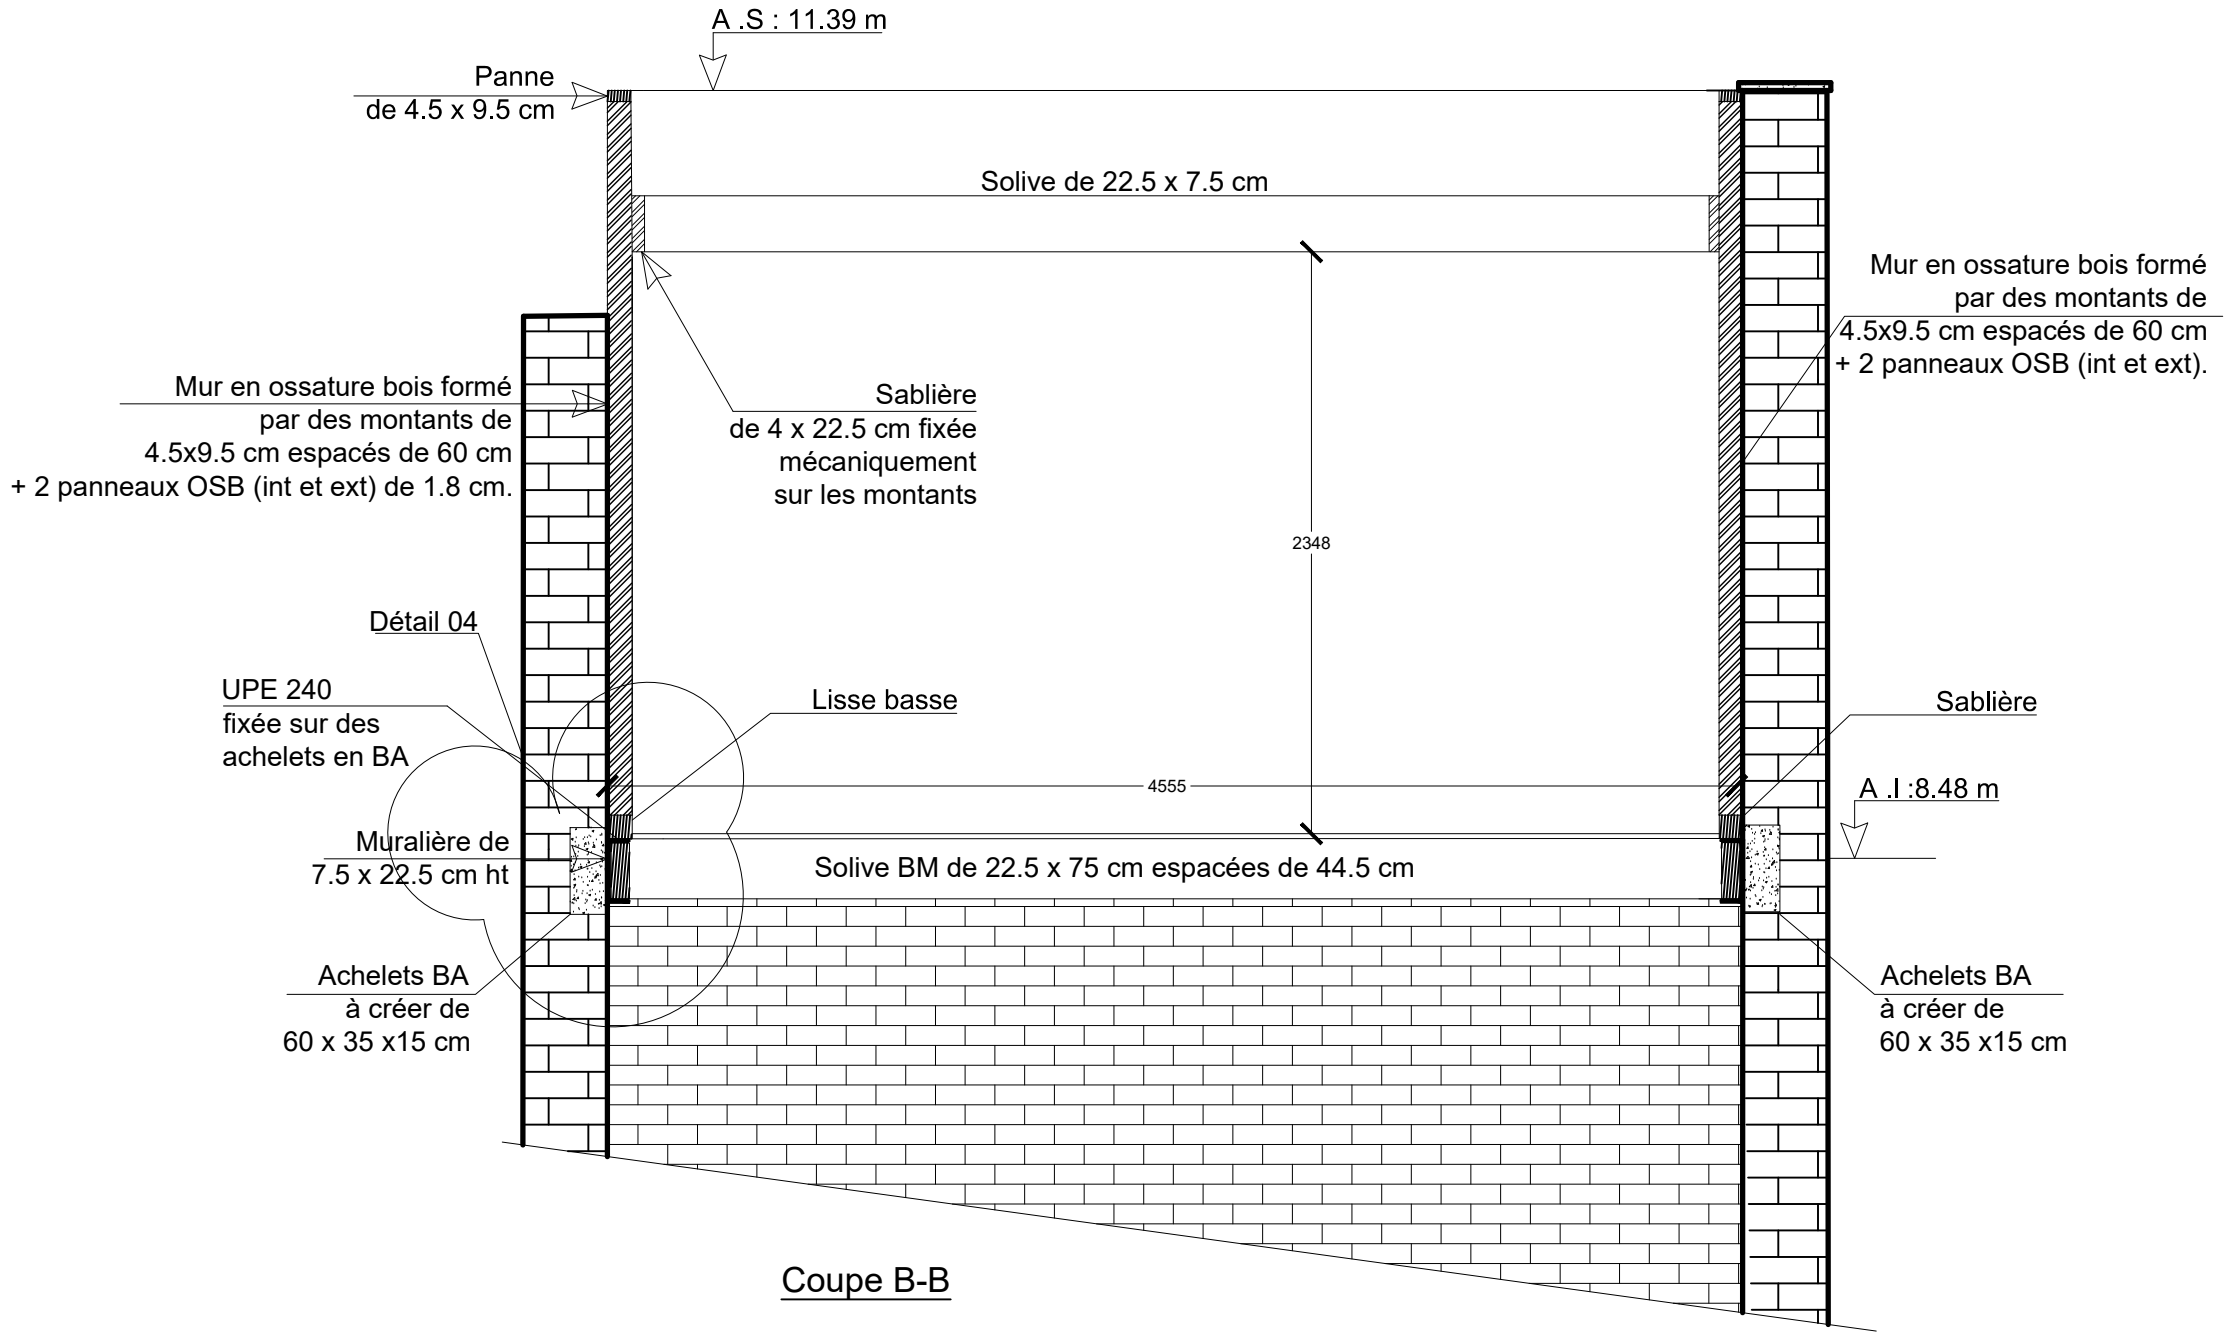

Coupe B-B


Maîtrise d'Ouvrage :
Mme Joséphine et M Quentin
24,Rue Denis du péage
59800 Lille
Parcelle CK 0034 .

BET STRUCTURE :
J.K.F. STRUCTURE
92 Bd du GLE du Gaulle
59100 Roubaix


Surélévation d'une maison mitoyenne.

Dossier d'Etude Structurelle :
Coupe B-B

Plan N° : GO 08
Ech : 1/30

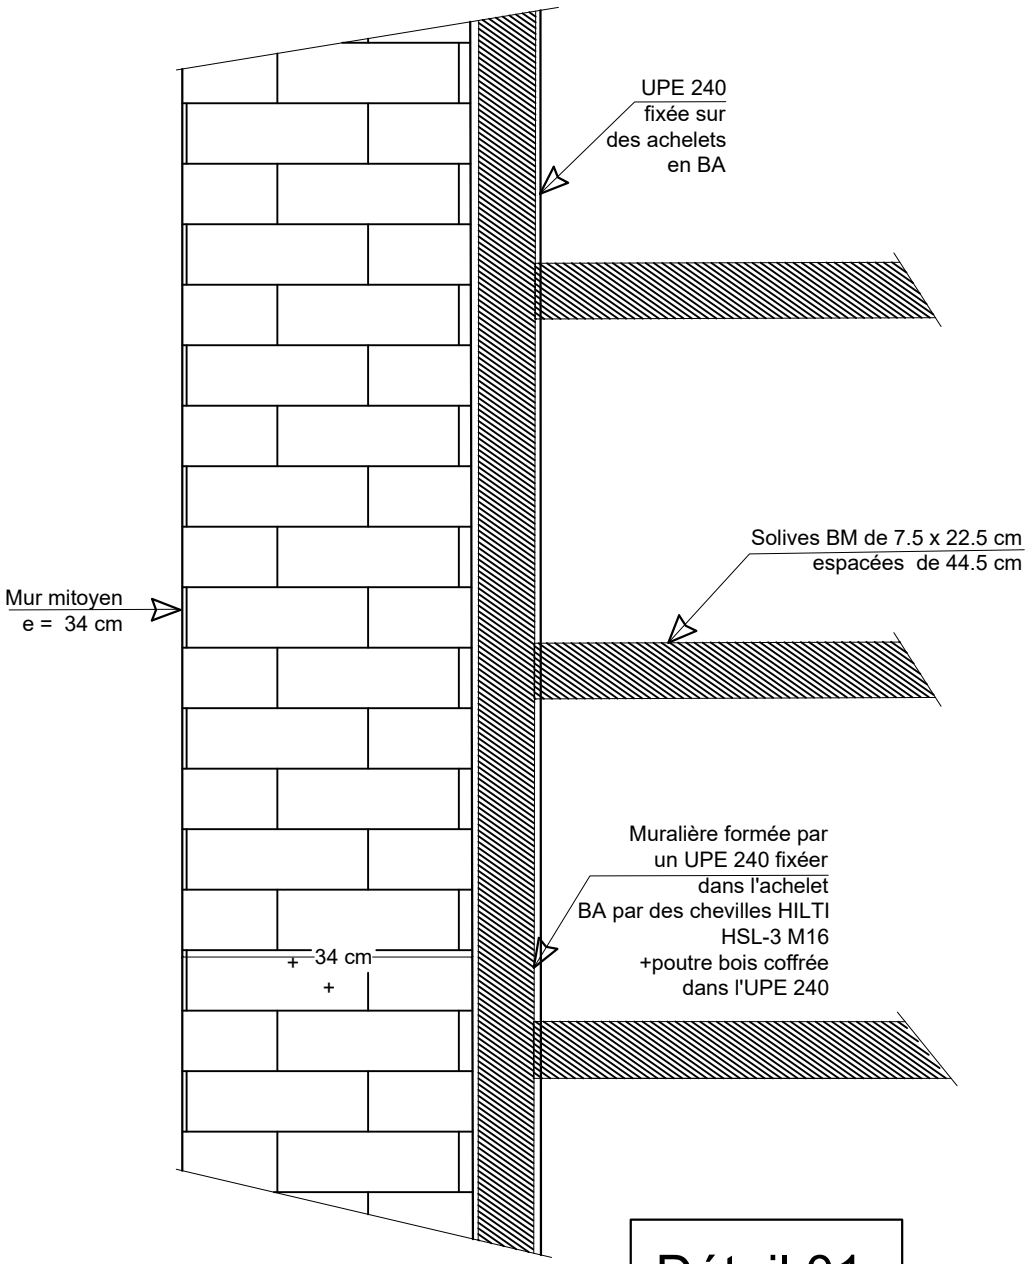

Détail 01

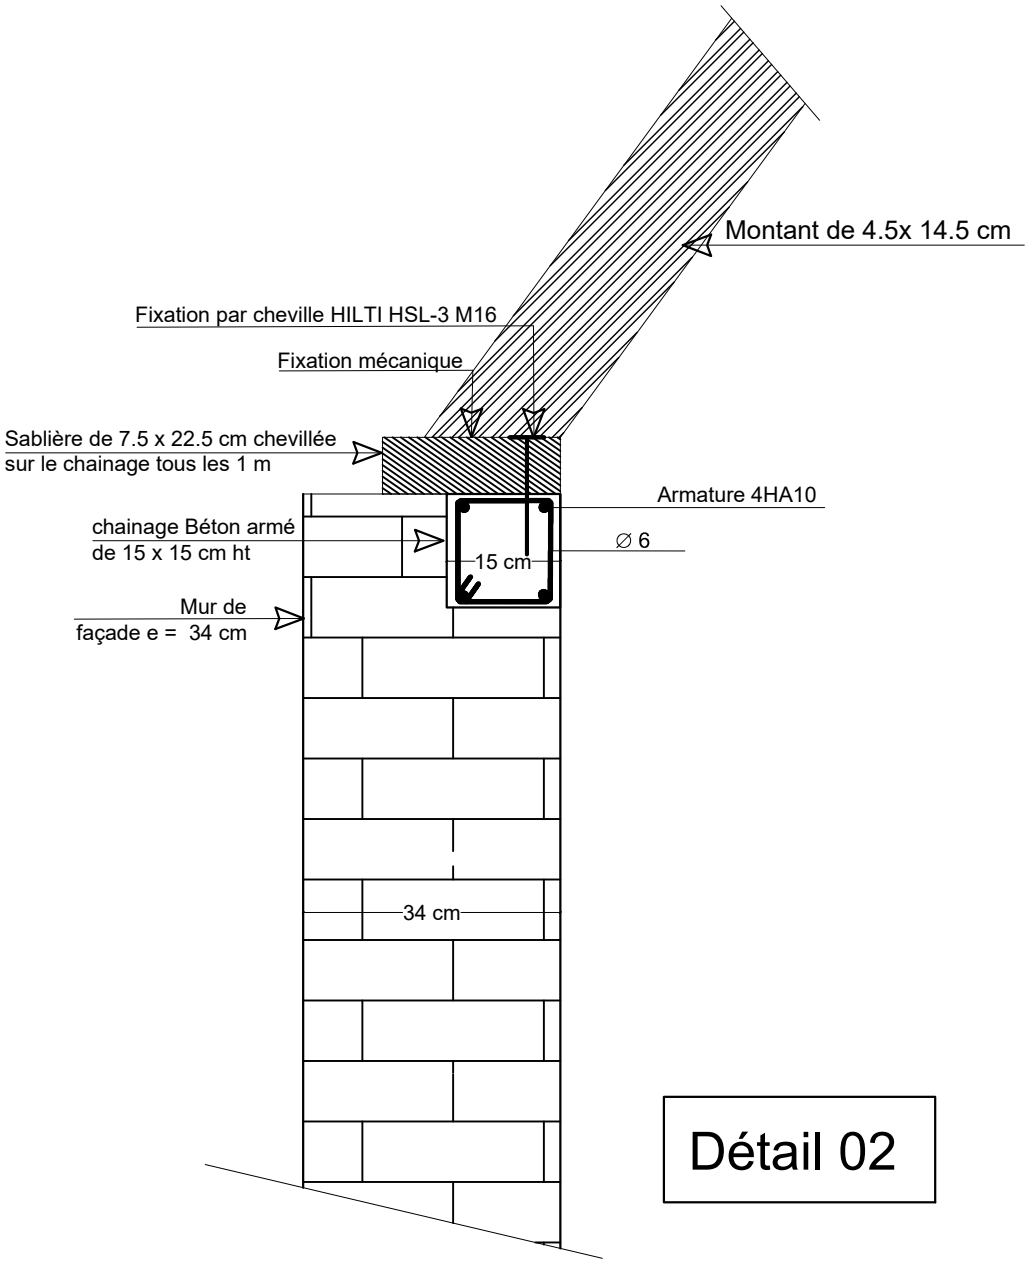

Détail 02


Maîtrise d'Ouvrage :
Mme Joséphine et M Quentin
24,Rue Denis du péage
59800 Lille,Parcelle CK 0034 .

BET STRUCTURE :
J.K.F. STRUCTURE
92 Bd du GLE du Gaulle
59100 Roubaix


Surélévation d'une maison mitoyenne.

Dossier d'Etude Structurelle :
Détail 01/ Détail 02

Plan N° : GO 09
Ech : 1/100

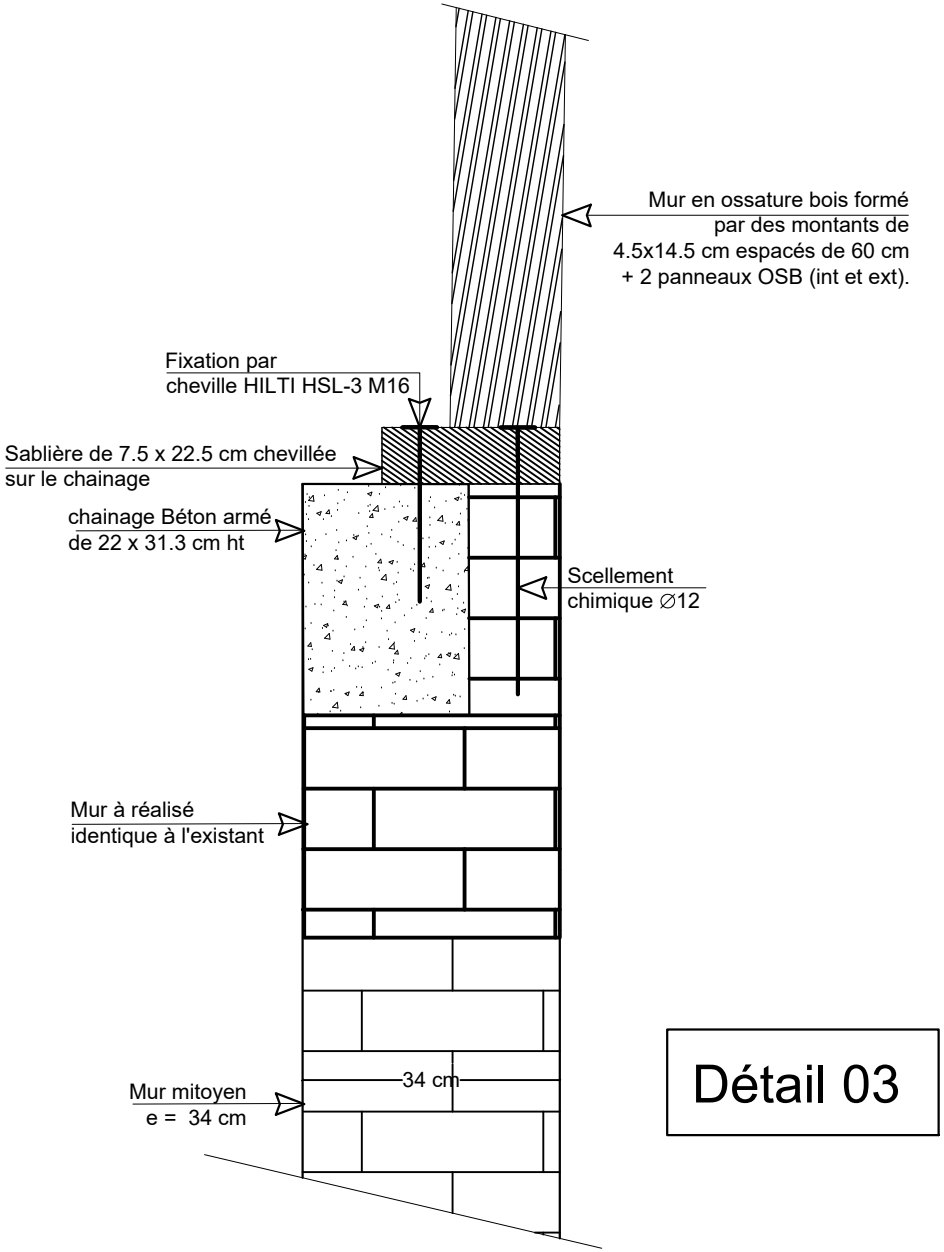

Détail 03

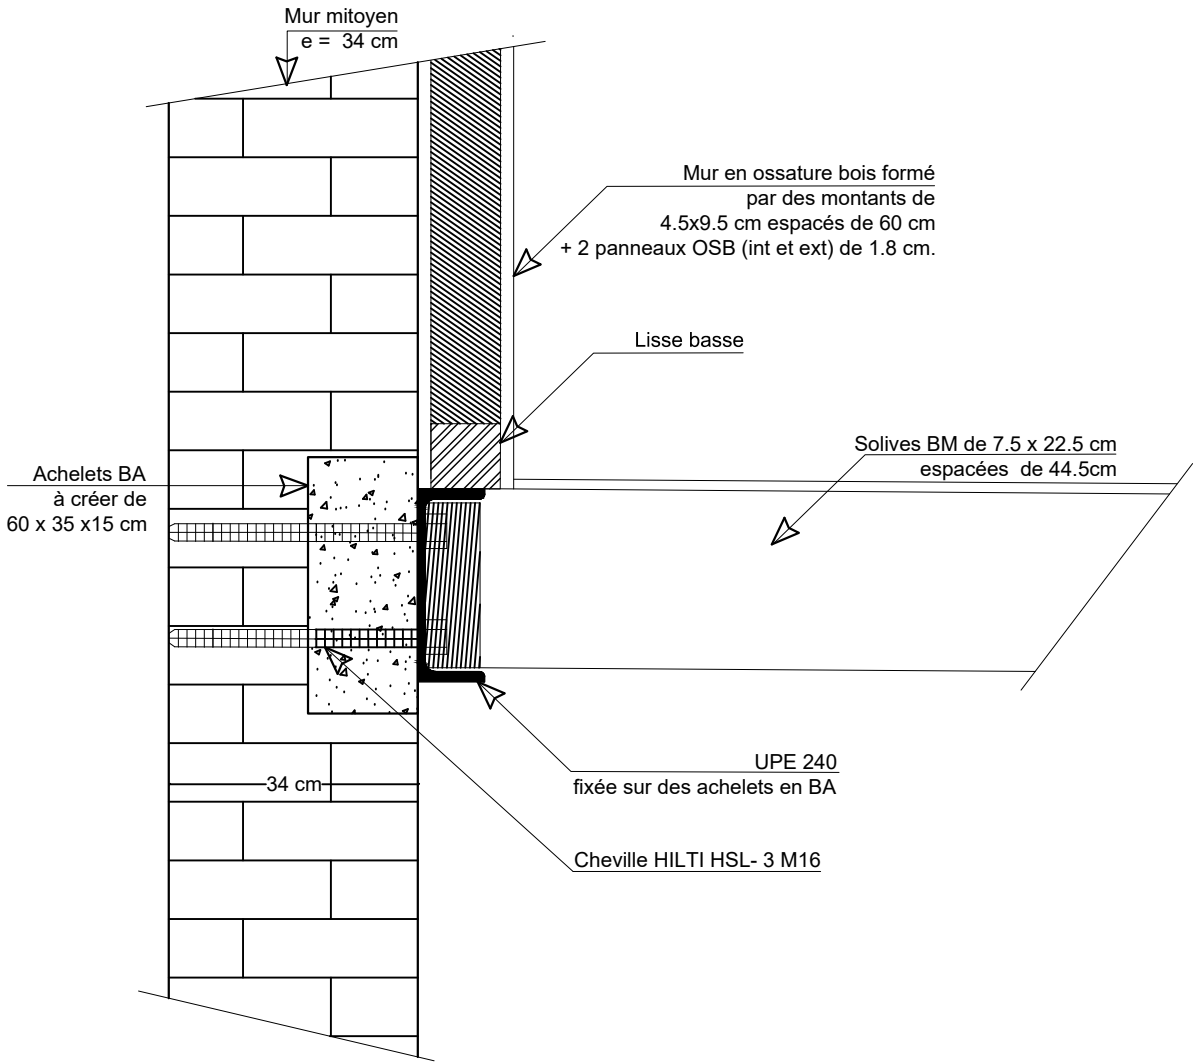

Détail 04


Maîtrise d'Ouvrage :
Mme Joséphine et M Quentin
24,Rue Denis du péage
59800 Lille,Parcelle CK 0034 .

BET STRUCTURE :
J.K.F. STRUCTURE
92 Bd du GLE du Gaulle
59100 Roubaix

Surélévation d'une maison mitoyenne.

Dossier d'Etude Structurelle :
Détail 03/ Détail 04

Plan N° : GO 10
Ech : 1/100

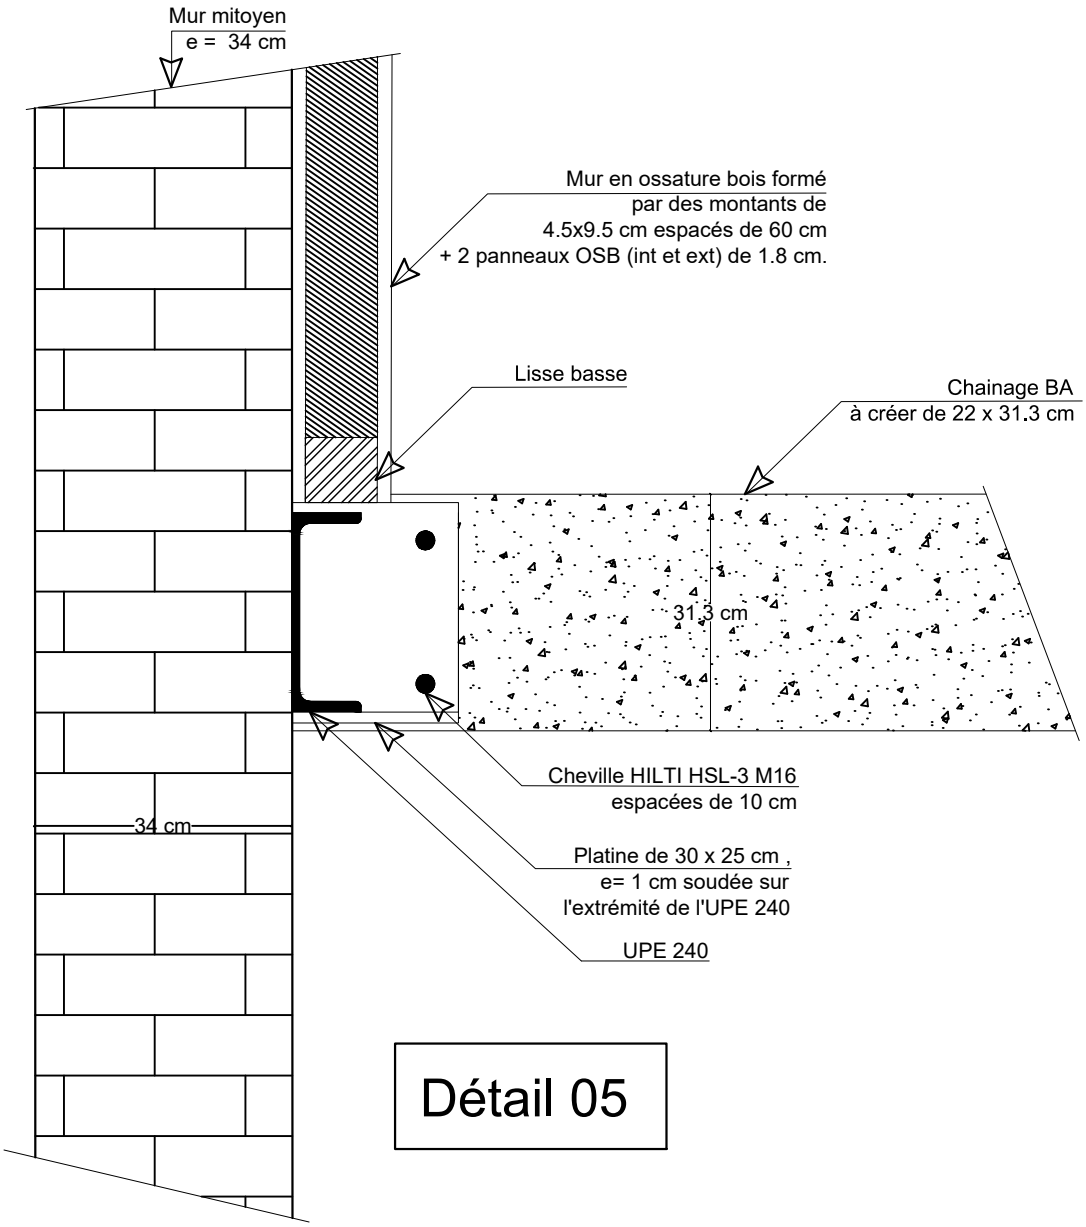

Détail 05

Maîtrise d'Ouvrage :
Mme Joséphine et M Quentin
24,Rue Denis du péage
59800 Lille,Parcelle CK 0034 .

BET STRUCTURE :
J.K.F. STRUCTURE
92 Bd du GLE du Gaulle
59100 Roubaix

Surélévation d'une maison mitoyenne.

Dossier d'Etude Structurelle :

Détail 05

Plan N° : GO 11

Ech : 1/100