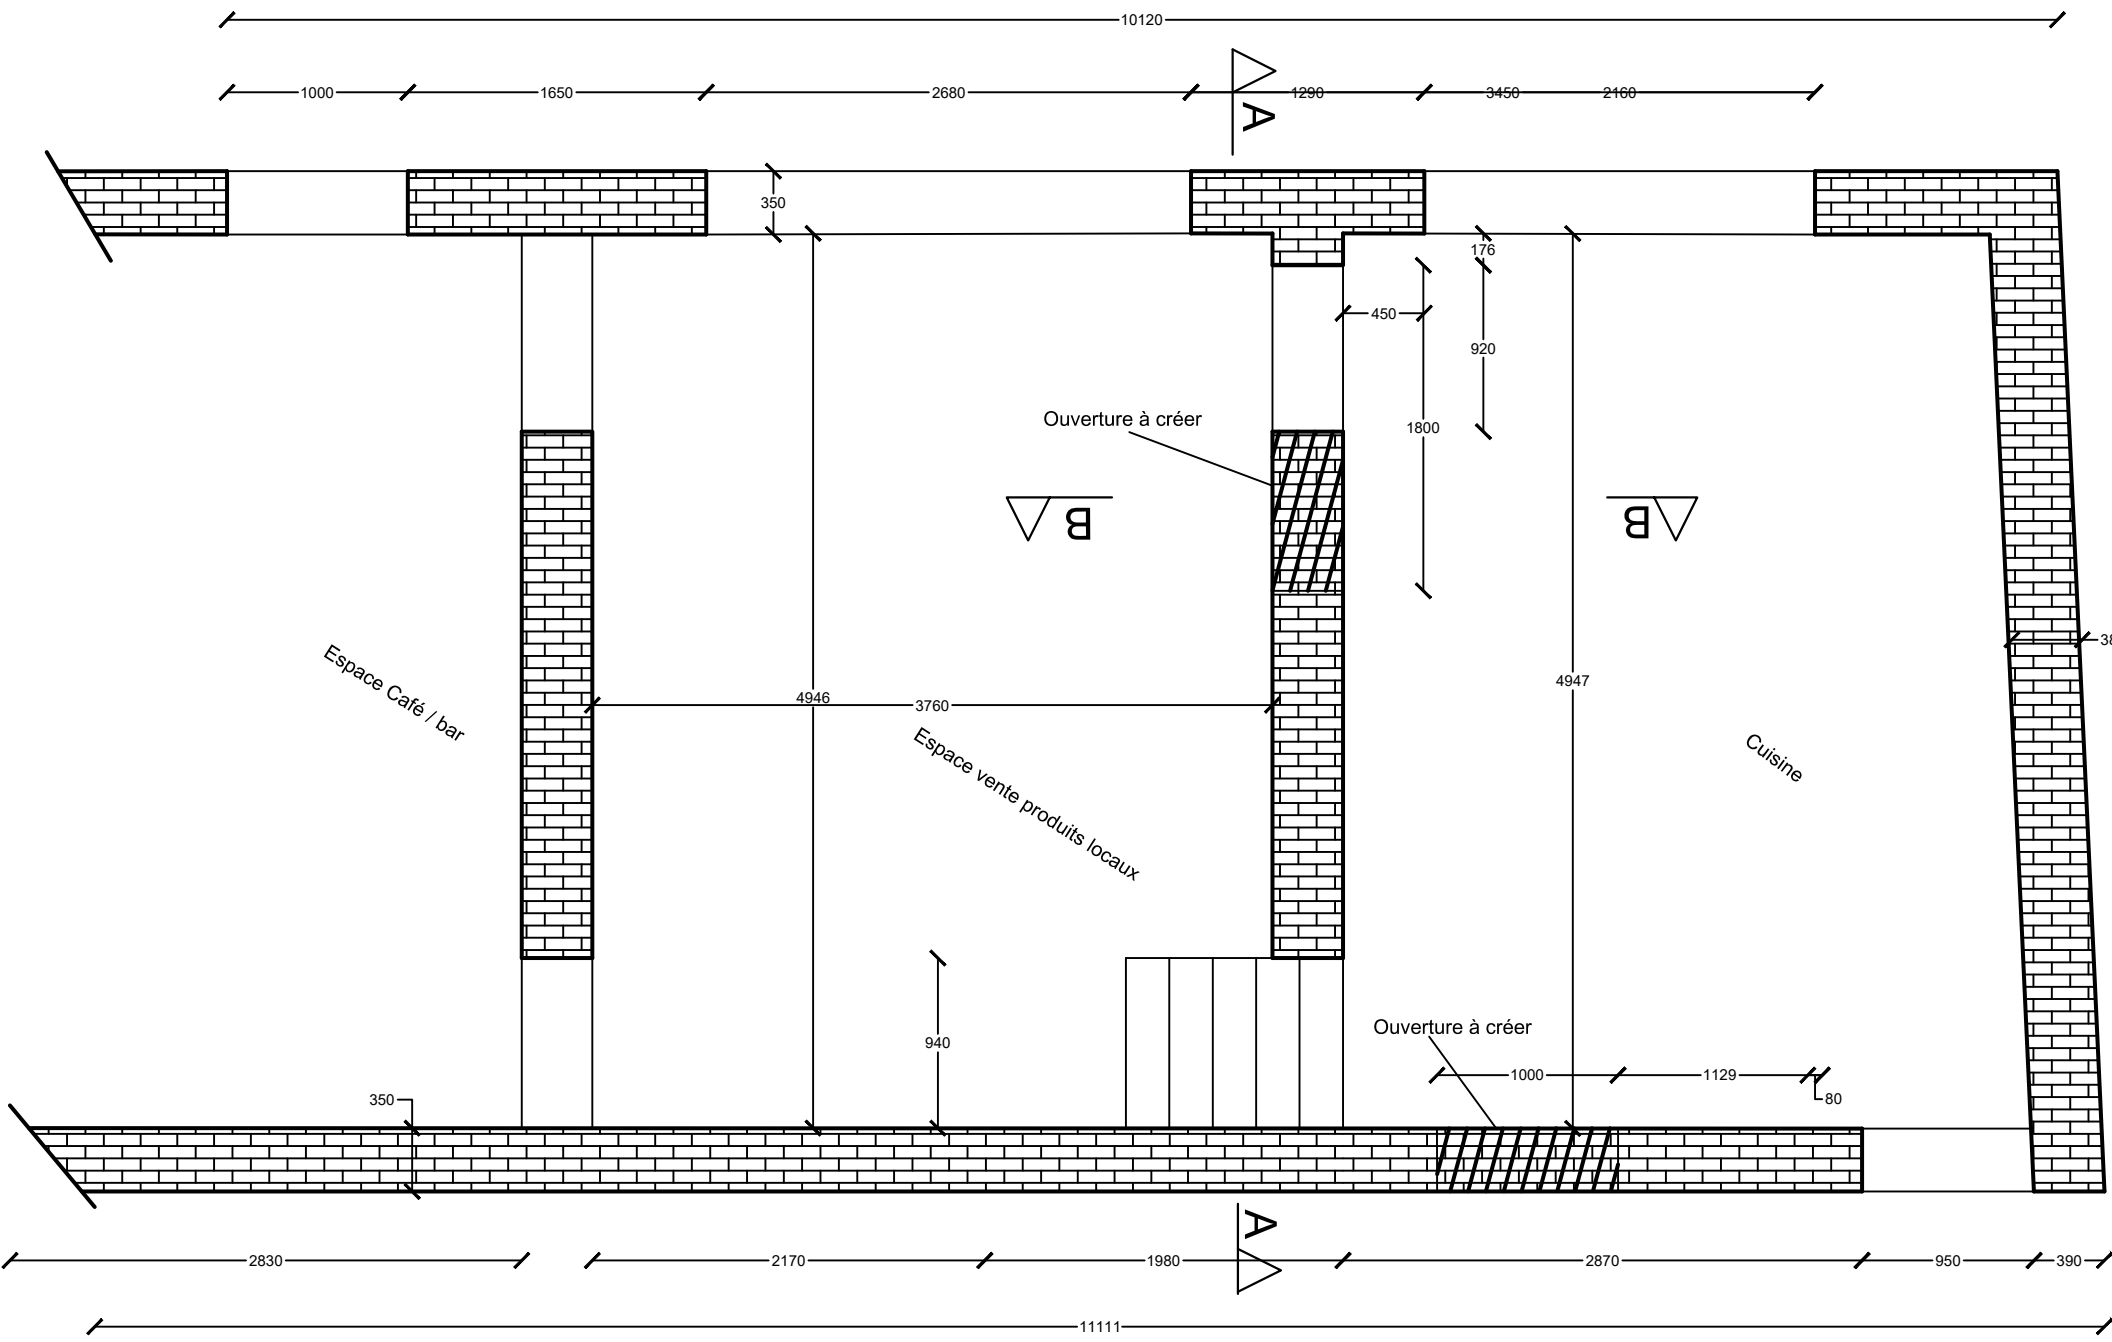


Maîtrise d'Ouvrage :
Mr Eric LELEU
Place de la liberté
59287 Guesnain.

BET STRUCTURE : J.K.F. Structure
92 Bd Du Gén de Gaulle 59100 Rbx
Tél : 06 63 07 71 93


Création de trois ouvertures dans une maison existante.

Dossier Etude Structurelle


VUE EN PLANS RDC EXISTANT.

Plan d'étude 01


Ech : 1/50

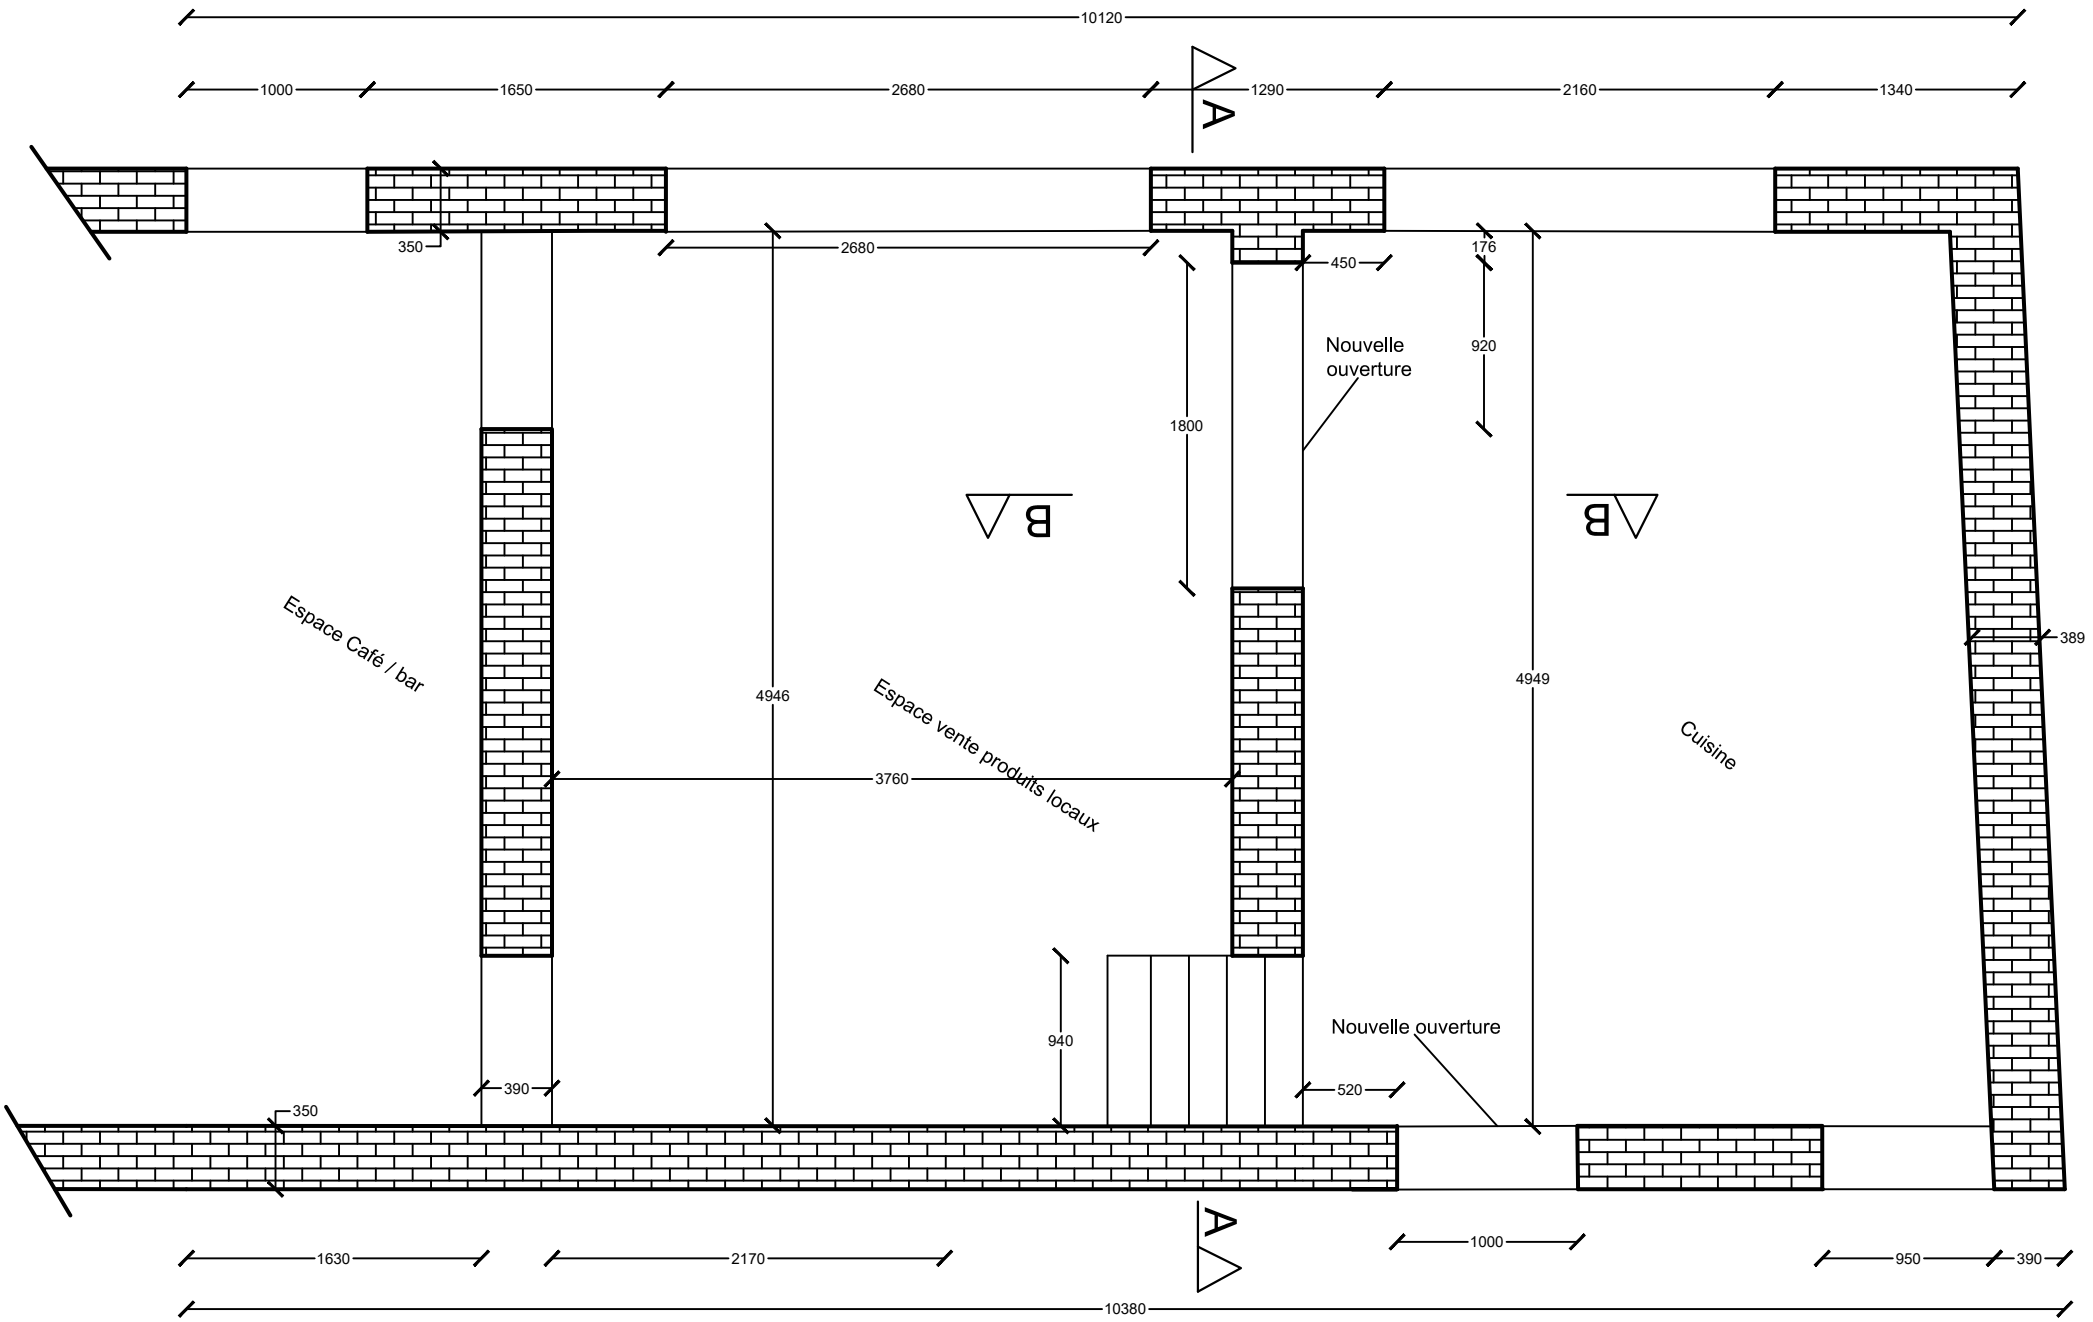

Maîtrise d'Ouvrage : Mr Eric LELEU Place de la liberté 59287 Guesnain.	**BET STRUCTURE :** J.K.F. Structure 92 Bd Du Gén de Gaulle 59100 Rbx Tél : 06 63 07 71 93	Création de trois ouvertures dans une maison existante.	**Dossier Etude Structurelle** VUE EN PLANS RDC PROJET.	**Plan d'étude 02** Ech : 1/50	

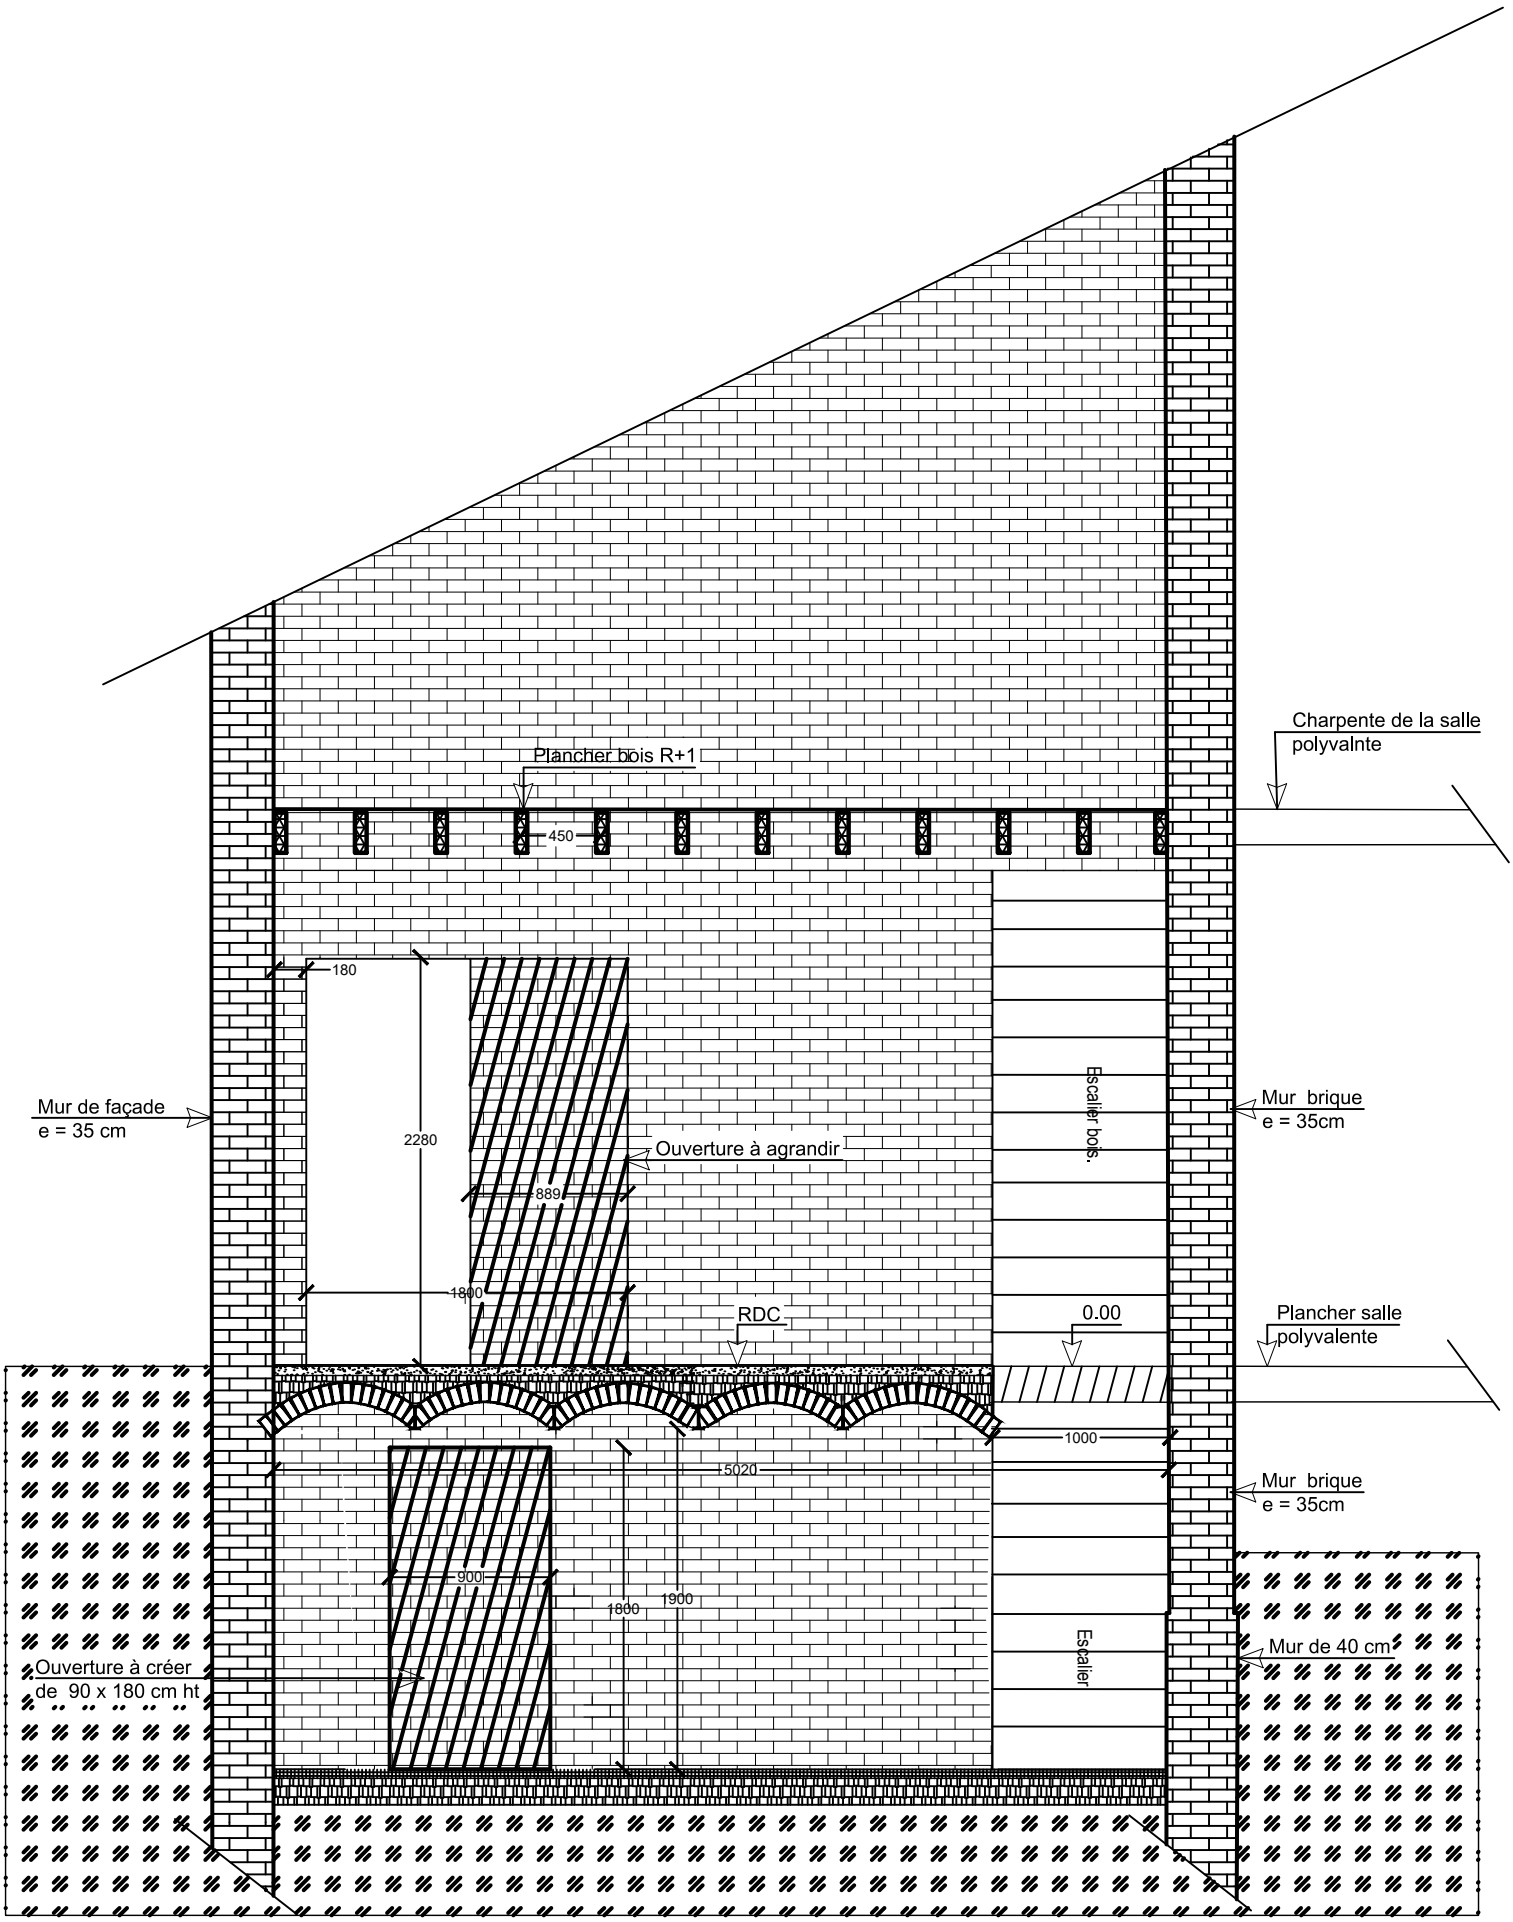

Maîtrise d'Ouvrage : Mr Eric LELEU Place de la liberté 59287 Guesnain.	**BET STRUCTURE :** J.K.F. Structure 92 Bd Du Gén de Gaulle 59100 Rbx Tél : 06 63 07 71 93	Création de trois ouvertures dans une maison existante.	**Dossier Etude Structurelle** COUPE A-A EXISTANT.	**Plan d'étude 03** Ech : 1/50

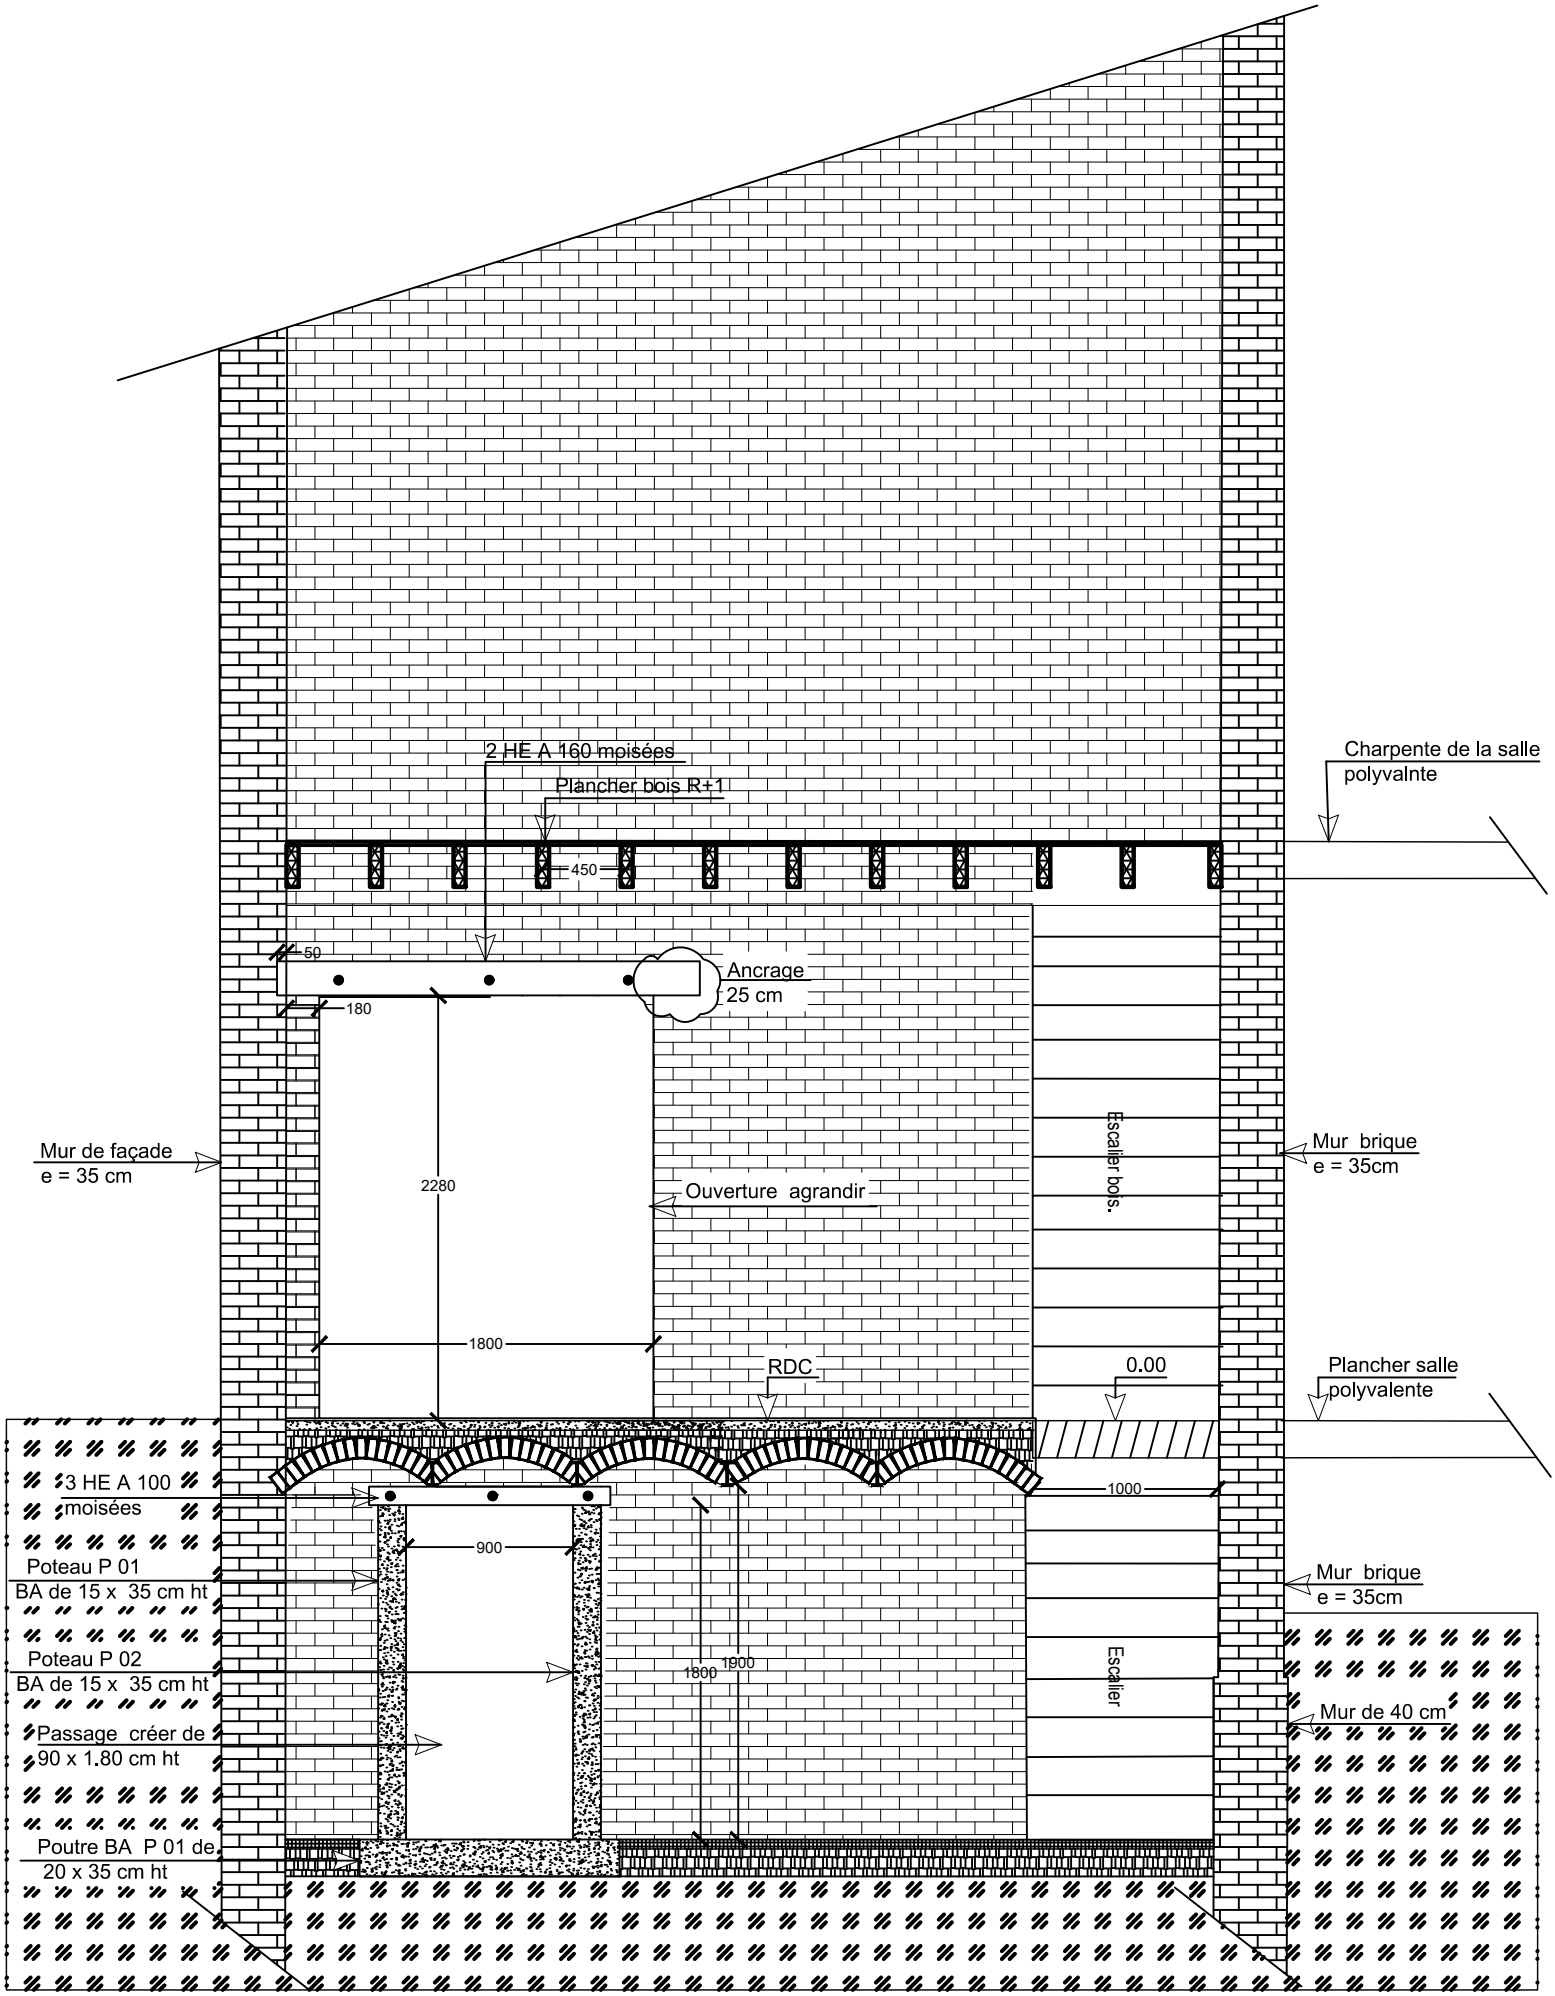


Maîtrise d'Ouvrage :
Mr Eric LELEU
Place de la liberté
59287 Guesnain.

BET STRUCTURE : J.K.F. Structure
92 Bd Du Gén de Gaulle 59100 Rbx
Tél : 06 63 07 71 93

Création de trois ouvertures dans une maison existante.

Dossier Etude Structurelle
COUPE A-A PROJET.

Plan d'étude 04
Ech : 1/50

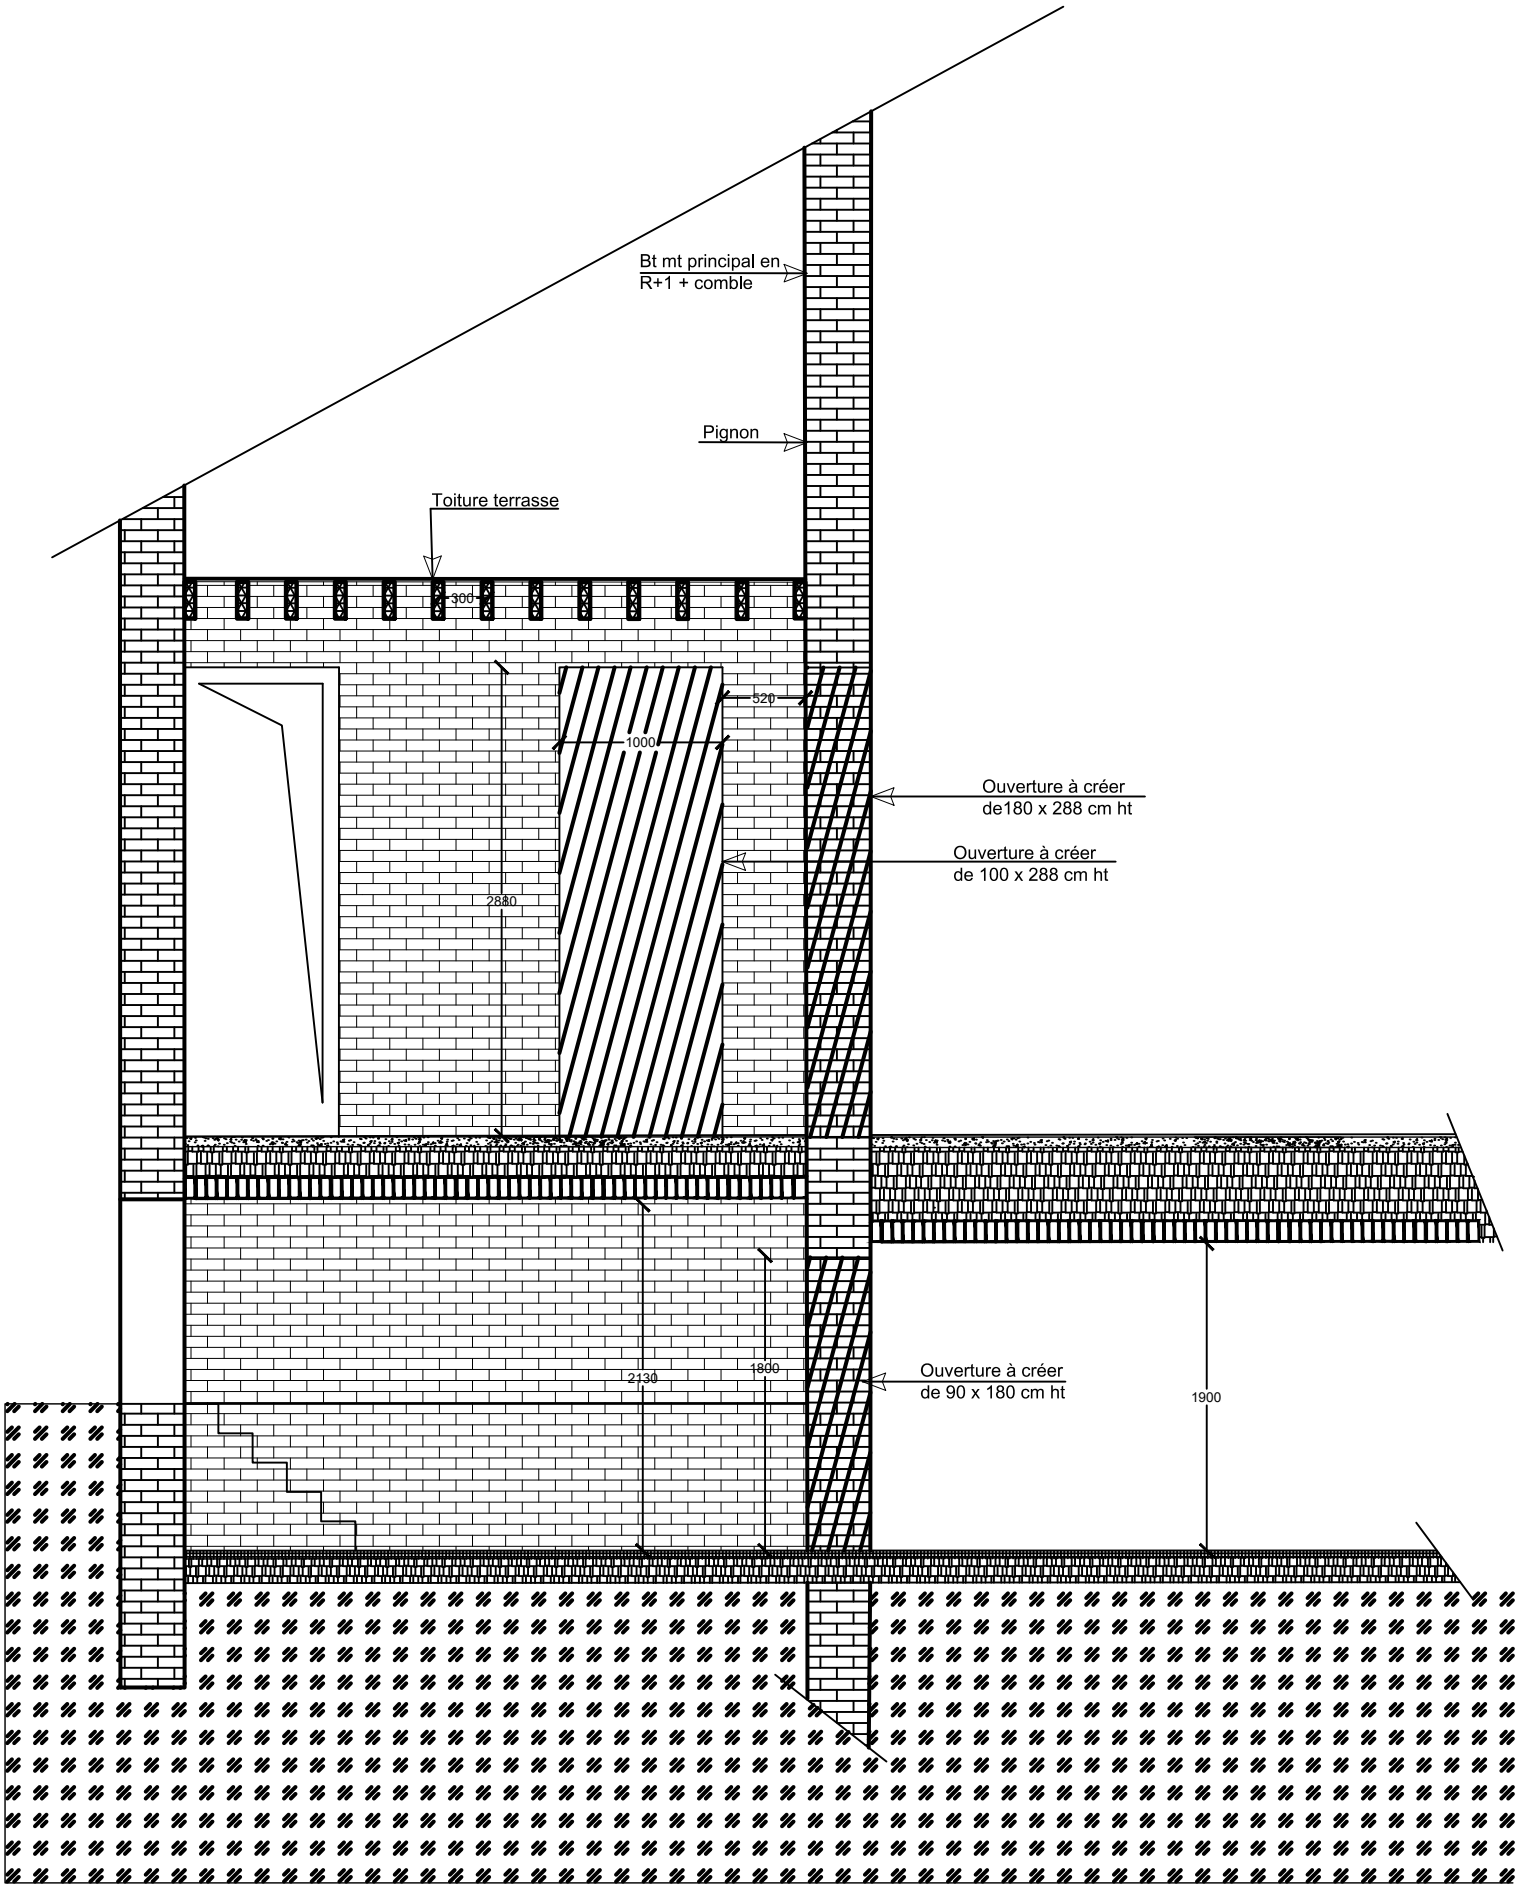

Maîtrise d'Ouvrage :
Mr Eric LELEU
Place de la liberté
59287 Guesnain.

BET STRUCTURE : J.K.F. Structure
92 Bd Du Gén de Gaulle 59100 Rbx
Tél : 06 63 07 71 93


Création de trois ouvertures dans une maison existante.

Dossier Etude Structurelle

COUPE B-B EXISTANT.

Plan d'étude 05

Ech : 1/50

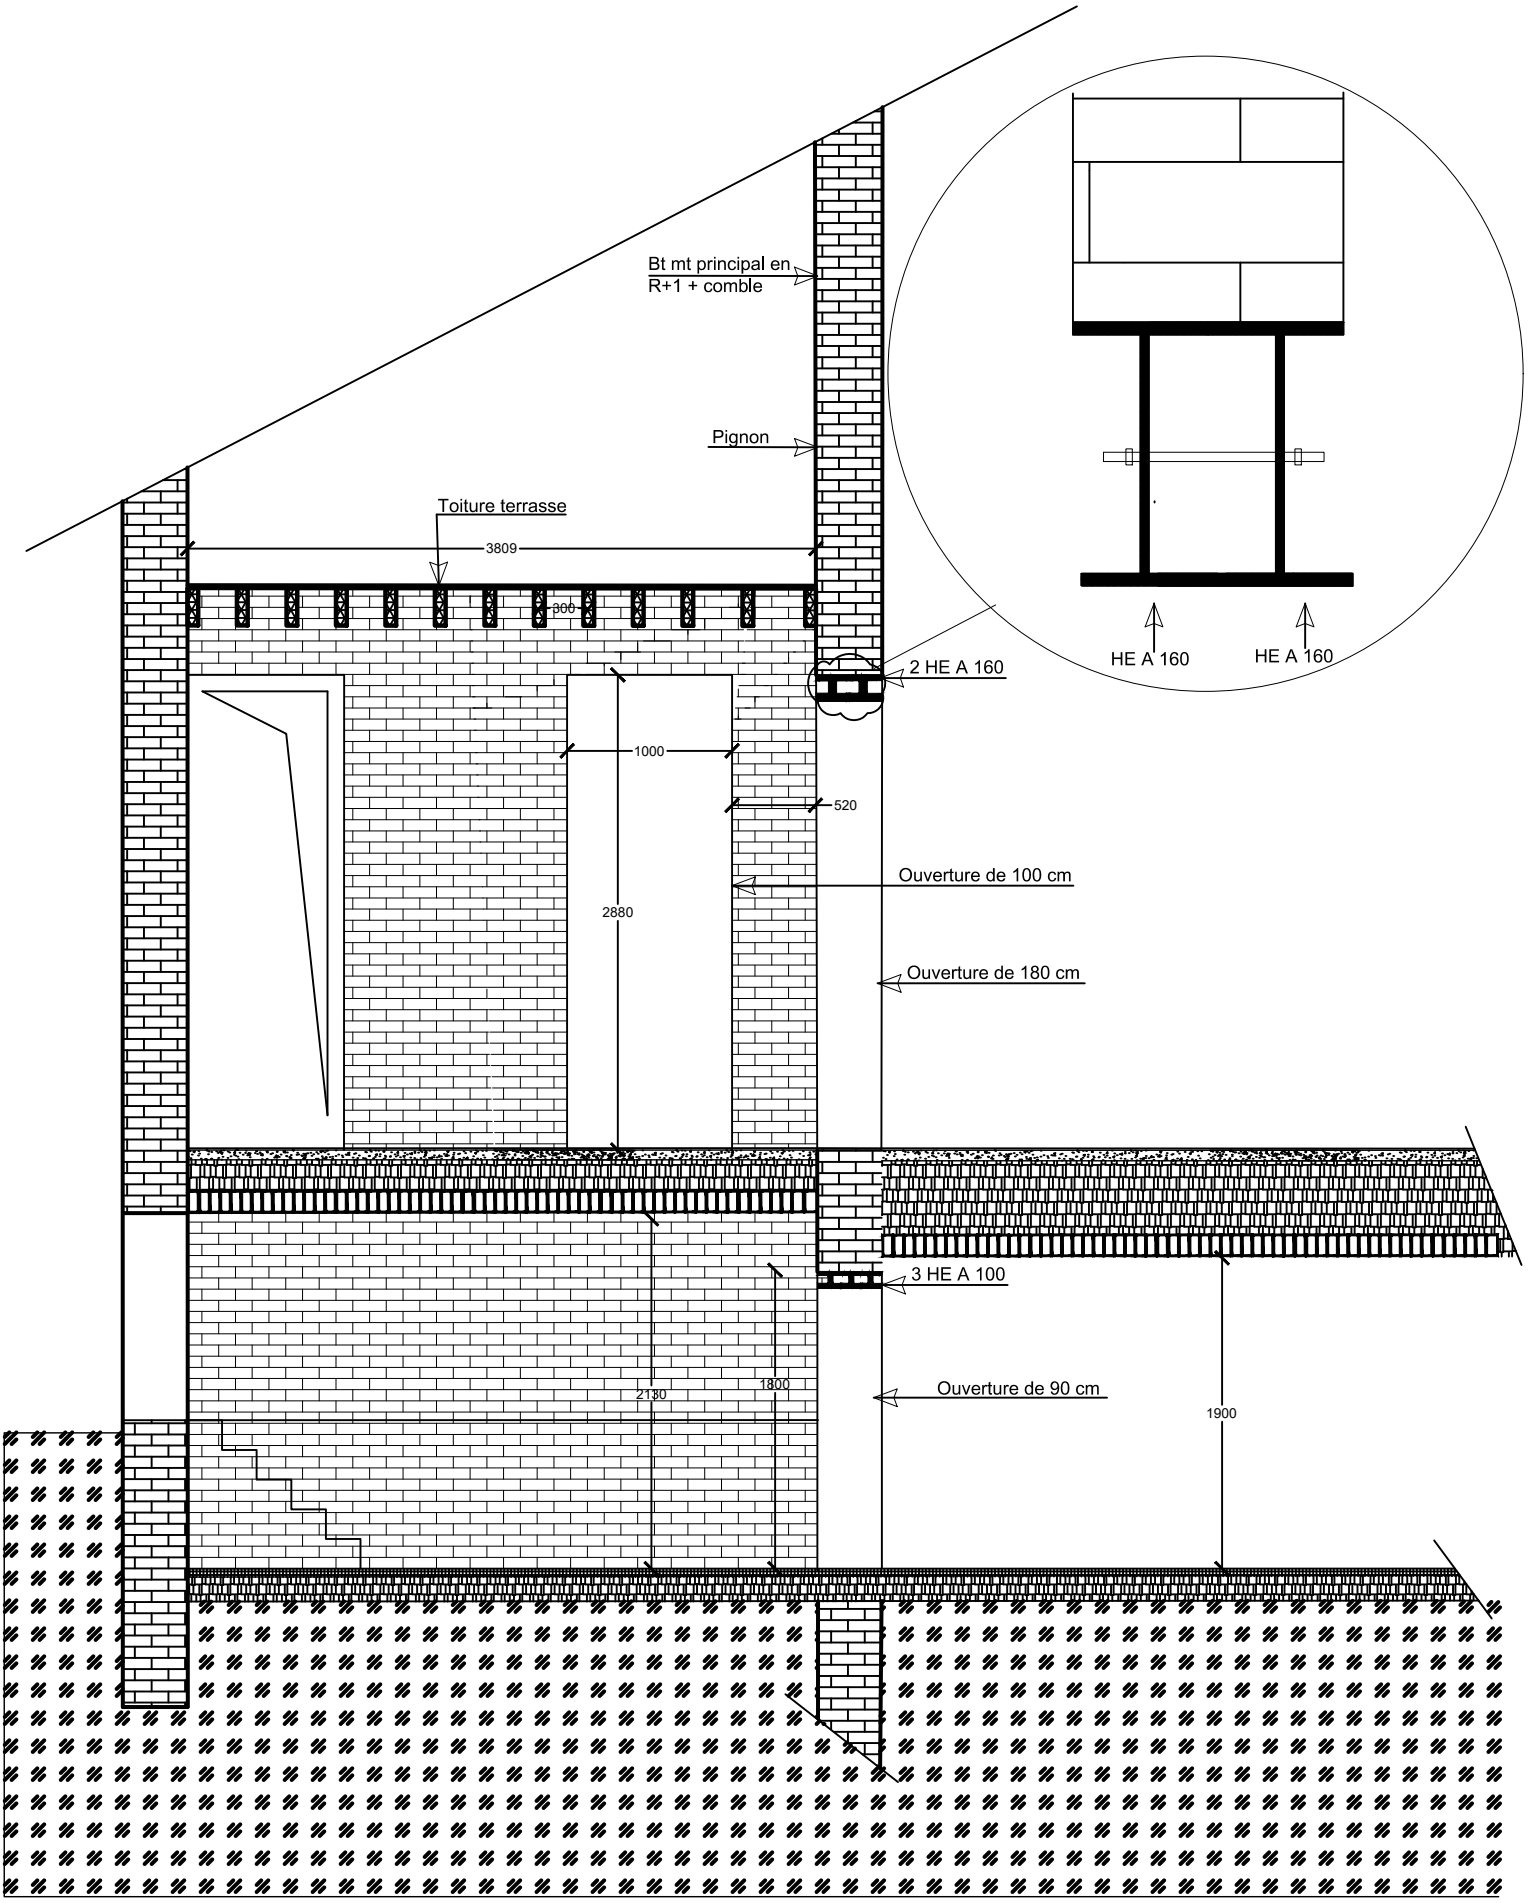

Maîtrise d'Ouvrage :
Mr Eric LELEU
Place de la liberté
59287 Guesnain.

BET STRUCTURE : J.K.F. Structure
92 Bd Du Gén de Gaulle 59100 Rbx
Tél : 06 63 07 71 93

Création de trois ouvertures dans une maison existante.

Dossier Etude Structurelle

COUPE B-B PROJET.

Plan d'étude 06

Ech : 1/50